


פתחי גישה אופן ארט בתיאום סופי מול אדריכל
כלל יחידות המיזוג אשר נמצאות בתוך נגרות יש לתאם סופית מול אדריכל ונגרות


Court 6
1st Floor

Option **No3**
VRF duct units

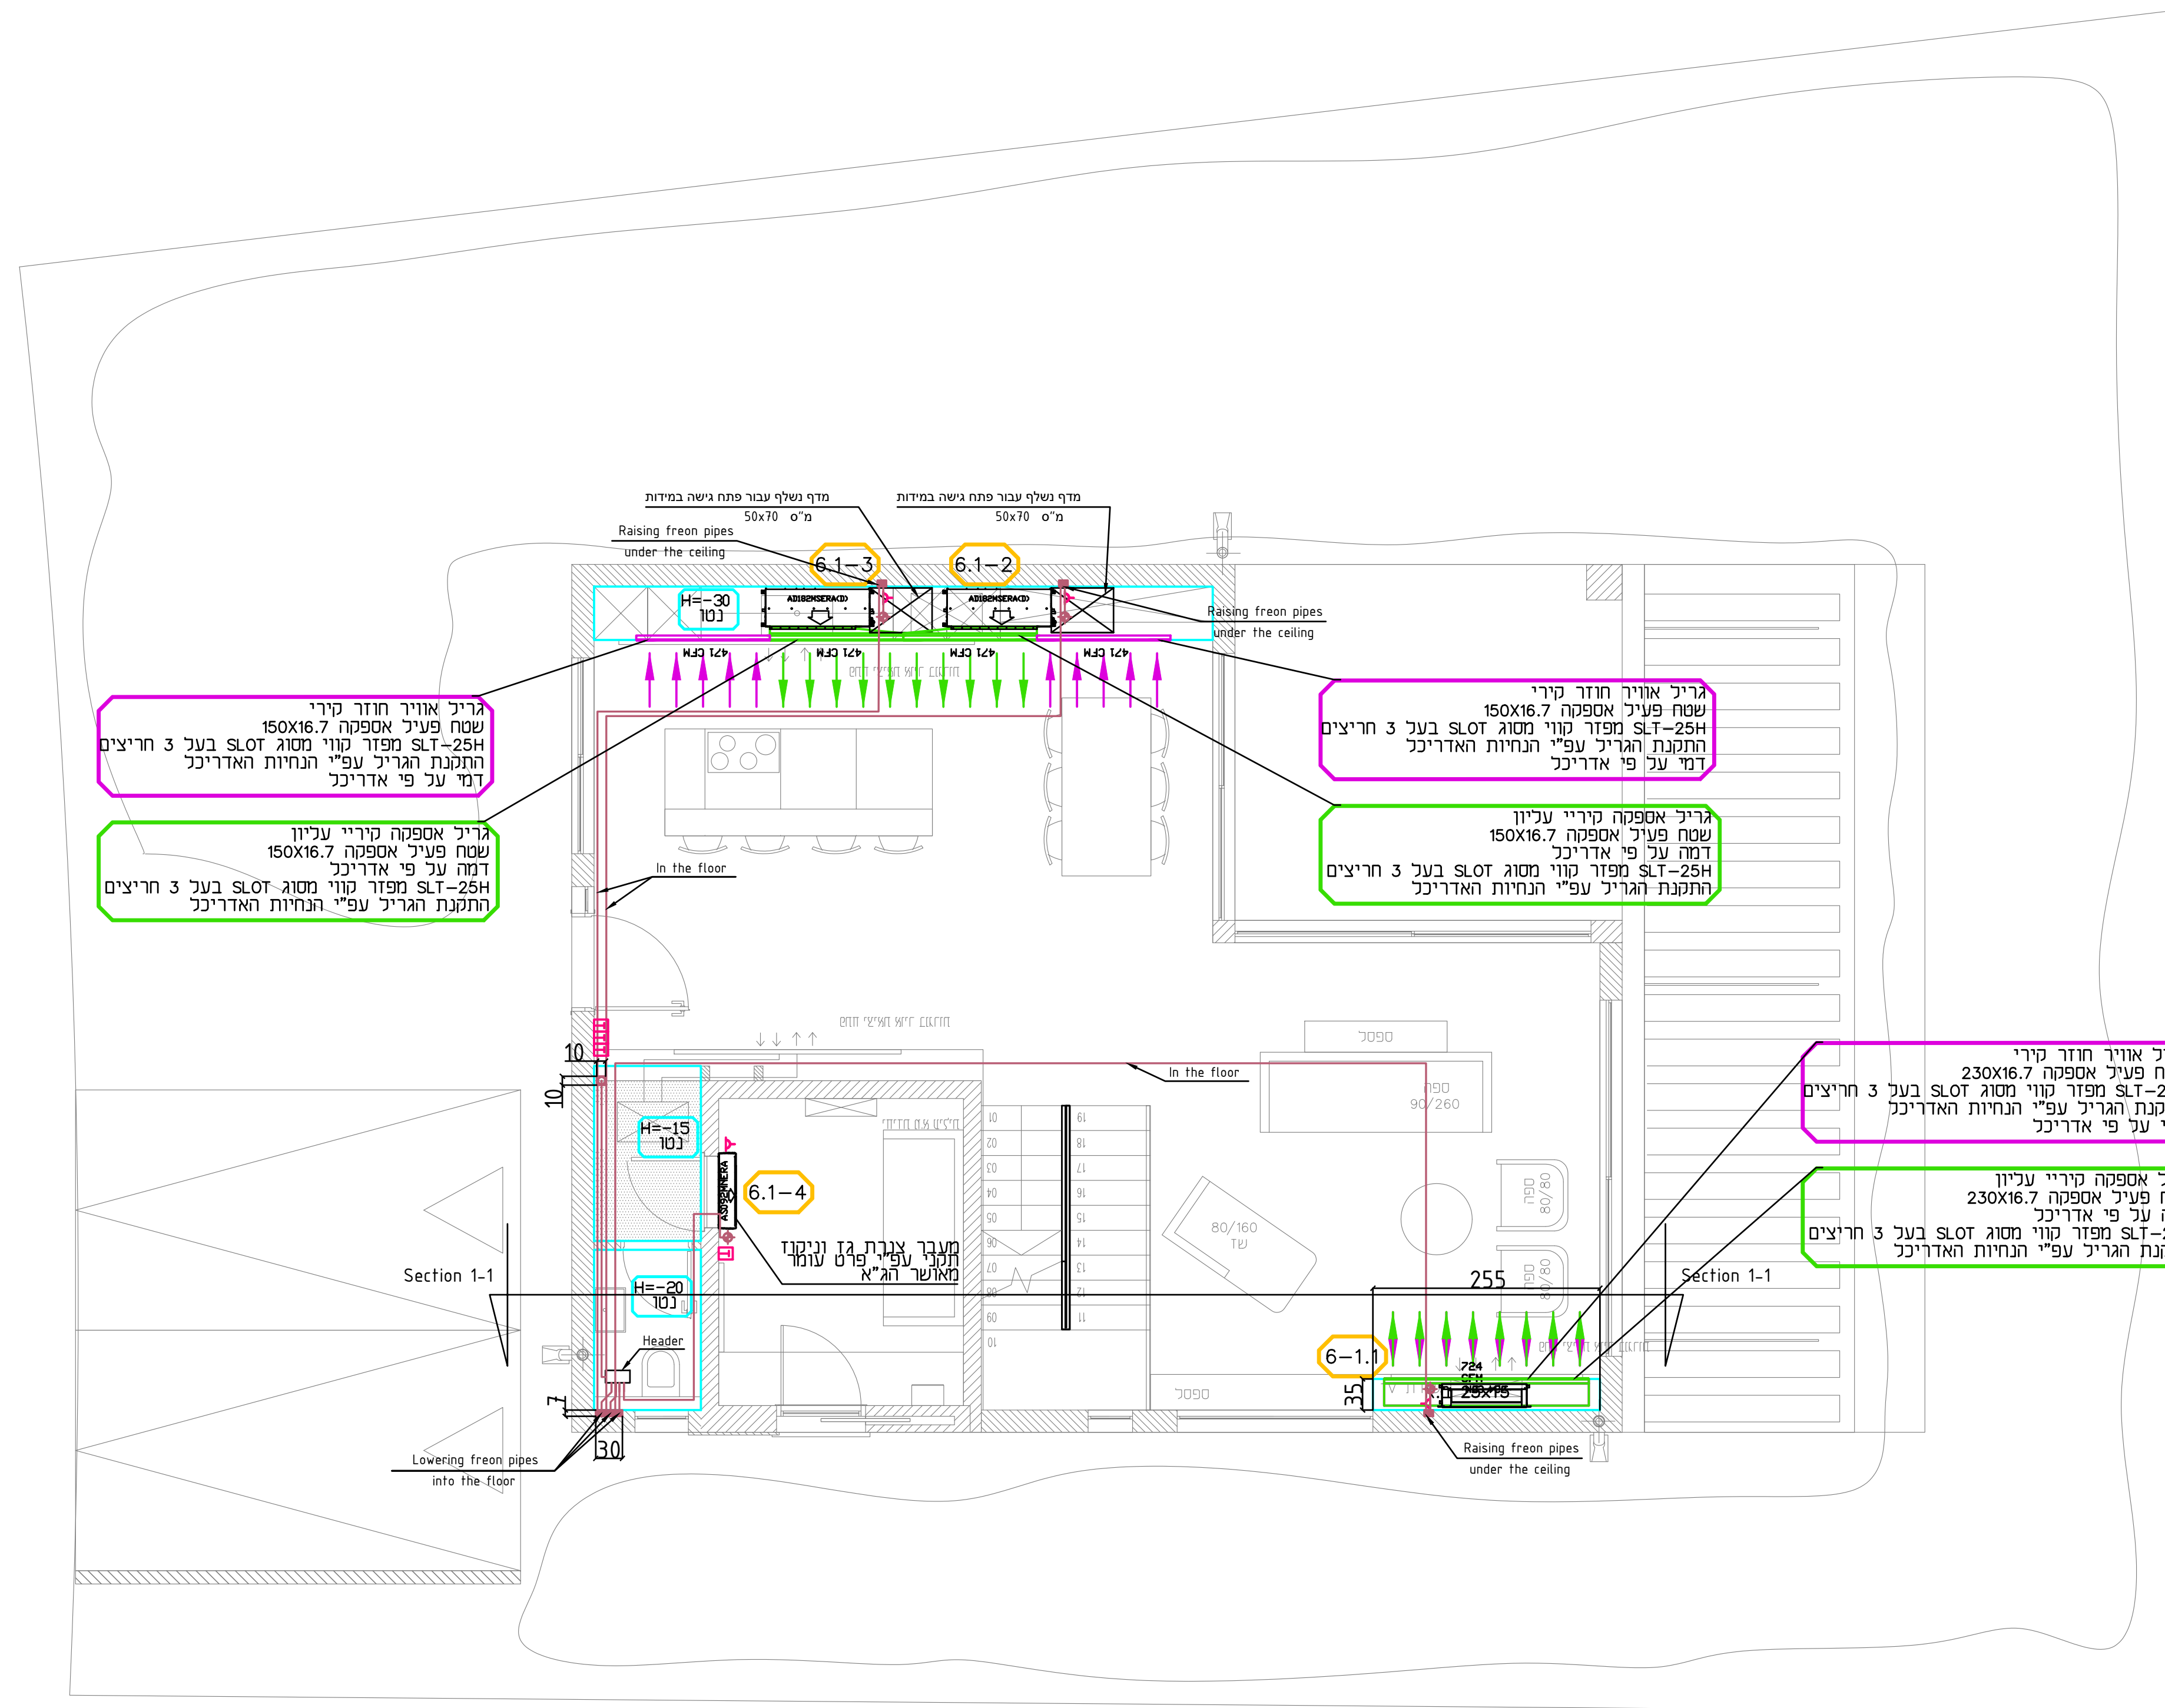

Court 6
2nd Floor

Option **No3**
VRF duct units

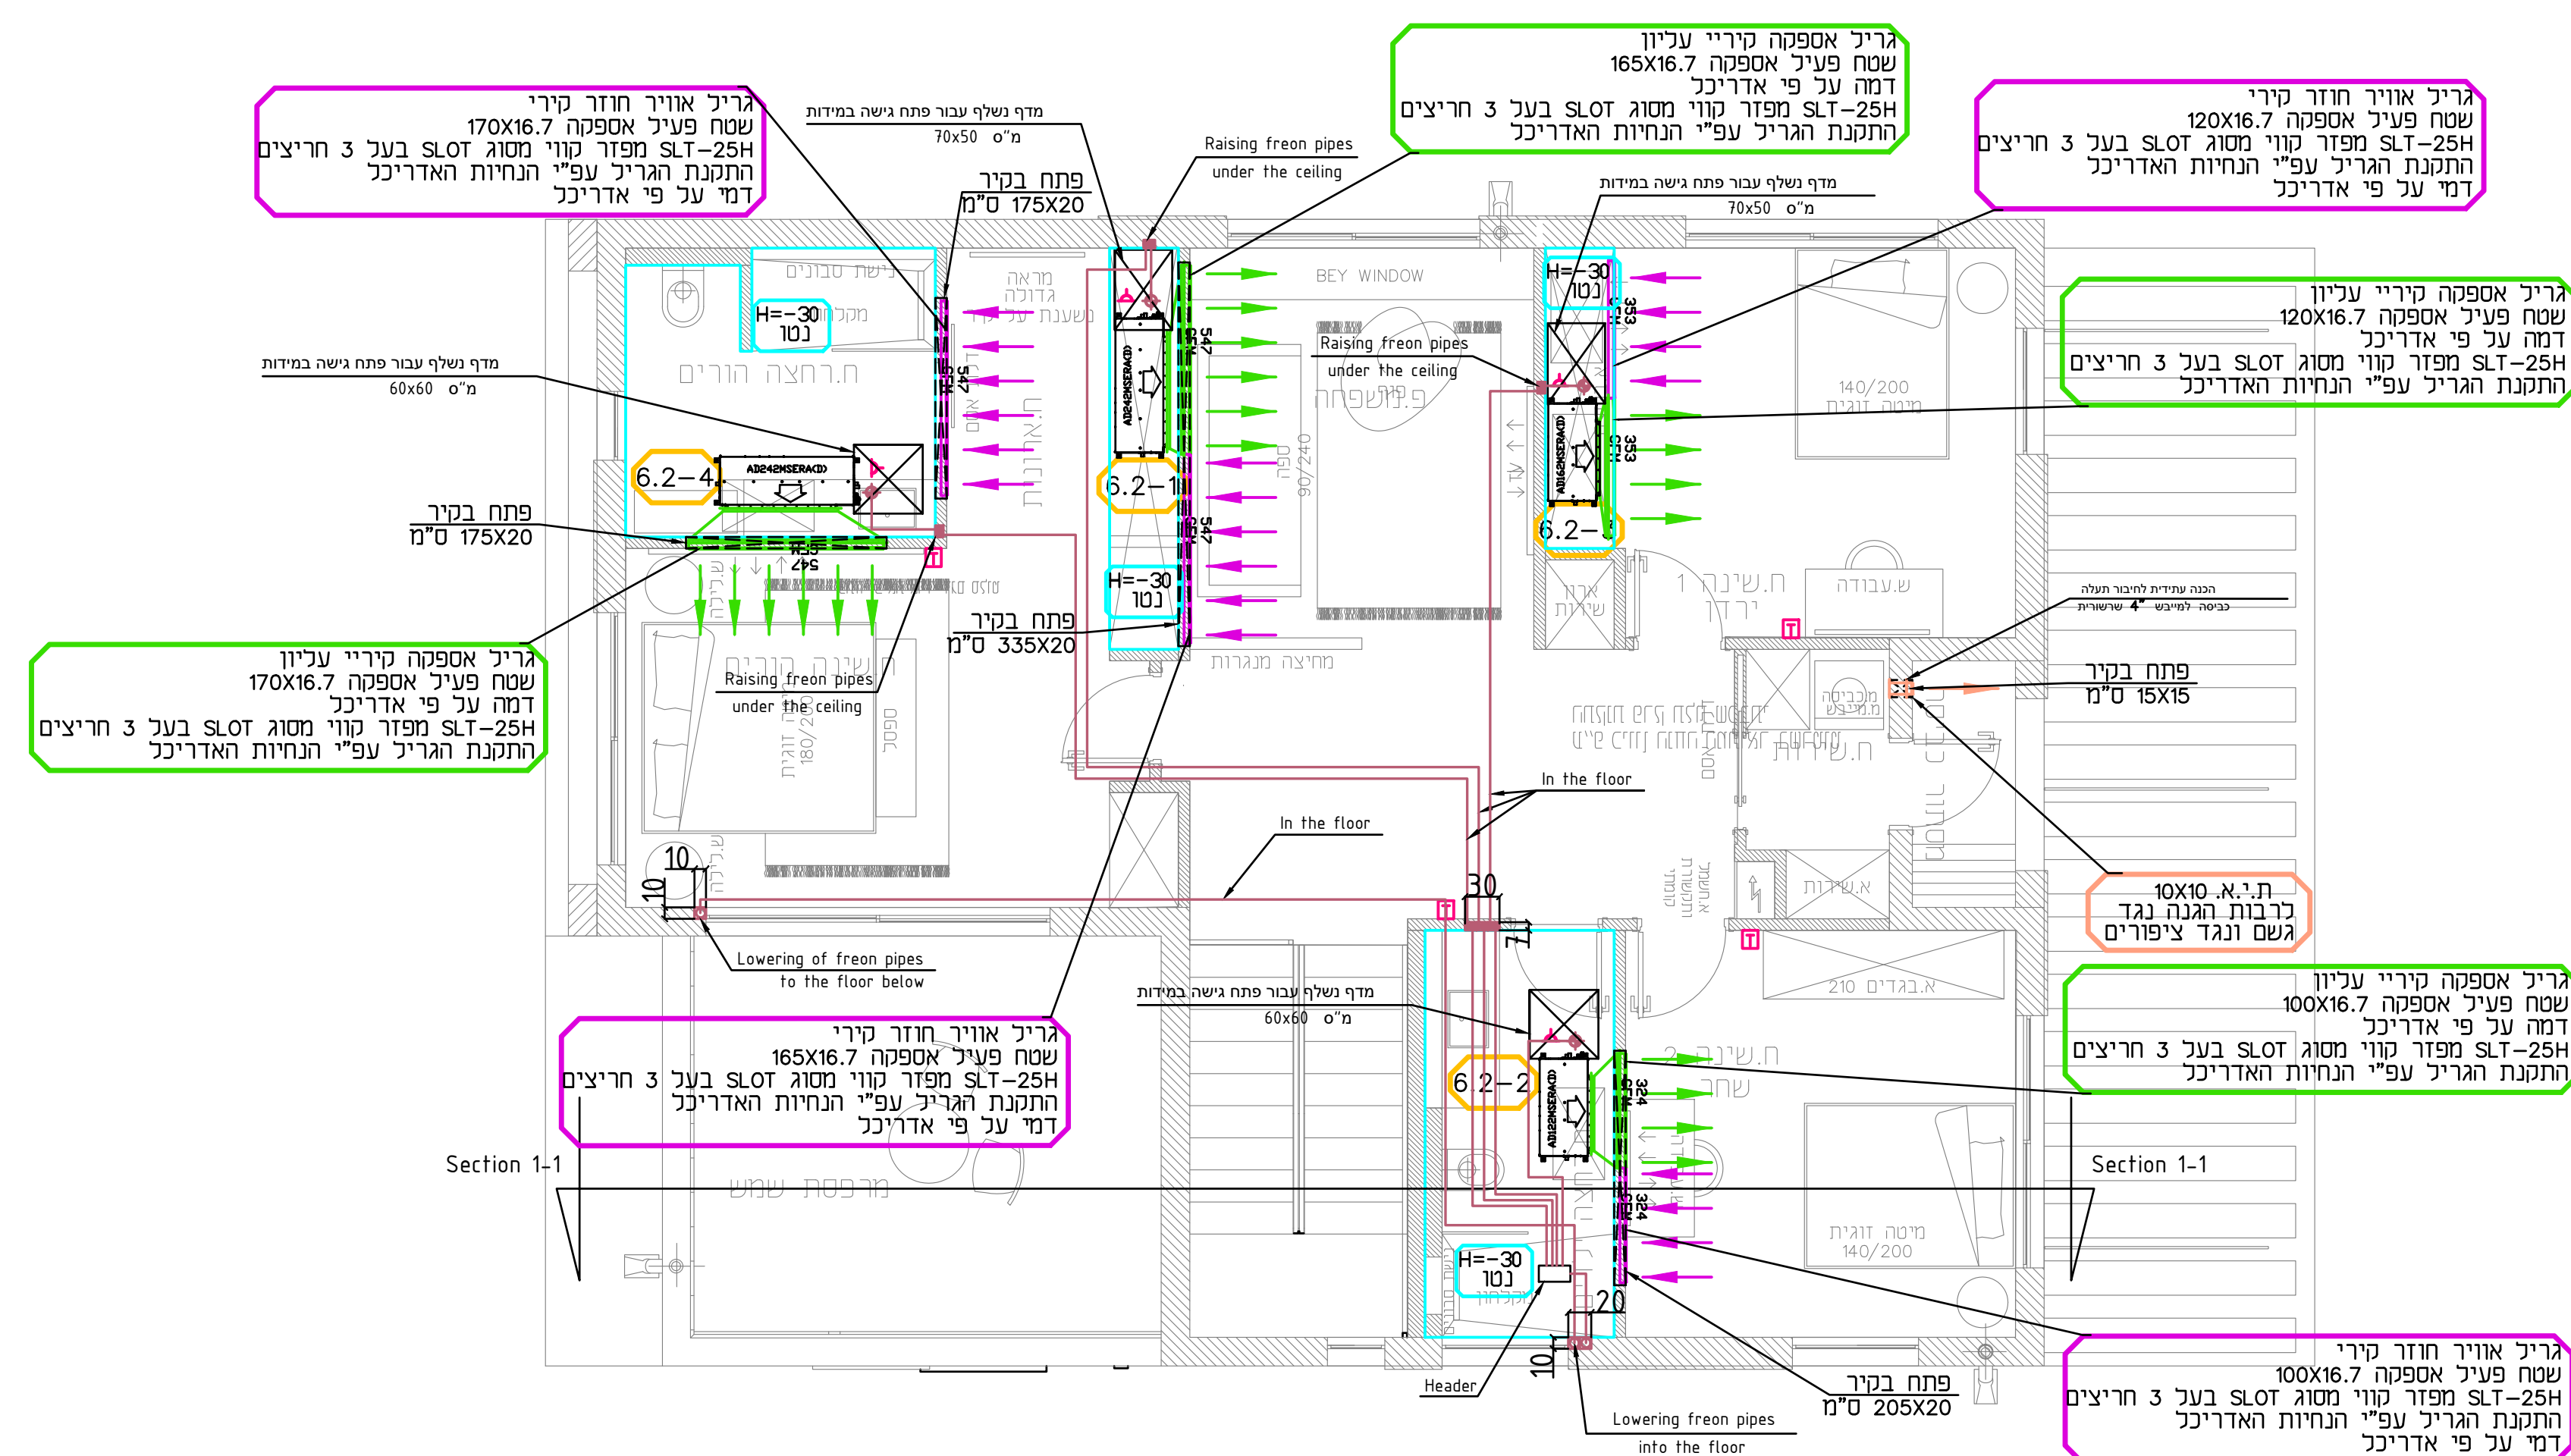

תפוצה

[illegible]

מהדורה

תחילת תפקוד	01.01.2025	א
תחילת תפקוד	02.05.2025	א
תחילת תפקוד	28.03.2025	א
תחילת תפקוד	11.03.2025	א
שנתיים	חצי	א

המבצע אחראי למידות ולהתאמתן למציאות בכל מקרה של אי התאמה, סתירה או טעות עליו להודיע למתכנן לפני התקדמותו בביצוע! אין לקבוע מידות על סמך מדידה בשרטוט. אין לעשות כל שימוש בתוכנית זו או ברעיונות הגלומים בה ללא אישור בכתב מאת המתכנן.

הערות

1. כל התעלות מחוץ למבנה יבודוד
ביבדוד אקוסטי בבו"ב 2"
מידות התעלות ון מידות פח
2. תעלות מזוג בתוך המבנה יבודוד
ביבדוד אקוסטי פנים 1"
מידות התעלות ון מידות פח
3. תעלות אוויר צה יבודוד
ביבדוד סרטי 1"
מידות התעלות ון מידות פח
4. יש אסאם בסימיקות וא פינות החיבור
של תעלות מזוג אוויר לפני כיפוף
הפחים המתחברים

מקרא


- מ- מפוח
 מ- מפה
 מ- מפוח אוויר קרוי
 מ- מפוח אוויר תהדית
 מ- חרס אוויר חודו
 מ- חרס אוויר צח
 ב- בידוד לאוסטי
 ב- בידוד טרמי
 ב- לכל בידוד
 ד- דמפר אש
 טרומסט לוח העפלה
 שקוע השמנל לטפול יוענע השמנל
 שקוע תכת פאזי לטפול יוענע השמנל
 משטח בחטון חד פאזי לטפול יוענע השמנל
 מנסה בחטון חד פאזי לטפול יוענע השמנל
 ניקוח מאייר לטפול יוענע אינסטקטור
 גולטע 25 מ"ס מחתותי גובה המאייר
 שבעה פאזי אחרונא

מקרא צבעים בתכנית

- | | |
|--------------------------|---|
| תעלות ותריסי אוויר חוזר |  |
| תעלות ותריסי אספקת אוויר |  |
| תעלות ותריסי אוויר צח |  |
| תעלות ותריסי יניקת אוויר |  |
| תעלות ותריסי שיחזור עשן |  |
| צנרת גז וחשמל |  |
| סימון מעגלי מ"זוג אוויר |  |

191	מבני מגורים צמודי קרקע נופיה אכזרי מנשה מגרש 6	ספ' מפרנסים	ספ' מפרנסים
1:50	מיזוג אוויר ואווירורר	ספ' מפרנסים	ספ' מפרנסים
02.05.2025	קומה ראשונה ושנייה	ספ' מפרנסים	ספ' מפרנסים
3		ספ' מפרנסים	ספ' מפרנסים
מדידת		ספ' מפרנסים	ספ' מפרנסים
○	□	●	△
כביש	מסדר	מסדר	מסדר
		11.03.2025	
		מסדר	מסדר

Option ~~No~~1
VRF duct unit in living room
and wall mounted in rooms

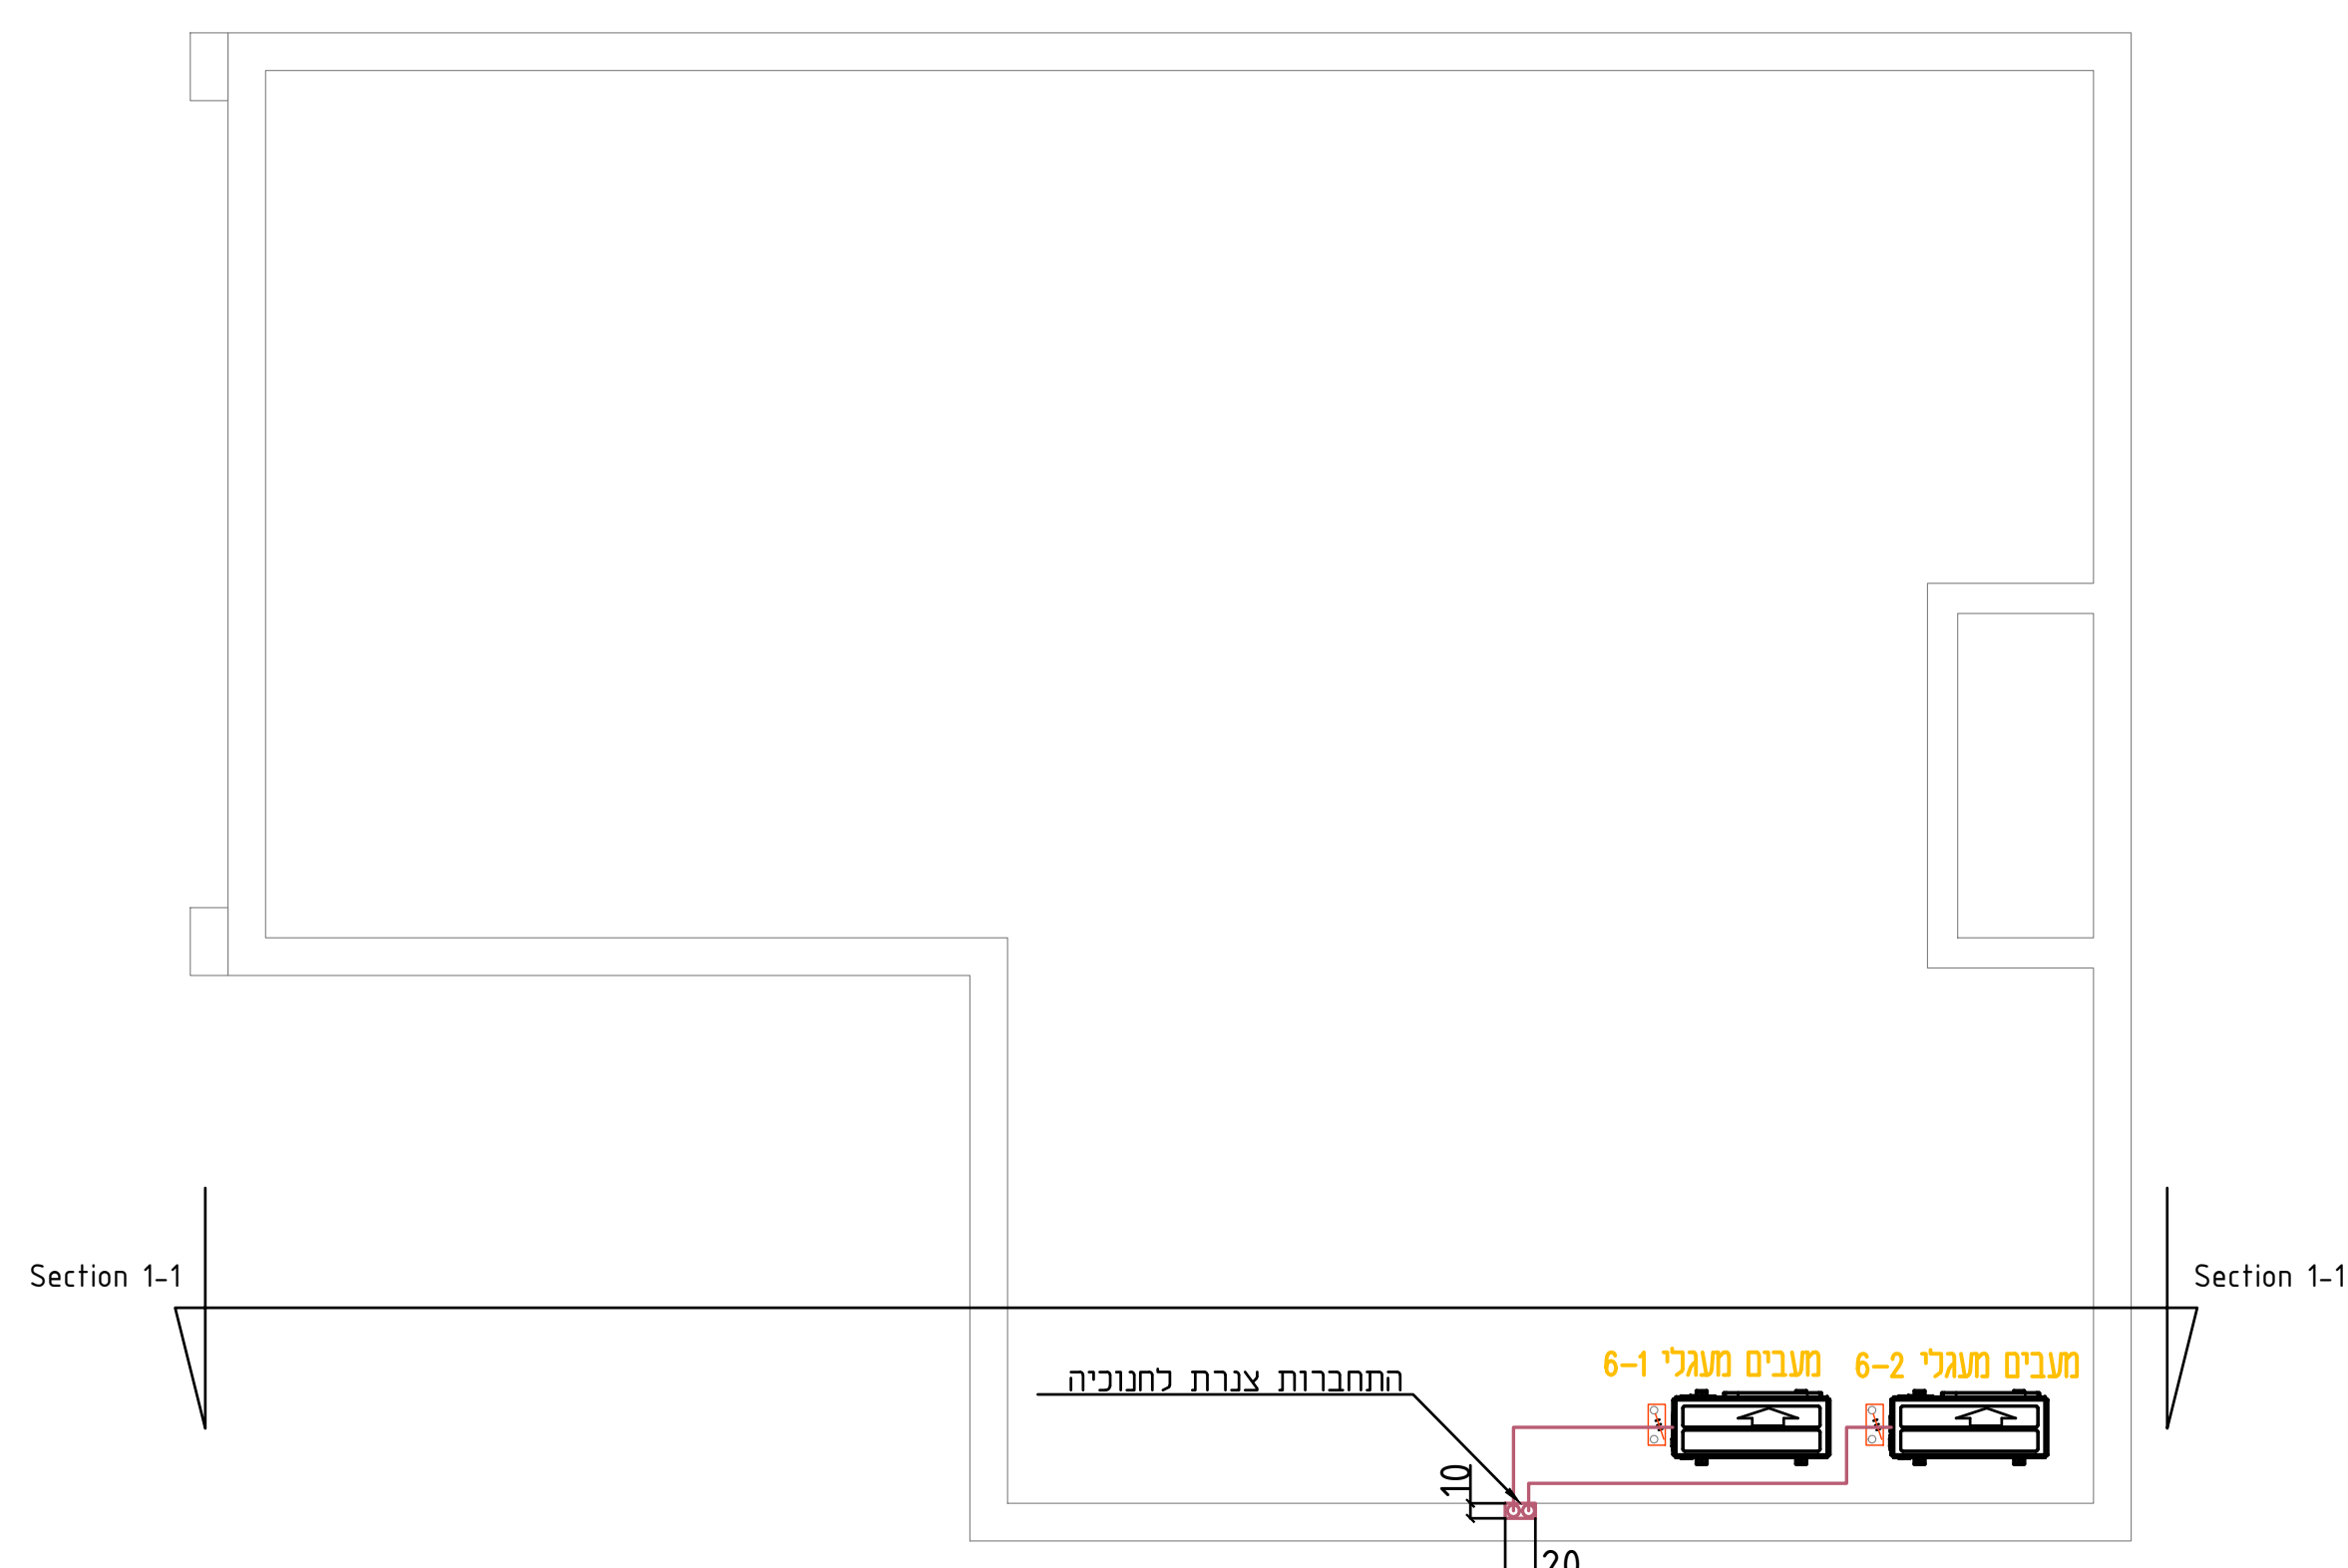

יחידות פתח טבעל 6-1											
חסימה הספק נטו W _{net} /kg	מחזור v/hz/Ps	מרחק פנל	מרחק מזג	משקל kg	רמת רעש db(A)	ספיט איור CFM	חופת כנור h/ft	מאייד	דגם	חוצרת	מש יחידה בתכנית
---	230/50/1	---	17/142.5/17.0"	22.2	33	471	19,100	Slim Duct Low ESP	AD182MSERA(D)	Haier	6-1.2 6-1.3
---	230/50/1	---	105.1/721.2/10.0"	33	42	724	27,300	Duct Medium ESP	AD282MJERA	Haier	6-1.1
---	230/50/1	---	5.7/283/201.0"	10	36	352	9,500	מאייד עילי	AS092MNERA	Haier	6-1.4

יחידות טעור כמעל 6-2										
מש' יחידה בחבנית	חוצרת	דגם	מאי"ר	חפזנה, קוור Blw/h	ספיט אדיר CFM	רשת רעש dB(A)	משקל kg	מידות מ"ר	מידות מחז וחזק V/m²/Hz	הספק נאָר W
6-2,2	Haier	AD122MSER(A)	Slim Duct Low ESP	12,300	324	30	18.5	42w/18.5h/85l	230/50/1	---
6-2,3	Haier	AD162MSER(A)	Slim Duct Low ESP	15,400	353	32	18.5	42w/18.5h/85l	230/50/1	---
6-2,1 6-2,4	Haier	AD242MSER(A)	Slim Duct Low ESP	24,800	547	36	24	42w/18.5h/117l	230/50/1	---

בסיס בטון בגובה מינימלי 10 ס"מ	מעבים מועילי 1-6
יחידת עיבוי עומדת ע"ג בולמי רעידות	AV08NMSETA
לטיפול קבלן מזוג אוויר	77.100 BTU/Hr
	מ"מ : 405/163.6/105.9
	גובה : 3x20 (A)
	נתיב חשמלי



מיקום סופי של המעבים
ייקבע בשטח
בתיאום עם האדריכל
והרלו מיוזג אוויר

מיקום סופי של הניקוזים
ייקבע בשטח בתאום עם האדריכל
יועץ אינסטלציה וקבלן מיזוג אוויר


6-2 מעבים מעגלי
 AV08NM5ETA : דגם
 77,100 BTU/hr : תפוקה
 40/163.6/105.7 : מידה
 3x20 (A) : נתיך חשמלי
 ס"מ



מיקום סופי של המעבים
ייקבע בשטח
בתיאום עם האדריכל
וקבלו מיזוג אוויר

מיקום סופי של הניקוזים
ייקבע בשטח בתאום עם האדריכל
יועץ אינסטלציה וקבלן מיזוג אוויר

Section 1-1

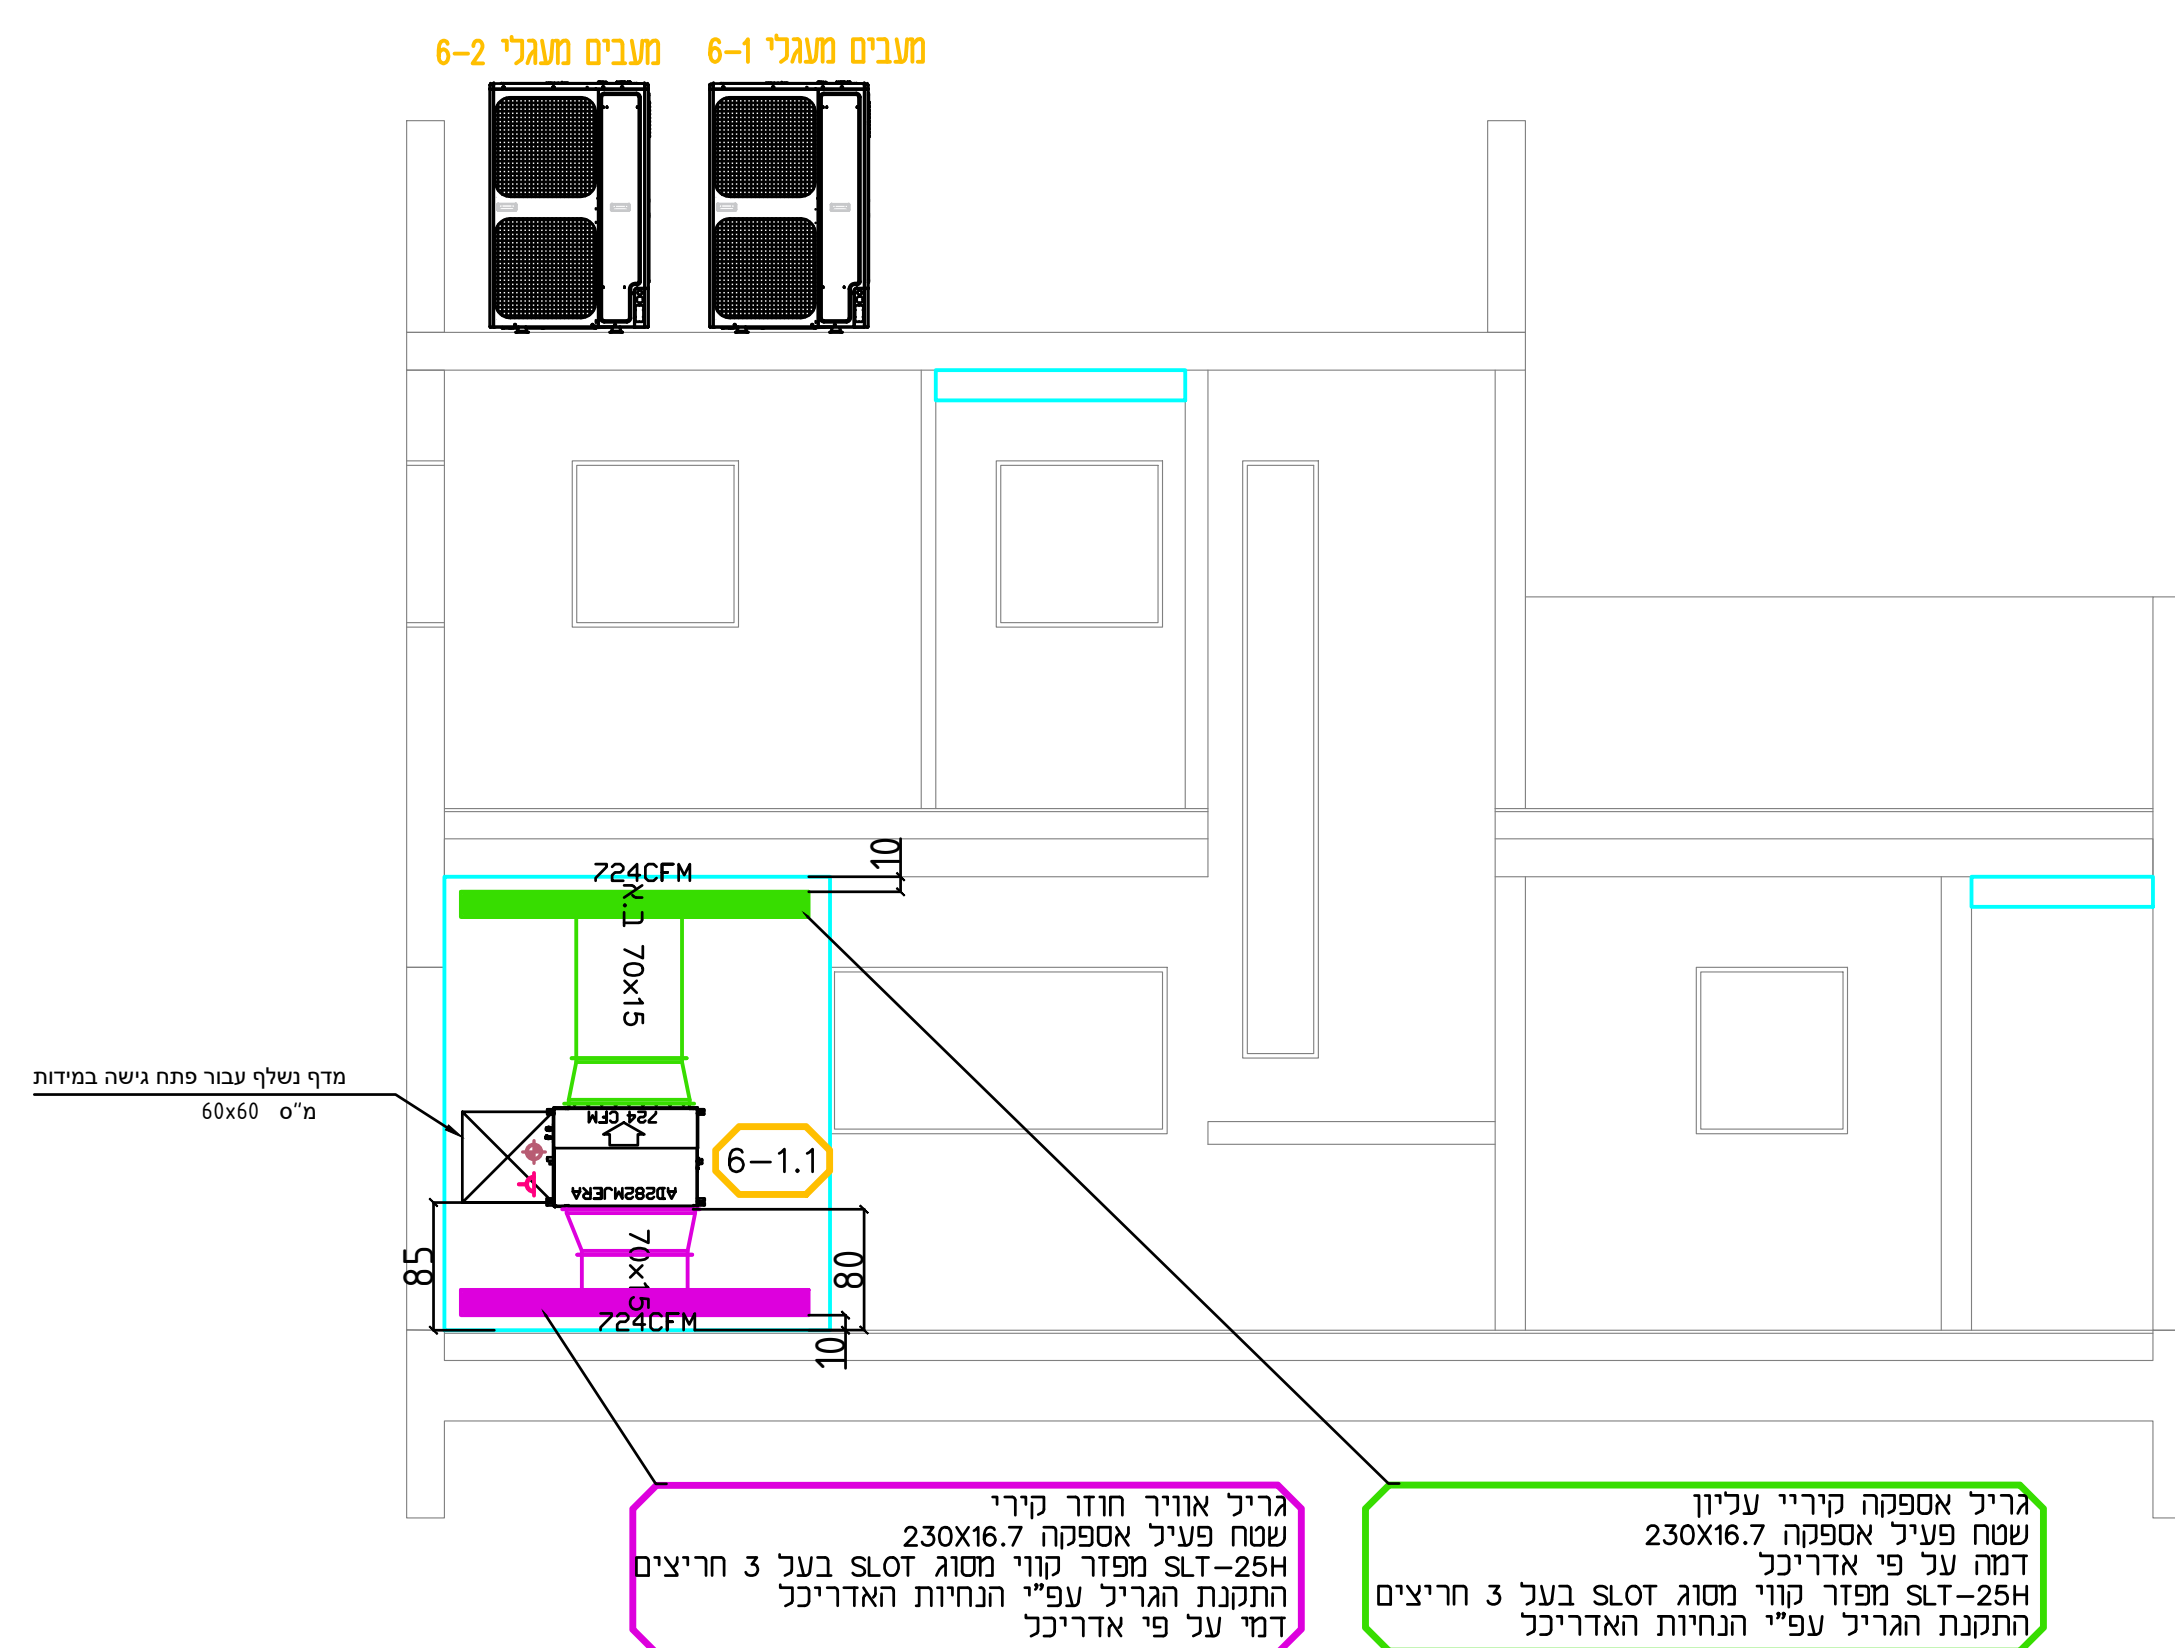[illegible]

תחילת תפקוד	01.01.2025	א
תחילת תפקוד	02.05.2025	א
תחילת תפקוד	28.03.2025	א
תחילת תפקוד	11.03.2025	א
שנתיים	חצי	א

המבצע אחראי למידות ולהתאמתן למציאות בכל מקרה של אי התאמה, סתירה או טעות עליו להודיע למתכנן לפני התקדמותו בביצוע! אין לקבוע מידות על סמך מדידה בשרטוט. אין לעשות כל שימוש בתוכנית זו או ברעיונות הגלומים בה ללא אישור בכתב מאת המתכנן.

1. כל התעלות מחוץ למבנה יבודדו
בבידוד אקוסטי בעובי 2"
מידות התעלות הן מידות פח

2. תעלות מזוג בתוך המבנה יבודדו
בבידוד אקוסטי פנימי "1"
מידות התעלות הן מידות פח

3. תעלות אוויר צה יבודדו
בבידוד טרמי 1"
מידות התעלות הן מידות פח

4. יש לאטום בסיליקון את פינות החיבור של תעלות מזוג אויר לפני כיפוף הפחים המתחברים

מפ- מפוח
מ.א.ק. - מפזר אוויר קירי
מ.א.ת. - מפזר אוויר תקרתי
ת.א.ח. - תריס אוויר חוזר
ת.א.צ. - תריס אוויר צח
ב.א. - בידוד אקוסטי
ב.ט. - בידוד טרמי
ג.ב. - ללא בידוד
ד.א. - דמפר אש

📖 סרמסטט לוח הפעלה
🏠 שקע חשמל לספוד יועץ חשמל
🏠 שקע תלת פאזי לספוד יועץ חשמל
📦 מפסק בטוחו חד פאזי לספוד יועץ חשמל
📦 מפסק בטוחו תלת פאזי לספוד יועץ חשמל
🔌 ניקוד מאיד לספוד יועץ אינסטלציה
📏 גובה 25 ס"מ מוחותית גובה המאיד
🔌 שלש הפעלה אלוטו

תעלות ותריסי אוויר חוזר	
תעלות ותריסי אספקת אוויר	
תעלות ותריסי אוויר צח	
תעלות ותריסי יניקת אוויר	
תעלות ותריסי שיחרור עשן	
צנרת גז וחשמל	
סימון מעגלי מיוזג אוויר	

[illegible]