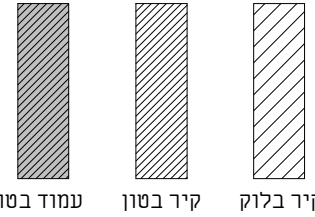


מתכונים:

ניהול פרויקט
מהיסוד - בן סולומון
פיקוח
מהיסוד - בן סולומון
קונסטרוקציה
ערן שילר
מיזוג אוויר
אייל ארז מהנדסים ויועצים בע"מ
אינסטלציה
איתן אלמסי
חשמל
איתן בסיס
אלומיניום
נוף
נתי בלוקא
חשמל חכם
חימום תת רצפתי
איטום
צבי טל
אקוסטיקה
מעליות
קרקע וביסוס
דיה הנדסת קרקע וביסוס
רישוי

[illegible]

מקרא קירות:

[illegible]

אדריכלות

CLIENT NAME: _____ שם המזמין:

קבוצת רכישה נופיה

PROJECT NAME: _____ שם הפרויקט:


נופיה - מגרש 7

DRAWING NAME: ס הגליון:

גליון שער

SHEET NUMBER: 190 גליון:

A3-1-100

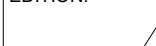SCALE:	קנה מידה:	EDITION:	חזרות:
STATUS:	סטוס		
למכר	נבדק ע"י:		רשט ע"י:
DATE:	22.09.25		תאריך:



NeumanHaynerArchitects

office@nh-arch.com
www.nh-arch.com

וימן חיינר אדריכלים
מורד ההדריס 2, בית חירות
טל 09-9545842

זכויות ייצור / ע"פ הנחיות עו"ד

נופיה - מגרש 7			
מס' גיליון	שם גיליון	מהדורה	תאריך הפצת מהדורה

22/09/2025	1	גליון שער	A3-1-100
22/09/2025	1	קומת קרקע	A3-1-101
22/09/2025	1	קומה א	A3-1-102
22/09/2025	1	גג	A3-1-103
22/09/2025	1	חזיתות 1	A3-2-200
22/09/2025	1	חזיתות 2	A3-2-201
22/09/2025	1	חתכים	A3-3-100
22/09/2025	1	גליון מדדגות	A3-4-100
22/09/2025	1	פרטים	A3-4-103
22/09/2025	1	פרטי פרגולה	A3-4-104
22/09/2025	1	רשימת פתחים	A3-6-1000



מתכונים:

ניהול פרויקט
מהיסוד - בן סולומון
פיקוח
מהיסוד - בן סולומון
קונסטרוקציה
ערן שילר
מיזוג אוויר
אייל ארז מהנדסים ויועצים בע"מ
אינסטלציה
איתן אלמסי
חשמל
איתן בסיס
אלומיניום
נוף
נתי בלוקא
חשמל חכם
חימום תת רצפתי
איטום
צבי טל
אקוסטיקה
מעליות
קרקע וביסוס
דיה הנדסת קרקע וביסוס
רישוי


[illegible]

מקרא קירות:

		
עמוד בטון	קיר בטון	קיר בלוק

[illegible]


אדריכלות

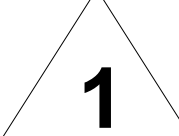CLIENT NAME:	המחיר: 0	
קבוצת רכישה נופיה		
PROJECT NAME:	הפרטים:	
נופיה - מגרש 7		
DRAWING NAME:	השם הכללי:	
קומת קרקע		
SHEET NUMBER:	מספר העליון:	
A3-1-101		
SCALE:	קנה מידה:	EDITION:
1 : 50		הדורה:
STATUS:	סטוס:	
למכר	בכרע עיני:	
DATE:	22.09.25	
	היום:	

NeumanHaynerArchitects

יומן חיינר אדריכלים
בית חירות 2, יוור ההדרים
09-9545842

office@nh-arch.com
www.nh-arch.com

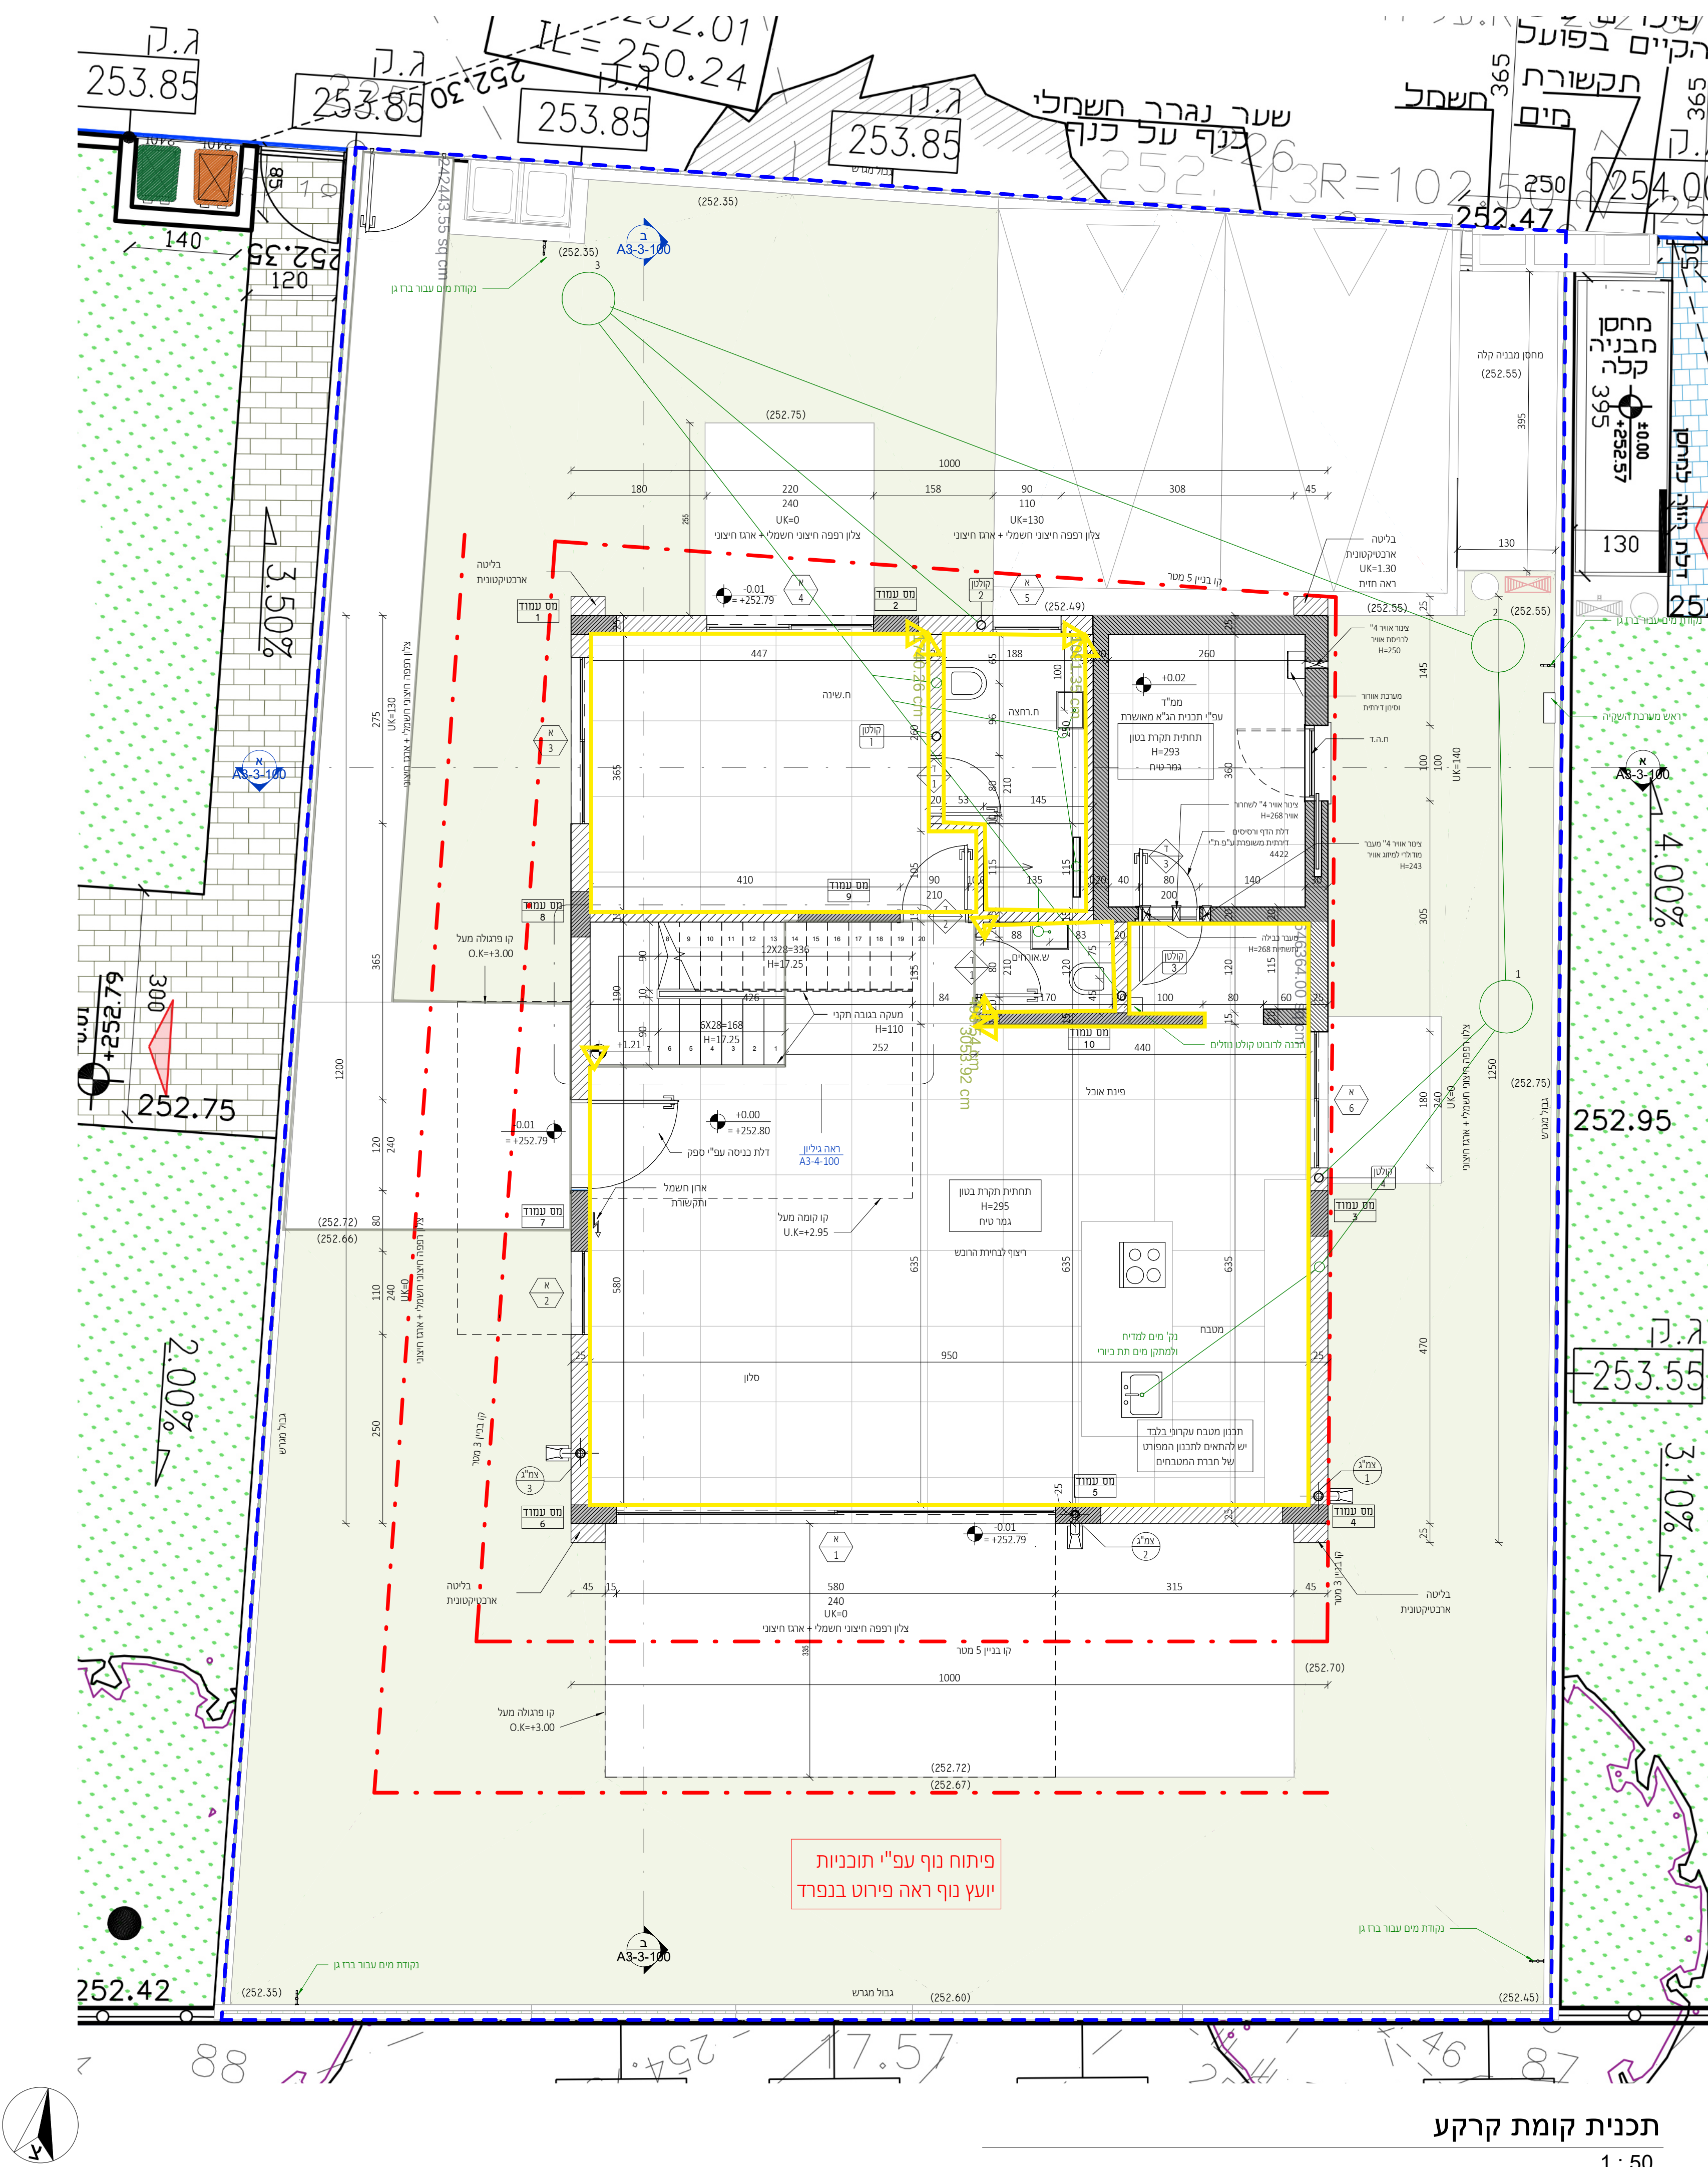

הערות:

1. יש לעבוד במקביל לתכניות יועצים המאושרות על ידי האדריכל.
2. פרטי ספי חלון - עפ"י חוברת אלומיניום של הספק הנבחר ובתיאום מול אדריכל.
3. חימום תת רצפתי (במידה ויש במגרש זה) עפ"י פרטי הספק ובתיאום מול אדריכל.
4. יש לעבוד במקביל לתכניות עיצוב פנים (במידה ויש מעצב פנים במגרש זה) המאושרות על ידי האדריכל.
5. באחריות הקבלן לעדכן את האדריכל על אי התאמה בין התכניות יועצים לאדריכלות.
6. כל הדלתות לפי מפרט מצורף.
7. כל אלמנטי הבטון יקבלו התייחסות תרמית לפי הנחיות יועץ.
8. פרטי איטום, בידוד וניקוז עפ"י תכניות יועצים ובאחריות הקבלן.

ניהול פרויקט
 מהיסוד - בן
 פיקוח
 מהיסוד - בן
 קונסטרוקציה
 ערן שילר
 מיזוג אוויר
 אייל ארז מה
 אינסטלציה
 איתן אלמסי
 חשמל
 איתן בסיס
 אלומיניום

איטום	_____
צבי טל	_____
אקוסטיקה	_____
מעליות	_____
קרקע וביסוס	_____
דיה הנדסת קרקע וביסוס	_____
רשוי	_____

[illegible]

אדריכלות	
CLIENT NAME:	המסין
קבוצת רכישה נופיה	
PROJECT NAME:	הפרויקט
נופיה - מגרש 7	
DRAWING NAME:	התכנון
קומה א	
SHEET NUMBER:	פר 2 מיליון
A3-1-102	

קומה א


מדידה:

22.09.25



ימן חיינר אדריכלים
 ורד ההדסים 2, בית חירות
 ל 09-9545842

זכריות ייצור / ע"פ הנחיות עו"ד

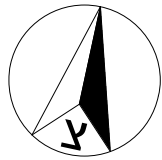

1 : 50

1. יש לעבוד במקביל לתכניות יועצים המאושרות על ידי האדריכל.
2. פרטי ספי חלון - עפ"י חוברת אלומיניום של הספק הנבחר ובתיאום מול אדריכל.
3. חימום תת רצפתי (במידה ויש במגרש זה) עפ"י פרטי הספק ובתיאום מול אדריכל.
4. יש לעבוד במקביל לתכניות עיצוב פנים (במידה ויש מעצב פנים במגרש זה) המאושרות על ידי האדריכל.
5. באחריות הקבלן לעדכן את האדריכל על אי התאמה בין התכניות יועצים לאדריכלות.
6. כל הדלתות לפי מפרט מצורף.
7. כל אלמנטי הבטון יקבלו התייחסות תרמית לפי הנחיות יועץ.
8. פרטי איטום, בידוד וניקוז עפ"י תכניות יועצים ובאחריות הקבלן.

מתכננים:

ניהול פרויקט
מהיסוד - בן סולמון
פיקוח
מהיסוד - בן סולמון
קונסטרוקציה
ערן שילר
מיזוג אוויר
אייל ארז מהנדסים ויועצים בע"מ
אינסטלציה
איתן אלמסי
חשמל
איתן בסיס
אלומיניום
נוף
נתי בלוקא
חשמל חכם
חימום תת רצפתי
איטום
צבי טל
אקוסטיקה
מעליות
קרקע וביסוס
דיה הנדסת קרקע וביסוס
רישוי


± 0.00 = +252.80	
הערות: 1. תכנית זו יש לקרוא יחד עם תכנית הרישום. 2. גובה אבטומטי - ראו תכנית פיתוח. 3. הפרדות הן בין קירות הבניה ולא כולל פיתוח. 4. פיתוח השטח סביב הבנויה, כולל, מדרגות, נדרות, שבילים, ריצופים, שפכים, גדרים, חניה וגן ראו תכנית פיתוח. 5. איטום קירות ורצפות הבנויה כמעט עם הקרקע ובידוד חרסי לאורך העמודים והקורות וכל המפרדות. כליות או עם סימני גימון - ראו תכנית קונסטרוקציה. 6. אף דום יבוצע בכל מישור אופקי הבולם מהבנויה. 7. ס"ח חרסי במסגרת - ע"פ מפרט חומרים, מאושר ע"י פיקוח הנדסי.	
המבצע אחראי למידות : עליו לבקר ולבדוק את כל המידות בתכנית ובקטע הנבדק. במסגרת של מידות או אי התאמה בתכנית /או בבנויה, עליו להודיע על כך מיד לאדריכל בסיום המשיך הנבדק. המבצע יחשמש או ויקי בתכנית שאושרו לביצוע. המבצע יחזיק באחריות, בכל שלב, של מידות של תכנית. אין לקבוע מידות על ידי חריזה בשטח. התכנית הנה רישום האדריכלי ואין לשנות כל שימוש בה או ברעיונות הגולמים בה, אלא באישור כותב מהאדריכל. חומרים /או יושם אשר שמו רשום בתכנית זו, ושם לבד באחריות המבצעת והמקבלת לתכנית. על המפקח והמקבל לודא התאמת התכנית האדריכלית ל"ביצוע" לתכנית זוהי, המפרט התכנית והאשרות ע"י כל הגורמים הרשמיים. התכנית כוללת את כל האחריות והידוע על ליום תחלתה.	
משרד קירות:	
קיר בלוק קיר בסון עמוד בסון	
<table><tr><td>תאריך</td><td>22/09/2025</td><td>תיאור</td><td>מכרז</td><td>מהדורה</td><td>1</td></tr><tr><td></td><td></td><td></td><td></td><td></td><td></td></tr><tr><td></td><td></td><td></td><td></td><td></td><td></td></tr><tr><td></td><td></td><td></td><td></td><td></td><td></td></tr><tr><td></td><td></td><td></td><td></td><td></td><td></td></tr><tr><td></td><td></td><td></td><td></td><td></td><td></td></tr><tr><td></td><td></td><td></td><td></td><td></td><td></td></tr><tr><td></td><td></td><td></td><td></td><td></td><td></td></tr><tr><td></td><td></td><td></td><td></td><td></td><td></td></tr><tr><td></td><td></td><td></td><td></td><td></td><td></td></tr><tr><td></td><td></td><td></td><td></td><td></td><td></td></tr><tr><td></td><td></td><td></td><td></td><td></td><td></td></tr></table>	תאריך	22/09/2025	תיאור	מכרז	מהדורה	1	
תאריך	22/09/2025	תיאור	מכרז	מהדורה	1	

אדריכלות

שם המסמך:	CLIENT NAME:
קבוצת רכישה נופיה	
שם הפרויקט:	PROJECT NAME:
נופיה - מגרש 7	
שם הגיליון:	DRAWING NAME:
חזיתות 1	
מספר גיליון:	SHEET NUMBER:
A3-2-200	
תאריך:	EDITION:
22.09.25	קנה מידה: 1 : 50
שורש ע"י:	סטוס: למכרז
תאריך:	נבדק ע"י:
22.09.25	


פיתוח נוף עפ"י תוכניות יועץ נוף ראה פירוט בנפרד

פיתוח נוף עפ"י תוכניות יועץ נוף ראה פירוט בנפרד

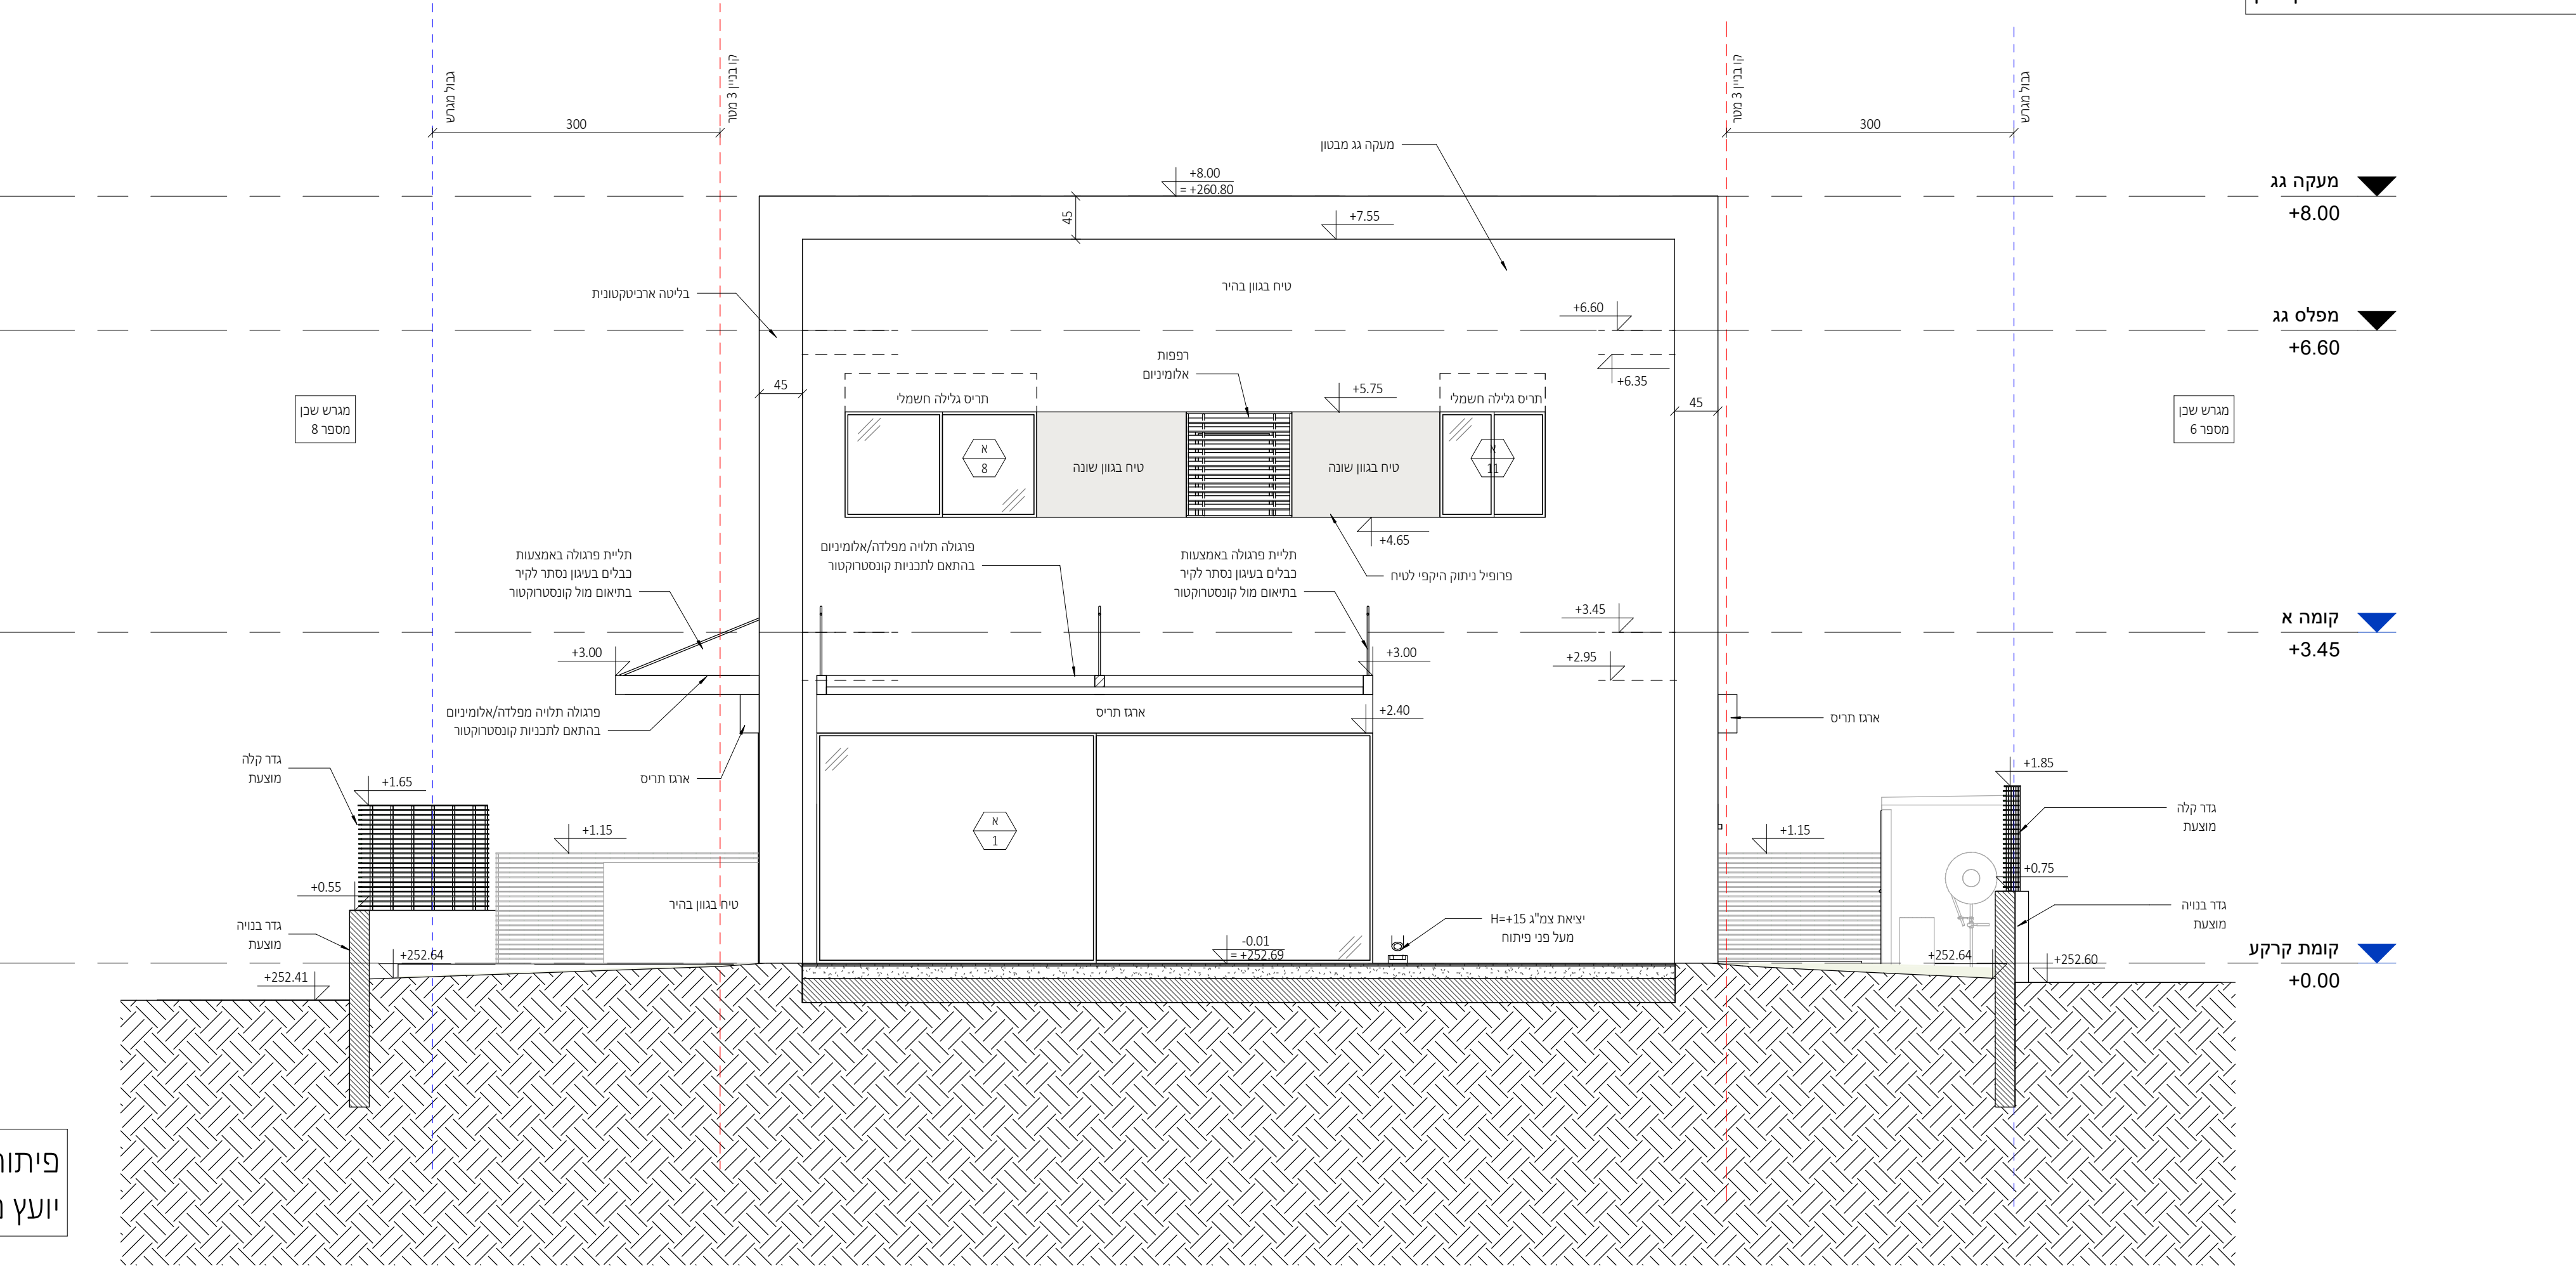

חזית דרומית

1 : 50

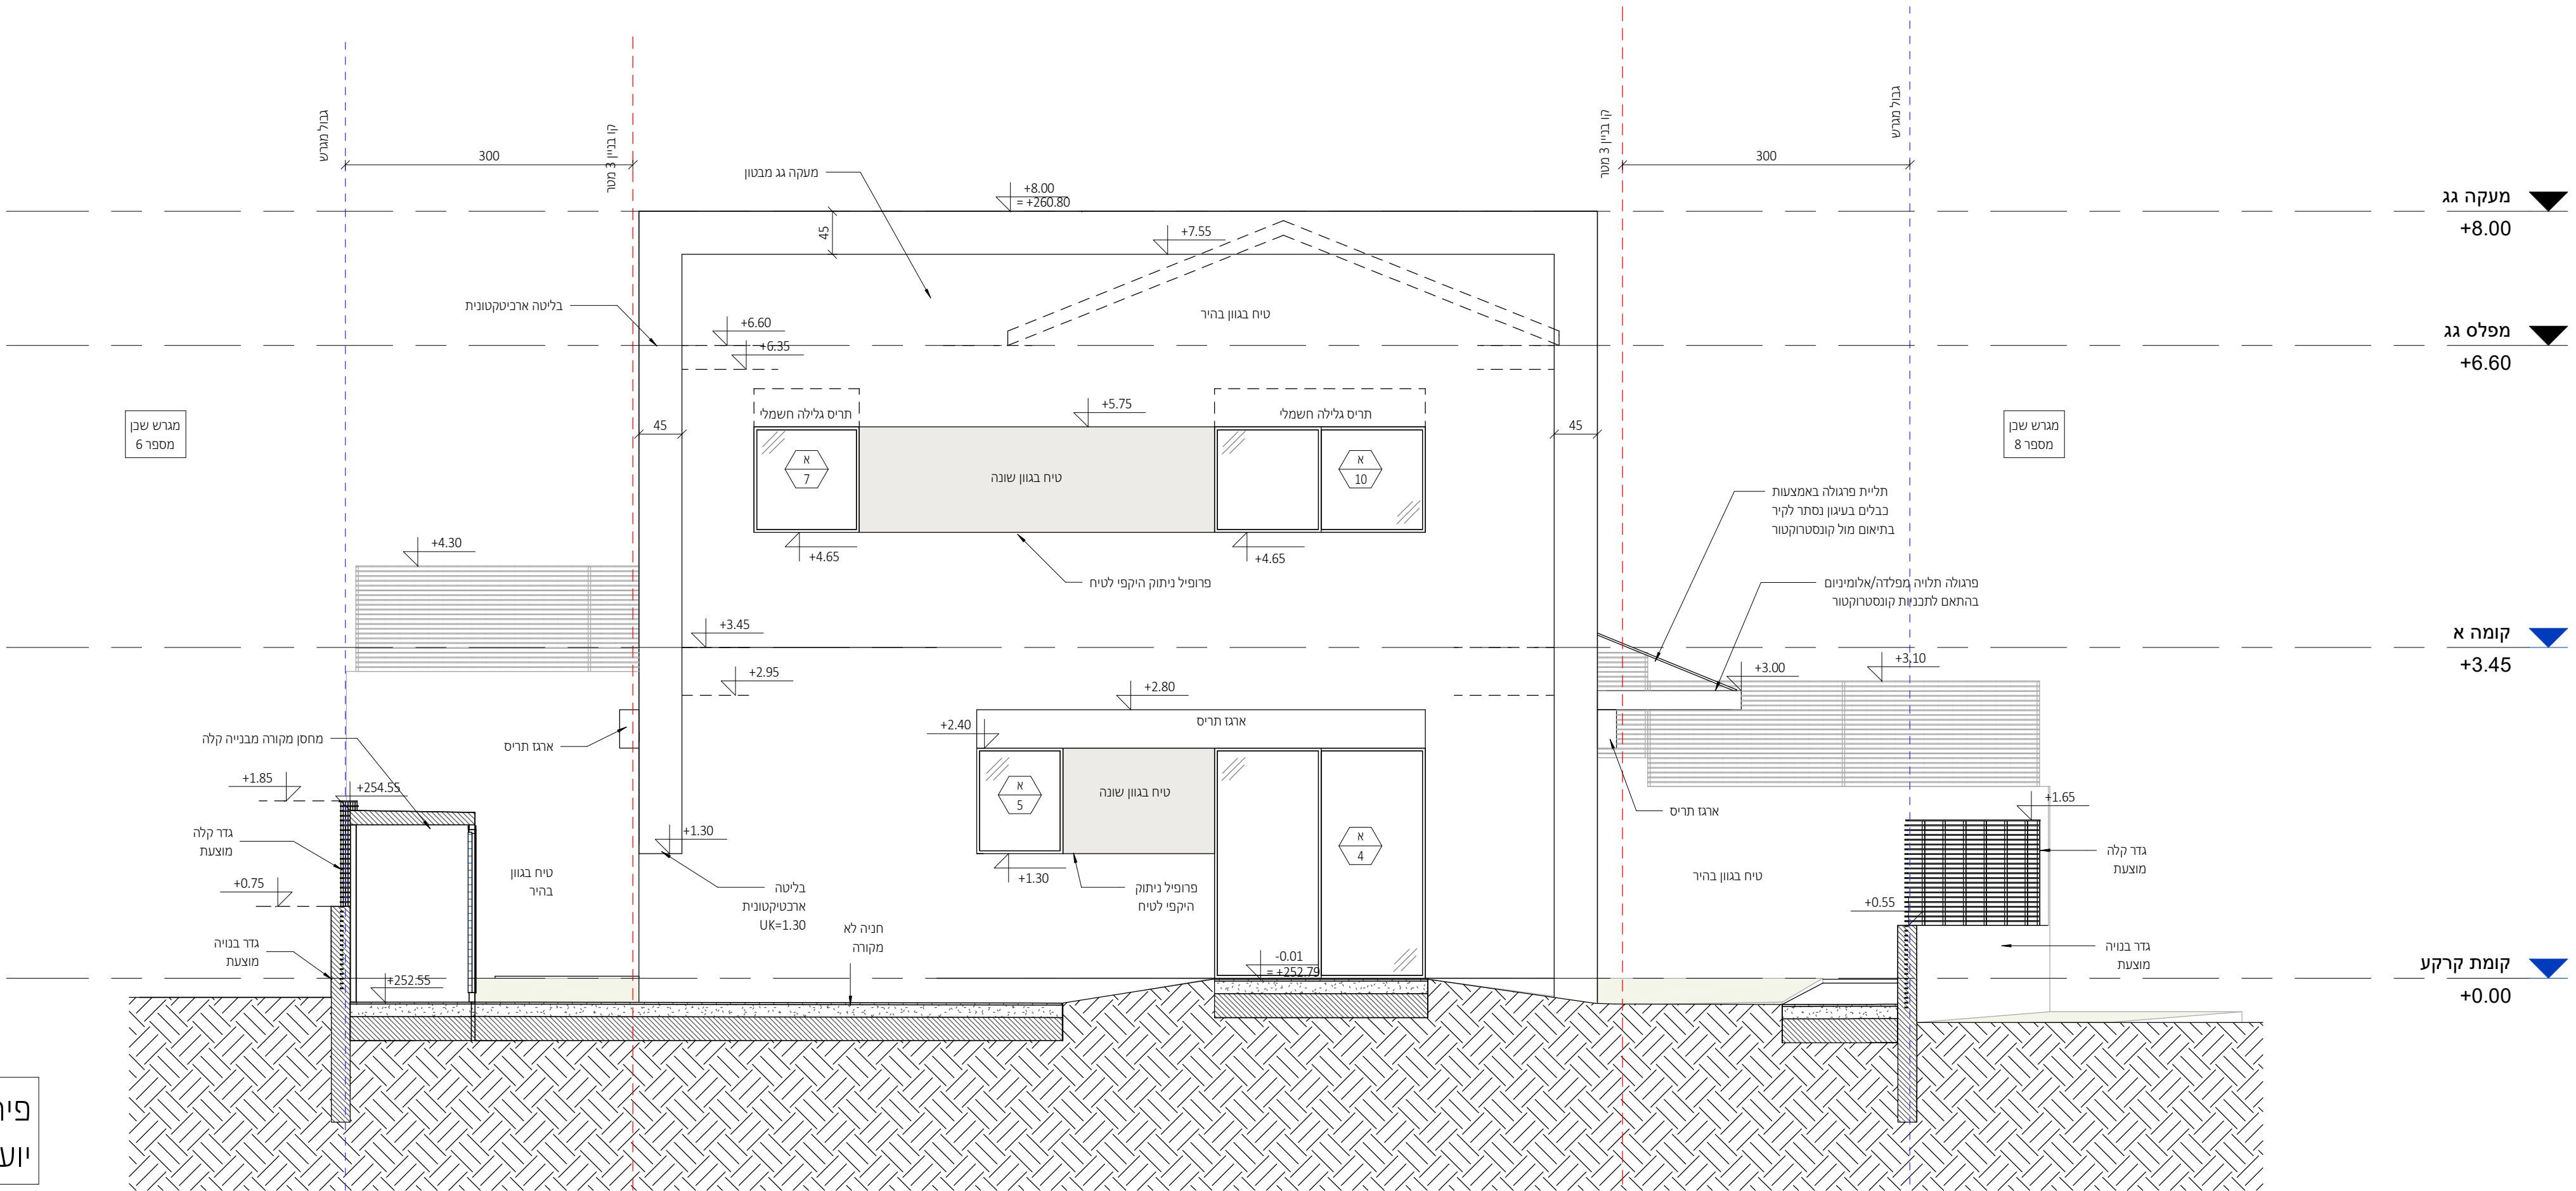

חזית צפונית

1 : 50

פרטי איטום, בידוד וניקוז עפ"י תכניות יועצים ובאחריות הקבלן

מתכונים:

ניהול פרויקט
מהיסוד - בן סולומון
פיקוח
מהיסוד - בן סולומון
קונסטרוקציה
ערן שילר
מיזוג אוויר
אייל ארז מהנדסים ויועצים בע"מ
אינסטלציה
איתן אלמסי
חשמל
איתן בסיס
אלומיניום
נוף
נתי בלוקא
חשמל חכם
חימום תת רצפתי
איטום
צבי טל
אקוסטיקה
מעליות
קרקע וביסוס
דיה הנדסת קרקע וביסוס
רישוי

[illegible][illegible]

אדריכלות

PROJECT NAME:		שם הפרויקט:	
DRAWING NAME:		שם הנגזרת:	
SHEET NUMBER:		מספר גליון:	
SCALE:		קנה מידה:	
TATUS:		סטוס	
DATE:		תאריך:	

קבוצת רכישה נופיה

נופיה - מגרש 7

חזיתות 2

A3-2-201

1 : 50

למכר

נבדק ע"י:


EDITION:

1

ודסס ע"י:

NeumanHaynerArchitects


office@nh-arch.com
www.nh-arch.com

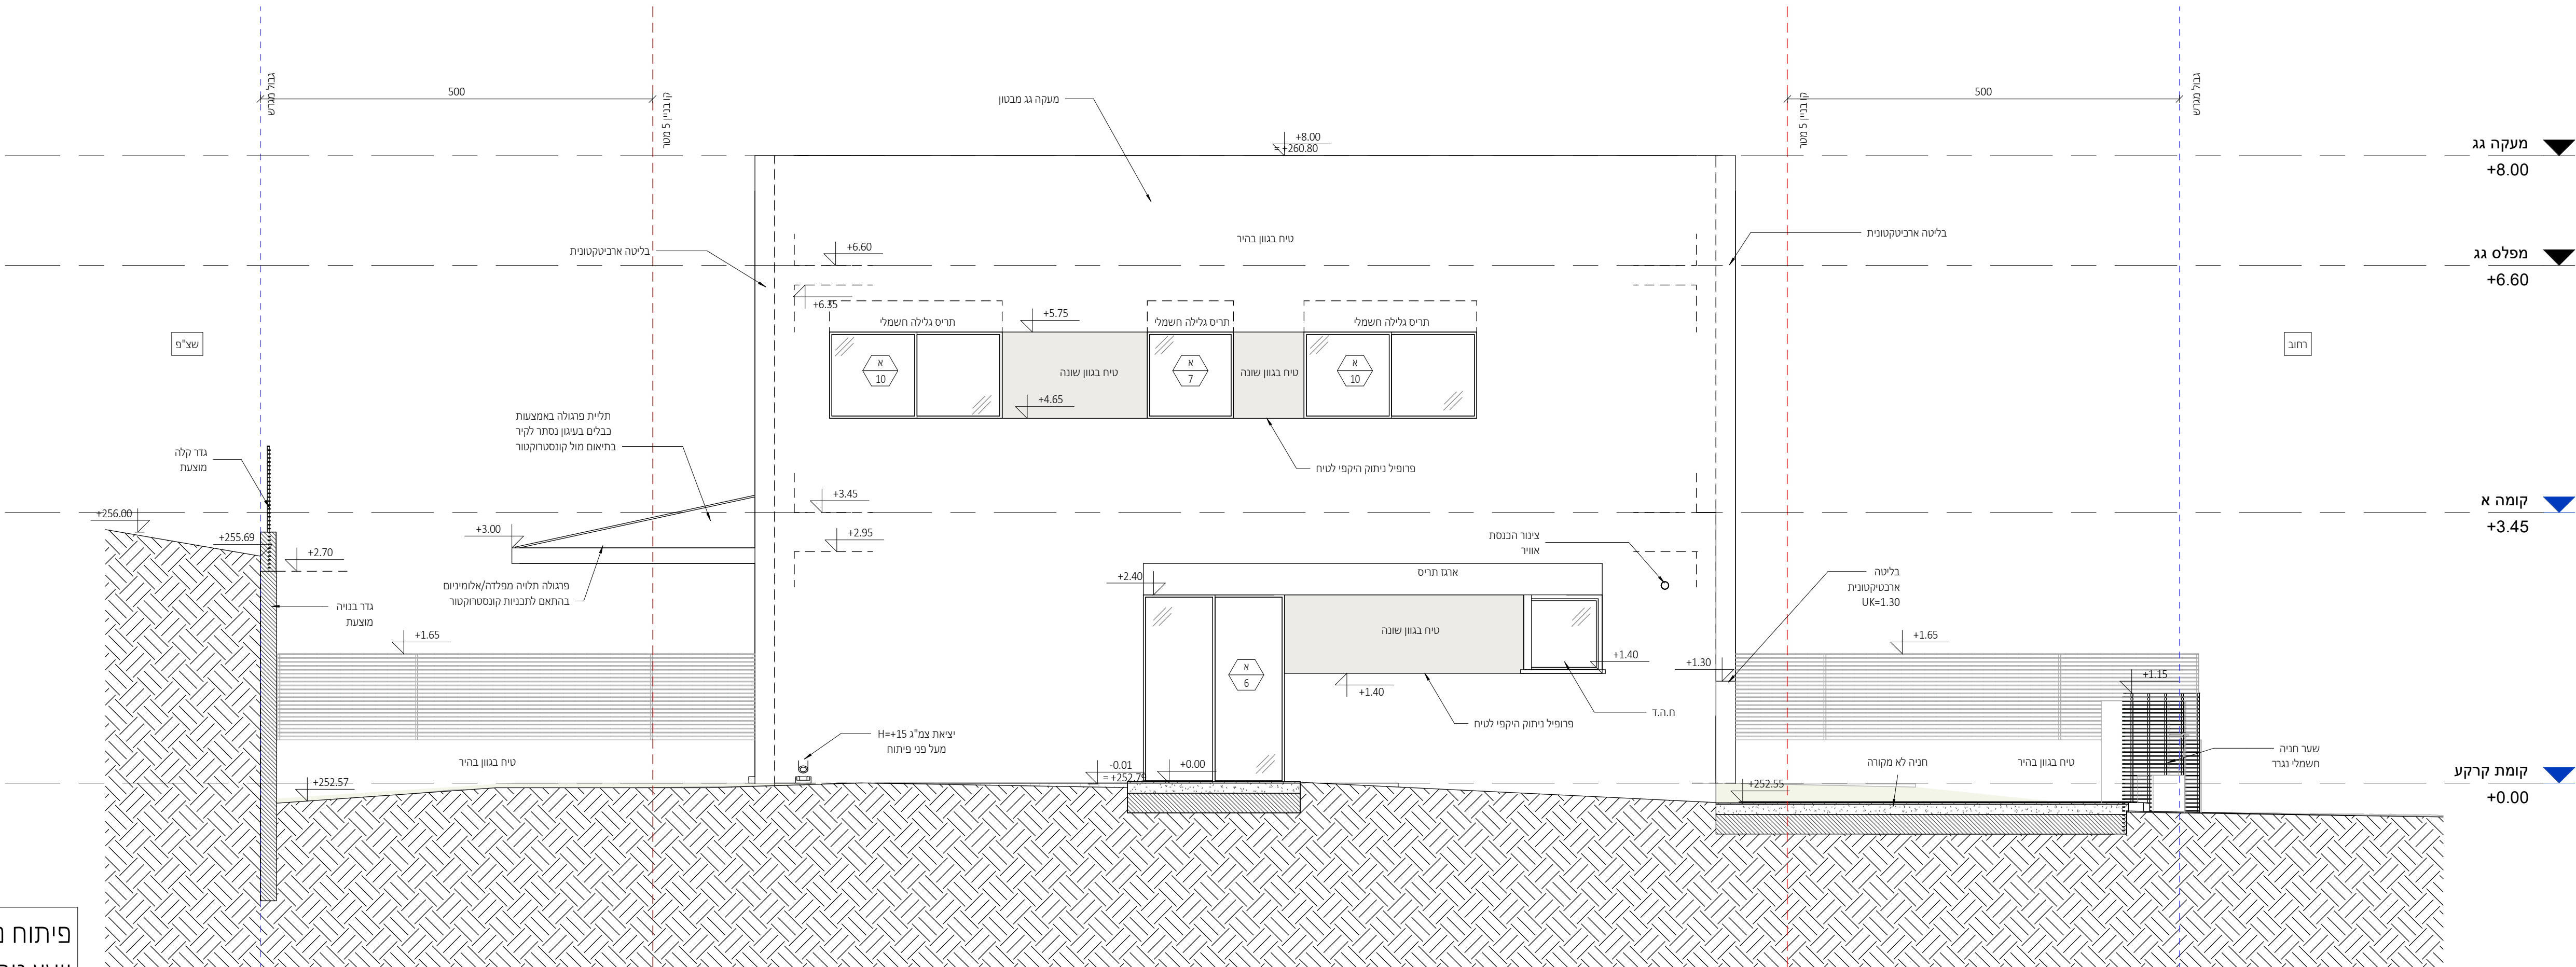

פיתוח נוף עפ"י תוכניות
יועץ נוף ראה פירוט בנפרד

חזית מזרחית

1 : 50

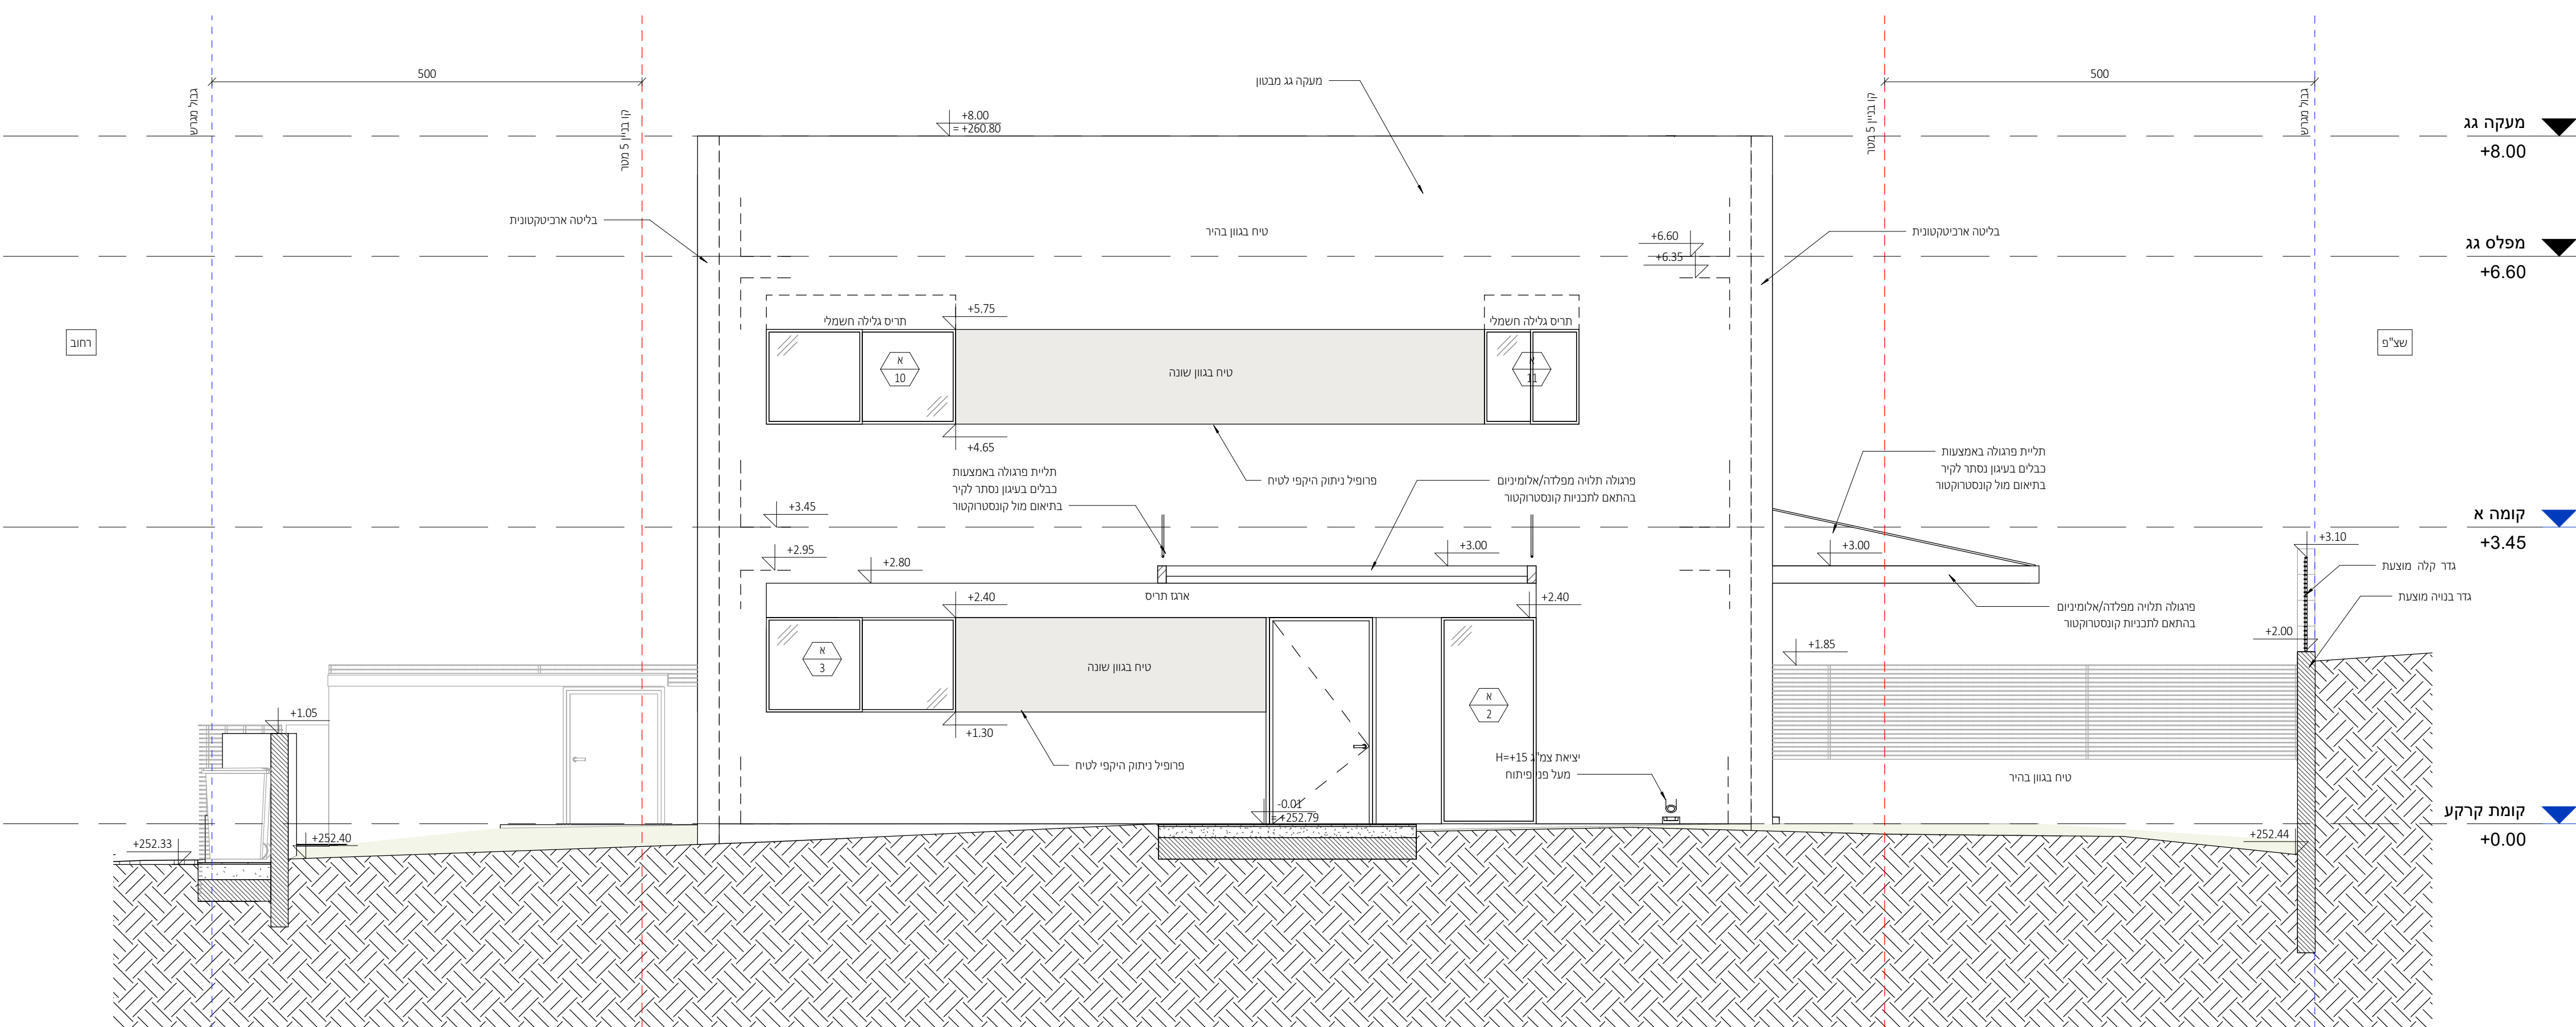


פיתוח נוף עפ"י תוכניות
יועץ נוף ראה פירוט בנפרד

חזית מערבית


1 : 50

פרטי איטום, בידוד וניקוז עפ"י תכניות יועצים ובאחריות הקבלן

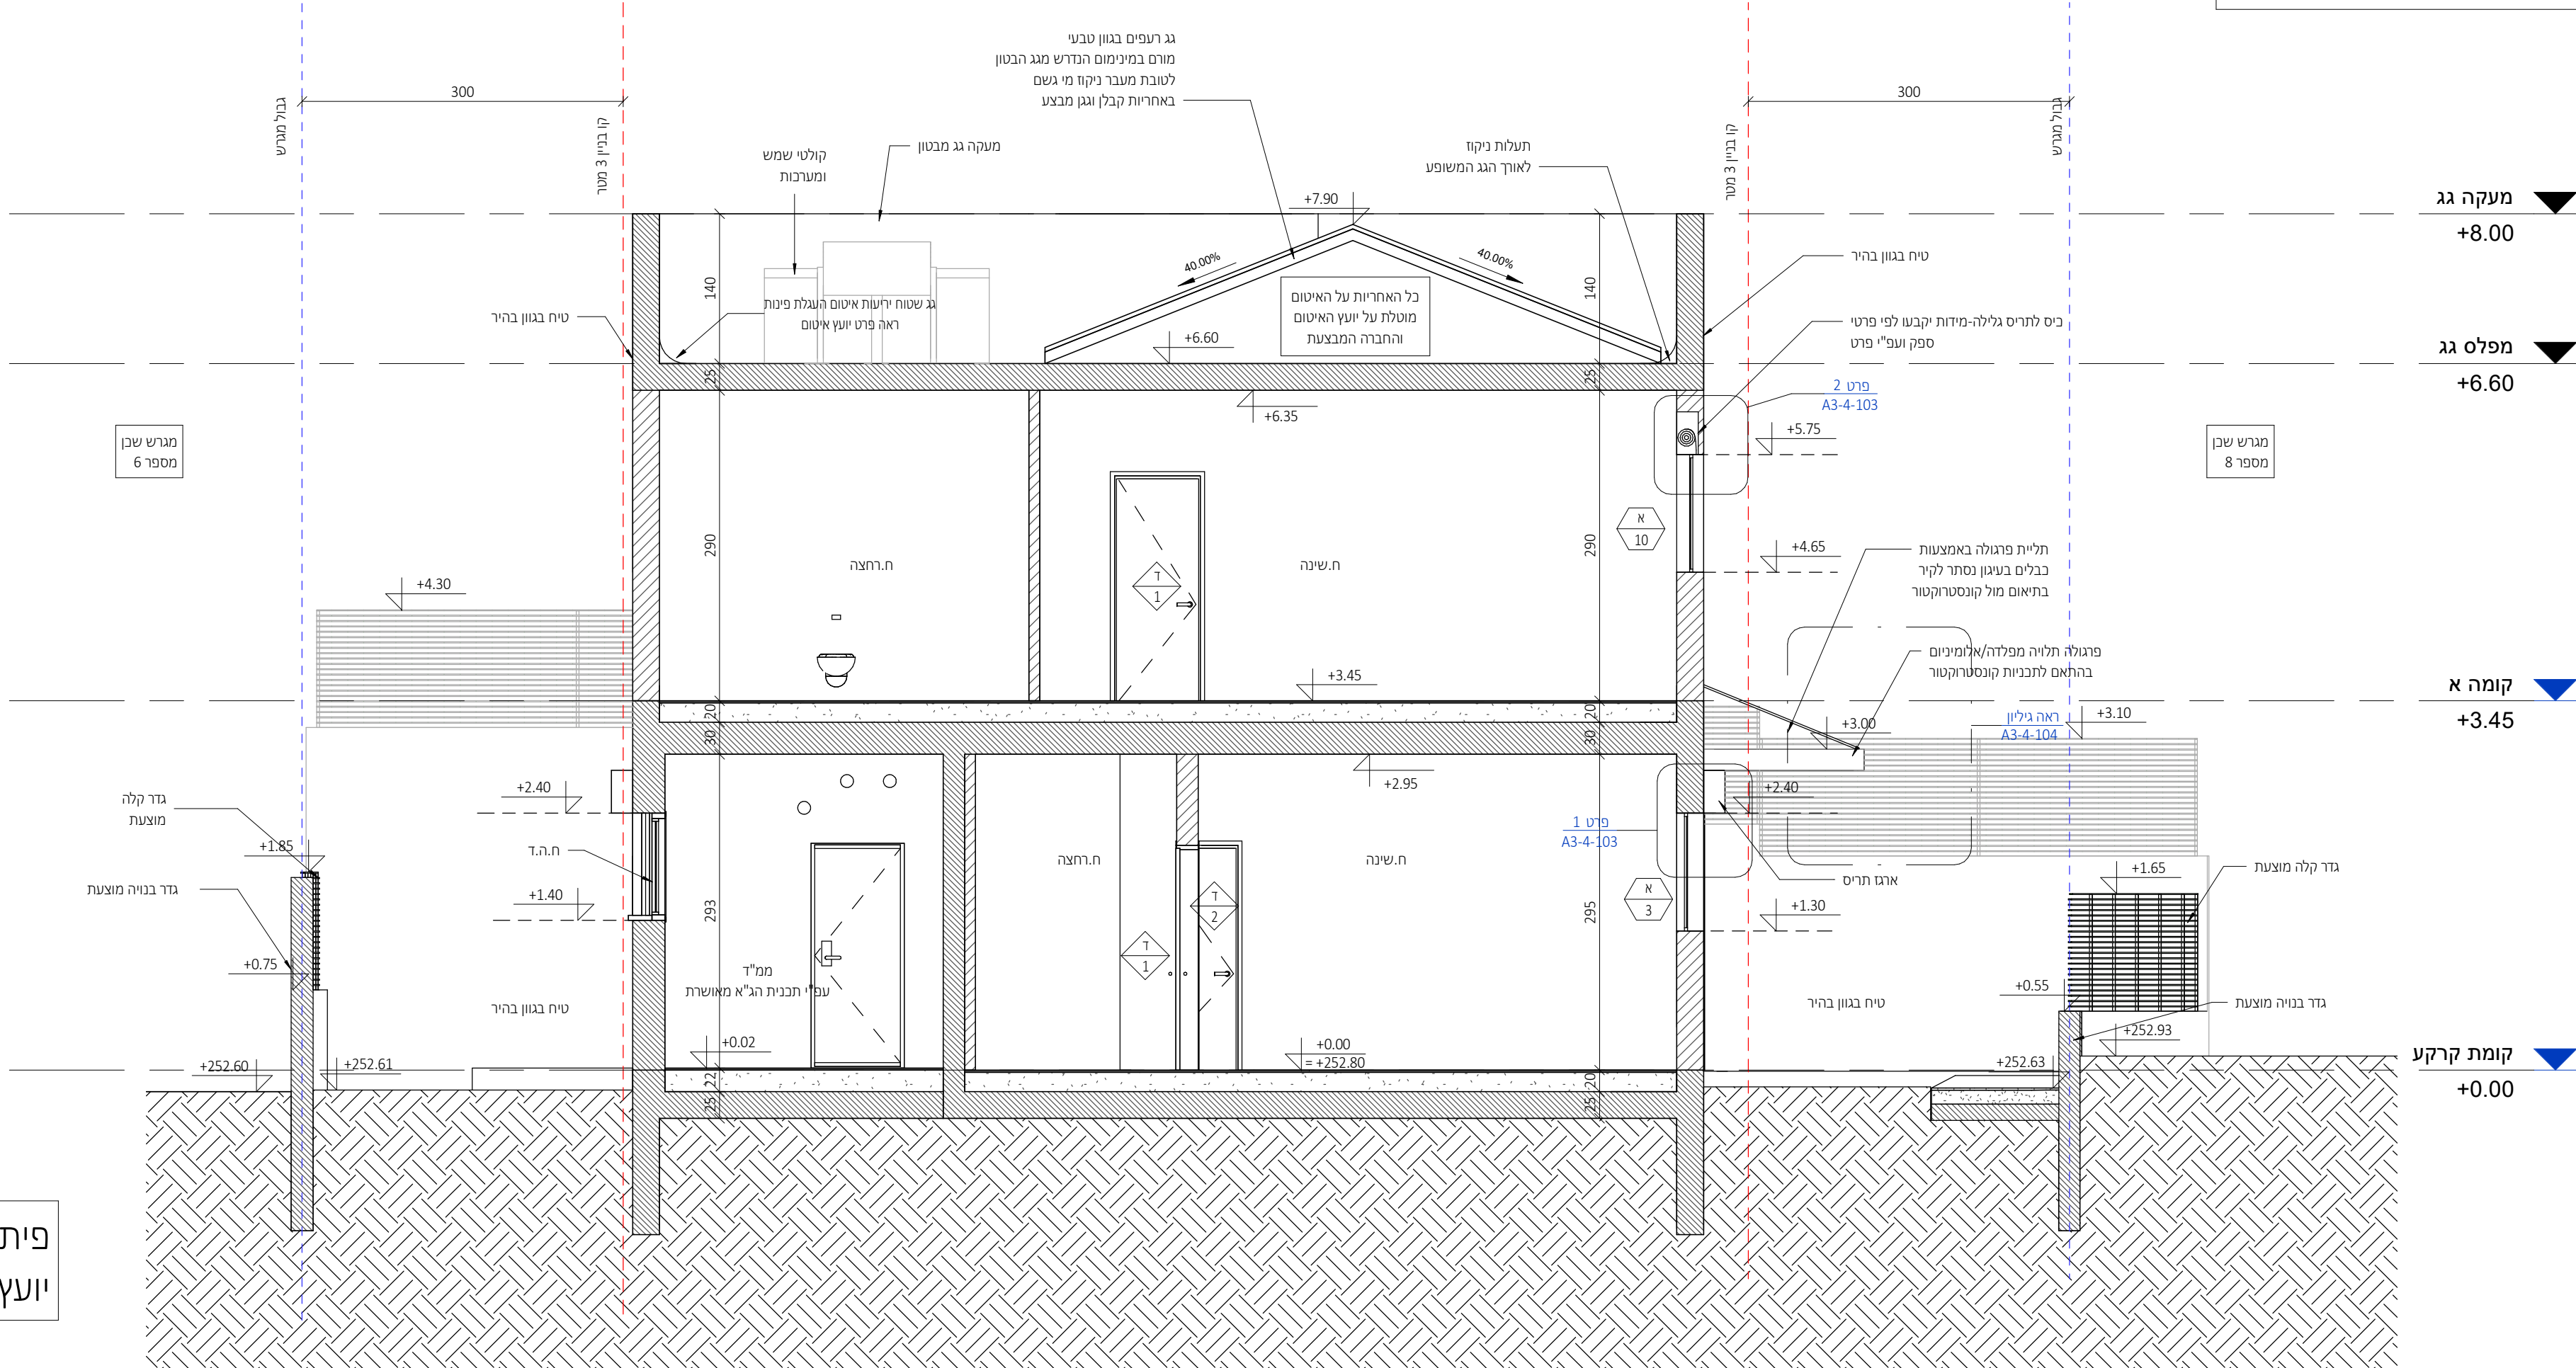

פיתוח נוף עפ"י תוכניות
יועץ נוף ראה פירוט בנפרד

חתך א-א

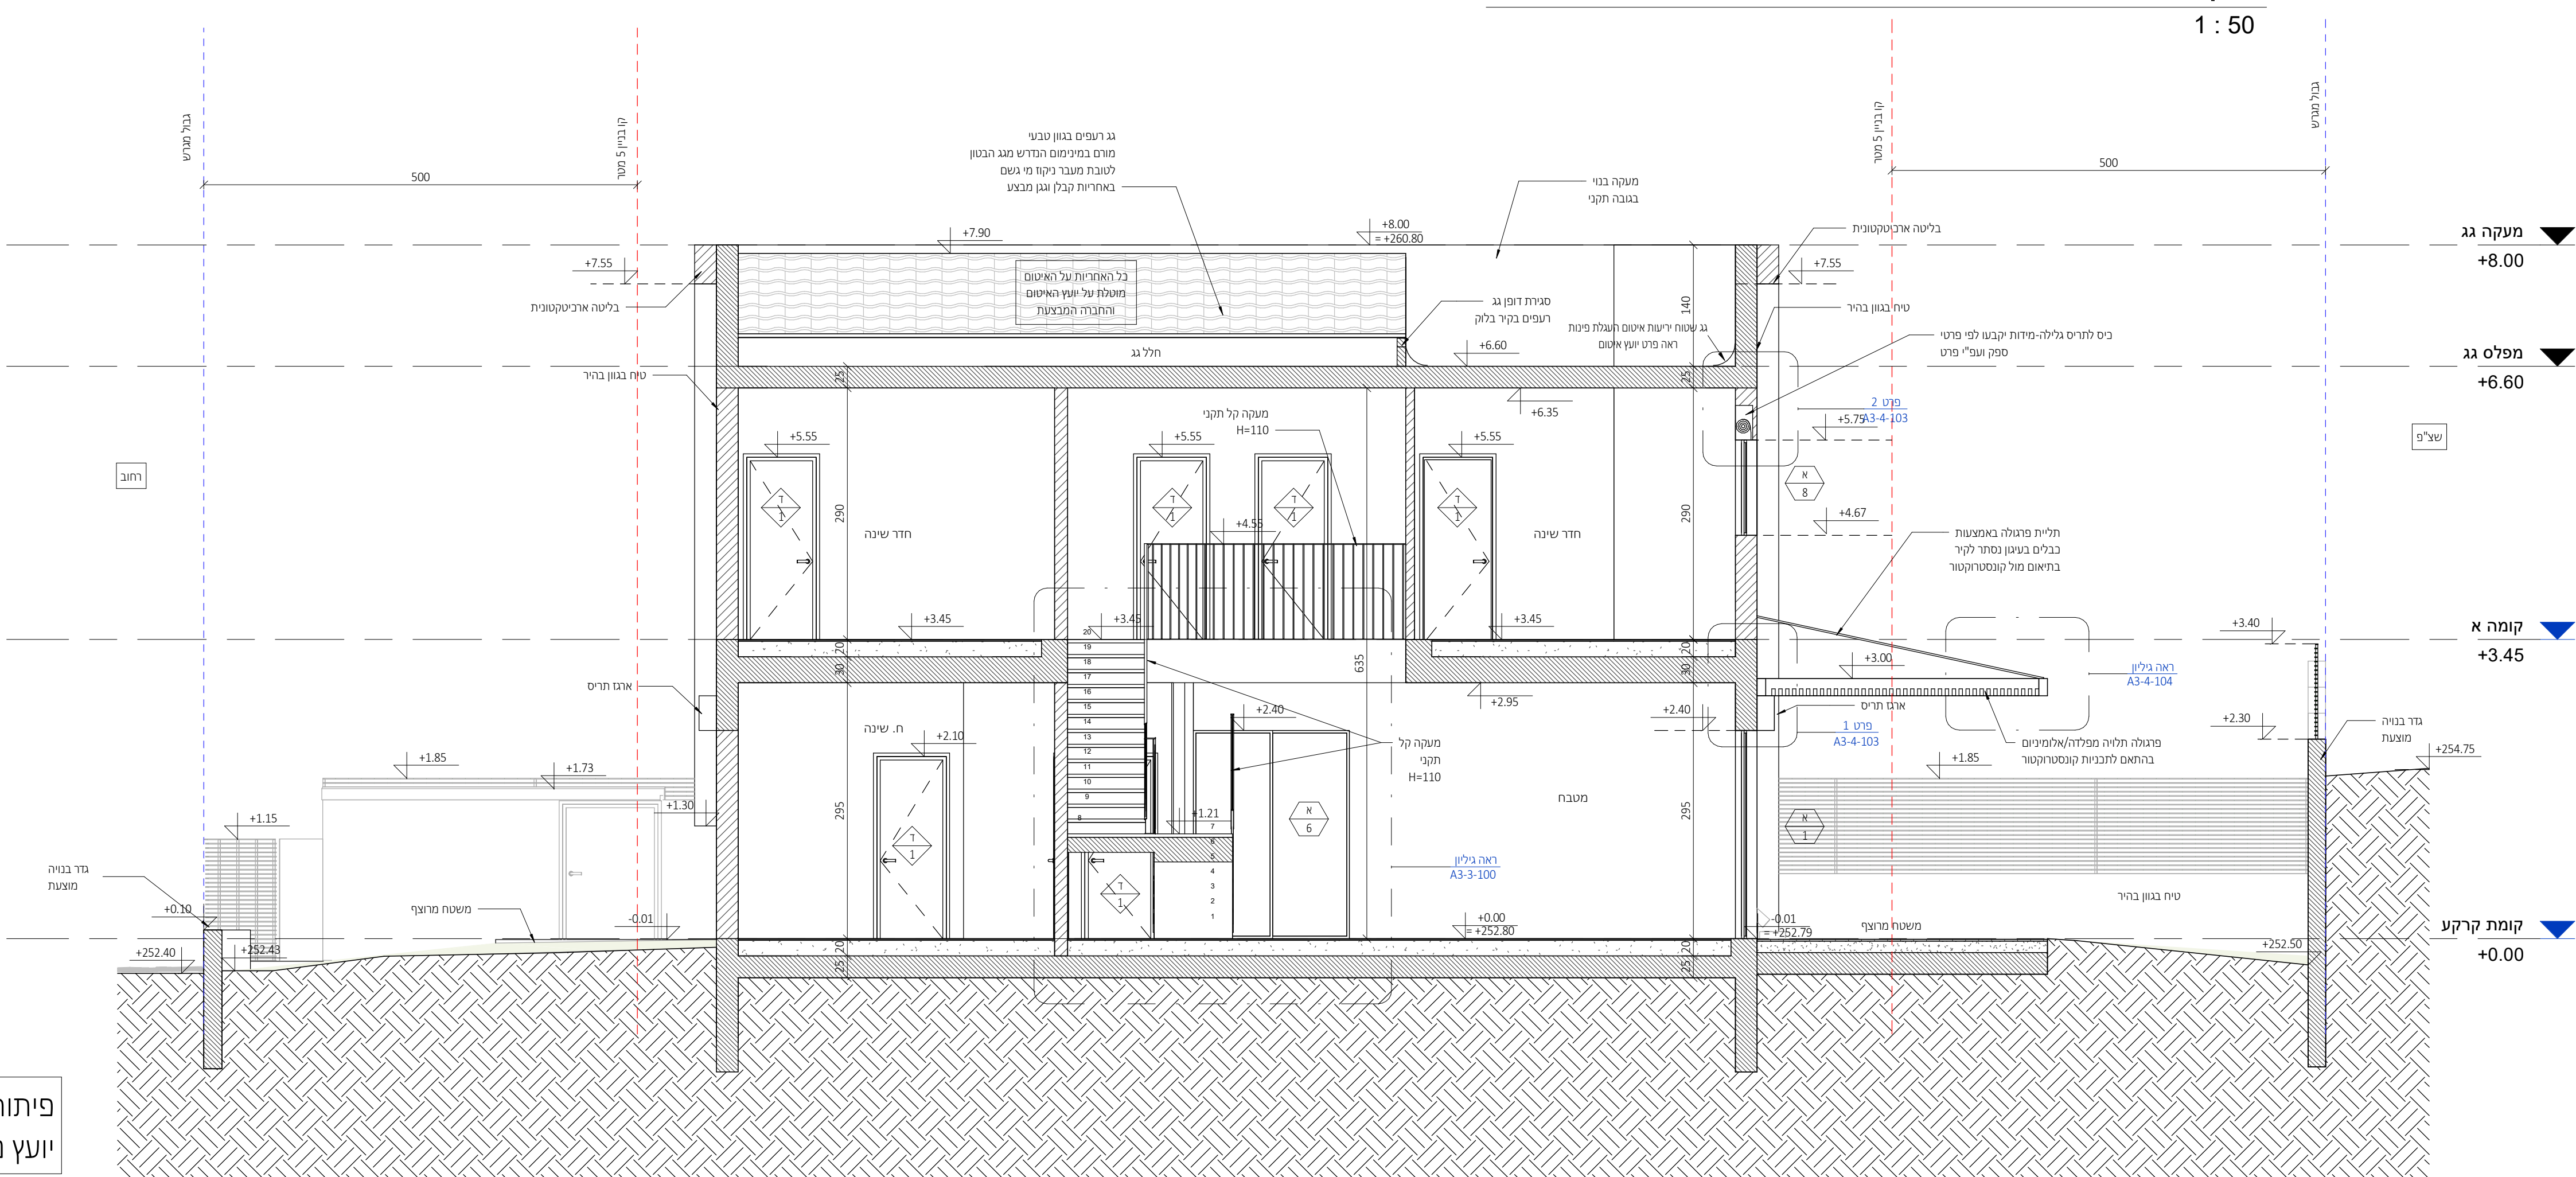

חתך ב-ב


1 : 50

מתכונים:


ניהול פרויקט
מהיסוד - בן סולמון
פיקוח
מהיסוד - בן סולמון
קונסטרוקציה
ערן שילר
מיזוג אוויר
אייל ארז מהנדסים ויועצים בע"מ
אינסטלציה
איתן אלמסי
חשמל
איתן בסיס
אלומיניום
נוף
נתי בלוקא
חשמל חכם
חימום תת רצפתי
איטום
צבי טל
אקוסטיקה
מעליות
קרקע וביסוס
דיה הנדסת קרקע וביסוס
רישוי

[illegible]

מקרא קירות:

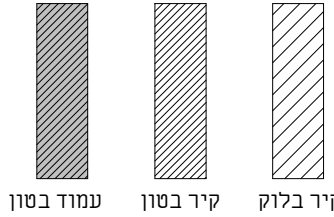[illegible]

אדריכלות

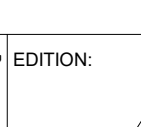LIENT NAME:		החומר:	
קבוצת רכישה נופיה			
PROJECT NAME:		הפרויקט:	
נופיה - מגרש 7			
DRAWING NAME:		התכנית:	
חתיכים			
SHEET NUMBER:		הפרט לגיליון:	
A3-3-100			
SCALE:	קנה מידה:	EDITION:	הדורה:
1 : 50			
STATUS:	סטוס		
למכר			
	נבדק עדי:		סטוס עדי:
DATE:	22.09.25		איר:

NeumanHaynerArchitects

office@nh-arch.com
www.nh-arch.com

זכויות ייצור / ע"פ הנחיות עו"ד

מתכננים:

ניהול פרויקט
מהיסוד - בן סולומון
פיקוח
מהיסוד - בן סולומון
קונסטרוקציה
ערן שילר
מיזוג אוויר
אייל ארז מהנדסים ויועצים בע"מ
אינסטליציה
איתן אלמסי
חשמל
איתן בסיס
אלומיניום
נוף
נתי בלוקא
חשמל חכם
חימום תת רצפתי
איטום
צבי טל
אקוסטיקה
מעליות
קרקע וביסוס
דיה הנדסת קרקע וביסוס
רישוי


± 0.00 = +252.80
הערות: 1. תכנית זו יש לקרוא יחד עם תכנית הרושמים. 2. גובה אבטומילר: ראו תכנית פיתוח. 3. המידות הן בין קירות הבניה ולא כולל פיתוח. 4. פיתוח השטח סביב הבנינה, כולל, מדרגות, גדרות, שביכים, ריצופים, שיפועים וכו'. 5. איטום קירות ורצפות הבניה כמעט עם הקרקע ובנידוד חתכי לאורך העמודים והקירות של חלל הבניה. כלירות אלו עם סימני גימון. ראו תכנית קונסטרוקציה. 6. אף מים יבוצע בכל מישור אופקי הבולם בחתבין. 7. סוף חתכי במסלול ע"פ מפרט החומרים. מאפשר טיי פיקוד העורף. הבצע אחראי לסידור: עליו לבקר ולבדוק את כל המידות בתכנית ובמקום הבנינה. במקום של שטח או אי התאמה בתכנית /או בבנין, עליו להודיע על כך מיד לאדריכל בסדר המשיך בעבודתו. התכנית יושמט או ויק תוכניתו שאפשר לביצוע. המבצע יחזיק באחריות, לכל מה, של שטח או של תכנית. אין לקבוע מידות על ידי חזירה בשטח. התכנית הנה תכנית האדריכל ואין לשנות כל שימוש בה או ברעיונות הגלומים בה, אלא באישור בכתב מהאדריכל. המבצע יחזיק באחריות, ויש לשלם עבור כל שימוש בתכנית זו, ויש לשלם באחריות על התפקוד והשקלן ליוזא התאמה התכנית האדריכלית לביצוע. לתכנית זו, תכנית התכנית והאישור יש" כל גורמים ורושמים. התכנית כוללת את כל האחריות והידוע על ליום התאמה.

משרד קירות:
קיר בלוק קיר בטון עמוד בטון

תאריך	תיאור	מהדורה
22/09/2025	מכרז	1


אדריכלות
שם המסמך:
קבוצת רכישה נופיה
שם הפרויקט:
נופיה - מגרש 7
שם הגיליון:
גליון מדרגות
מספר גליון:
A3-4-100
תאריך:
22.09.25

NeumanHaynerArchitects
נירן חיינר אדריכלים מודד והנדס 2, בית היריות 09-9545842 78 office@nh-arch.com www.nh-arch.com
זכיות יימור / ע"פ הנחיות ע"ד

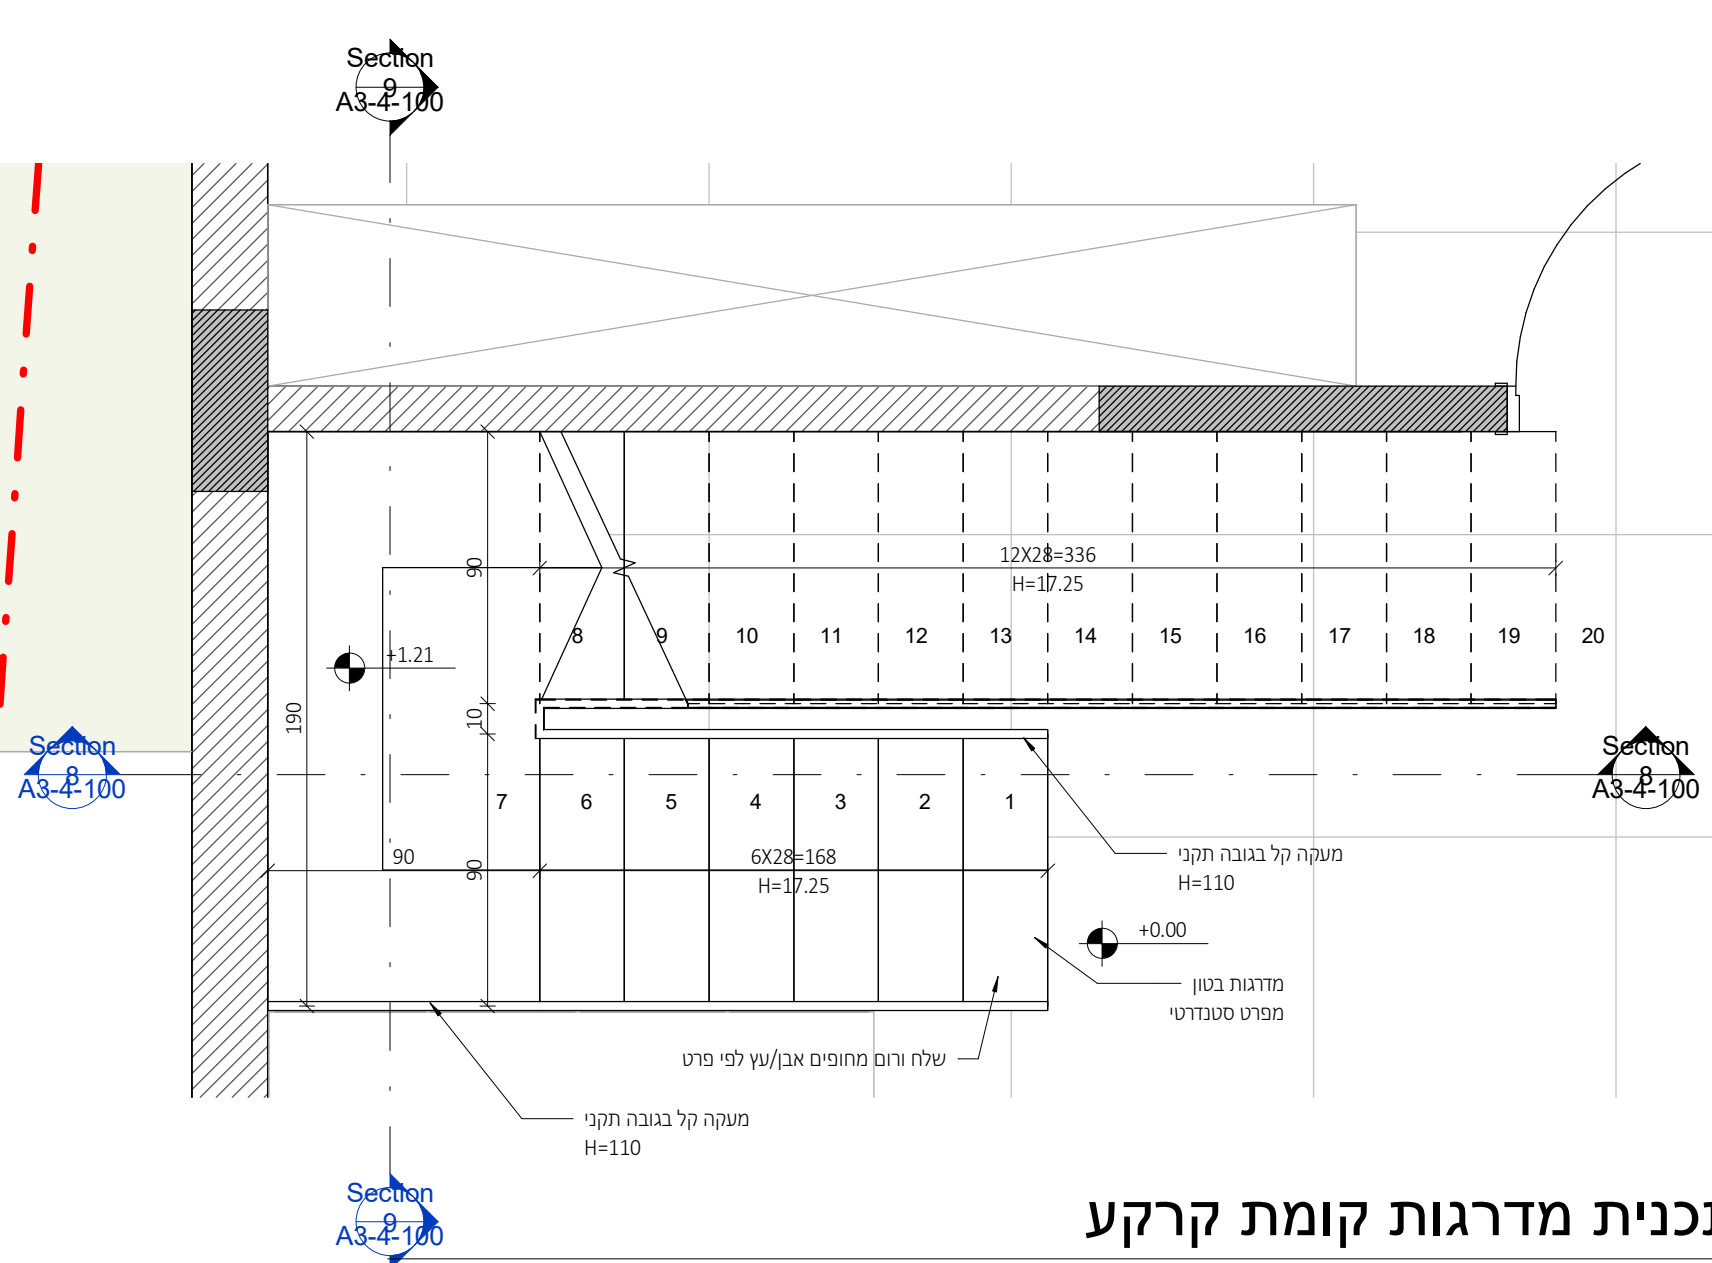


תכנית מדרגות קומת קרקע

1 : 25

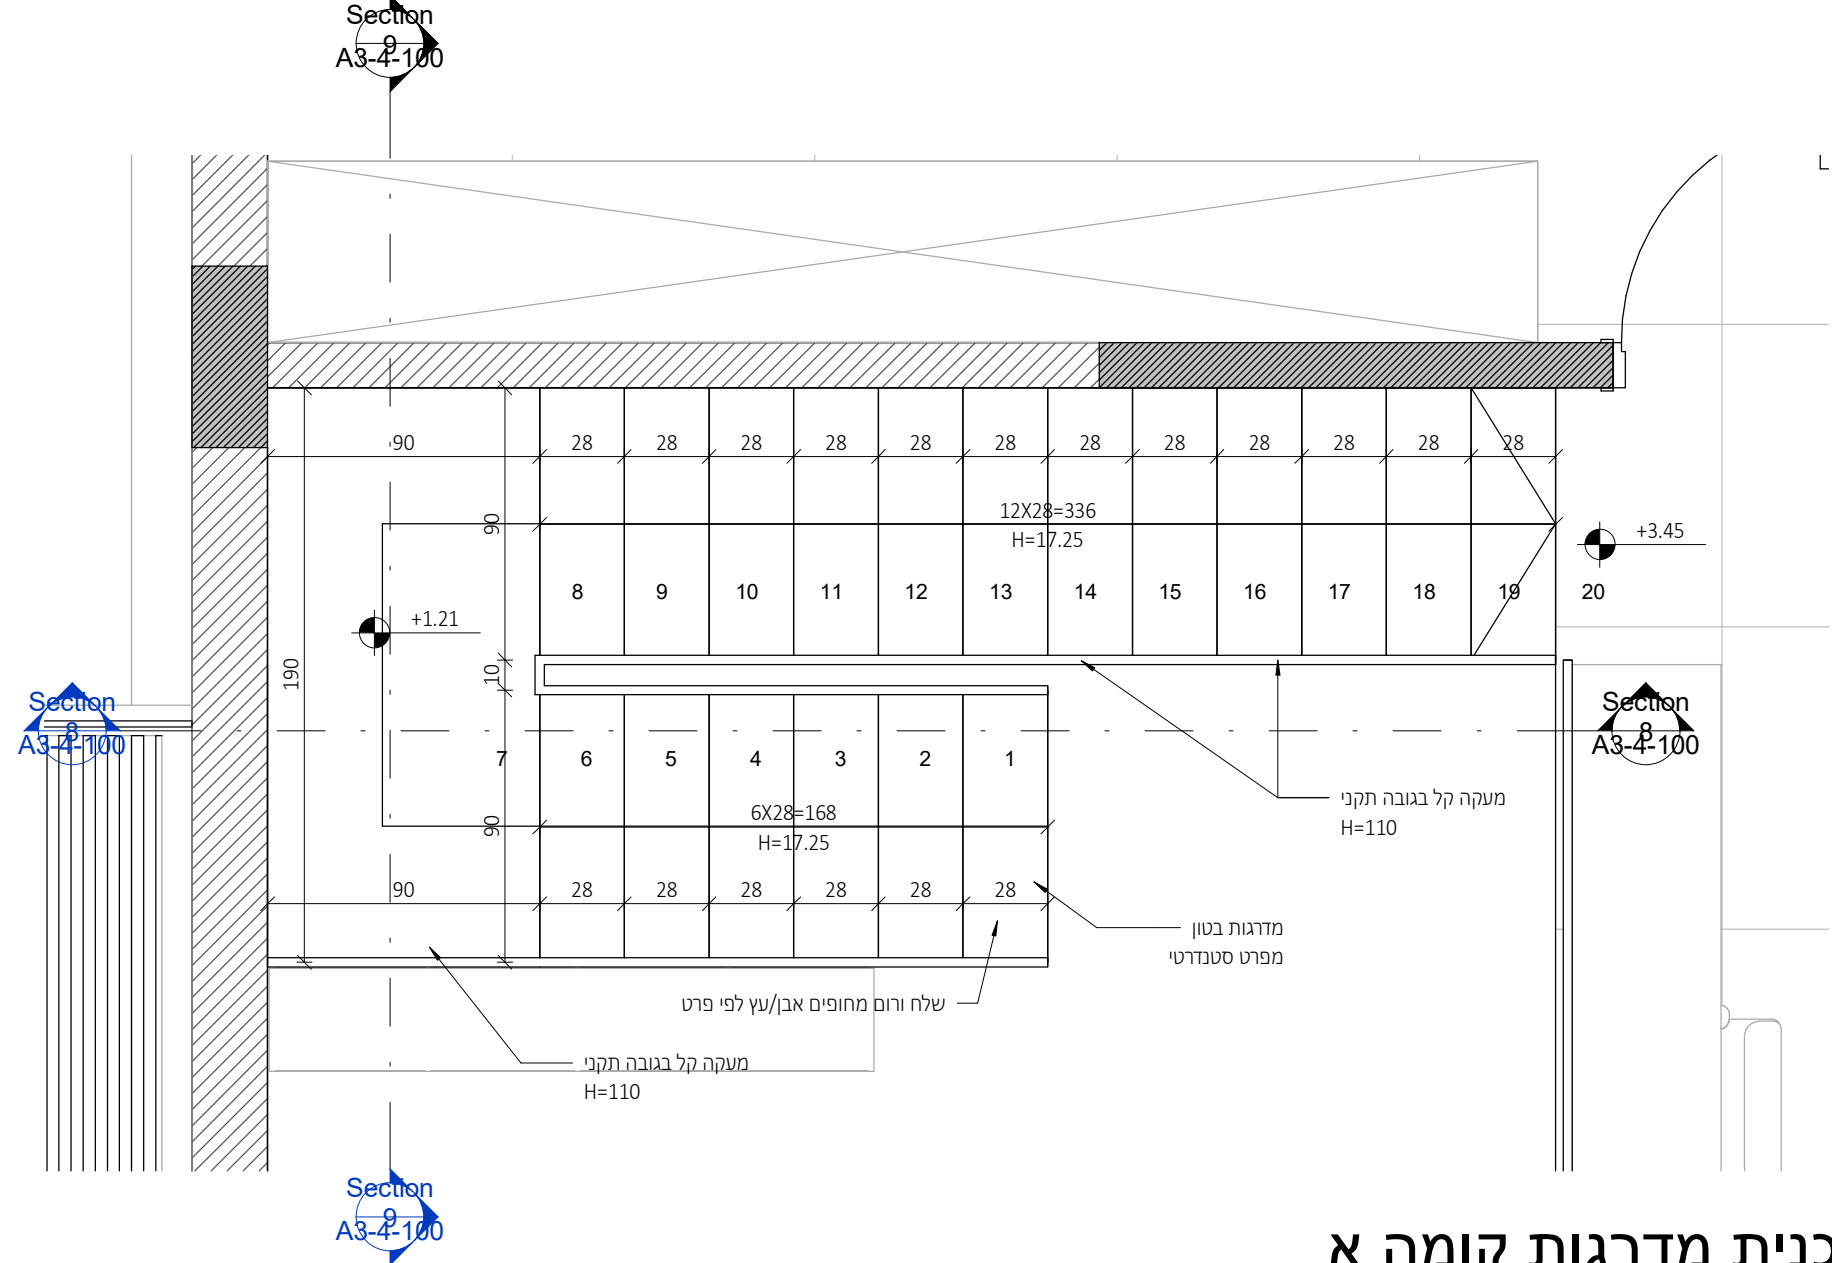

תכנית מדרגות קומה א

1 : 25

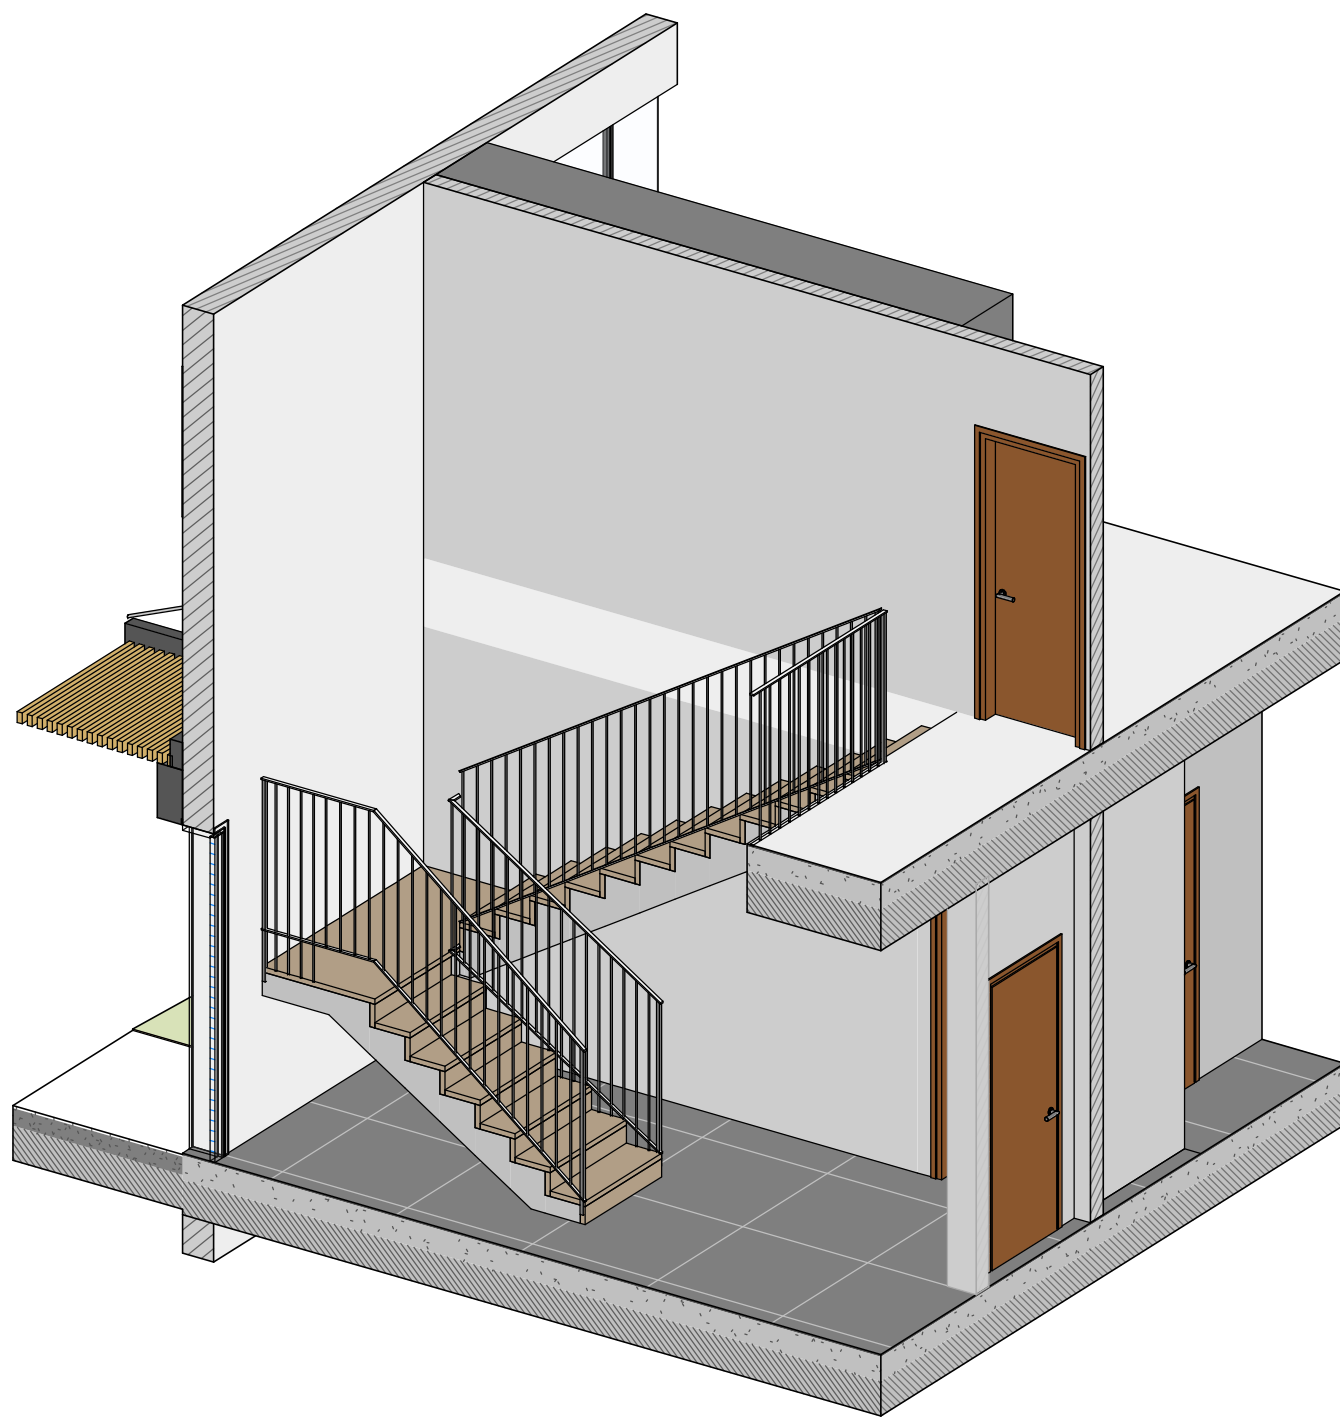


להמשך תיאום

דגם נבחר

מדרגות סטנדרטיות - מפרט סטנדרטי


על הקבלן לשלוח S.D לאישור אדריכל

יש לבצע התאמה לפרט לאחר בחירת חיפוי המדרגות*

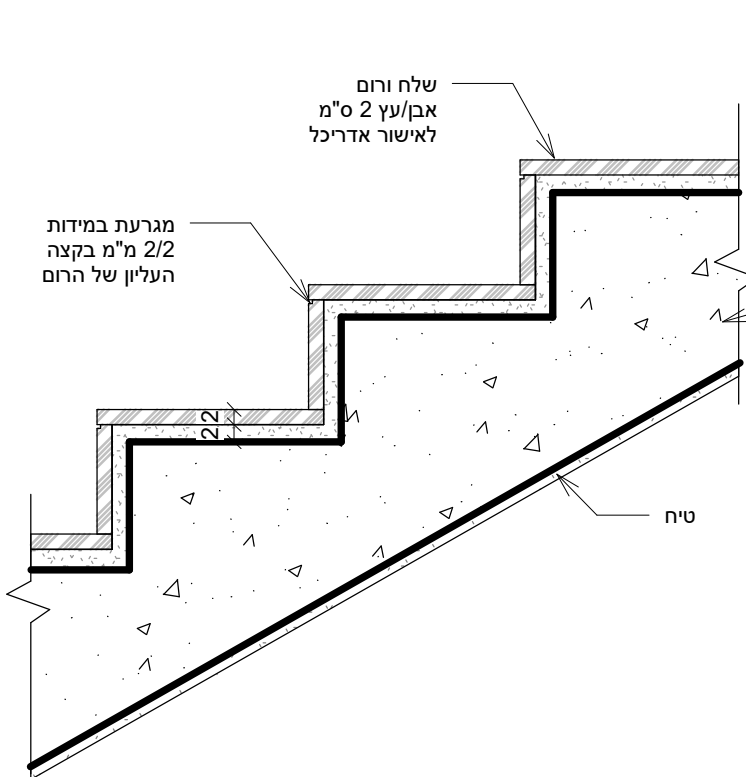


פרט מדרגות פנים - עץ/אבן

1 : 10

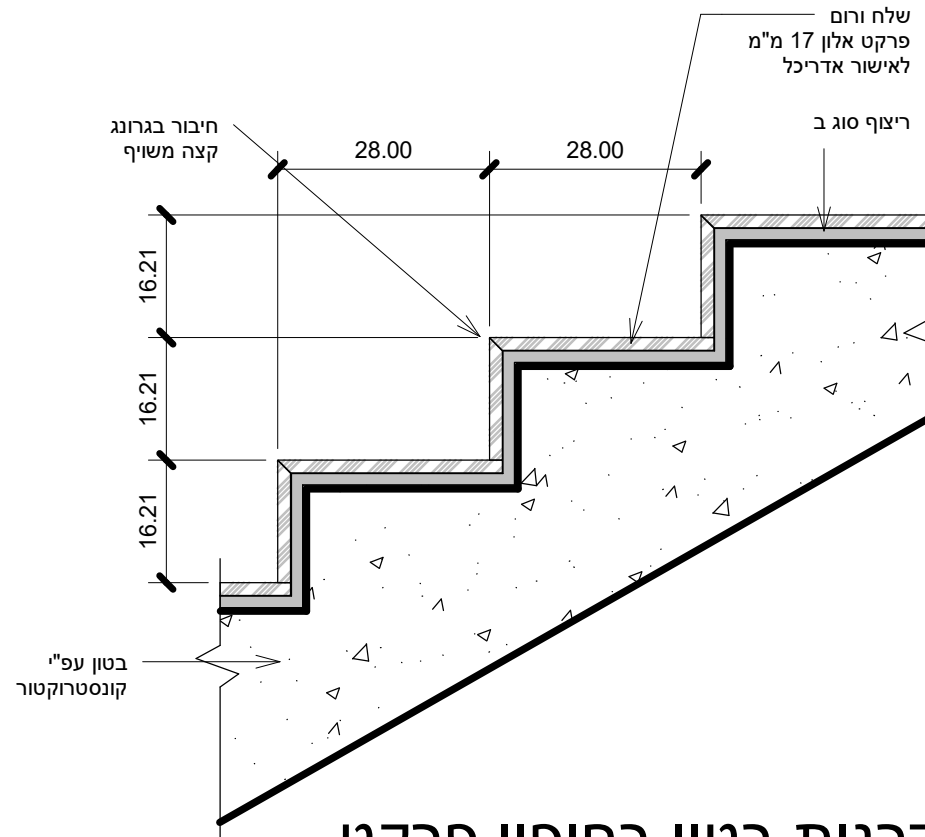


פרט מדרגות בטון בחיפוי פרקט

1 : 10

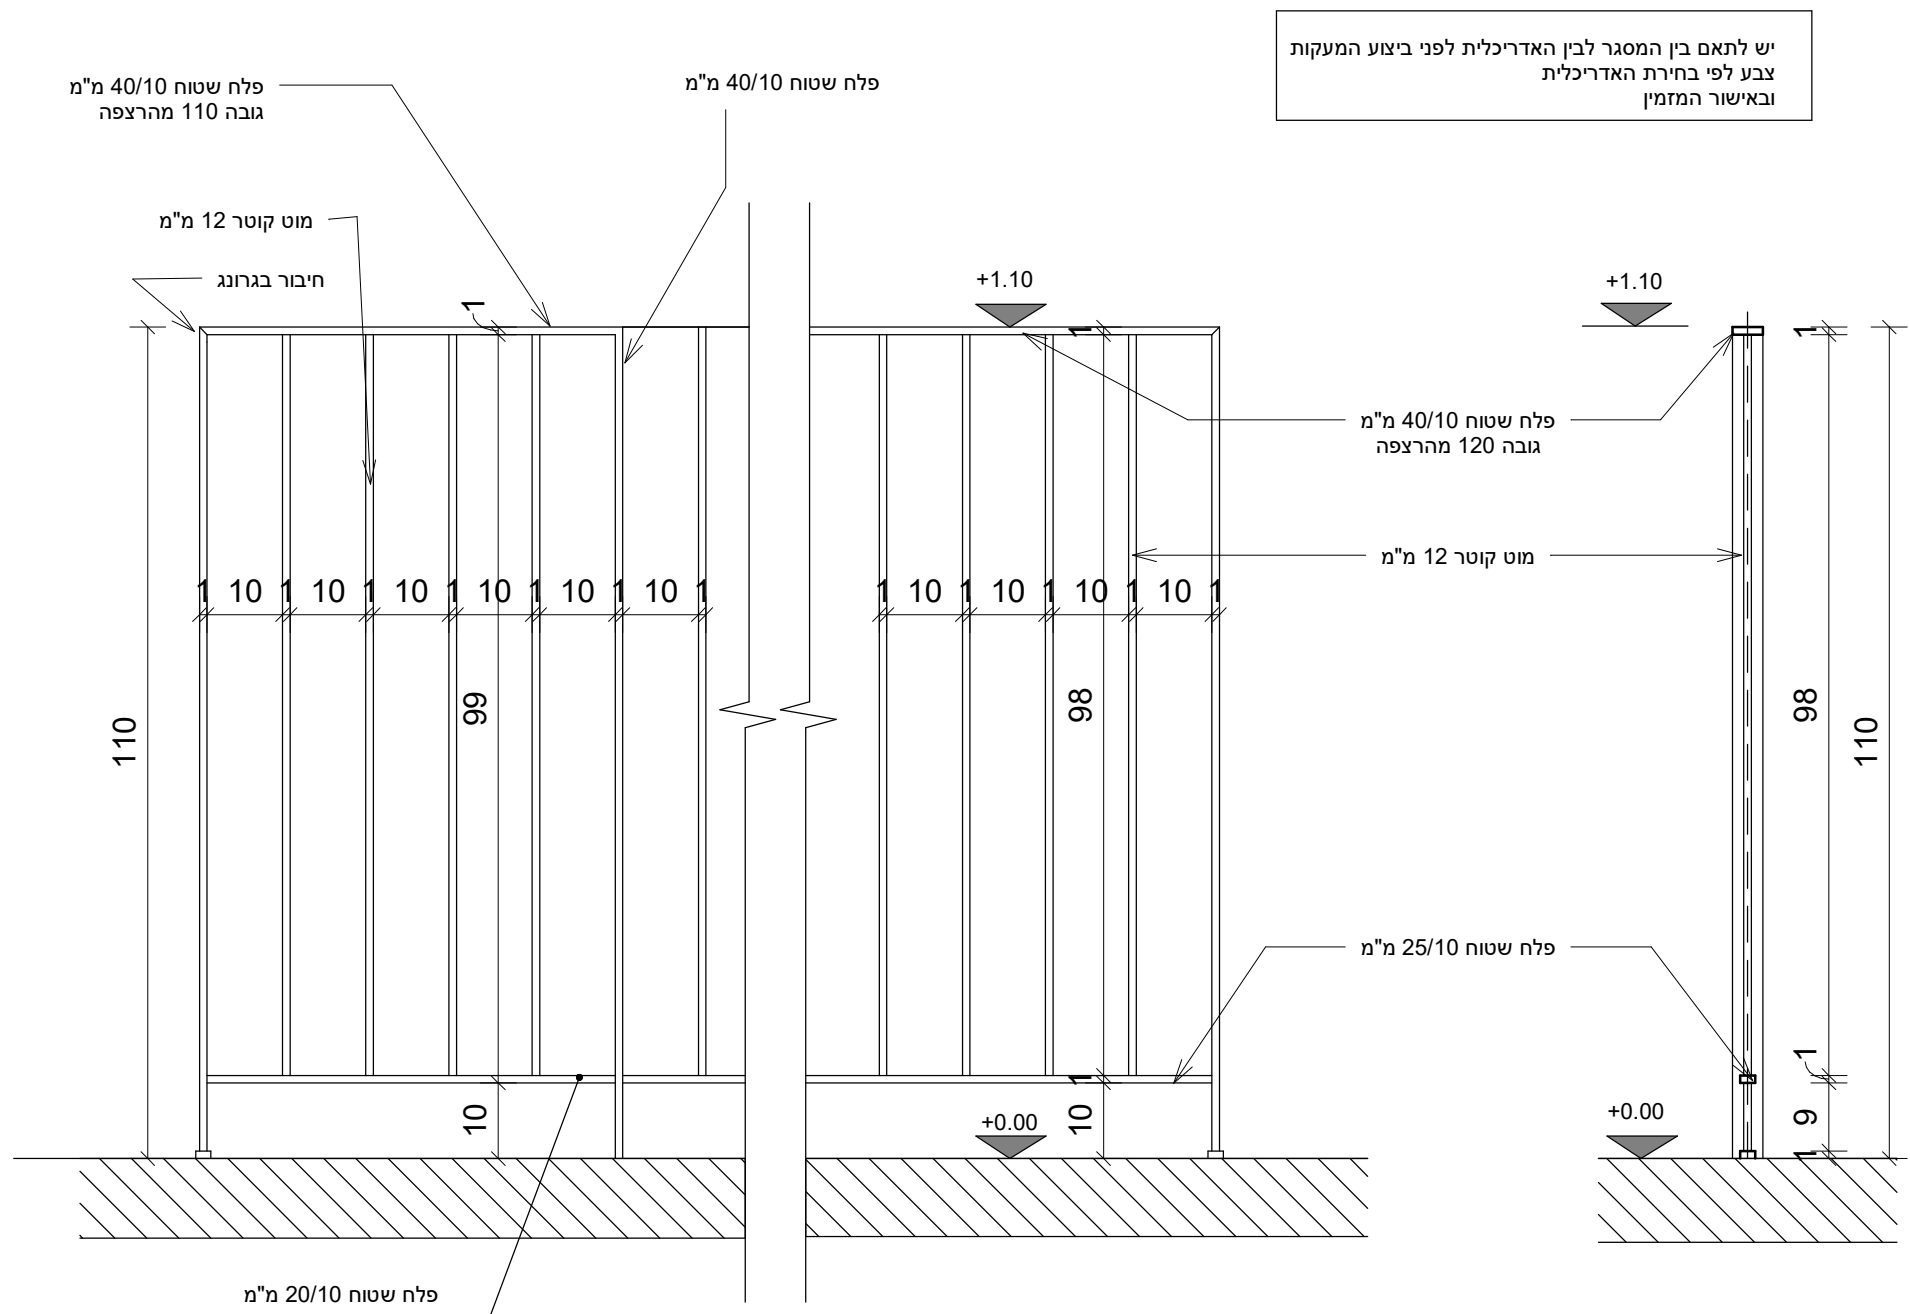


מעקה אנכי

1 : 10

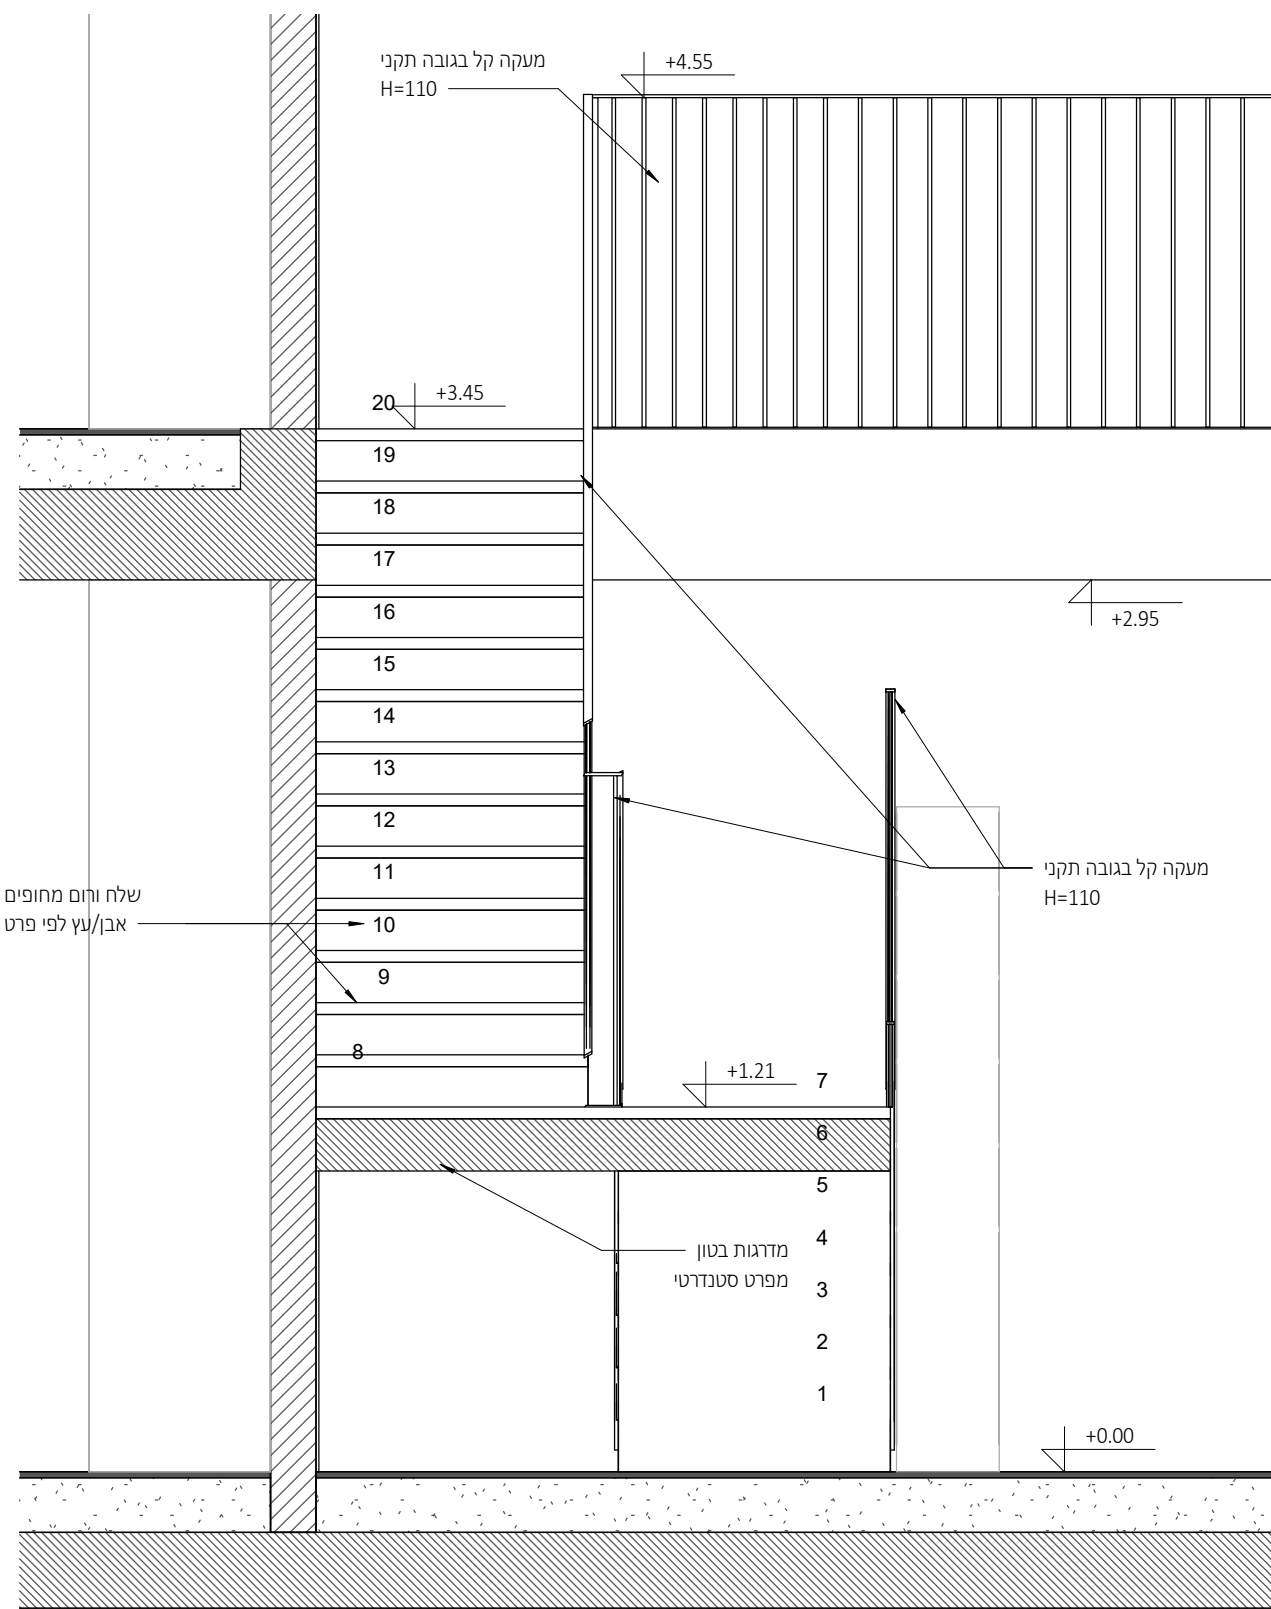

Section 9

1 : 25

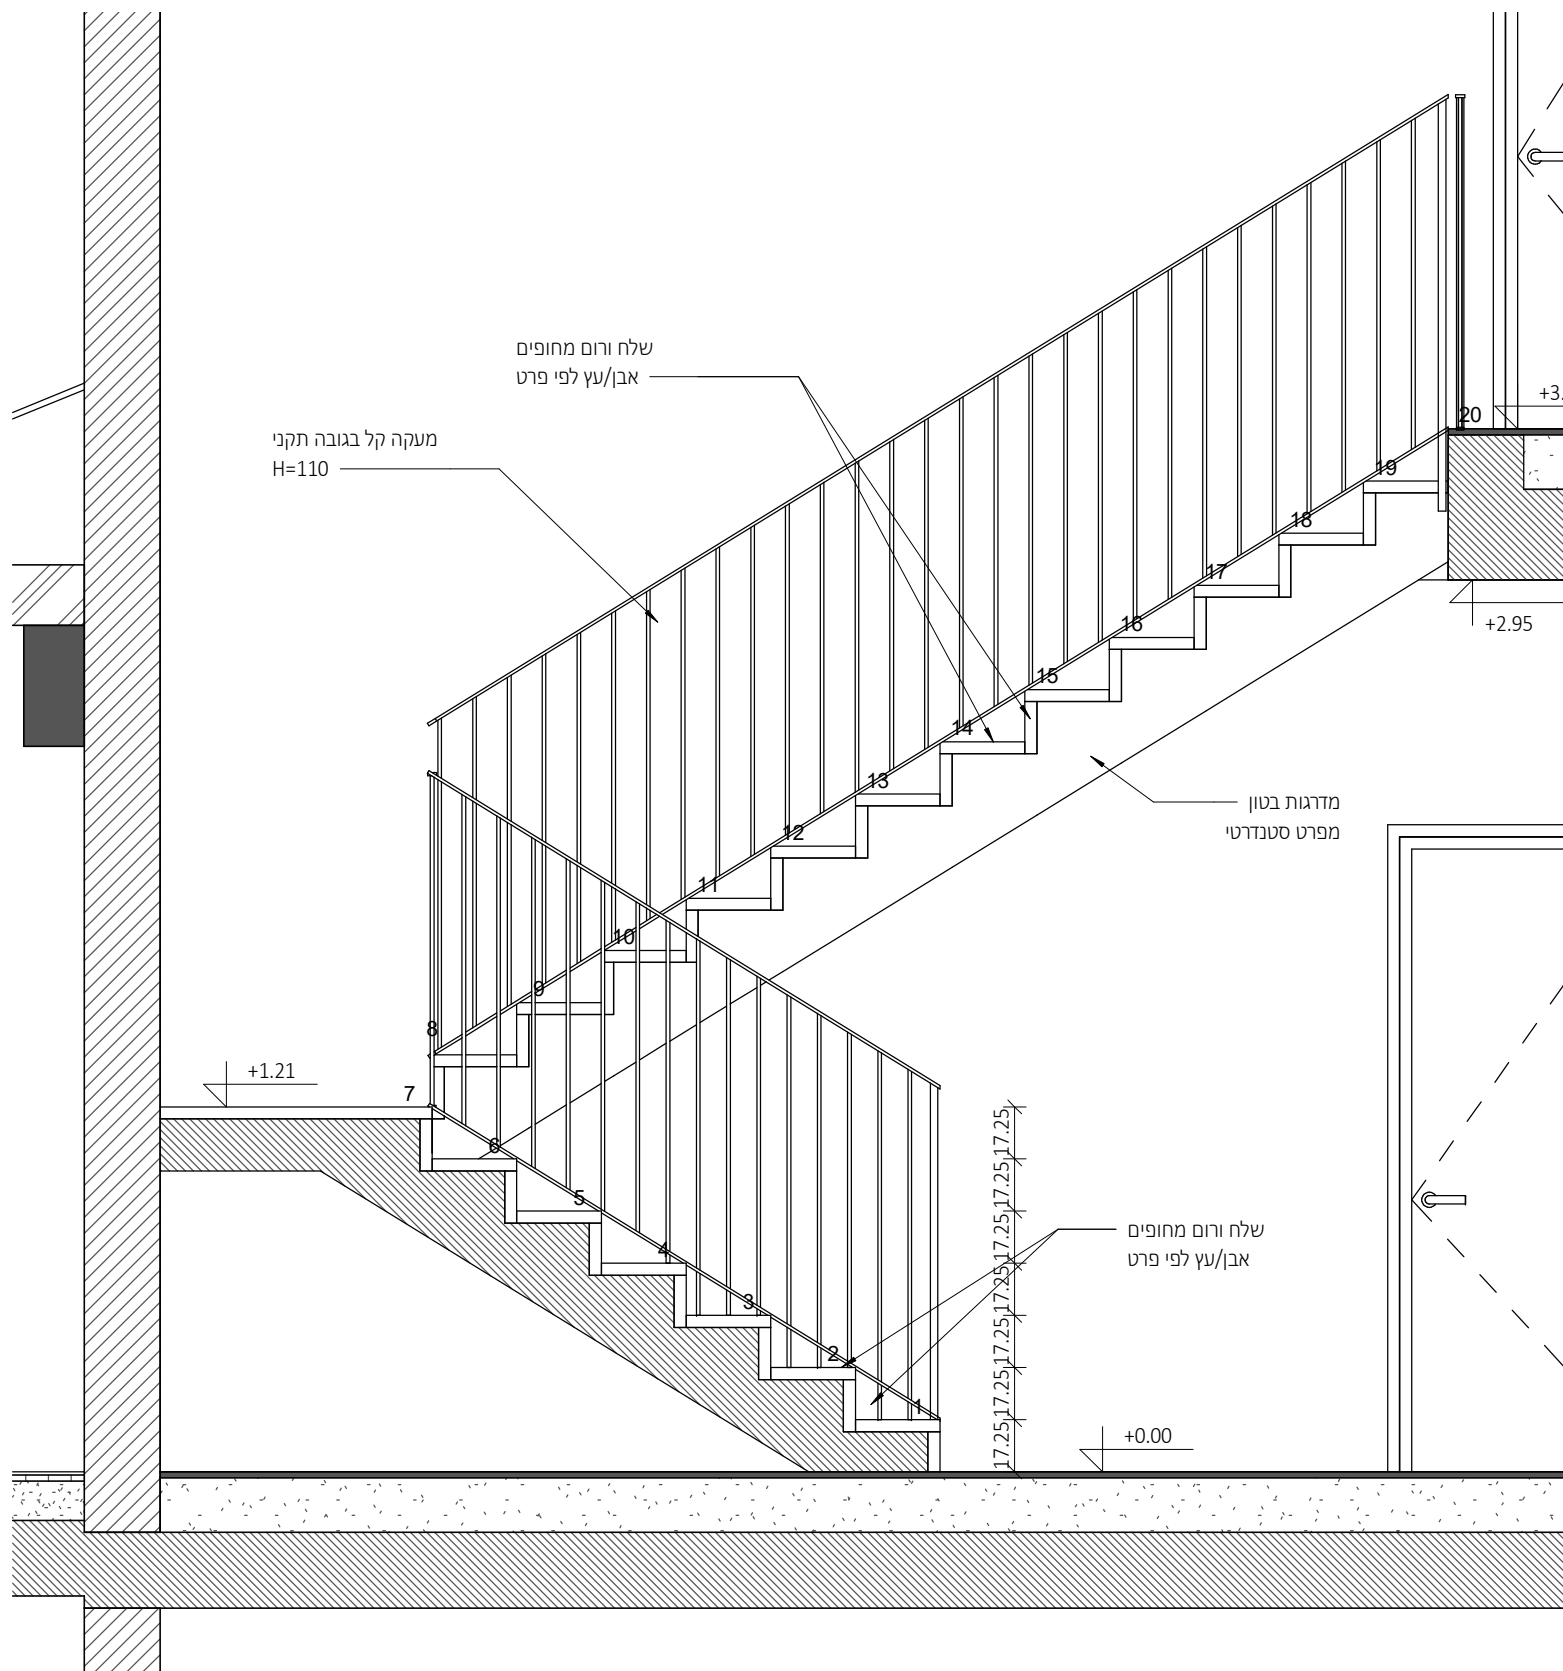

Section 8

1 : 25

מתכננים:


ניהול פרויקט
מהיסוד - בן סולומון
פיקוח
מהיסוד - בן סולומון
קונסטרוקציה
ערן שילר
מיזוג אוויר
אייל ארז מהנדסים ויועצים בע"מ
אינסטלציה
איתן אלמסי
חשמל
איתן בסיס
אלומיניום
בופ
נתי בלוקא
חשמל חכם
חימום תת רצפתי
איטום
צבי טל
אקוסטיקה
מעליות
קרקע וביסוס
דיה הנדסת קרקע וביסוס
רישוי

± 0.00 = +252.80

הערות:
1. תכנית זו יש לקרוא יחד עם תכניות הריטשים.
2. גובה אבסולוטי - ראו תכנית פיתוח.
3. המידות הן בין קירות הבניה ולא כולל פחים.
4. פיתוח השטח סביב הבנוה, כולל, מדרגות, גדרות, שבילים, ריצופים, שטחים בגובה, חניה גינה וראו תכנית פיתוח.
5. איטום קירות ורצפות הבנוה כמנוע עם הקרקע ובידוד תרמי לאורך העמודים והקורות וכל התפרות. כלירות או עם סימני גינה - ראו תכנית קונסטרוקציה.
6. אף דום יבוצע בכל מישור אופקי הכולל חתוכין.
7. פוח חתמי בממד" ע"פ מפרט חומקיר, מאושר ט"י פיקוד העורף.

המבצע אחראי לסידור : עליו לבקר ולבדוק את כל המידות בתכנית ובנקודת הבנייה.
במסגרת של שטח או אי התאמה בתכנית /או בבנוי, עליו להודיע על כך מיד לאדריכל בסדר המשיך בעבודתו.
המבצע ישתמש אך ורק בתכנית שאושרו לביצוע.
המבצע יחזיק באחר, בכל של, של מחדכן של תכנית.
את לקבוע מידות של ידי חזירה בשר שום.
התכנית תהיה רכוש האדריכל ואין לשנות כל שימוש בה או ברעיונות הגלומים בה, אלא באישור בכתב מאדריכל.
מחדס /או יושע אשר שמו רשום בתכנית זו, נושא לכיד באחריות המקצועית והתקנית לתכנית.
על המפקח והמכין לודא התאמת התכנית האדריכלית "לביצוע" לתכנית הידית, הפכה והתכנית המאושרות ע"י כל הגורמים הרשמיים.
התכנית כוללת את כל האחריות והידוע עד ליום תחלתה.

משרד קירות:

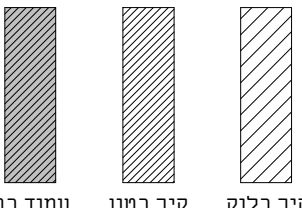
קיר בלוק
קיר בסון
מחוד בסון

תאריך	תיאור	מהדורה
22/09/2025	מכרז	1

אדריכלות

שם המסמן: CLIENT NAME:

קבוצת רכישה נופיה

שם הפרויקט: PROJECT NAME:

נופיה - מגרש 7

שם הגליון: DRAWING NAME:

פרטים

מספר גליון: SHEET NUMBER:


A3-4-103

SCALE:	קנה מידה:	EDITION:	מהדורה:
As indicated			
STATUS:	סטוס		
למכרז			
	נבדק ע"י:		
DATE:	22.09.25		תאריך:



נרסן חיינר אדריכלים
מורד ההודים 2, בית חירות
09-9545842 78
office@nh-arch.com
www.nh-arch.com


זכיות ייצור / ע"פ הנחיות ע"ד

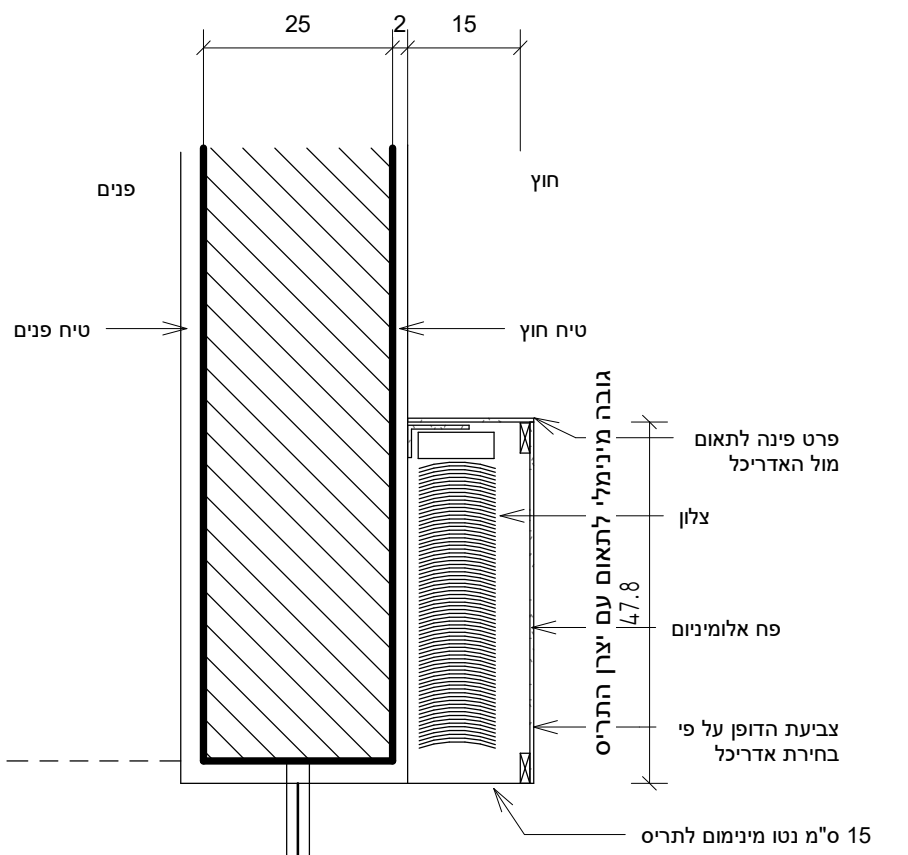

מידות ארגז תריס סופיות
לתאום מול יצון התריסים

פרט 1 - כיס צלון חיצוני


1 : 10

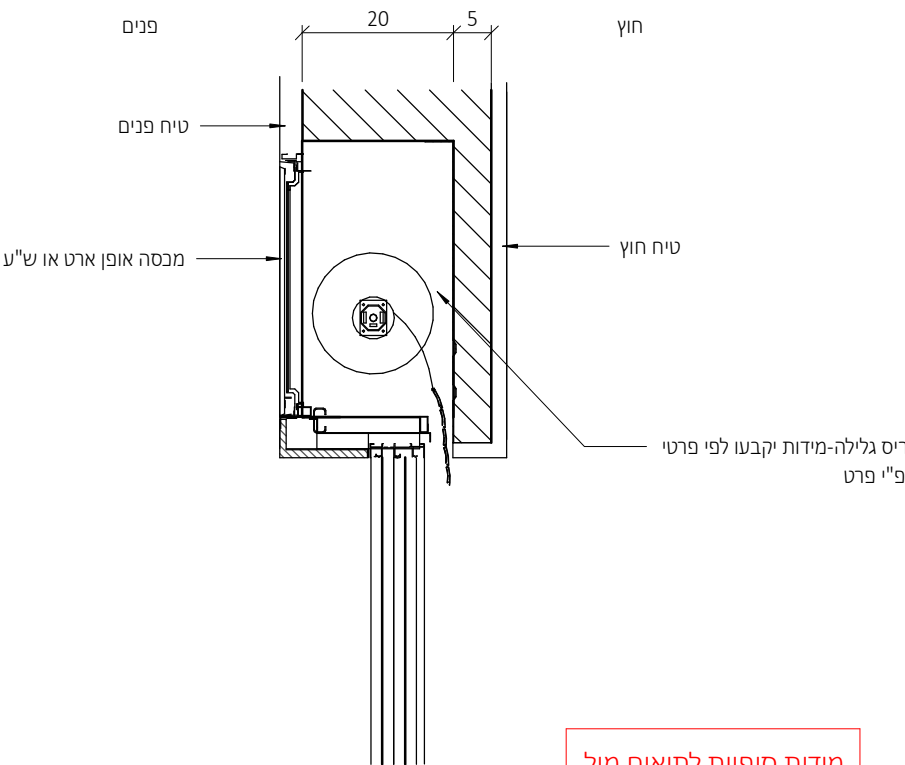

מידות סופיות לתאום מול
יצון התריסים

פרט 2 - תריס גלילה

1 : 10

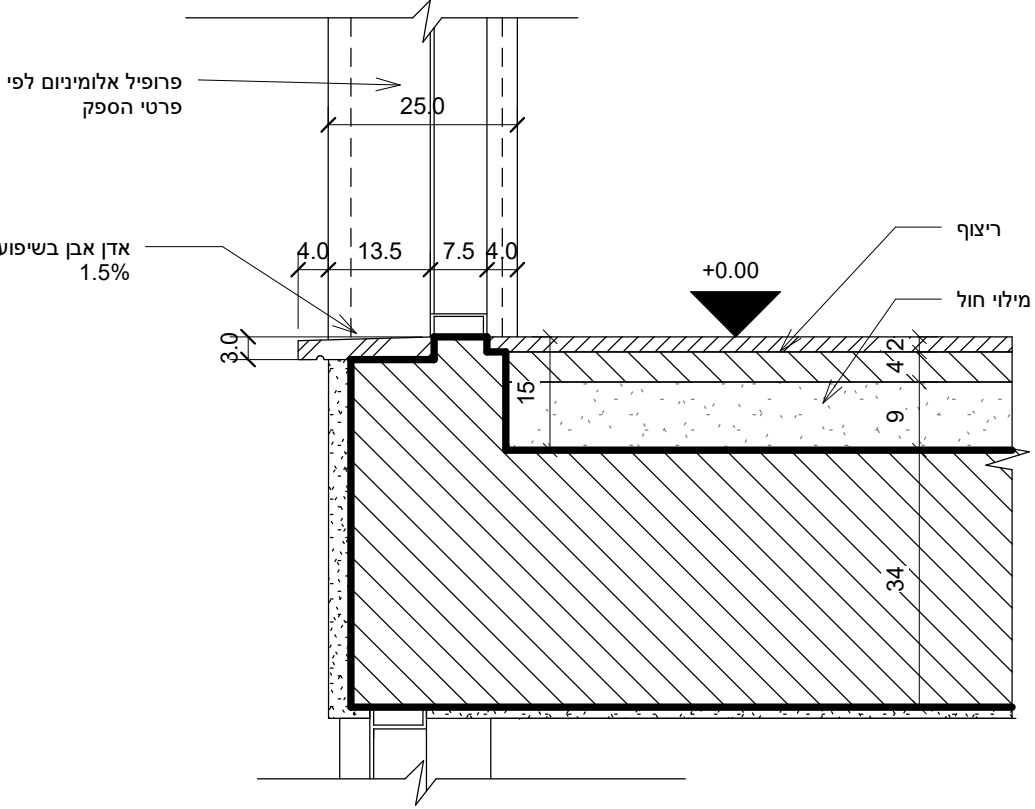


הערה : פרטי האיטום הם עקרוניים בלבד
כל האחריות על האיטום מוטלת על יועץ
האיטום החברה המבצעת
יש לעבוד לפי פרטי האיטום של יועץ הפרויקט.
גובה החלון המופיע בתכניות מצוין את פני סף
האבן. יש להנמיך את הבטון בהתאם

פרט עקרוני בלבד - פרט סופי מספק החלונות

פרט 3 - מפגש חלון ורצפה

1 : 10

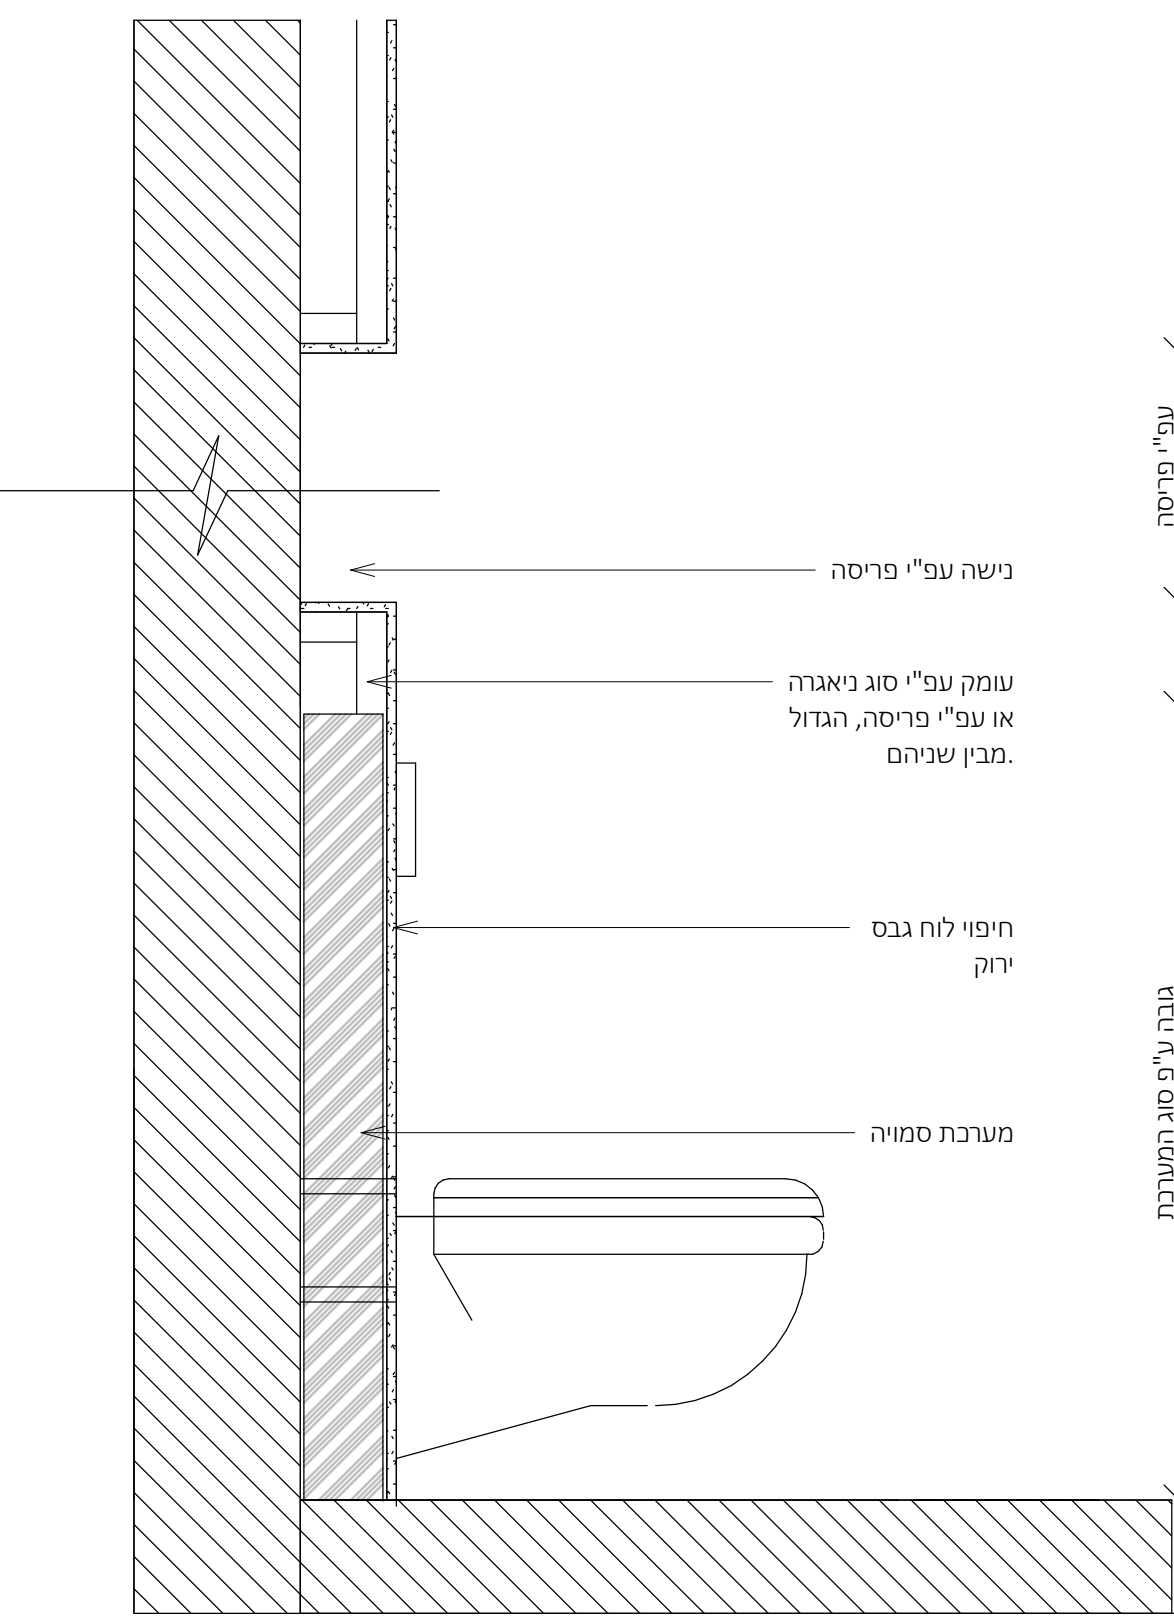

פרט 6 -אסלה תלויה מנגנון סמוי בעיבוי גבס

1 : 10

יש לעבוד במקביל לפרטים שסיפק
מעצב הפנים (במידה וקיים במגרש זה)
המאושרות על ידי האדריכל.

פרטי האיטום באחריות יועץ האיטום
ראה חוברת פרטי איטום מצורפת

להמשך תיאום

רשימת חלונות					
סוג	תיאור	כמות	גובה	רוחב	מס פריט

קומת קרקע

1	580	240	1	צלון רפפה חיצוני חשמלי + ארגז חיצוני	ויטרינה פרופיל 7500 קליל
2	110	240	1	צלון רפפה חיצוני חשמלי + ארגז חיצוני	חלון קבוע פרופיל 7000 קליל
3	220	110	1	צלון רפפה חיצוני חשמלי + ארגז חיצוני	חלון הזזה פרופיל 7000 קליל
4	220	240	1	צלון רפפה חיצוני חשמלי + ארגז חיצוני	ויטרינה פרופיל 7500 קליל
5	90	110	1	צלון רפפה חיצוני חשמלי + ארגז חיצוני	חלון קיפ פרופיל 4500 קליל
6	180	240	1	צלון רפפה חיצוני חשמלי + ארגז חיצוני	ויטרינה פרופיל 7500 קליל

קומה א

7	110	110	2	תריס גלילה חשמלי	חלון קיפ פרופיל 4500 קליל
8	200	110	1	תריס גלילה חשמלי	חלון הזזה פרופיל 7000 קליל
9	80	210	1	תריס גלילה חשמלי	דלת כנף פרופיל 4350 קליל
10	220	110	4	תריס גלילה חשמלי	חלון הזזה פרופיל 7000 קליל
11	110	110	2	תריס גלילה חשמלי	חלון הזזה פרופיל 7000 קליל

סוג זכוכית – בהתאם למפורט בדו"ח התרמי (תנאי המינימום בעמוד 9 מתוך המפרט התרמי). כמו כן, הזכוכית תקבע בתיאום עם הקבלן לאחר אישור יועץ התרמי וחברת הניהול

כל פריט יחולק למינימום הכנפיים האפשרי (לתיאום מול ספק האלומיניום ובמסגרת שרטוטי shop drawing)

רשימת דלתות					
סוג	הערות	כמות	גובה	רוחב	מספר פריט
0	דלת חוץ דגם גארדה	1	240	120	
1	דלת פנים "אקוודור" תוצרת חמדיה	9	210	80	
2	דלת פנים "אקוודור" תוצרת חמדיה	1	210	90	
3	דלת פנים "אקוודור" תוצרת חמדיה	1	200	80	

נוימן חיינר אדריכלים בע"מ

כל הזכויות שמורות
ט.ל.ח

NeumanHaynerArchitects



רשימת פתחים

שם התכנית:		מהדורה:	
A3-6-1000		22/09/2025	
גליון מספר:		שם הפרויקט:	
7		למכרז	
שם המממן:		קנה מידה:	
קבוצת רכישה נופיה		22/09/2025 12:19:05	



D:\NH-Arch-Dropbox\NH-Arch-Projects\NH-בתים ודירות\00\7\תכנית\info\

FILE NAME: כלל הפרויקטים להיתר\00\7\תכנית\info\