תפוצה															תאריך
מנהל הפרויקט	אדריכל	מזמין/יזם	חשמל	קבלן	בטיחות	אקוסטיקה	אינסטלציה	קונסטרוקציה	אדריכל נוף	מטבחים	חברת חשמל	חברת בזק			

מס'	שינויים	תאריך

עודכן ע"י: יפעת

לוח חשמל דירתי ראשי #1

הנחיות לבניית לוח חשמל:
- מבנה לוח חשמל פלסטי חסין אש סדרת FW מתוצרת Hager דגם FW62US2 ל-144 מודולים (6x12)2X לפחות
- דלת פח IP30 מתכתית
- בדיד כפול Class-2
- צבע לבן
- מהדקי אפס והארקה עם חיבור מהיר
- ציוד חשמלי יהיה מסוג ABB שניידר הגר או EATON בלבד בעל זרם
- יש לשמור בלוח 30% מקום לתוספת עתידית בלוח

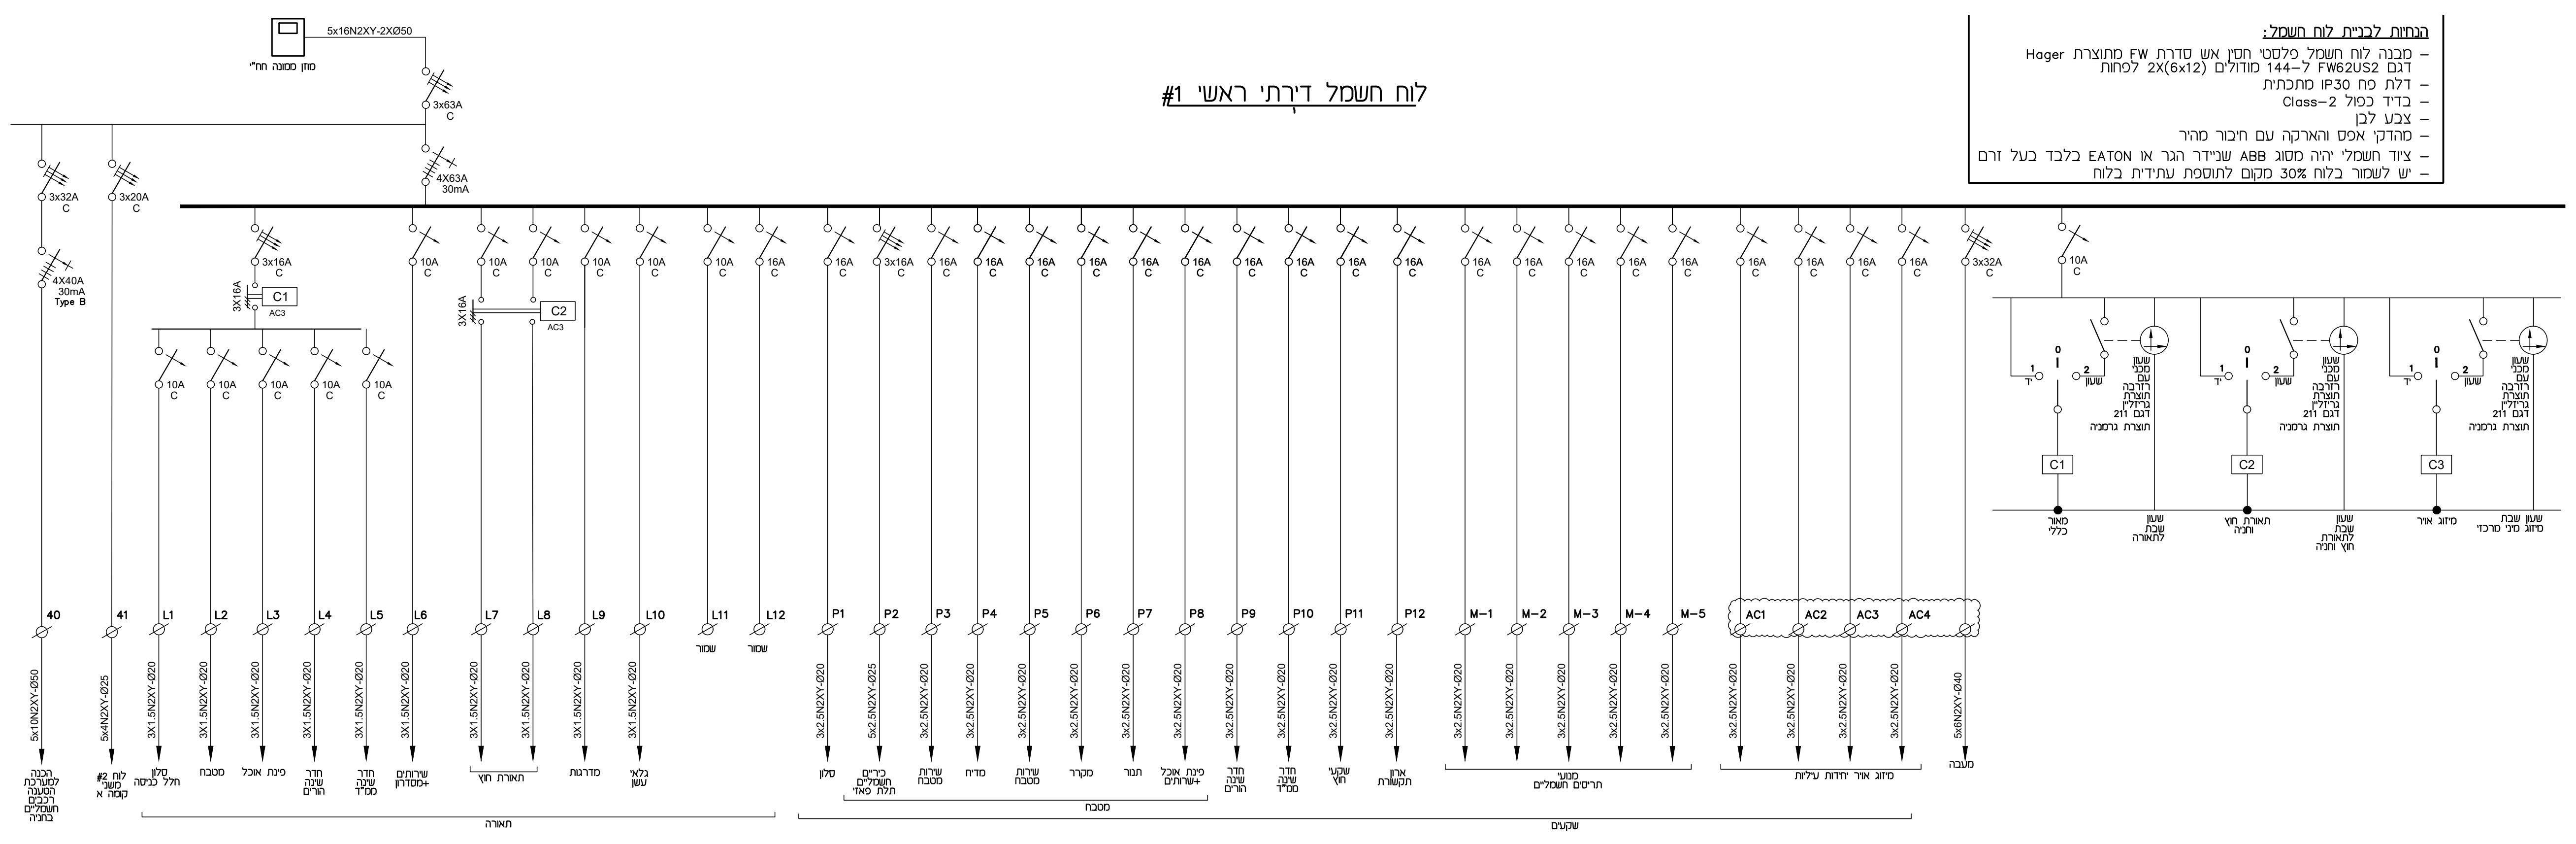

לוח חשמל משני #2 קומה א'

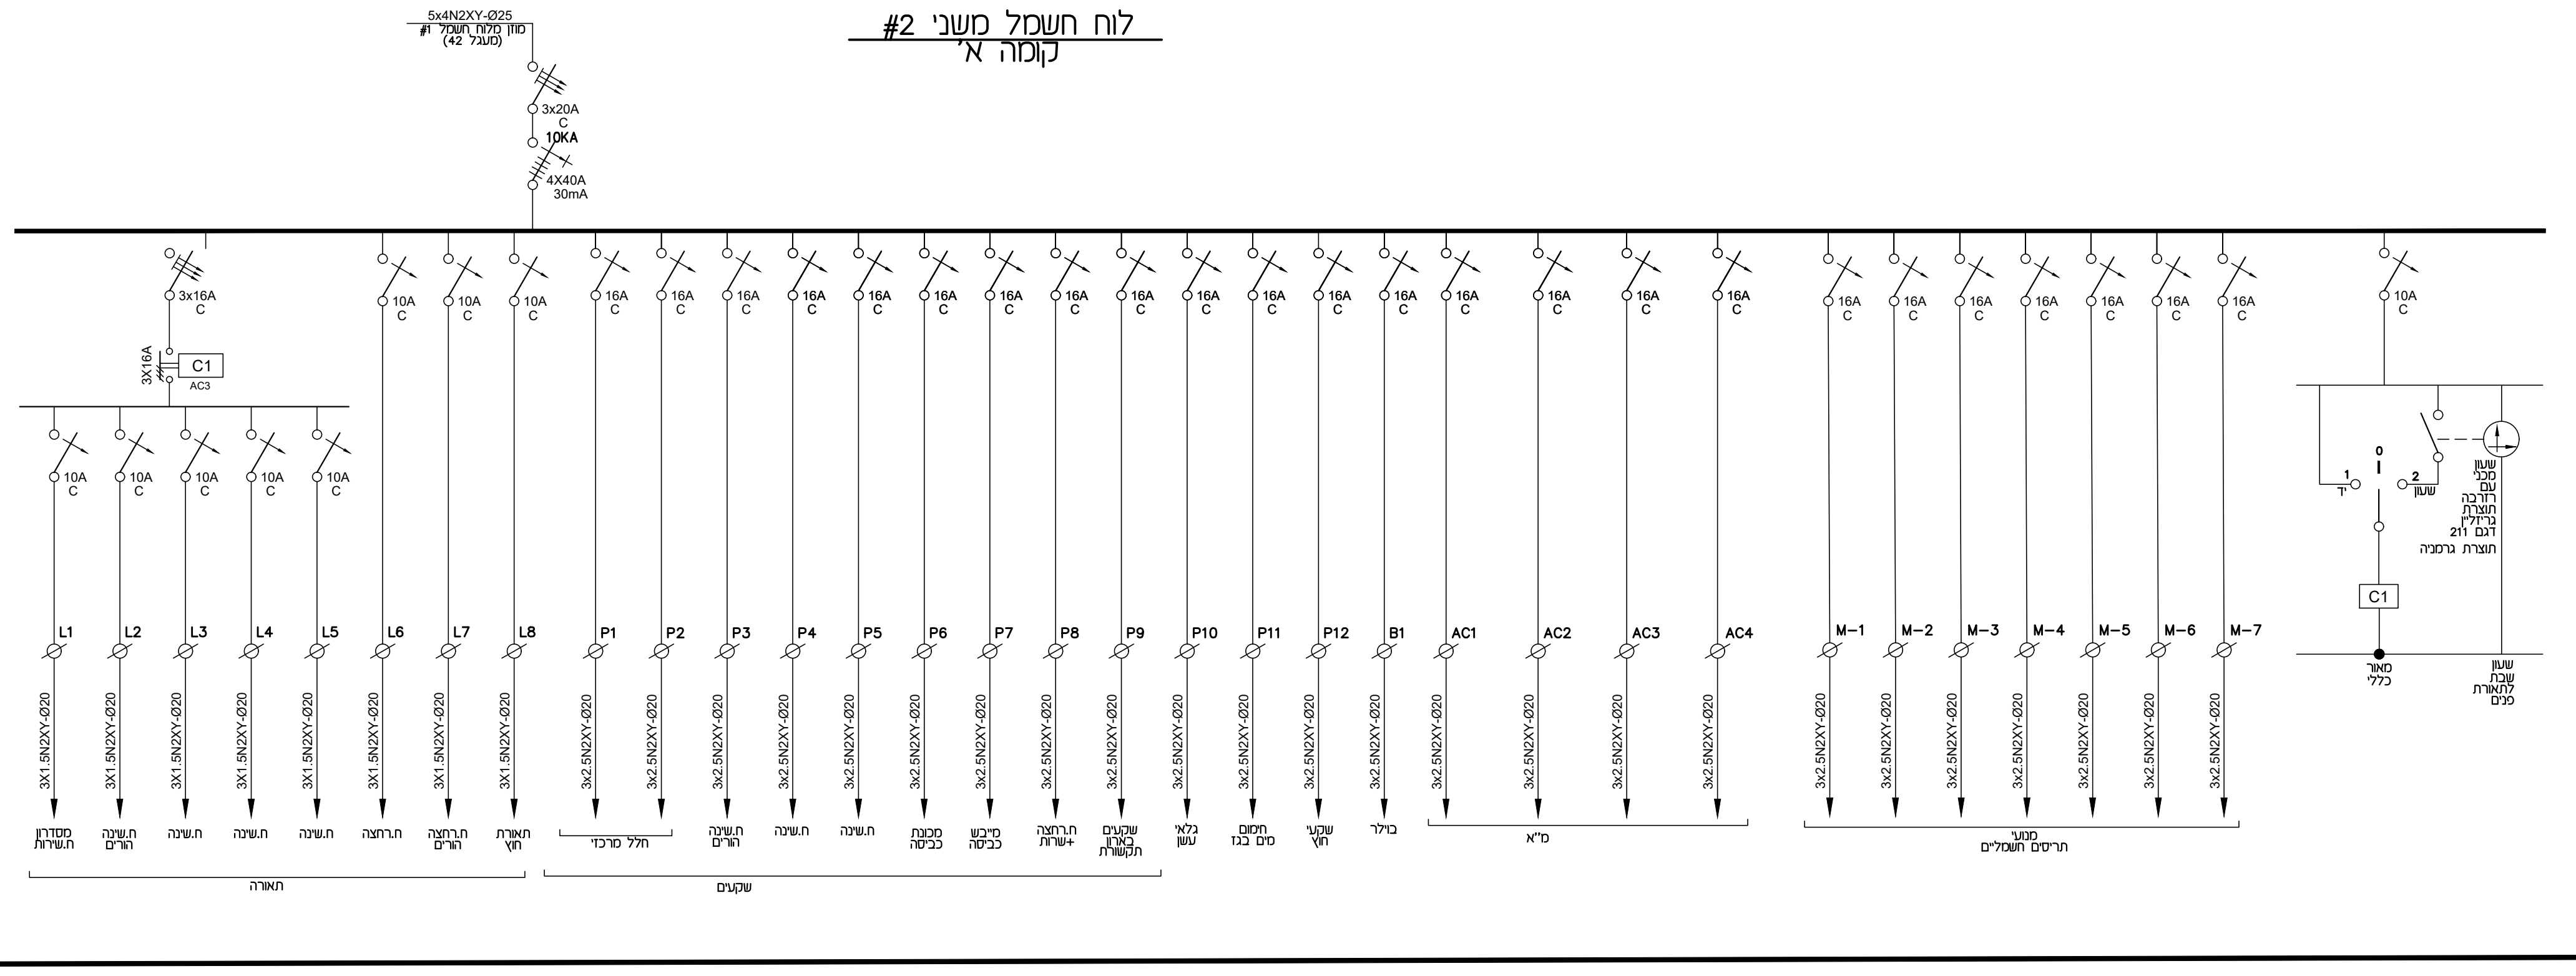

א. בסיס
הנדסת חשמל בע"מ
משרד: יד חרוצים 16, ירושלים 93420
טל: 074-7021015 נייד: 050-6550484
פקס: 077-5131015 דוא"ל: office@ebasis.co.il

שם הפרויקט:
נופיה-אלפי מנשה

שם התכנית:
לוח #1- מגרש 7, נופיה

				קנה מידה:
○ לעיון	○ לאישור	○ למכרז	● לביצוע	1:50

File: מס' קובץ:	Date: תאריך:
675W.dwg	05.03.2025

תכנן:	שרטט:	אישר:
יפעת	ליאל	איתן

מס' עדכון:	מס' הגליון:	מס' הפרויקט:
0	7	675

פרט יציאת צנרת חשמל בגג לבוילר וכדו'

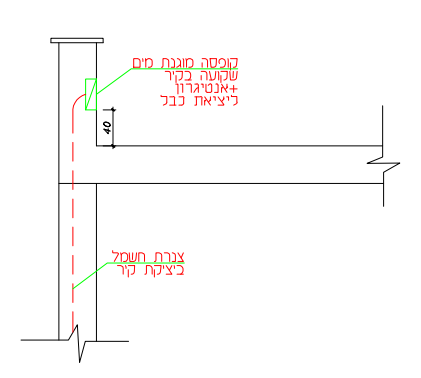

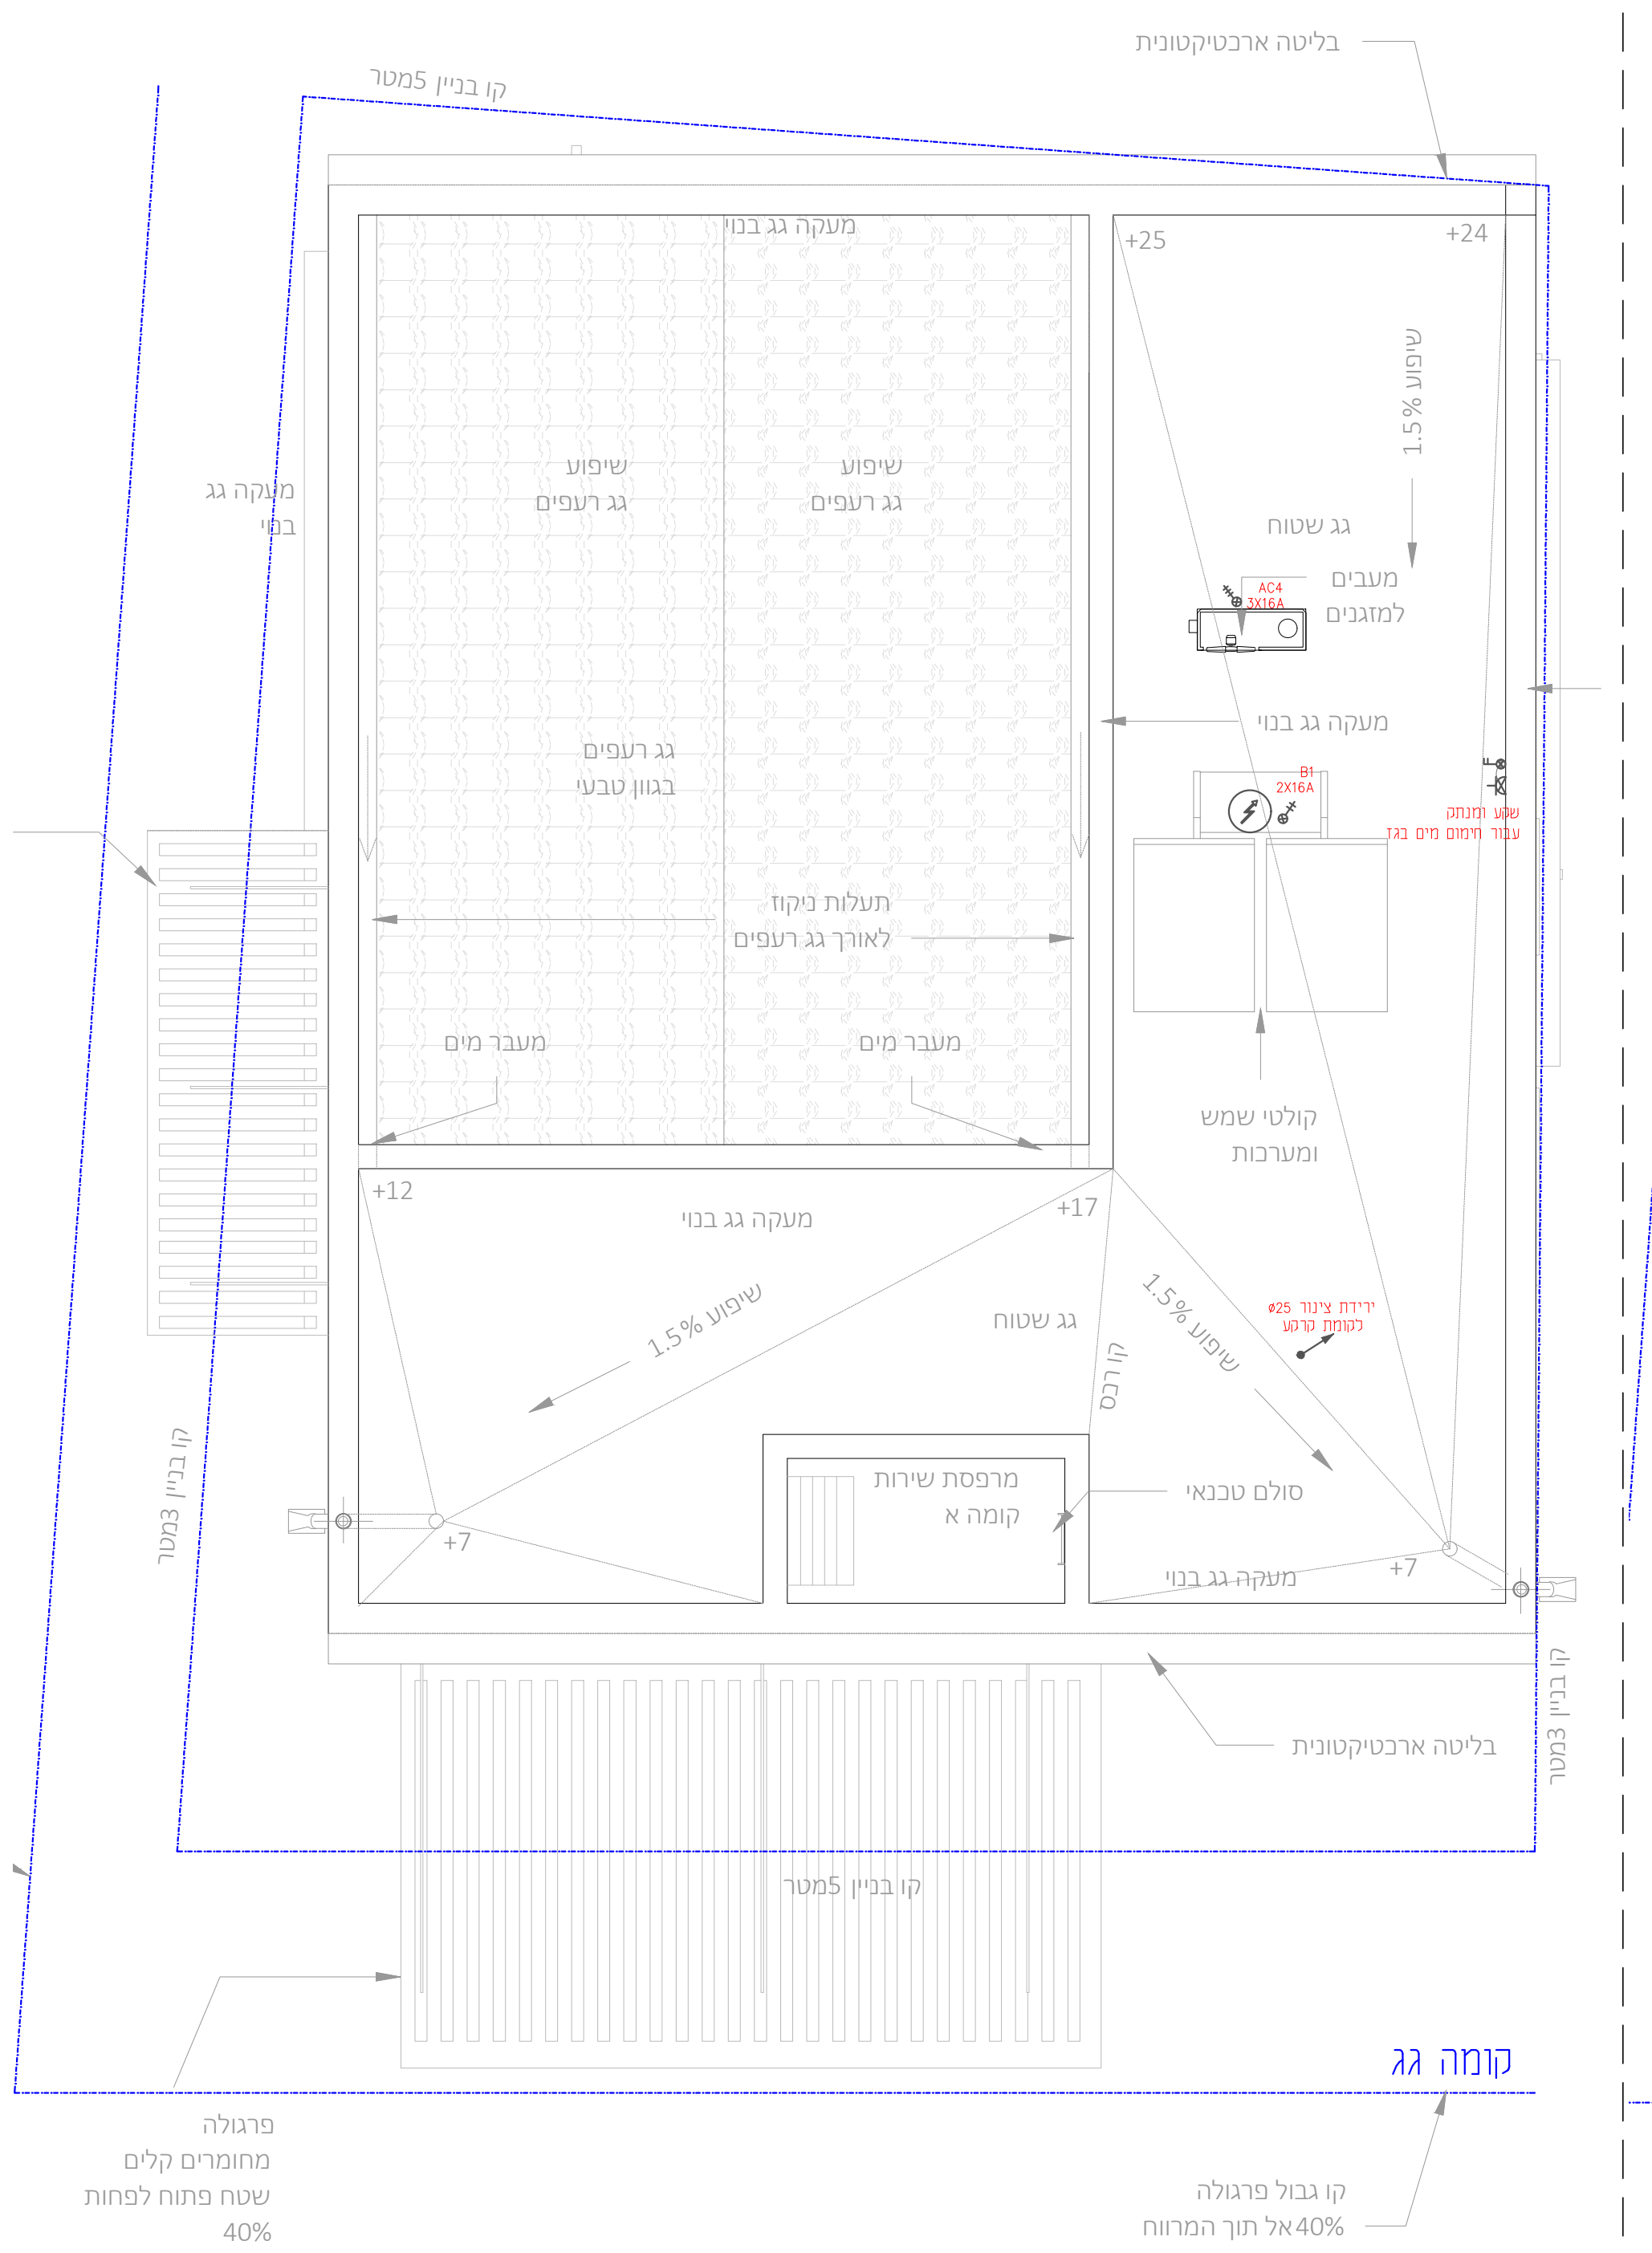

קומה גג

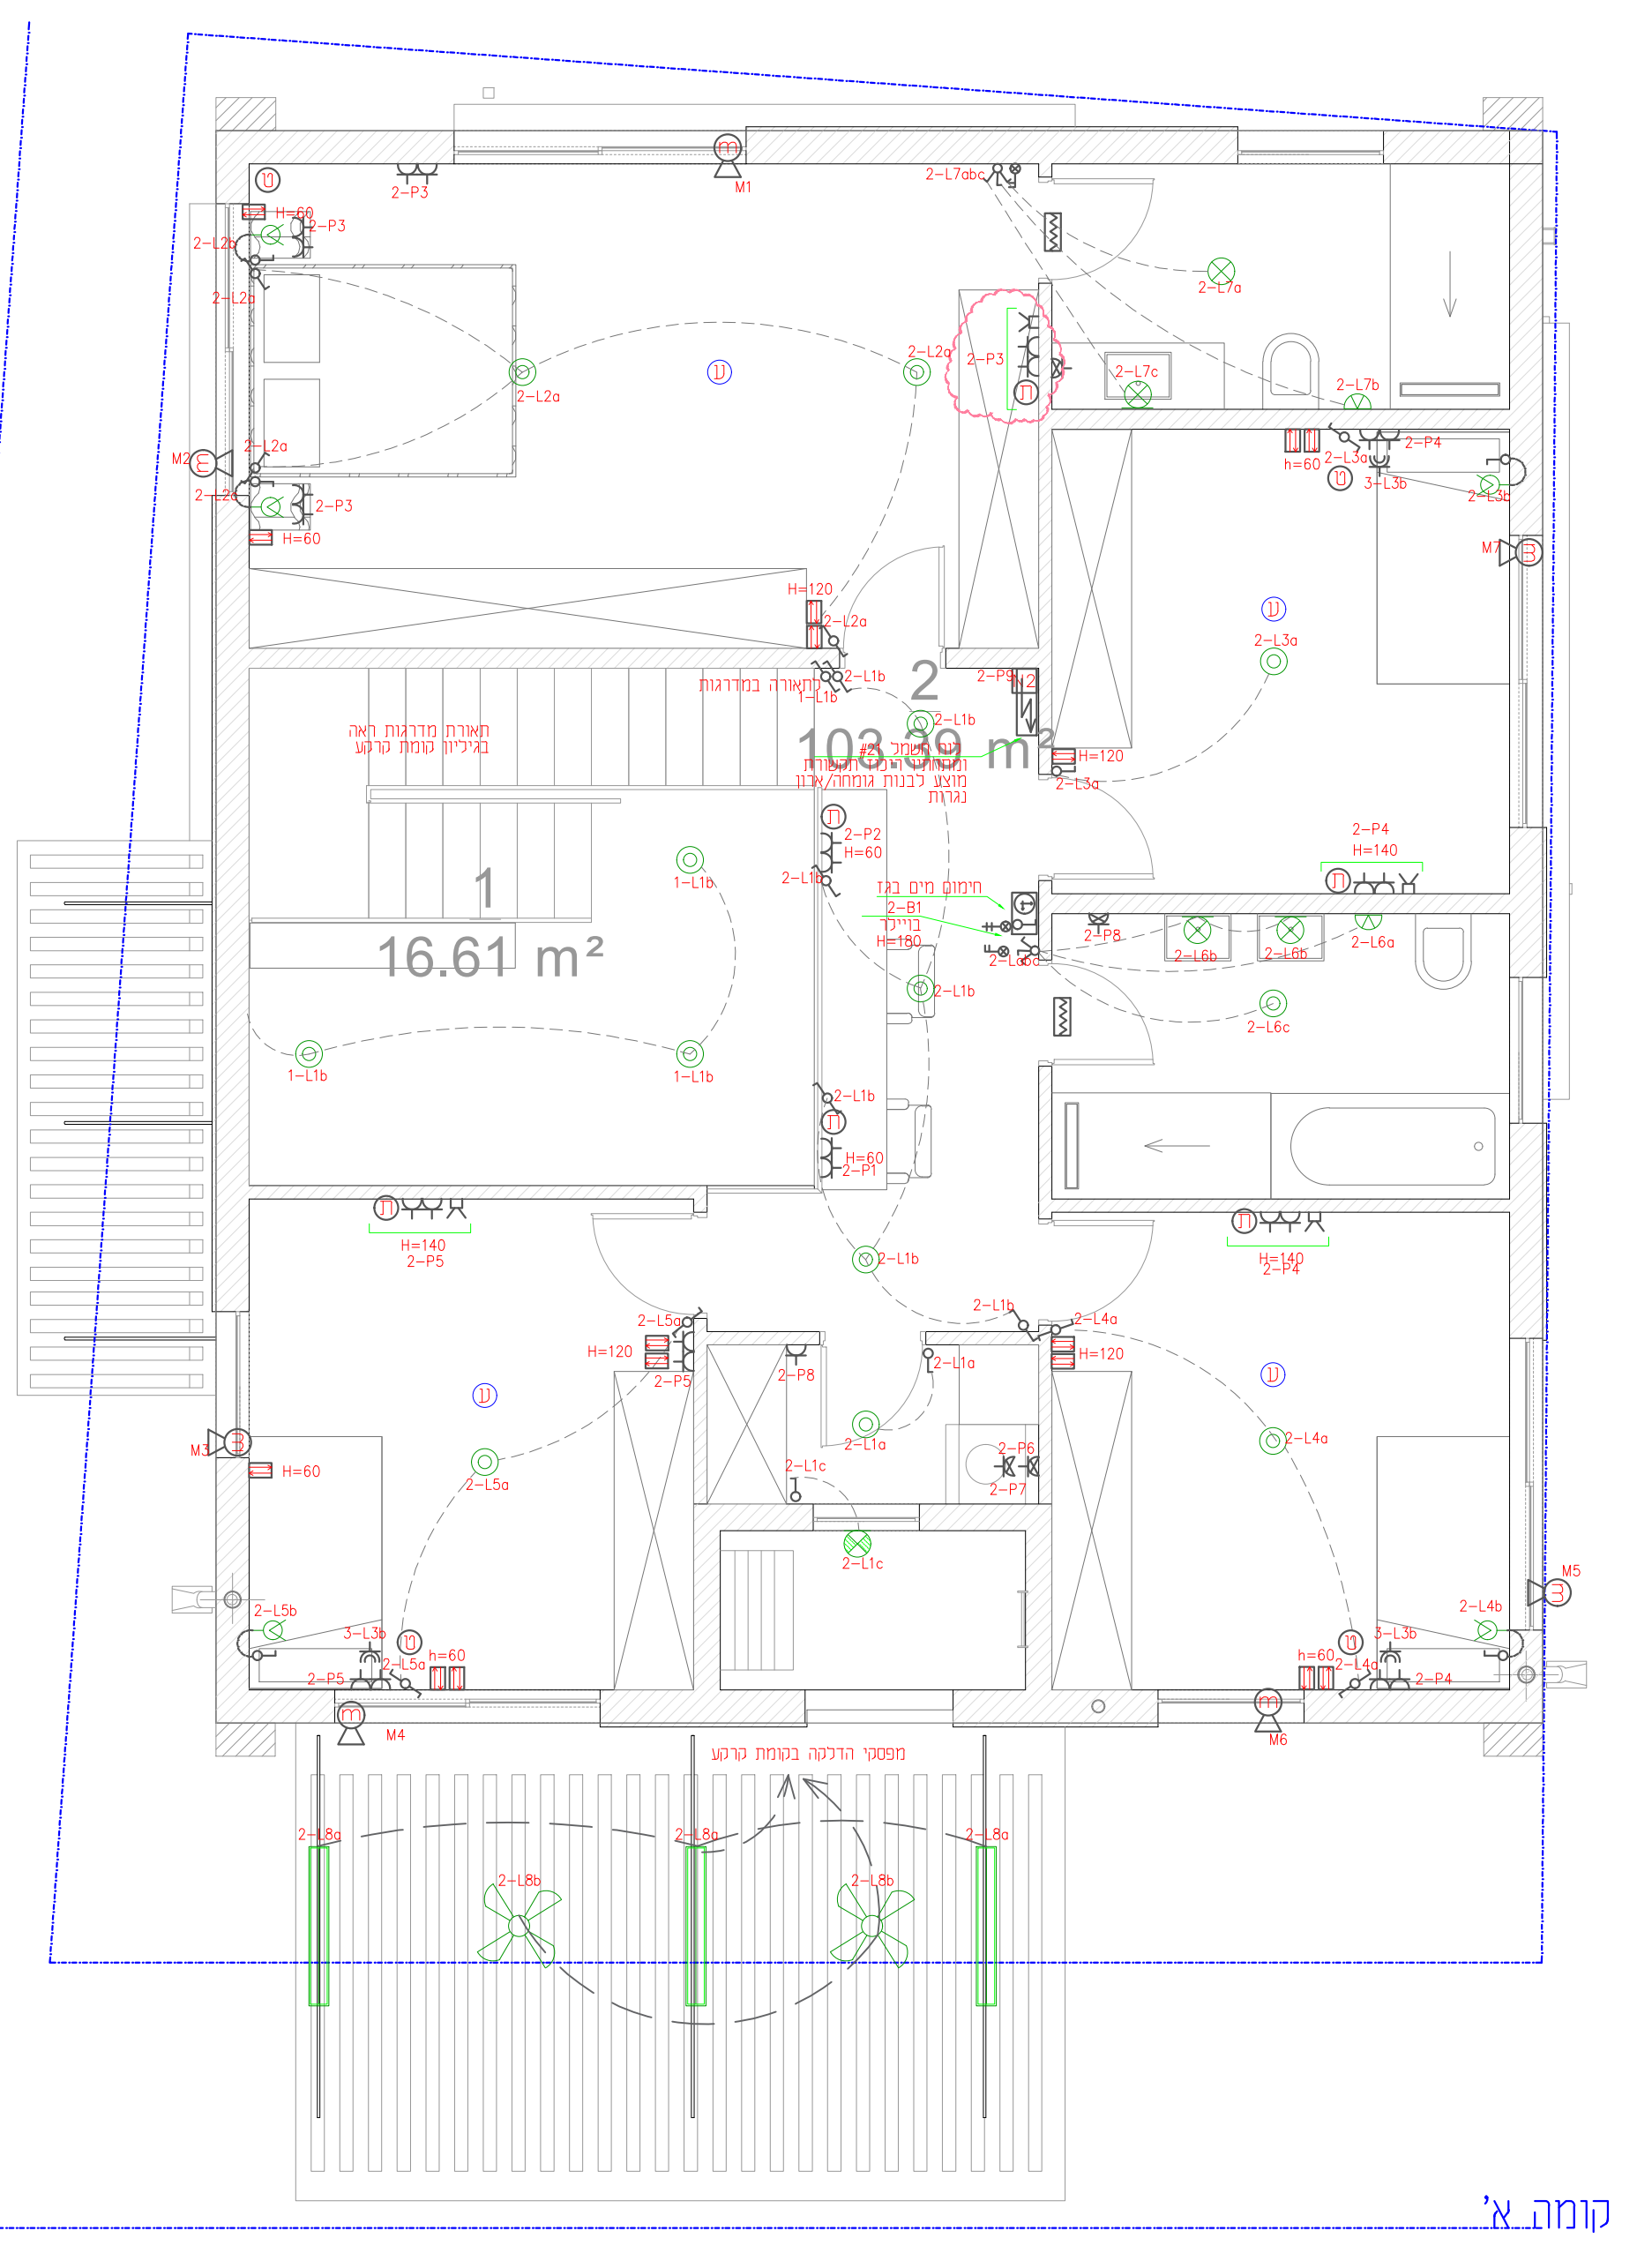

קומה א'

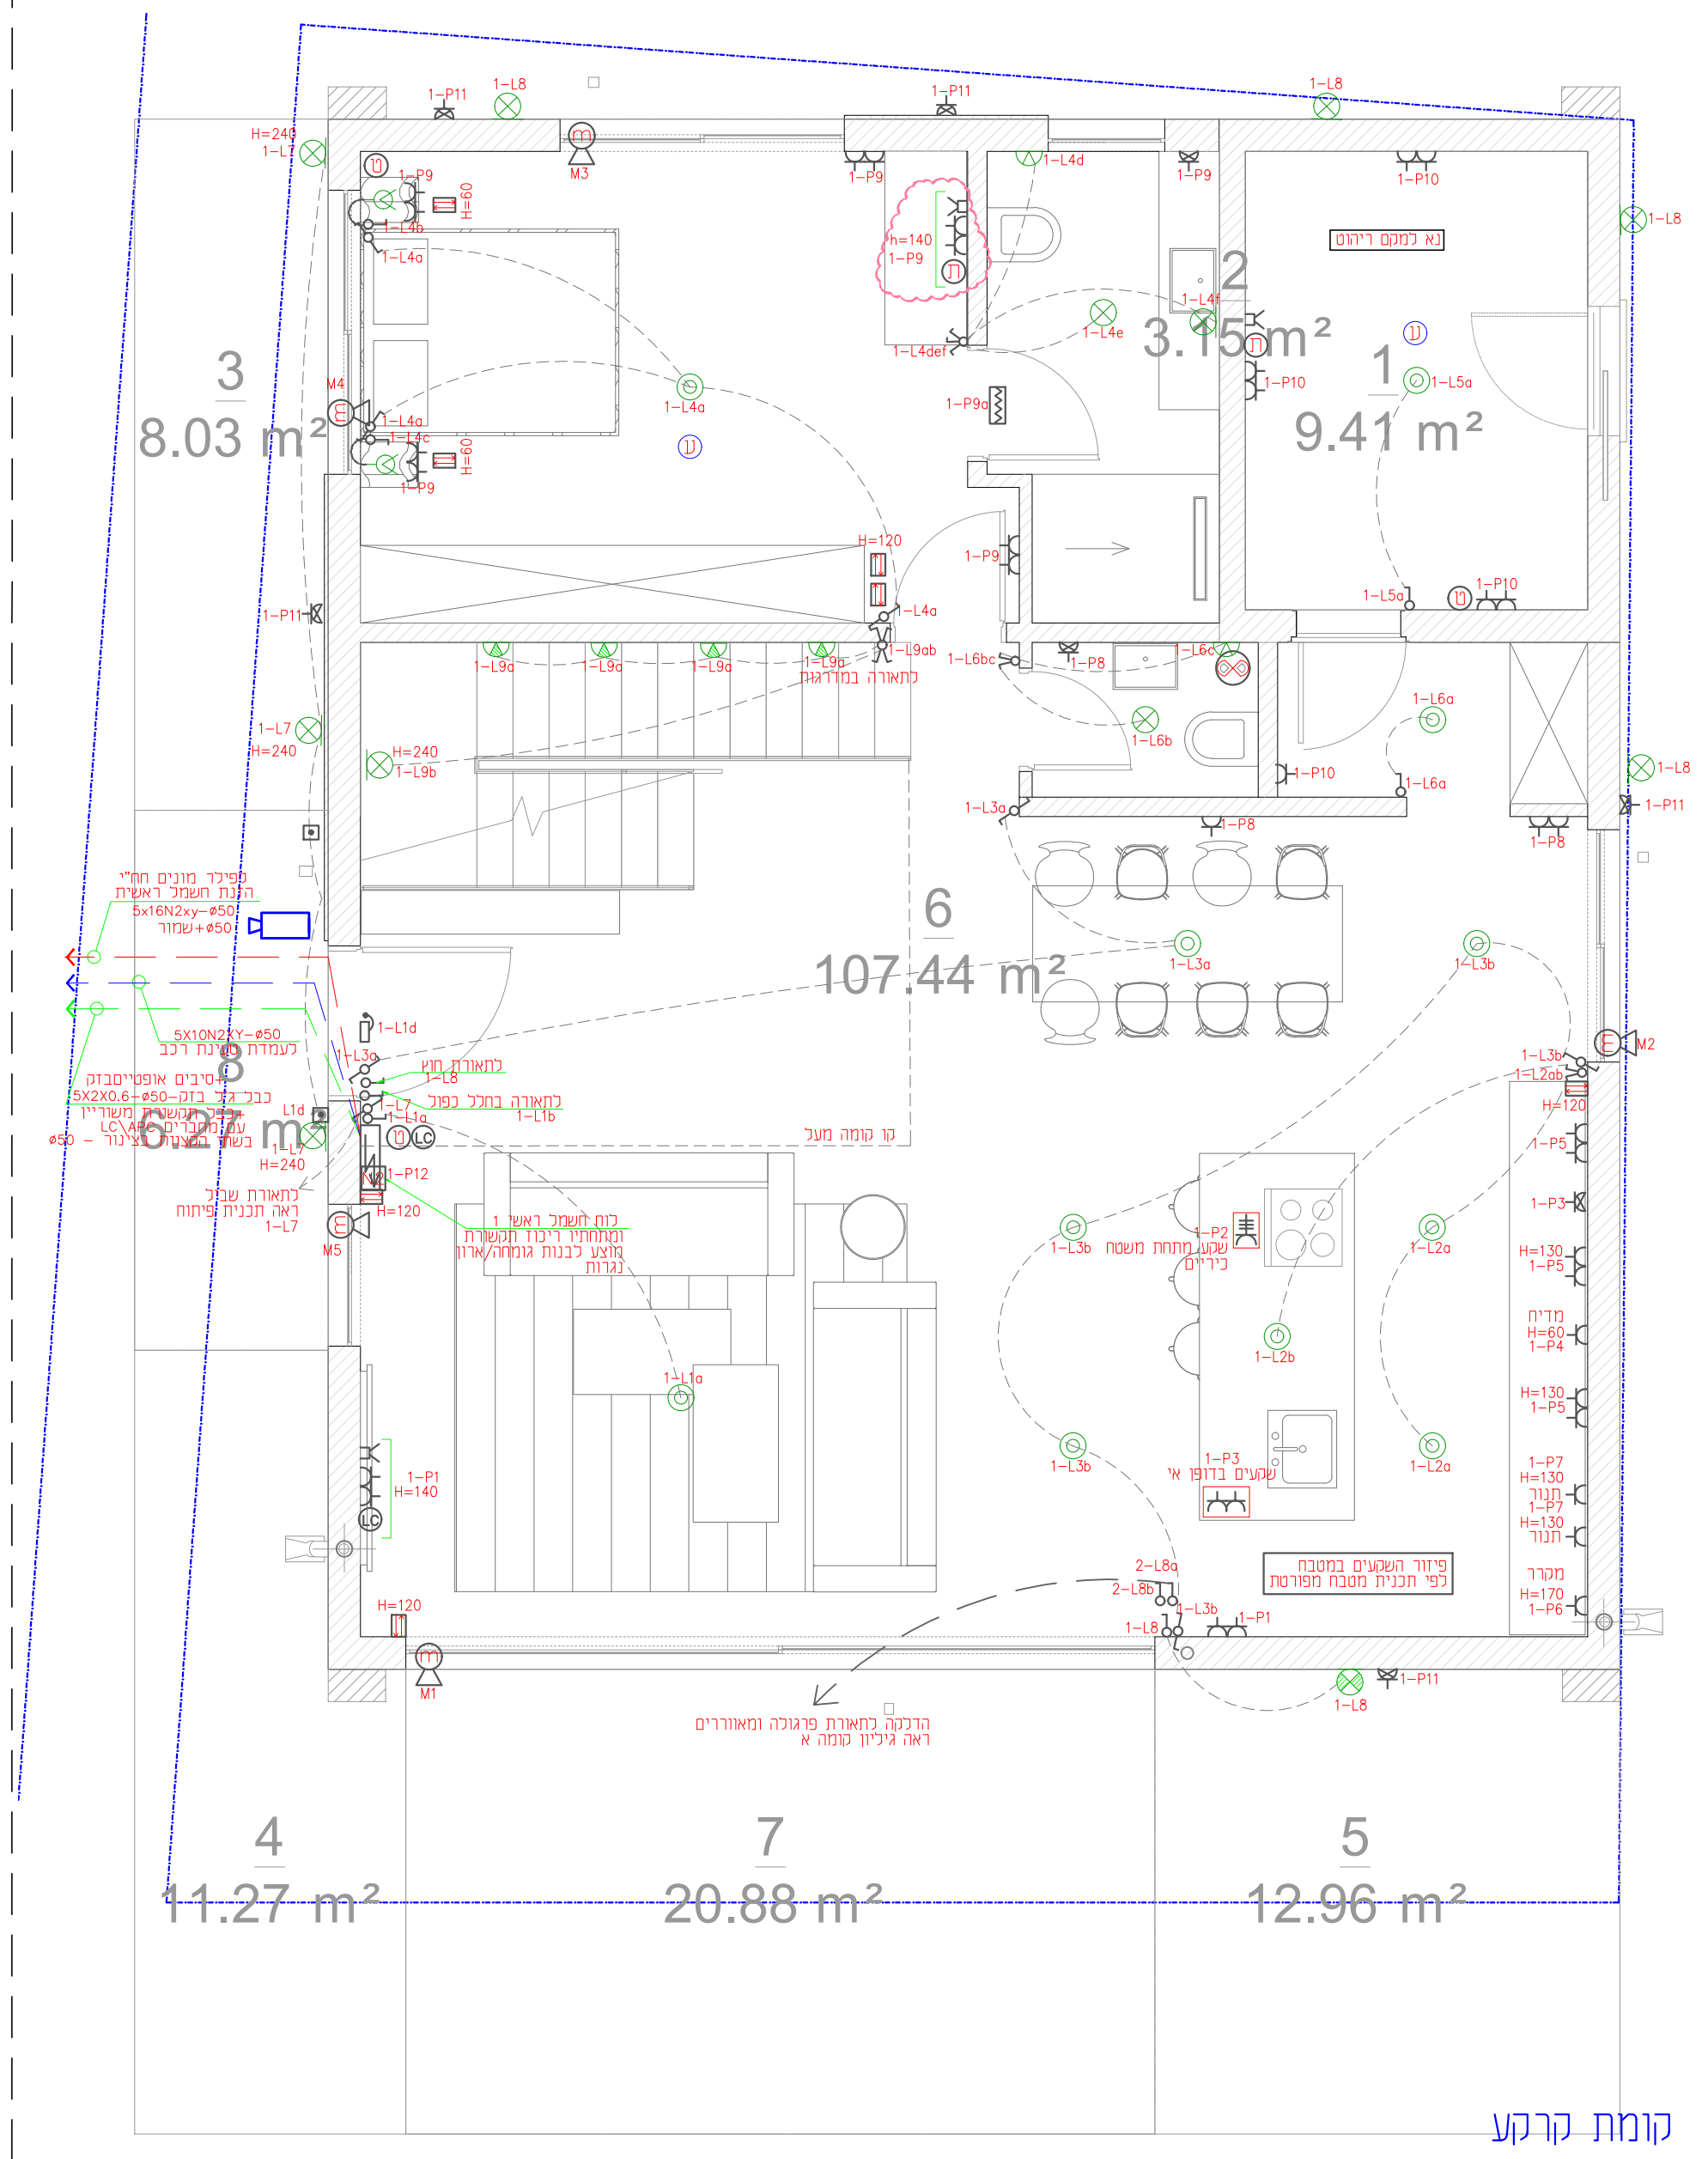

קומת קרקע

מקרא חשמל ותאורה:

לוח		לוח חשמל
חשמל ותקשורת		שקע 16A בודד זוג שקעי 16A — H=60 אלא אם צוין אחרת
	N2	מקבץ שקעים טיפוסי סיום באביזר N2 "ניסקו" בארון תקשורת מתחת לוח חשמל
		שקע חד פאזי מוגן מים H=60 אלא אם צוין אחרת
		שקע ליחידת מ"א 16A H=220 מיקום סופי לפי תכנית מיזוג ובתיאום מול אדריכל
	ט	נקודת טלפון מלאה-צנרת, כבילה ושקע טלפון H=60
		CIMA BOX הכולל: 4 שקעי שרות+2 תקשורת
	ת	נקודת תקשורת H=60, צינור ø25 עם חוט משיכה מריכוז תקשורת דירתי
		נקודת טלויזיה מושלמת+צינור שמור ø20 H=60
	LC	נקודת תקשורת מלאה הכוללת: כבל תקשורת אופטי תקני מותקן בצינור ø25 סיום בית תקע אופטי LC\APD לפי דרישות ת"י 1-11801 עם ראשים מוכנים מראש להתקנה בארון תקשורת דירתי ובסלון עם חוט משיכה מריכוז תקשורת דירתי
	m	מנוע חשמלי H=200
	T	הכנה לתרמוסטט מזגן- צינור 20 לחלל תקרה
	T	תרמוסטט חימום תת רצפתי- יבוצע לפי הנחיות ספק
		שקע לתנור חימום חשמלי 10 סמ מעל פתח דלת
		בויילר
		הכנה לוונטה סיום בשקע
מפסקים		מפסק מאור בודד H=90 מפסק כפול H=90 מפסק מאור מחליף H=90 — אלא אם צוין אחרת במפסקי הדלקה ליד מיטה H=60
		לחצן פעמון דלת H=90
		מנתק מואר 2X16A / 3X16A
		מפסק דו קוטבי מואר לתנור חימום חשמלי H=160
		מפסק הרמה/הורדה לתריס חשמלי 5 סמ מעל מפסק תאורה ע"פ פרט
		מפסק עם שעון בקיר לבויילר H=180
	א	פנל צפיה (מוניטור) +לחצן פתיחה דלת H=120
תאורה וגלאי אש		תאורת חרום חד תכליתית LED 3w
	ע	גלאי עשן בתקרה
		נקודת מאור בתקרה
		ג"ת פנים תקרתי מוגן מים
		ג"ת LED עגול שקוע בתקרה
		ג"ת LED עגול קירי גובה H=220
		ג"ת פנים קירי למנורת לילה H=120
		ג"ת פנים/חוץ קירי מוגן מים H=240 , במרתף H=220
		ג"ת קירי נמוך לתאורת התמצאות מדרגות/שירותים, h=15 מהרצפה /מרום מדרגה
		ג"ת מלבני IP65 להתקנה על פרגולה
		מאוורר להתקנה בחוץ
		פעמון דלת 220V (גונג) התקנה מעל דלת כניסה
		הכנה מצלמה אבטחה, צינור 25 וחוט משיכה מארון תקשורת דירתי

פרט לגבהים של הדלקות, תאורה ותריסים:

חזית לוח חשמל ראשי וארונות תקשורת

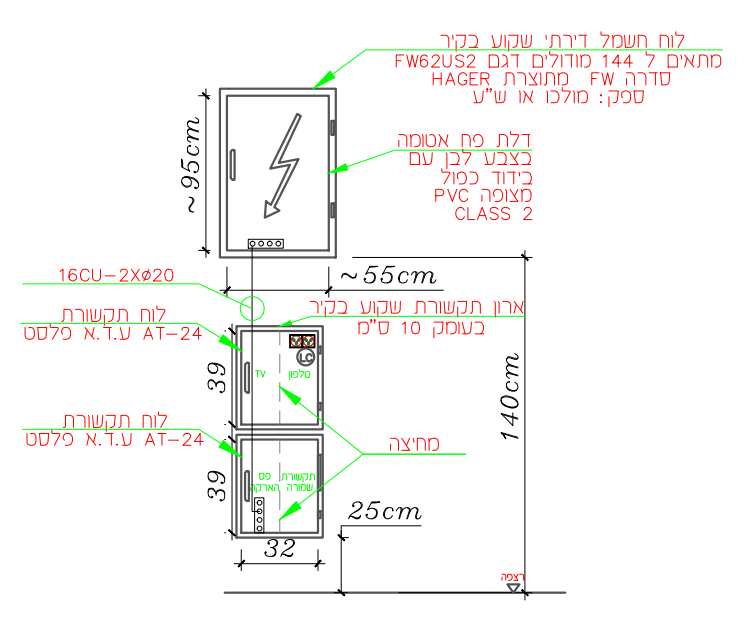

תפוצה														תאריך
מנהל הפרויקט	אדריכל	מזמין/יזם	חשמל	קבלן	בטיחות	אקוסטיקה	אינסטלציה	קונסטרוקציה	אדריכל נוף	מטבחים	חברת חשמל	חברת בזק		

מס'	שינויים	תאריך
1	עדכון תכנית	10.12.24
2	עדכון תכנית	15.12.24
3	עדכון תכנית	24.12.24
4	עדכון תכנית	8.5.24

עודכן ע"י: ליאל

הערות:
- במידה והוחלט על הכנות לבית חכם: כהכנה לבית חכם ולדלת חכמה יש להשחיל חוט 0 כחול נוסף בכל מפסק הדלקה התכנון עצמו יעשה ע"י ספק בית חכם
- הכנות למיזוג אויר,חימום תת רצפתי, מערכות אבטחה, וחימום מים בחשמל יהיו עם הנחיות יועץ לכל תחום141
- יש לקרוא תכנית זו יחד עם תכנית אדריכלות למקרא בלוקים אדריכלות

מעגלים שמורים ליחידות מ"א פנימיות:
1-AC1
1-AC2
1-AC3

הערות:
* כל הגבהים בתכנית הינם למרכז אביזר אלא אם ציין במפורש אחרת
* מיקום סופי לנקודות תאורה ייקבע ע"פ תכנית עיצוב פנים תאורת חוץ- ע"פ יועץ פיתוח
* מיקום סופי לשקעי מיזוג עפ"י תוכנית יועץ מיזוג

א. בסיס
הנדסת חשמל בע"מ
משרד: יד חרוצים 16, ירושלים 93420
טל: 074-7021015 נייד: 050-6550484
פקס: 077-5131015 דוא"ל: office@ebasis.co.il

שם הפרויקט:
נופיה-אלפי מנשה
מגרש 7

שם הגיליון:
תוכנית חשמל טיפוסית

○ לביצוע ○ למכרז ● לאישור ○ לעיון

קנה מידה: 1:50

מס' קובץ: File: 675-7.dwg

תאריך: Date: 15.08.2024

תכנן: איתן
שרטט: אביבה
אישר: איתן

מס' עדכון: 4
מס' הגליון: E
מס' הפרויקט: 675