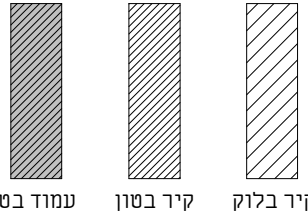


מתכונים:


ניהול פרויקט
מהיסוד - בן סלומון
פיקוח
מהיסוד - בן סלומון
קונסטרוקציה
ערן שילר
מיזוג אוויר
אייל ארז מהנדסים ויועצים בע"מ
אינסטלציה
איתן אלמסי
חשמל
איתן בסיס
אלומיניום
נוף
נתי בלוקא
חשמל חכם
חימום תת רצפתי
איטום
צבי טל
אקוסטיקה
מעליות
קרקע וביסוס
דיה הנדסת קרקע וביסוס
רישוי

[illegible]

מקרא קירות:

[illegible]

אדריכלות

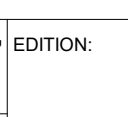CLIENT NAME:		המזכיר	
קבוצת רכישה נופיה			
PROJECT NAME:		הפרויקט:	
נופיה - מגרש 8			
DRAWING NAME:		שם הגרסה:	
גליון שער			
SHEET NUMBER:		מספר הגליון:	
A3-1-100			
SCALE:	קנה מידה:	EDITION:	דפוס:
STATUS:	סטוס		
למכור			
	נבדק עדי:		דפוס עדי:
DATE:	22.09.25		איר:



נופיה - מגרש 8			
מס' גליון	שם גליון	מהדורה	תאריך הפצת מהדורה
A3-1-100	גליון שער	1	22.09.2025
A3-1-101	קומת קרקע	1	22.09.2025
A3-1-102	קומה א	1	22.09.2025
A3-1-103	גג	1	22.09.2025
A3-2-200	חזיתות 1	1	22.09.2025
A3-2-201	חזיתות 2	1	22.09.2025
A3-3-100	חתכים	1	22.09.2025
A3-4-100	גליון מדרגות	1	22.09.2025
A3-4-103	פרטים	1	22.09.2025
A3-4-104	פרטי פרגולה	1	22.09.2025
A3-6-1000	רשימת פתחים	1	22.09.2025



וימן חיינר אדריכלים
מורד ההדרים 2, בית 1
טל 09-9545842

אורד ההדרים 2, בית חירות
טל 09-9545842

זכויות ייצור / ע"פ הנחיות עו"ד

ניהל פרויקט
מהיסוד - בן שלומון
פיקוח
מהיסוד - בן סולומון
קונסטרוקציה
ערן שילר
מיזוג אוויר
אייל ארז מהנדסים ויועצים בע"מ
אינסטלציה
איתן אלמסי
חשמל
איתן בסיס
אלומיניום
נוף
נתי בלוקא
חשמל חכם
חימום תת רצפתי
איטום
צבי טל
אקוסטיקה
מעליות
קרקע וביסוס
דיה הנדסת קרקע וביסוס
רישוי

הערות:
 1. הכנית זו איש קלודו יחד עם הכנית העופשית.
 2. גבוב אבסורסוטי, ראו הכנית פרחו.
 3. המרתה חן בין הכנית הבניה (ראו כלול סיח).
 4. פיתוח השטח פסח חנה הבניה, כלול, מדגות, שרילוס, ריצופים,
 5. פוטופים בניה וקולו-ראו הכנית פרחו.
 6. אסוריקי רופצת חנה הבניה בניה וקולו-ראו הכנית פרחו.
 7. הכנית רופצת חנה הבניה בניה וקולו-ראו הכנית פרחו.
 8. אף חנה ביוצא בניה אופיק חנה הבניה.
 9. סיח חנה במחנה-ניפ פסח חנה הבניה, מאושר עיי פיקוד העורף.

הסכנת אחרי יסודות: עליו לקבל בדיוק את כל החדות הכתובת ובמקום הנבחר.

בדקור של שטח או שטח של התחביר הכתיב ו/או גביו, עליו להודיע על כך בכתב.

התחביר יתקבל על ידי חתום או חתימה.

הסכנת יסודות אחרי: כל כת, עליו שדורש כל הכתיב.

אין לקבל דיוק על ידי חתום בפרט.

התחביר יהיה חתום האדריכל או חתום של כל שטח או כל פרטיות.

התחביר יהיה, אלא שכל כתוב האדריכל.

חתימה או חתום של פרטיות הכתיב, ושם לבדו באחריות.

הסכנת יסודות הכתיב.

הסכנת הבקבול והתחביר האחריות האחריות על כל גרסאות חתומים.

לחתימה יהיה, התחביר הכתיב האחריות על כל גרסאות חתומים.

הסכנת כלות כלל האחריות הדיוק על ידי חתום.

עמוד בטון קיר בטון חלוק

[illegible]


PROJECT NAME:		הפרויקט:	
קבוצת רכישה נופיה נופיה - מגרש 8			
DRAWING NAME:		שם הציור:	
קומת קרקע			
SHEET NUMBER:		מספר גיליון:	
A3-1-101			
SCALE:	קנה מידה:	EDITION:	דפוס:
1 : 50	מספרים	1	דפוס ע"י:
STATUS:	מצב	נבדק ע"י:	תאריך:
למכר			
DATE:		22.09.25	

NeumanHaynerArchitects

office@nh-arch.com
www.nh-arch.com

יומן חיינר אדריכלים
בית חירות 2, החדרים
09-9545842

1. יש לעבוד במקביל לתכניות יועצים המאפשרות על ידי האדריכל.
2. פרטי ספי חלון - עפ"י חוברת אלומיניום של הספק הנבחר ובתיאום מול אדריכל.
3. חימום תת רצפתי (במידה ויש במגרש זה) עפ"י פרטי הספק ובתיאום מול אדריכל.
4. יש לעבוד במקביל לתכניות עיצוב פנים (במידה ויש מעצב פנים במגרש זה) המאפשרות על ידי האדריכל
5. באחריות הקבלן לעדכן את האדריכל על אי התאמה בין התכניות יועצים לאדריכלות.
6. כל הדלתות לפי מפרט מצורף.
7. כל אלמנטי הבטון יקבלו התייחסות תרמית לפי הנחיות יועץ.
8. פרטי איטום, בידוד וניקוז עפ"י תכניות יועצים ובאחריות הקבלן.

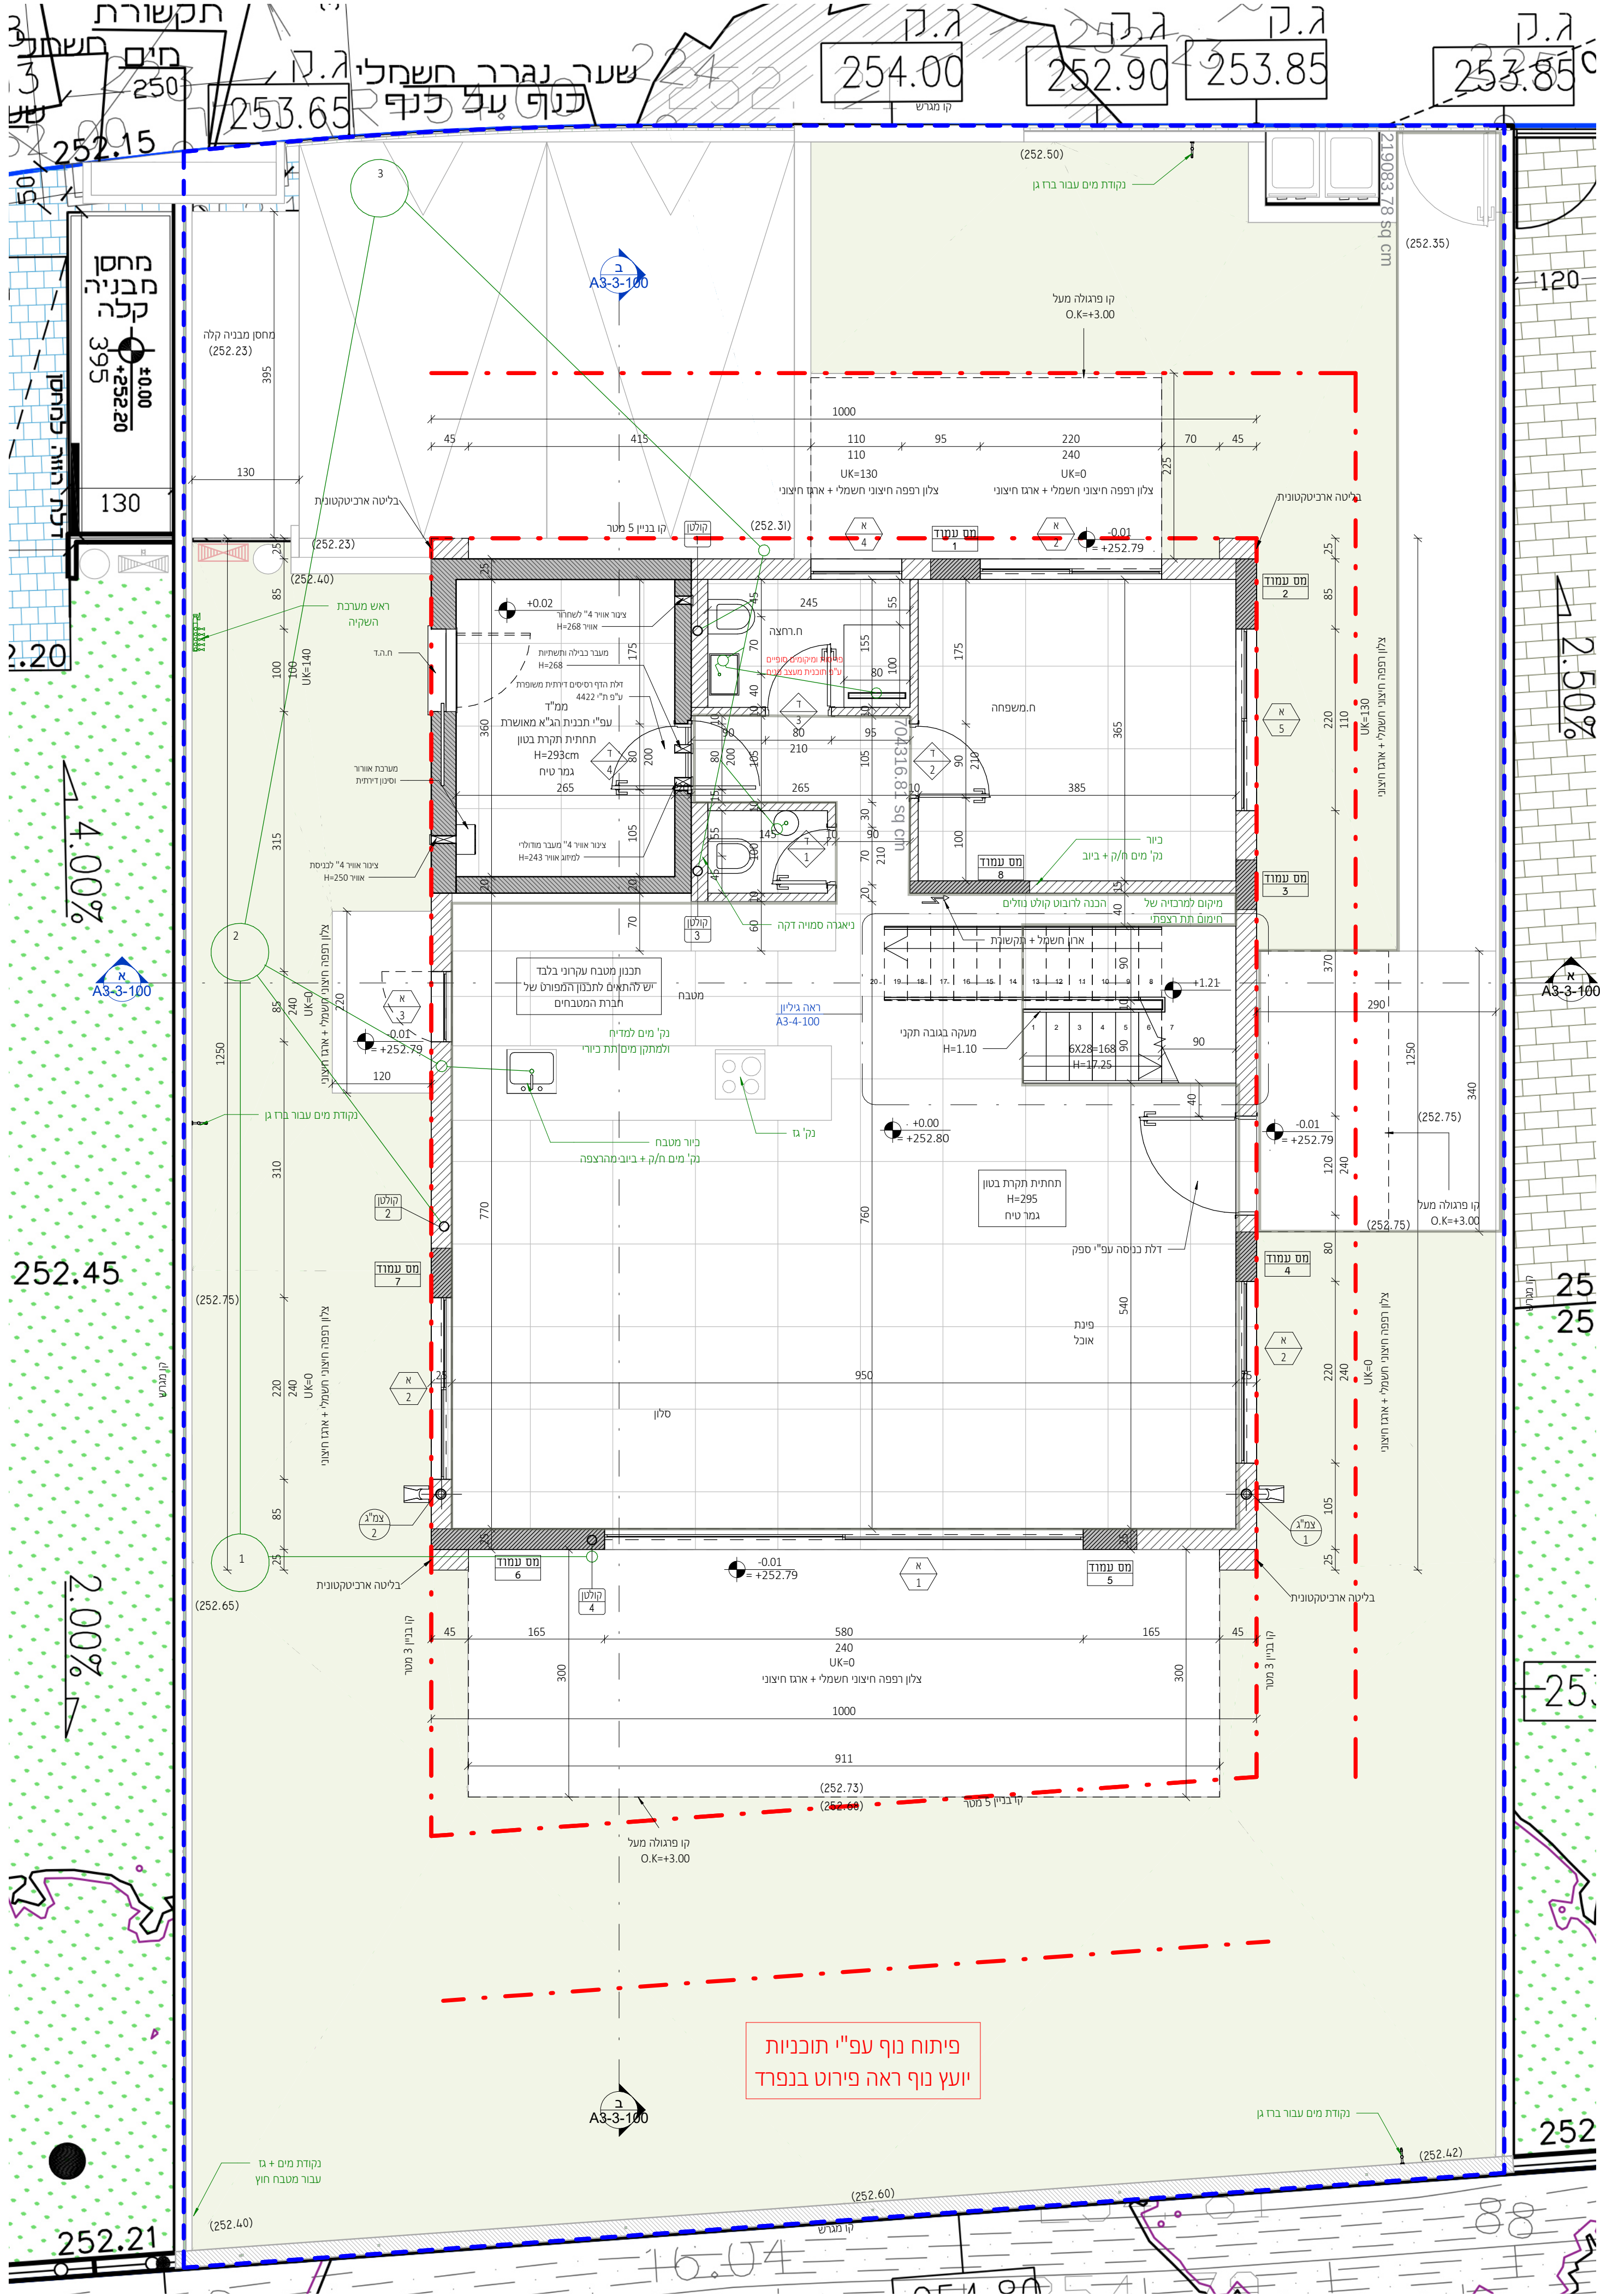

1 : 50

ניהול פרויקט	
מהיסוד - בן סלומון	
פיקוח	
מהיסוד - בן סולומון	
קונסטרוקציה	
ערן שילר	
מיוזג אוויר	
אייל ארז מהנדסים ויועצים בע"מ	
אינסטלציה	
איתן אלמסי	
חשמל	
איתן בסיס	
אלומיניום	
נוף	
נתי בלוקא	
חשמל חכם	
חימום תת רצפתי	
איטום	
צבי טל	
אקוסטיקה	
מעליות	
קרקע וביסוס	
דיה הנדסת קרקע וביסוס	
ירשני	

[illegible]

עמוד בסון קיר בסון ר בלוק

אדריכלות

קבוצת רכישה נופיה

בופיה - מגרש 8

קומה א

A3-1-102


ברז

NeumanHaynerArchitects

ימון חיינר אדריכלים
 בורד ההדורים 2, בית חירות
 09-9545842 ל'

office@nh-arch.com
 www.nh-arch.com

1. יש לעבוד במקביל לתכניות יועצים המאושרות על ידי האדריכל.
2. פרטי ספי חלון - עפ"י חוברת אלומיניום של הספק הנבחר ובתיאום מול אדריכל.
3. חימום תת רצפתי (במידה ויש במגרש זה) עפ"י פרטי הספק ובתיאום מול אדריכל.
4. יש לעבוד במקביל לתכניות עיצוב פנים (במידה ויש מעצב פנים במגרש זה) המאושרות על ידי האדריכל.
5. באחריות הקבלן לעדכן את האדריכל על אי התאמה בין התכניות יועצים לאדריכלות.
6. כל הדלתות לפי מפרט מצורף.
7. כל אלמנטי הבטון יקבלו התייחסות תרמית לפי הנחיות יועץ.
8. פרטי איטום, בידוד וניקוז עפ"י תכניות יועצים ובאחריות הקבלן.

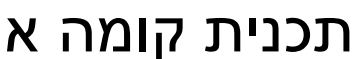


פרטי איטום, בידוד וניקוז עפ"י תכניות יועצים ובאחריות הקבלן

מתכונים:

ניהול פרויקט
מהיסוד - בן סלומון
פיקוח
מהיסוד - בן סלומון
קונסטרוקציה
ערן שילר
מיזוג אוויר
אייל ארז מהנדסים ויועצים בע"מ
אינסטלציה
איתן אלמסי
חשמל
איתן בסיס
אלומיניום
נוף
נתי בלוקא
חשמל חכם
חימום תת רצפתי
איטום
צבי טל
אקוסטיקה
מעליות
קרקע וביסוס
דיה הנדסת קרקע וביסוס
רישוי

[illegible][illegible]

אדריכלות

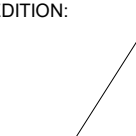
LIENT NAME:		המזכיר:	
קבוצת רכישה נופיה			
PROJECT NAME:		שם הפרויקט:	
נופיה - מגרש 8			
DRAWING NAME:		שם הגליון:	
חזיתות 1			
SHEET NUMBER:		מספר הגליון:	
A3-2-200			
SCALE:	קנה מידה:	EDITION:	חזרה:
1 : 50			
STATUS:	סטטוס		
למכר			
	נבדק ע"י:		דפוס ע"י:
DATE:	22.09.25		תאריך:

NeumanHaynerArchitects


וימן חיינר אדריכלים
 וורד ההדסים 2, בית חירות
 09-9545842 טל

office@nh-arch.com
 www.nh-arch.com

זכויות ייצור / ע"פ הנחיות עו"ד

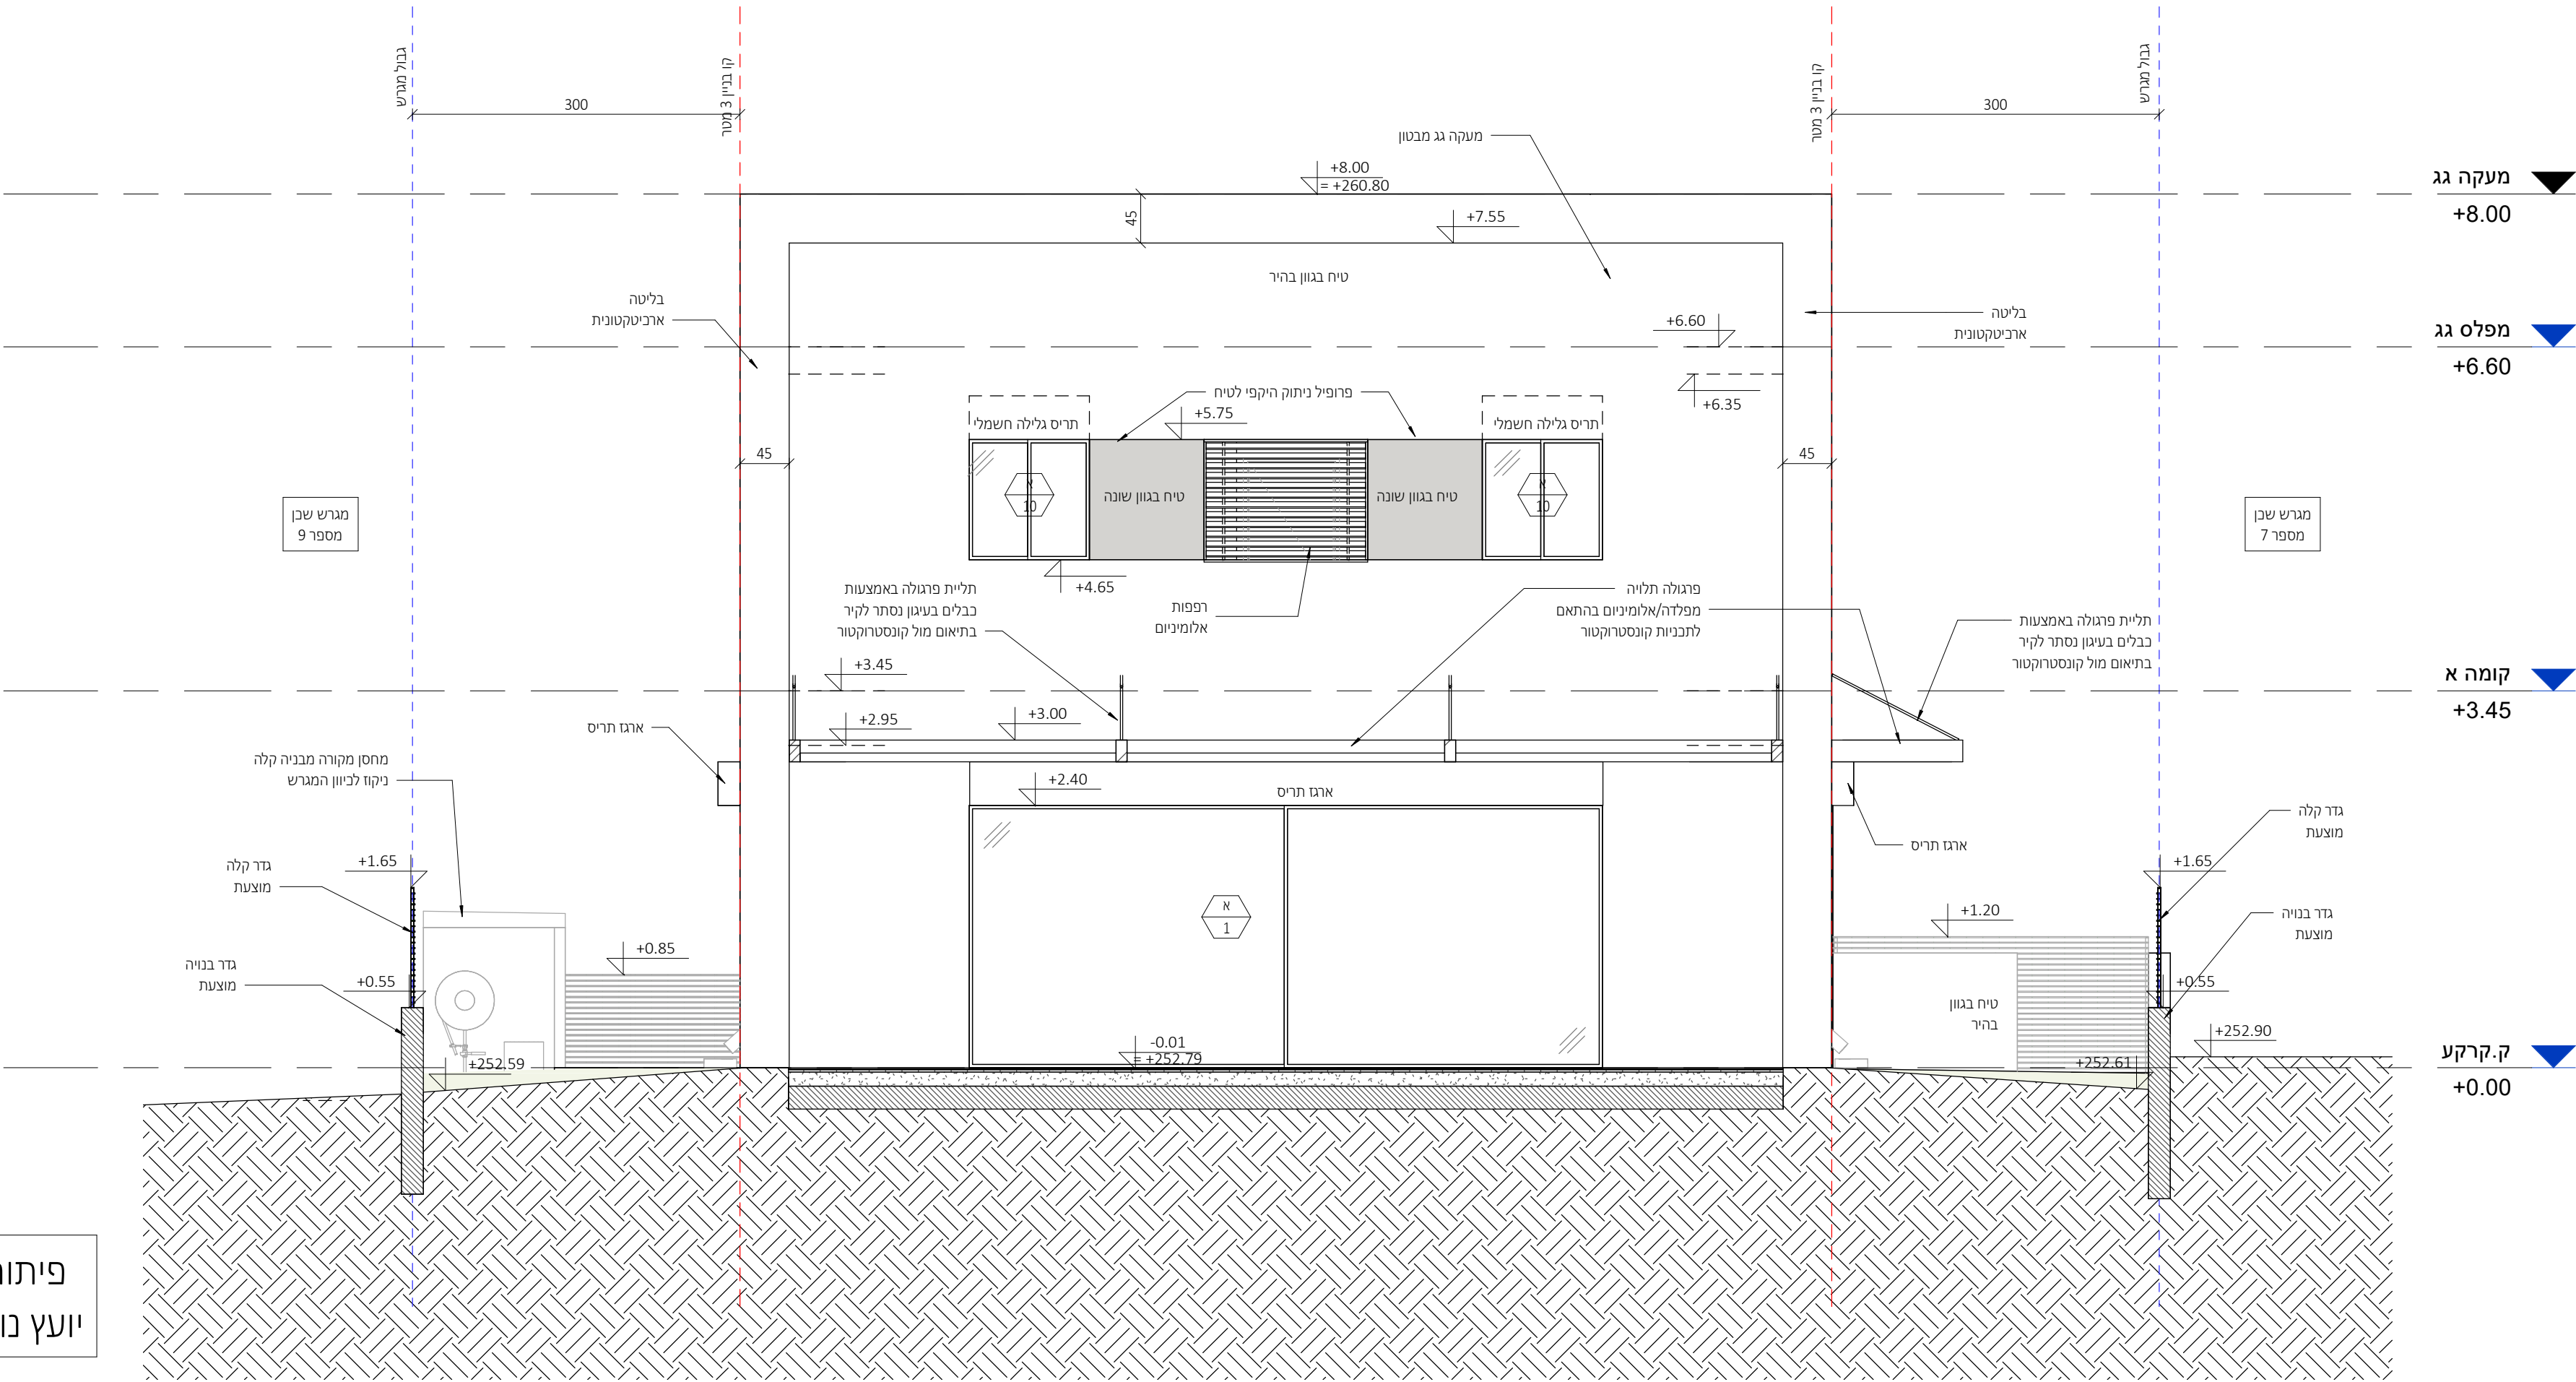

פיתוח נוף עפ"י תוכניות
יועץ נוף ראה פירוט בנפרד

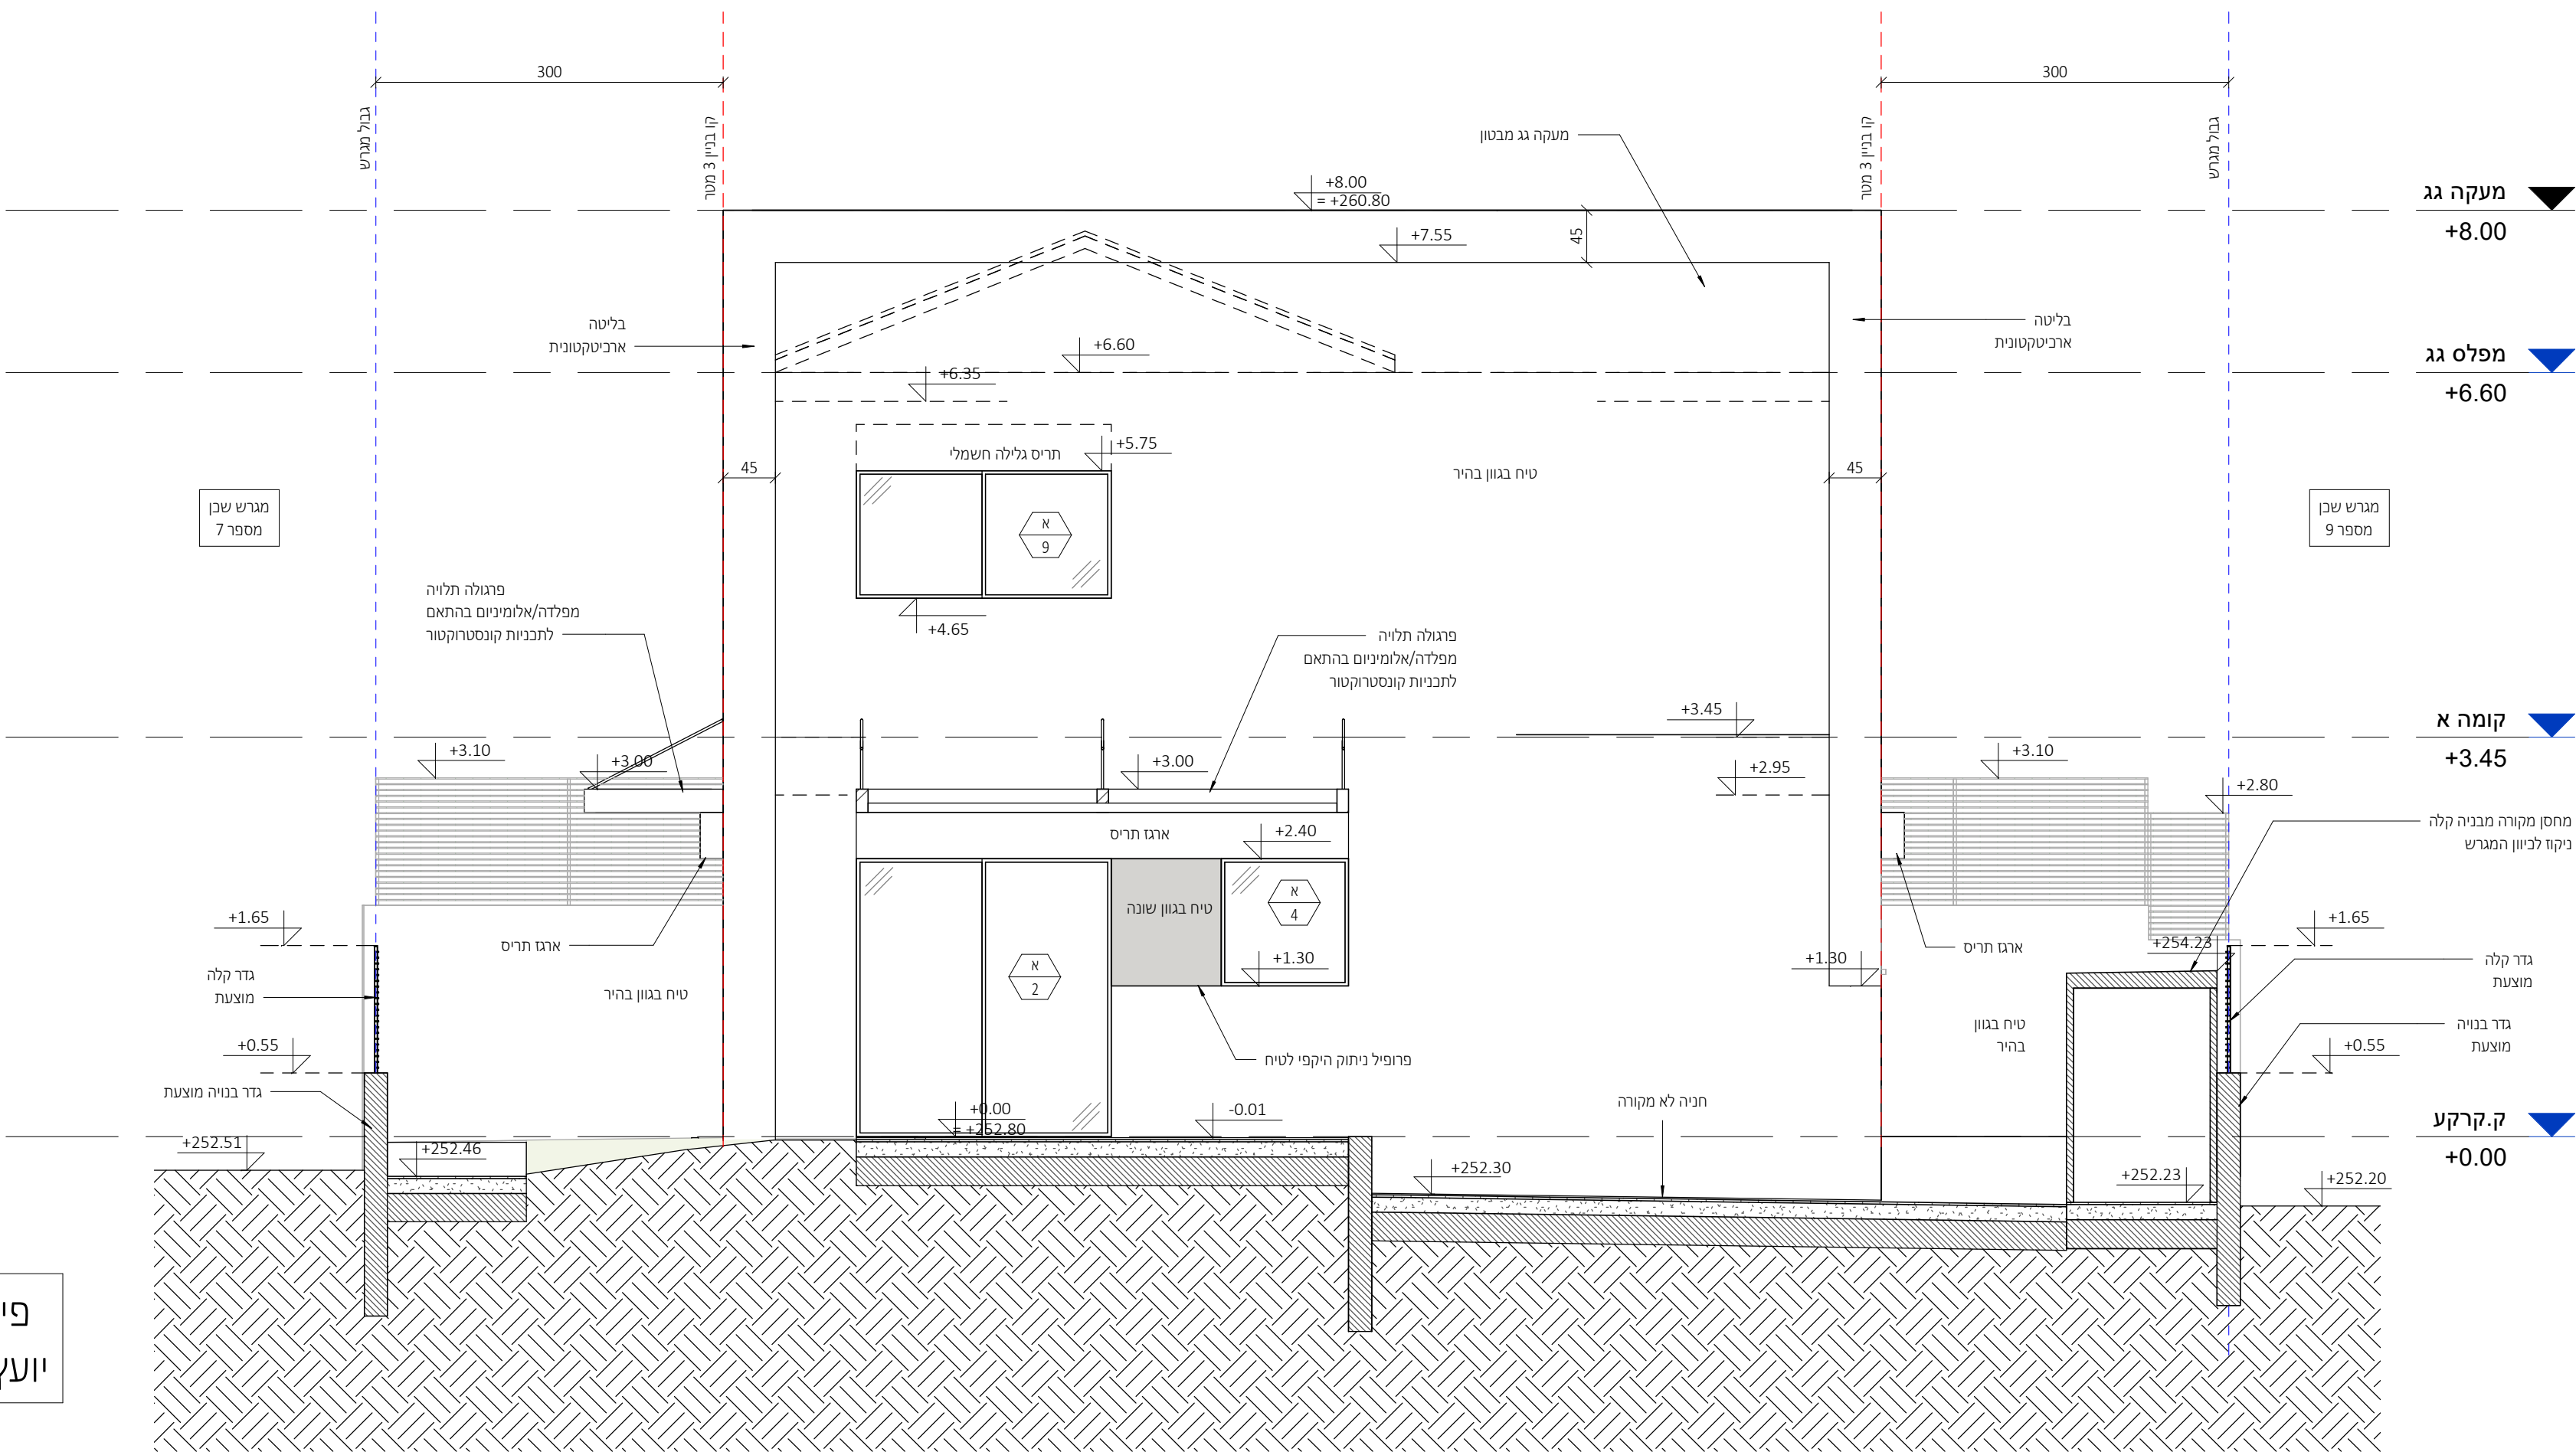

פיתוח נוף עפ"י תוכניות
ועץ נוף ראה פירוט בנפרד


חזית דרומית

1 : 50


חזית צפונית

1 : 50

פרטי איטום, בידוד וניקוז עפ"י תכניות יועצים ובאחריות הקבלן

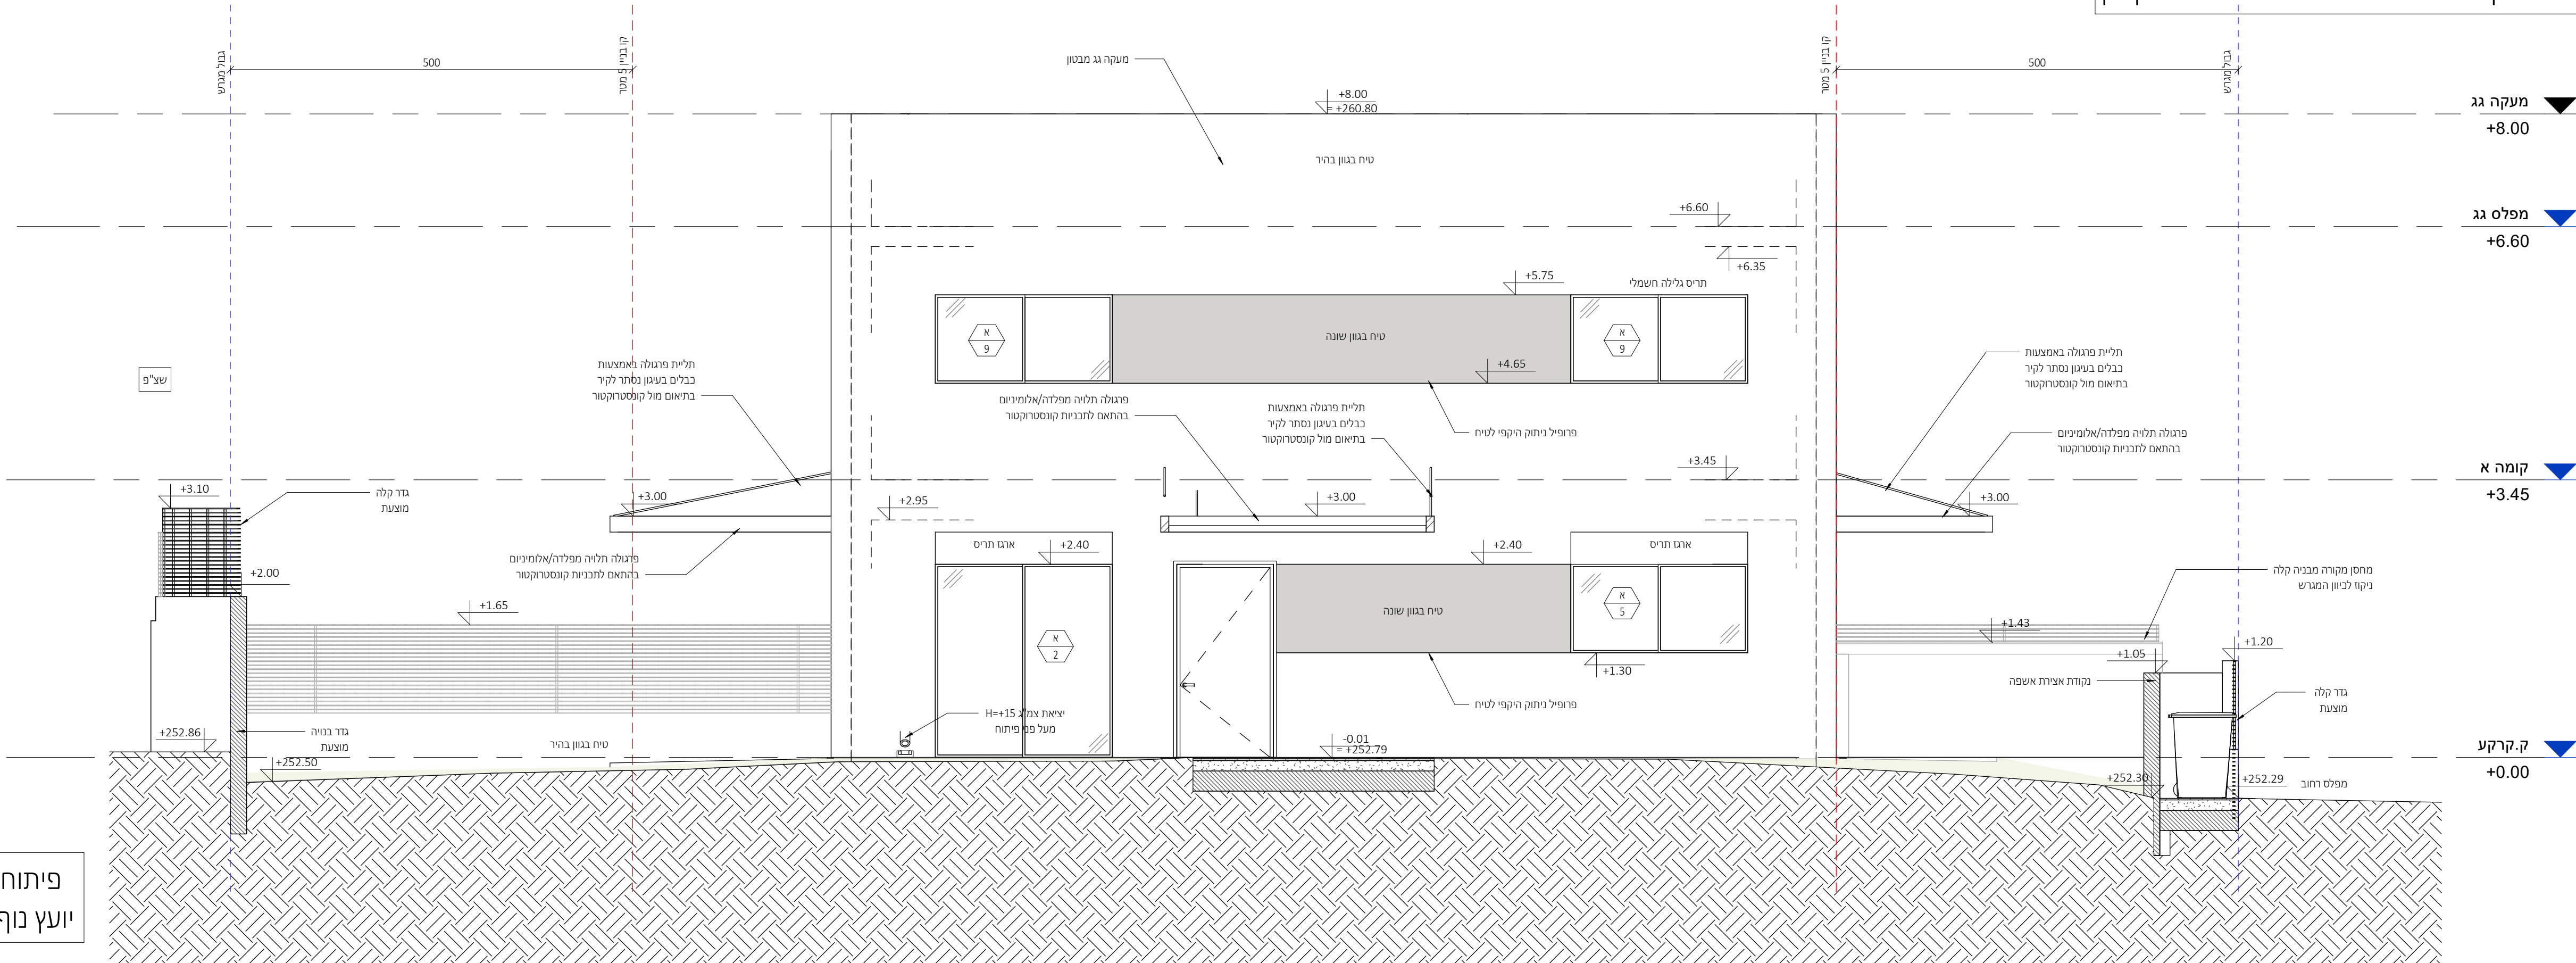

פיתוח נוף עפ"י תוכניות
ועץ נוף ראה פירוט בנפרד

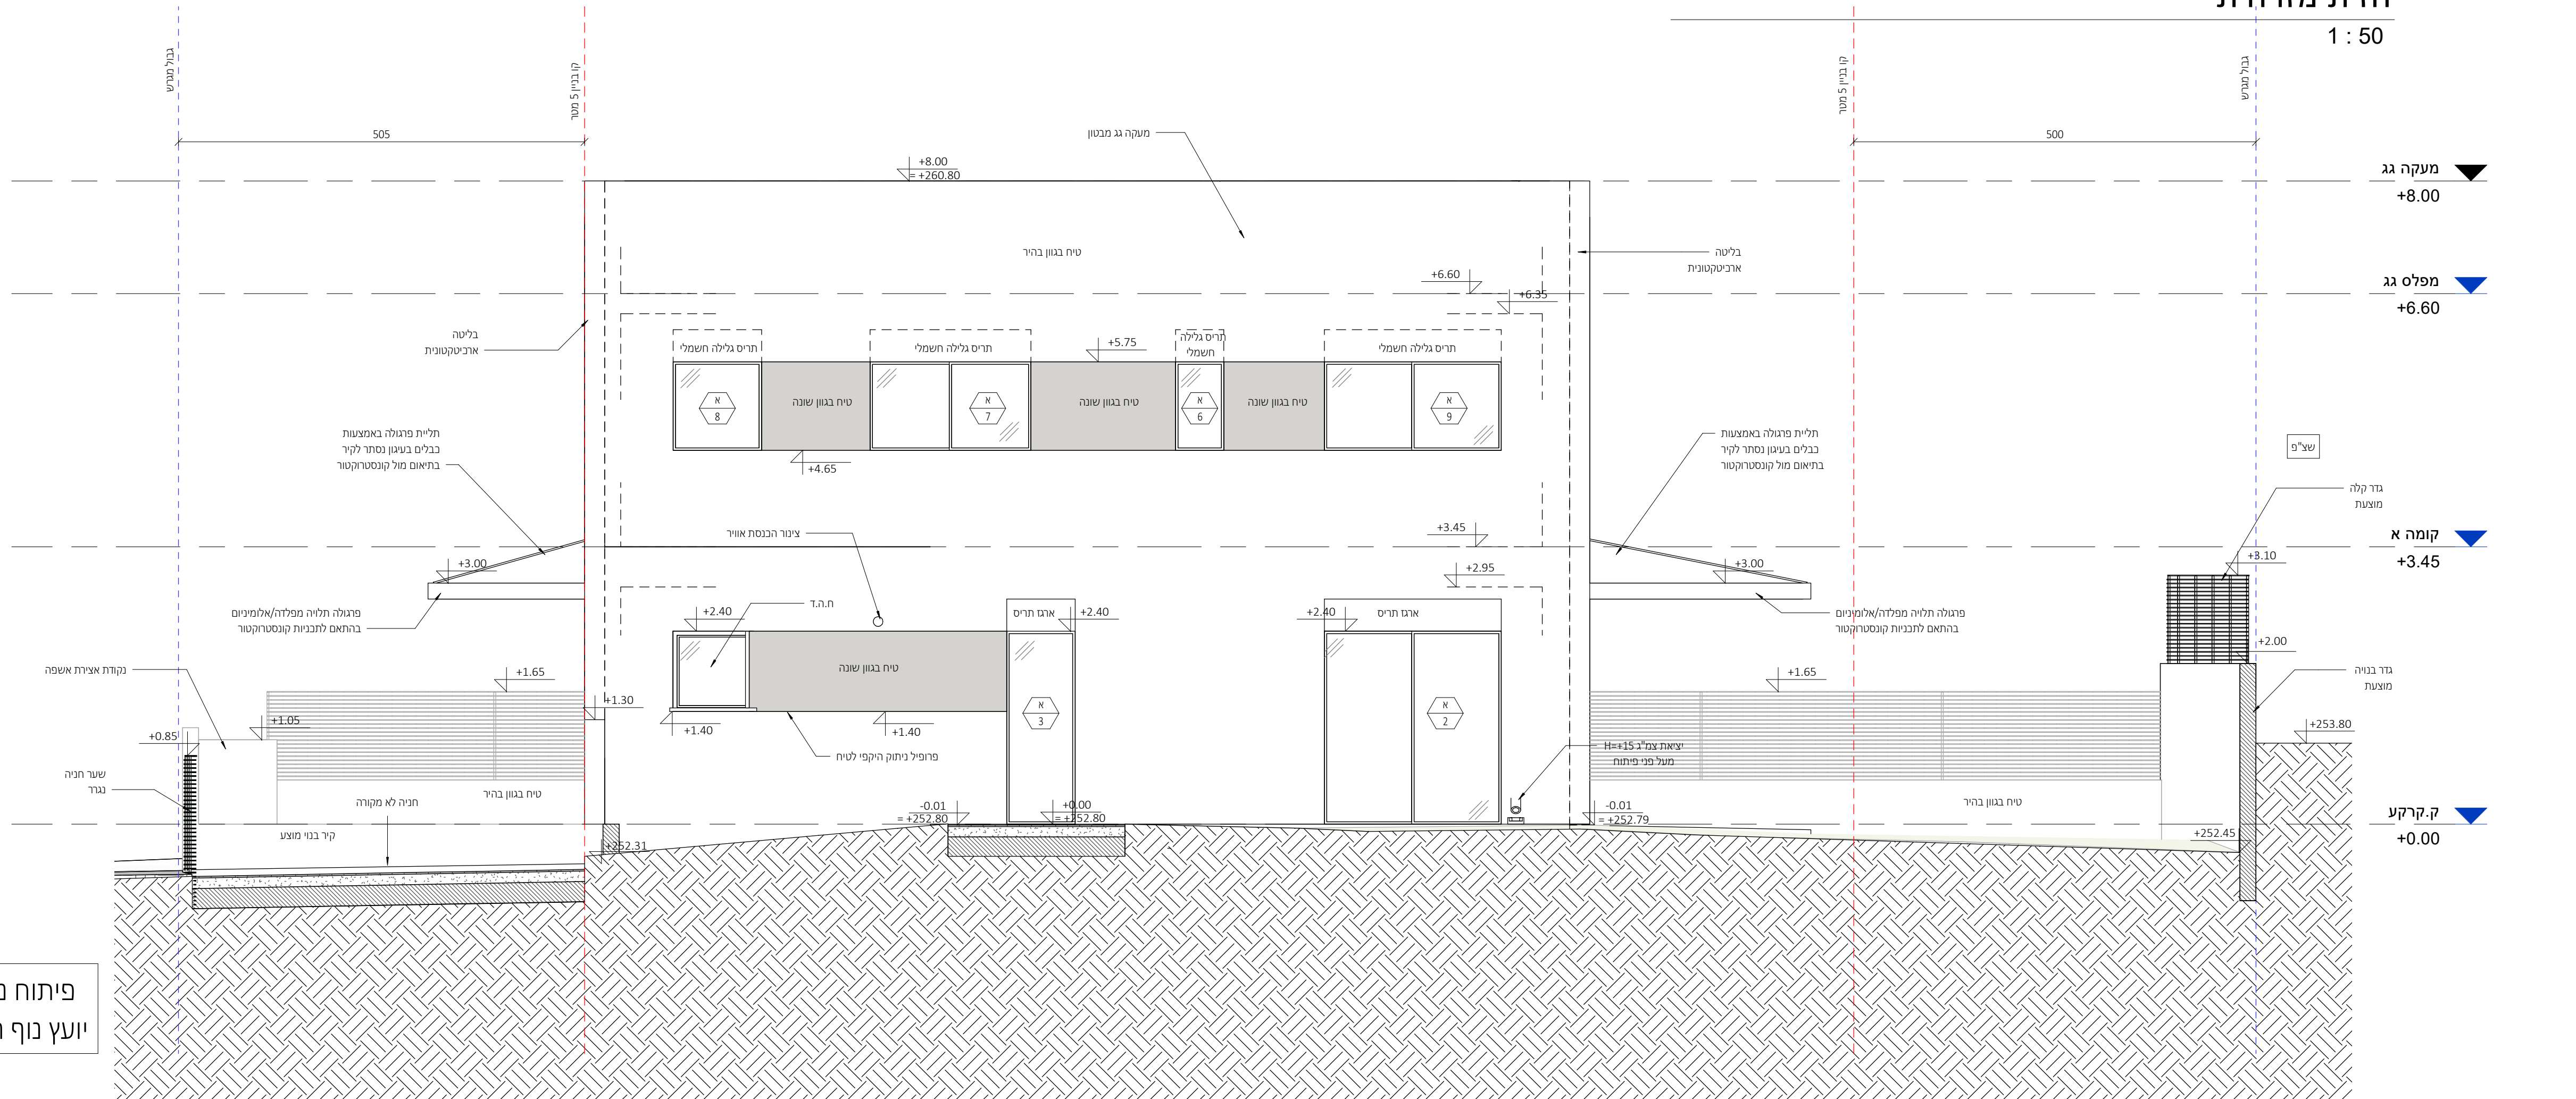

פיתוח נוף עפ"י תוכניות
עץ נוף ראה פירוט בנפרד

חזית מערבית

1 : 50

ניהול פרויקט
מהיסוד - בן שלומון
פיקוח
מהיסוד - בן שלומון
קונסטרוקציה
ערן שילר
מיוזג אוויר
אילי ארז מהנדסים ויועצים בע"מ
אינסטלציה
איתן אלמסי
חשמל
איתן בסיס
אלומיניום
נזף
נתי בלוקא
חשמל חכם
חימום תת רצפתי
איטום
צבי טל
אקוסטיקה
מעליות
קרקע וביסוס
דיה הנדסת קרקע וביסוס
רישוי

[illegible][illegible]

תאריך:		מספר:	
שם:		חומר:	
צבע:		מידות:	
1 : 50		1	
לוח:			
מספר:		חומר:	
22.09.25		17	

מתכננים:

ניהול פרויקט
מהיסוד - בן סלומון
פיקוח
מהיסוד - בן סולומון
קונסטרוקציה
ערן שילר
מיזוג אוויר
אייל ארז מהנדסים ויועצים בע"מ
אינסטלציה
איתן אלמסי
חשמל
איתן בסיס
אלומיניום
בנף
נתי בלוקא
חשמל חכם
חימום תת רצפתי
איטום
צבי טל
אקוסטיקה
מעליות
קרקע וביסוס
דיה הנדסת קרקע וביסוס
רישוי


± 0.00 = +252.80
הערות: 1. תכנית זו יש לקרוא יחד עם תכנית הרוטטים. 2. גובה אבסולוטי - ראו תכנית פיתוח. 3. המידות הן בין קירות הבניה ולא כולל פיתח. 4. פיתוח השטח סביב הבנוה, כולל, מדרגות, גדרות, שבילים, ריצופים, שטחים גרוהם, חניה וגן ראו תכנית פיתוח. 5. איסוס קירות ורצפות הבנוה כמעט עם הקרקע ובנידוד תחסי לאורך העמודים והקורות ופלט המיקות. כליות או עם סימני גיטון - ראו תכנית קונסטרוקציה. 6. אף חיס יבוצע בכל מישור אופקי הבולם חתוכין. 7. סית חתמי במסיד - ע"פ מפרט חומרים, מאושר ע"י פיקוח העורך. המבצע אחראי לסידות : עליו לבקר ולבדוק את כל המידות בתכנית ובקשות הבנייה. במסגרת של מטרות או אי התאמה בתכנית /או בבנוי, עליו להודיע על כך מיד לאדריכל בסופו המשיך בעבודותיו. המבצע ישתמש או ויק בתכנית שאושרו לכניסיו. המבצע יחזיק אחרא, לכל מה, של משרדו של תכנית. אח לקבוע מידות על ידי חזירה בשו שום. התכנית הנה רעיון האדריכל ואין לשנות כל שימוש בה או ברעיונות הגלומים בה, אלא באישור כתוב מהאדריכל. המבצעים והמקיות לתכנית. על המפקח והמקין לוודא התאמת התכנית האדריכלית "כניסיו" לתכנית יחית, המכר והתכנית הואושרות ע"י כל גורמים הרשמיים. התכנית כוללת את כל האמצעים והידוע עד ליום תחמאת.

משרד קירות:
קיר בלוק קיר בסון מחד בסון

תאריך	תיאור	מהדורה
22.09.2025	מכרז	1

אדריכלות
שם המסמך:
קבוצת רכישה נופיה
שם הפרויקט:
נופיה - מגרש 8
שם הגליון:
גליון מדרגות
מספר גליון:
A3-4-100
מחזור:
EDITION: קנה מידה: SCALE:
As indicated
סטוס:
למכרז
שורסס ע"י:
נבדק ע"י:
תאריך:
22.09.25

NeumanHaynerArchitects נירסן חיינר אדריכלים מודד תודיס 2, בית חירות 09-9546842 78	11112025 11:56:01 זכיות יימור / ע"פ הנחיות ע"ד
---	--

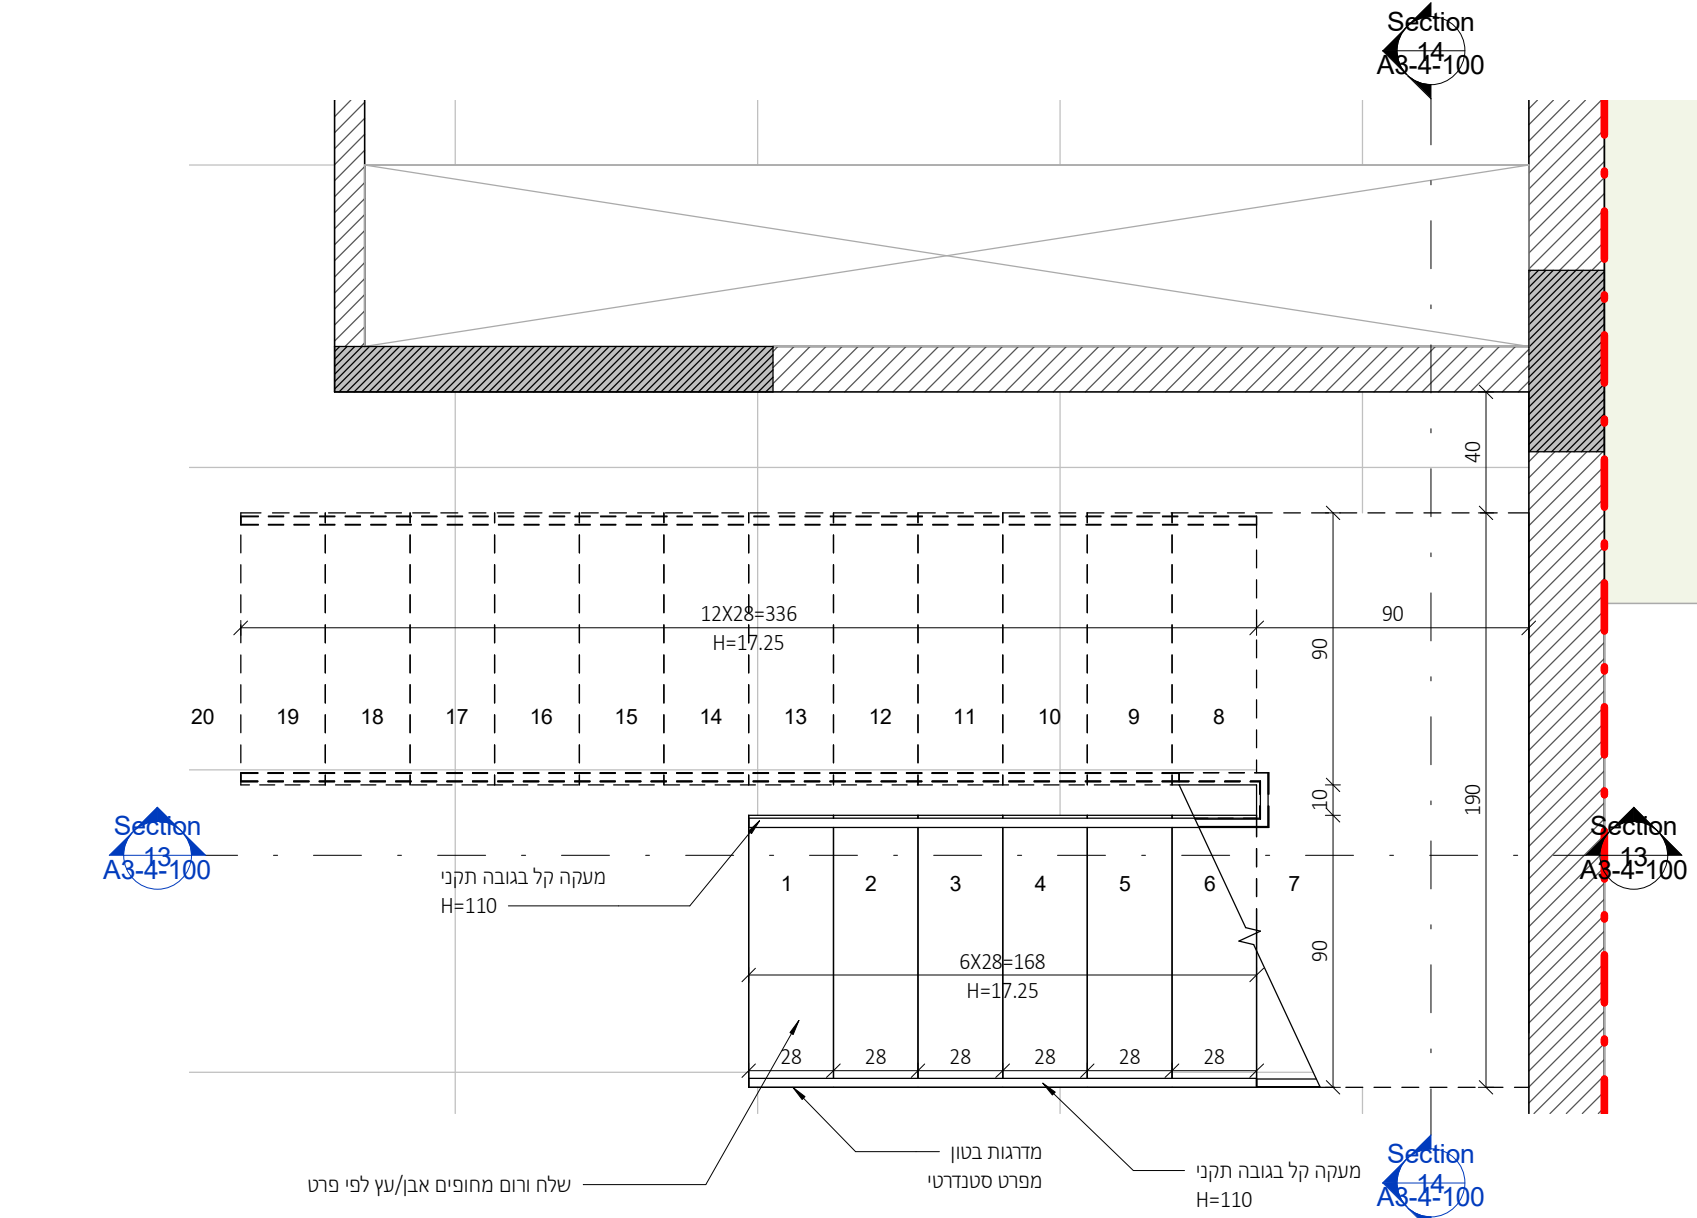


תכנית מדרגות קומת קרקע

1 : 25




תמונה להמחשה בלבד

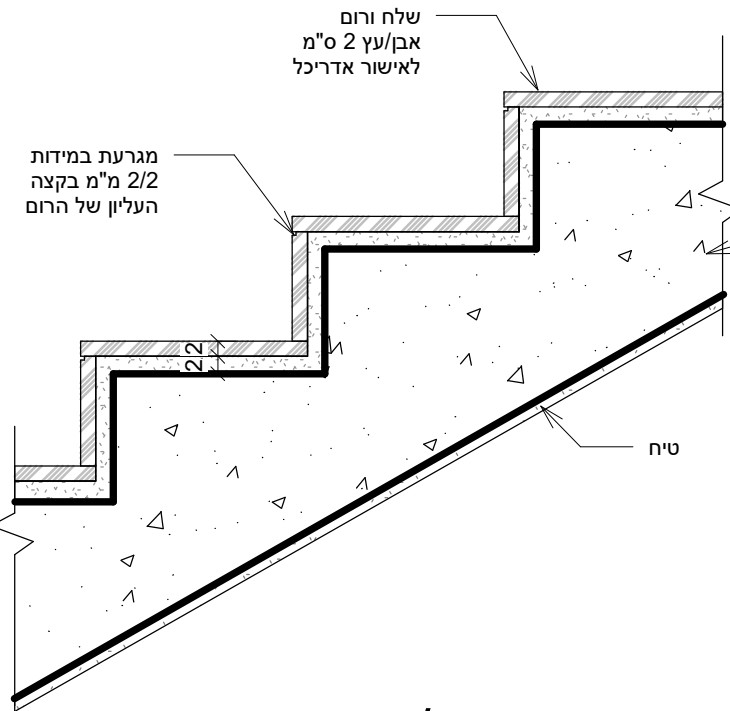

פרט מדרגות פנים - עץ/אבן


1 : 10

יש לתאם בין המסגר לבין האדריכלית לפי ביצוע המעקות ובואשור המזמן

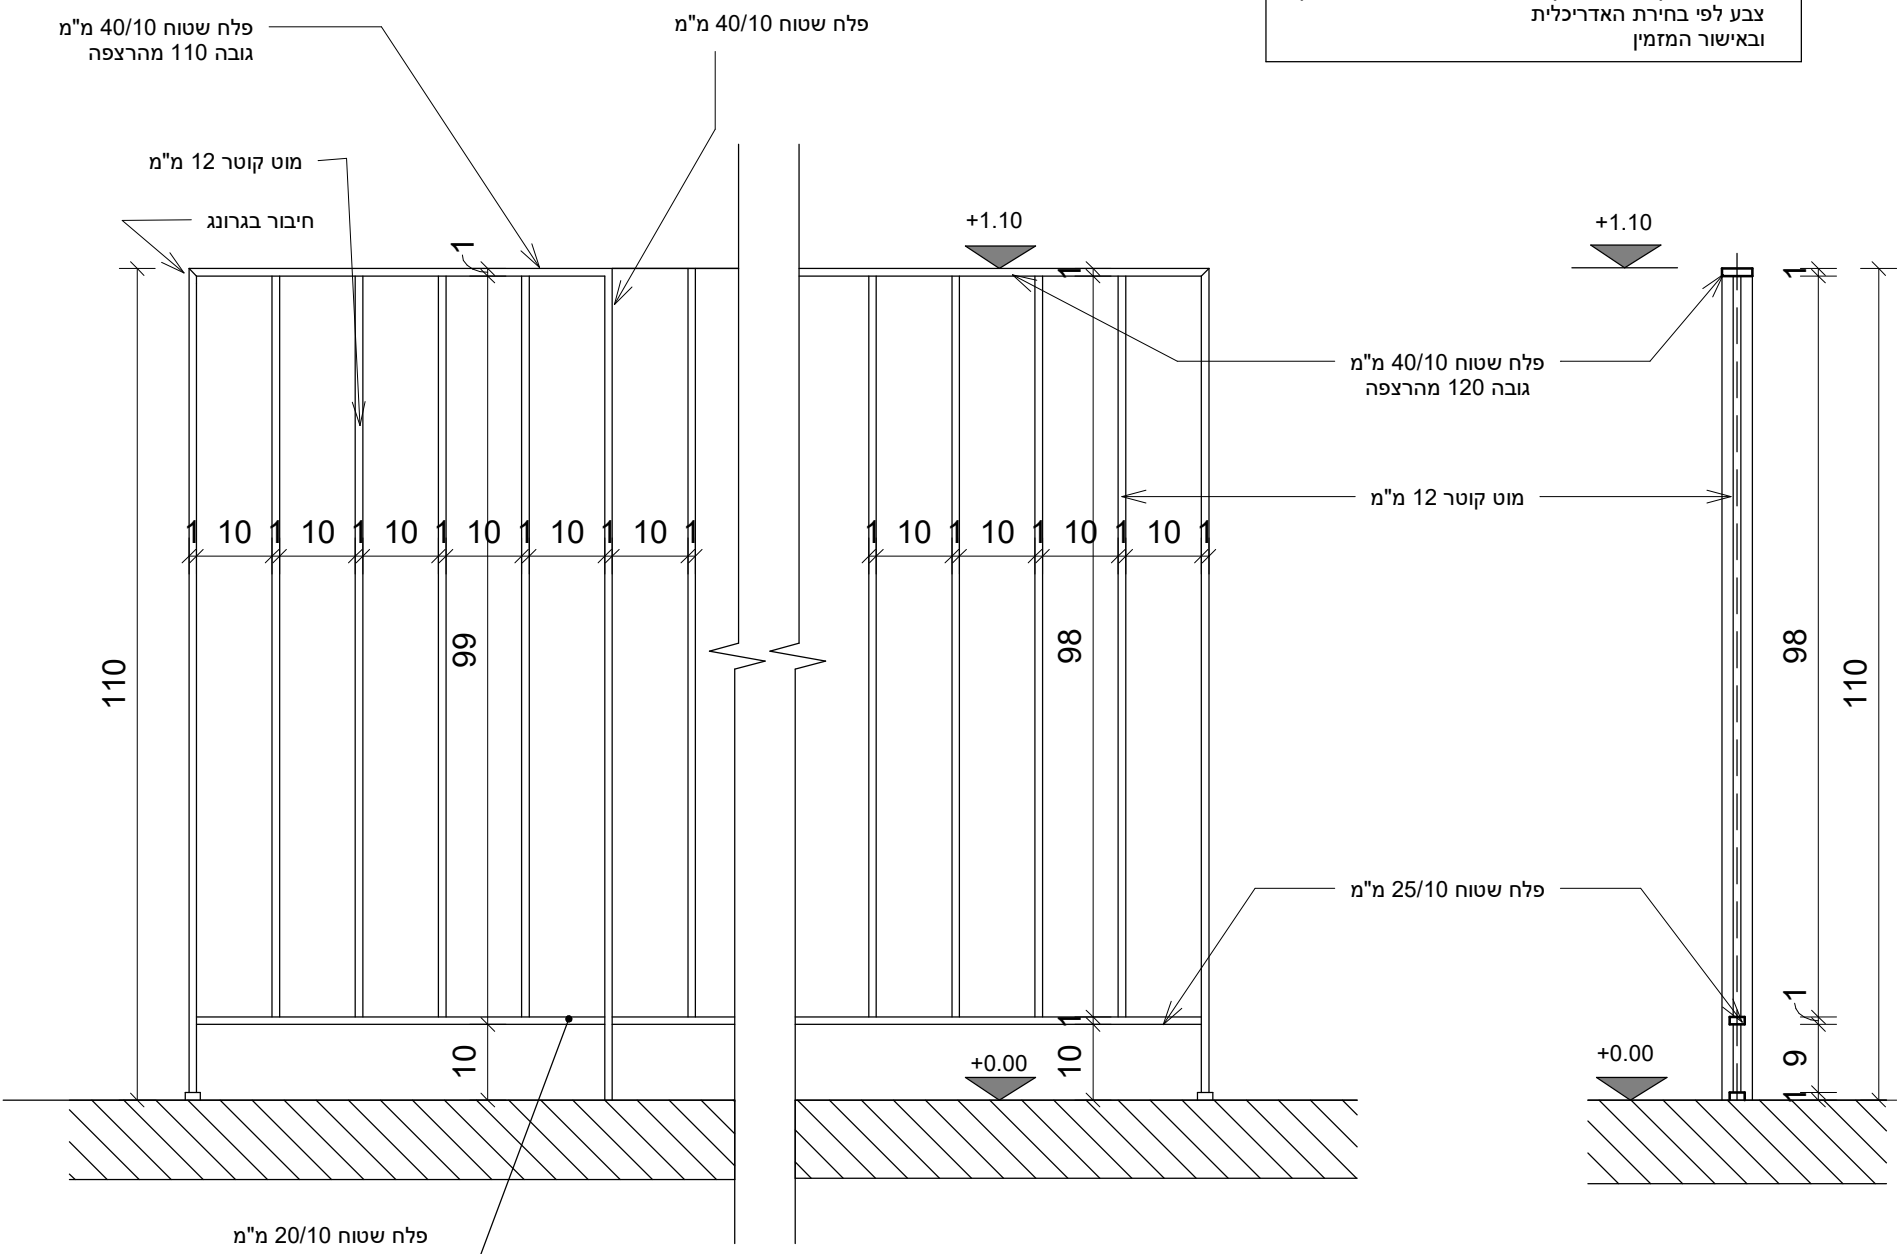


מעקה אנכי

1 : 10

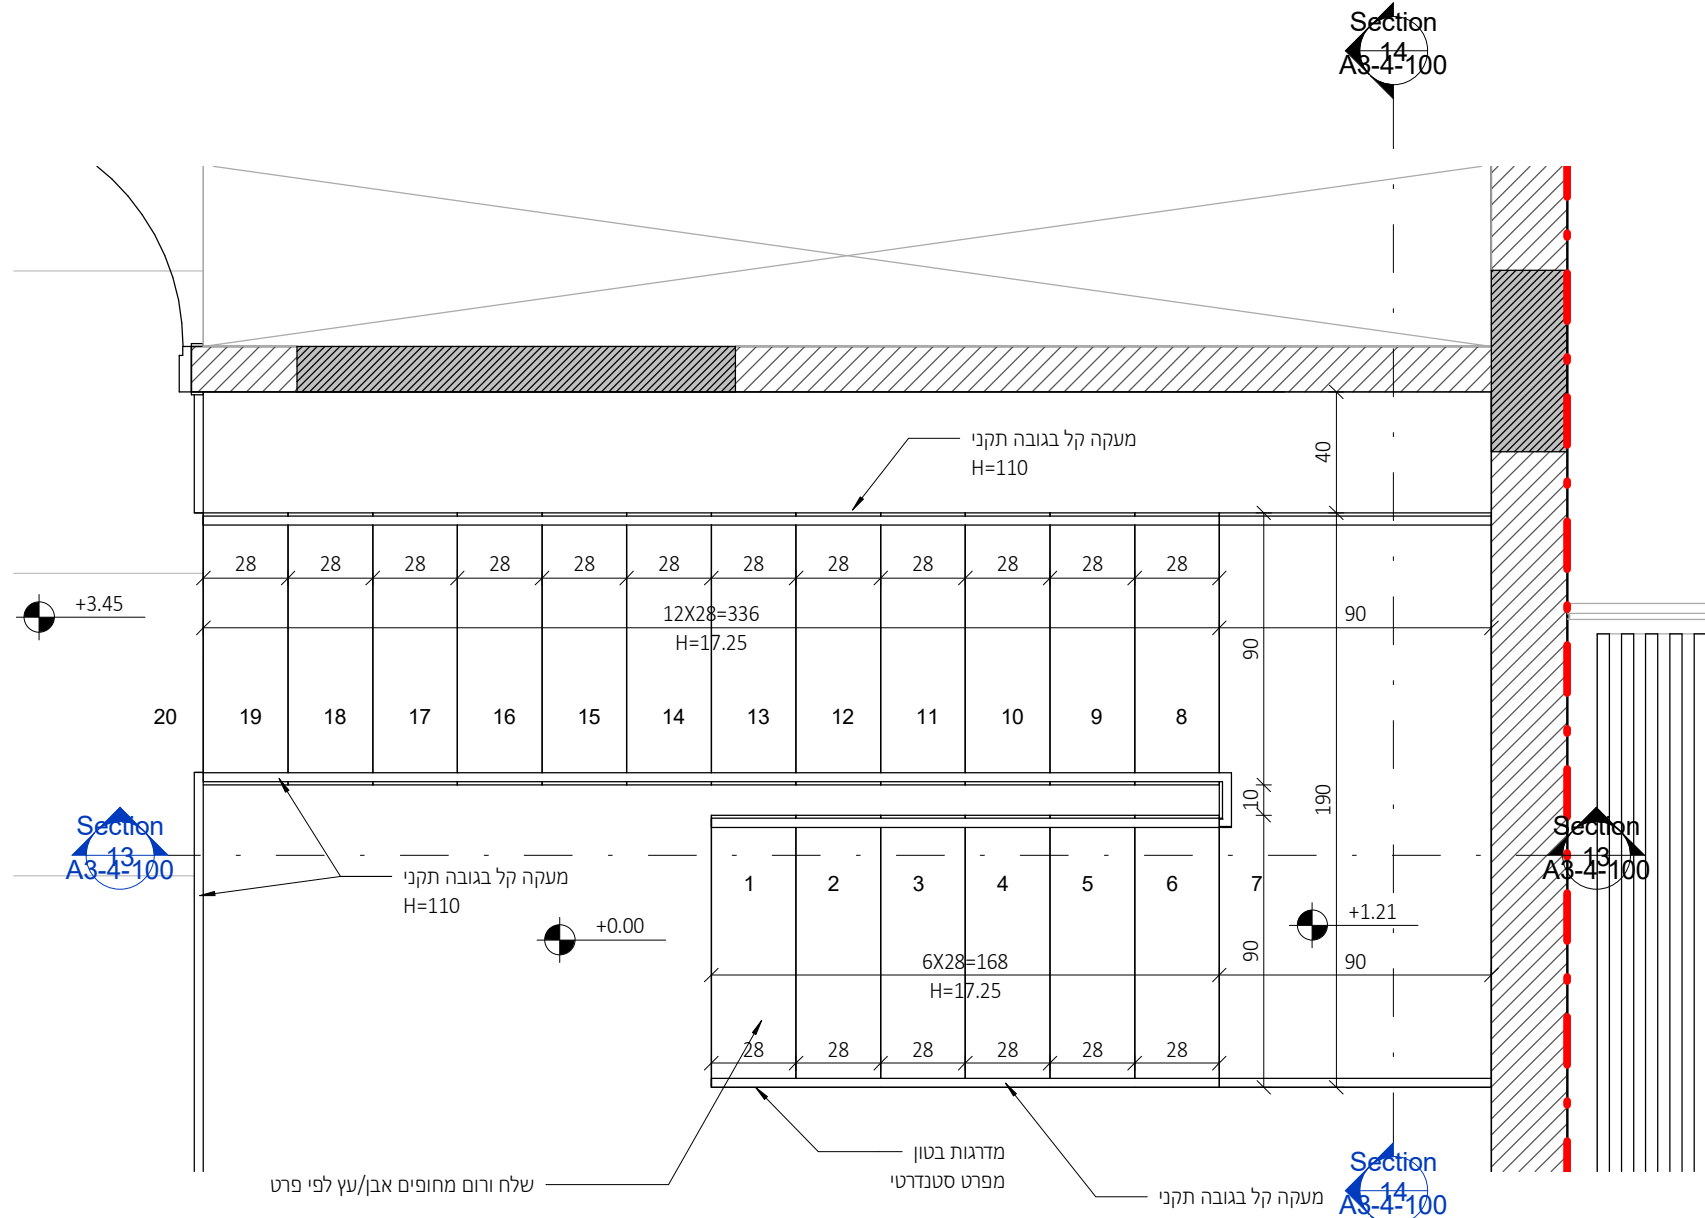


תכנית מדרגות קומה א

1 : 25

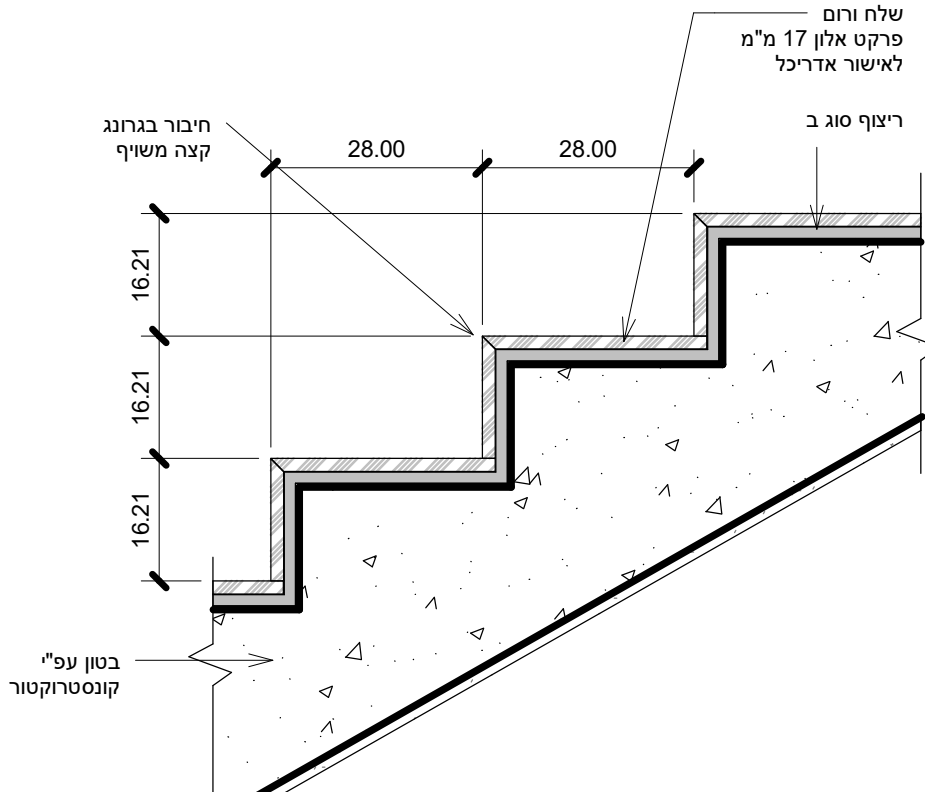


פרט מדרגות בטון בחיפוי פרקט

1 : 10

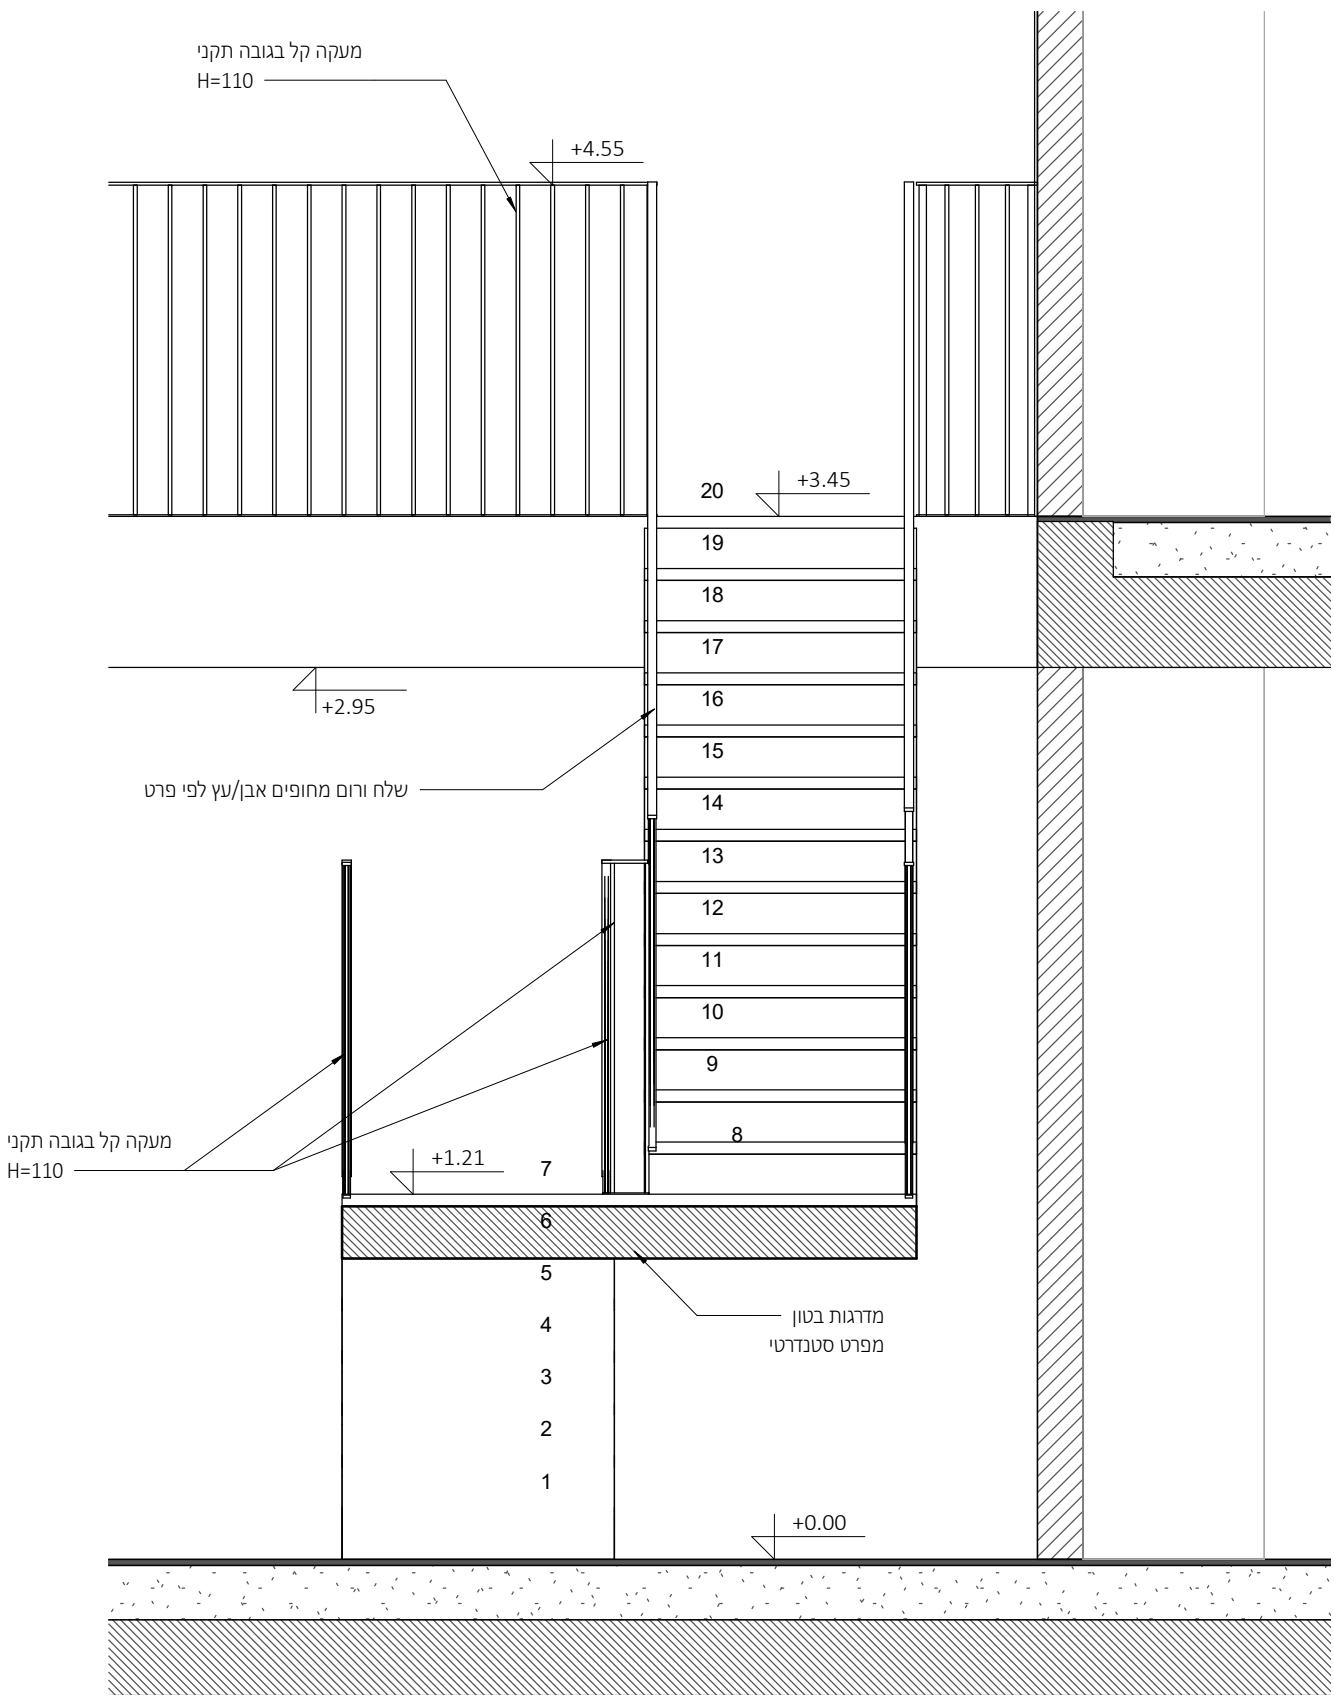

Section 14

1 : 25

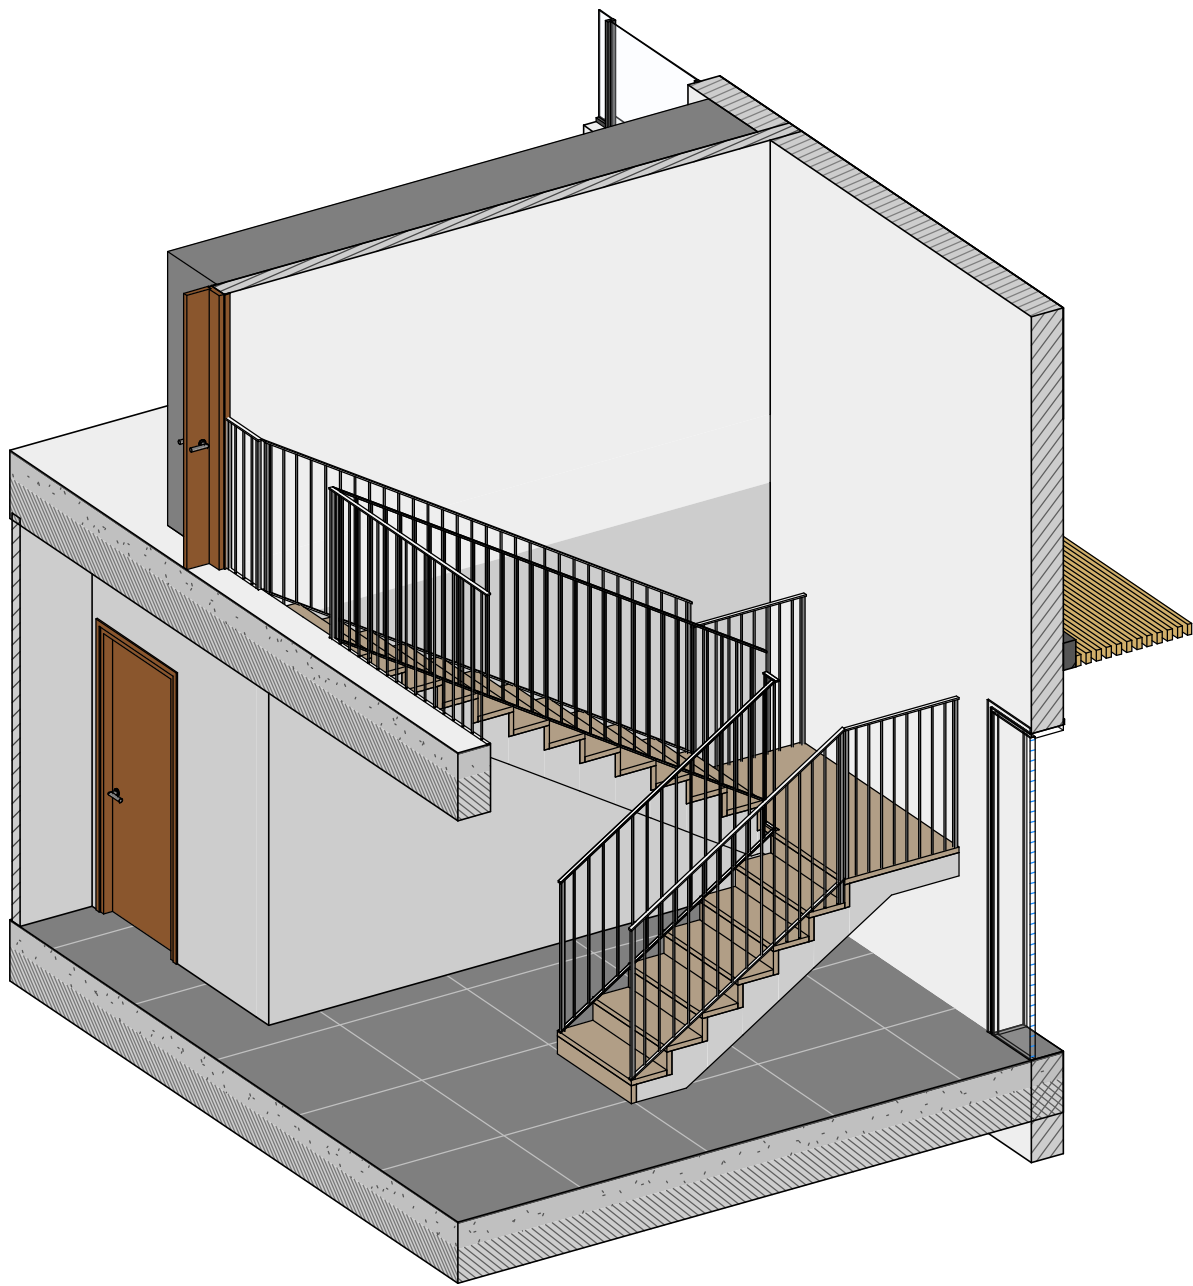


להמשך תיאום

דגם נבחר

מדרגות סטנדרטיות - מפרט סטנדרטי

על הקבלן לשלוח S.D לאישור אדריכל

יש לבצע התאמה לפרט לאחר בחירת חיפוי המדרגות*

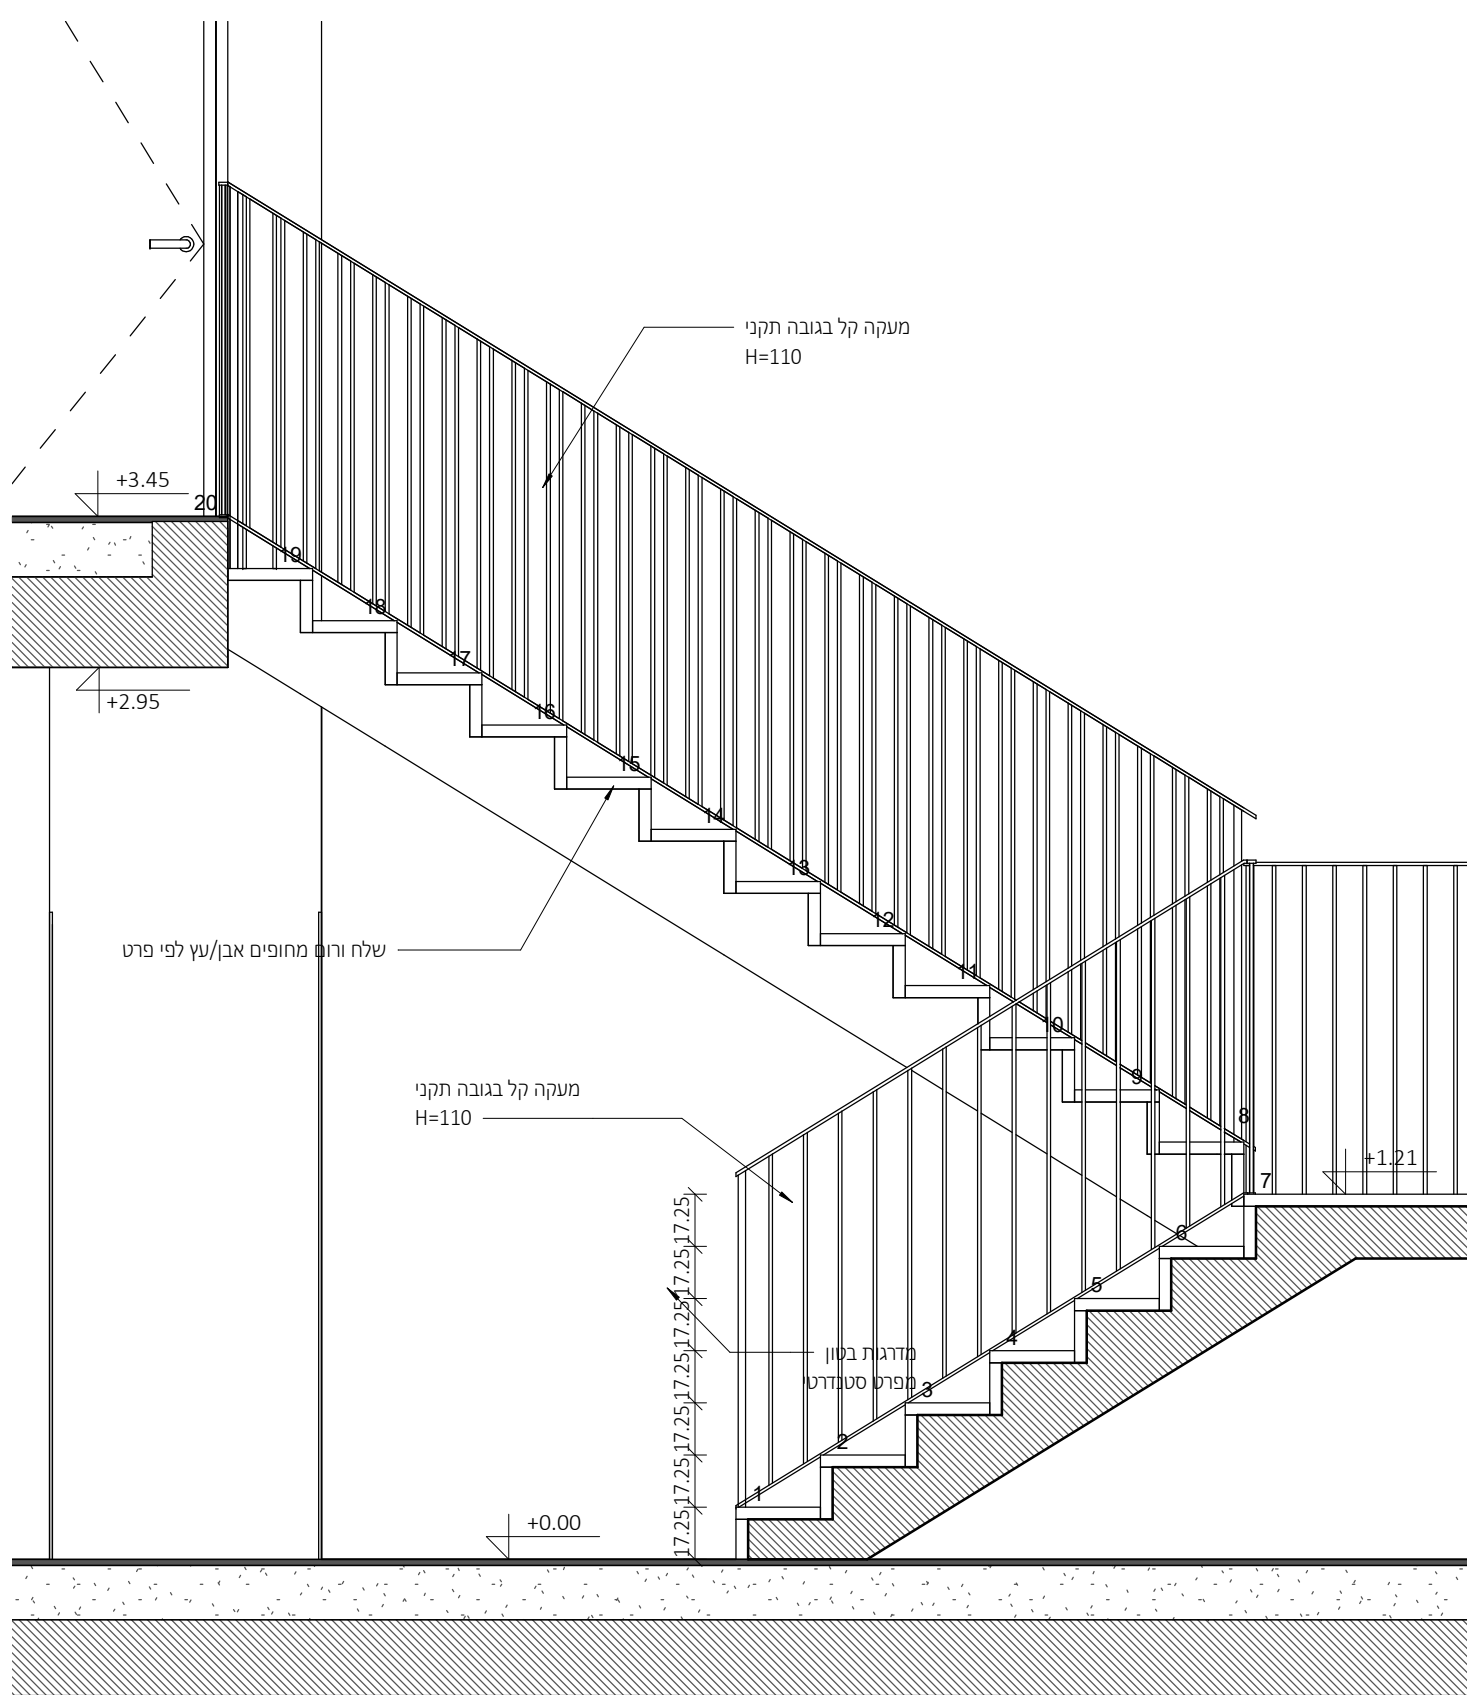

Section 13

1 : 25

ניהול פרויקט
מהיסוד - בן סלומון
פיקוח
מהיסוד - בן סלומון
קונסטרוקציה
ערן שילר
מיזוג אוויר
אייל ארז מהנדסים ויועצים בע"מ
אינסטלציה
איתן אלמסי
חשמל
איתן בסיס
אלומיניום
נוף
נתי בלוקא
חשמל חכם
חימום תת רצפתי
איטום
צבי טל
אקוסטיקה
מעליות
קרקע וביסוס
דיה הנדסת קרקע וביסוס
רישוי



פרטי האיטום באחריות יועץ האיטום
ראה חוברת פרטי איטום מצורפת

להמשך תיאום

[illegible]



אדריכלות			
CLIENT NAME:		שם הלקוח:	
קבוצת רכישה נופיה			
PROJECT NAME:		שם הפרויקט:	
נופיה - מגרש 8			
DRAWING NAME:		שם התכנית:	
פרטים			
SHEET NUMBER:		מספר העמוד:	
A3-4-103			
CALC:	עוד חזירה:	EDITION:	הדורה:
As indicated			
TATUS:	סטטוס		
למכור			
	(נבדק עדי)		רשום עדי:
DATE:	22.09.25		תאריך:

פרגולת אלומיניום




תמונה להמחשה בלבד

להמשך תיאום

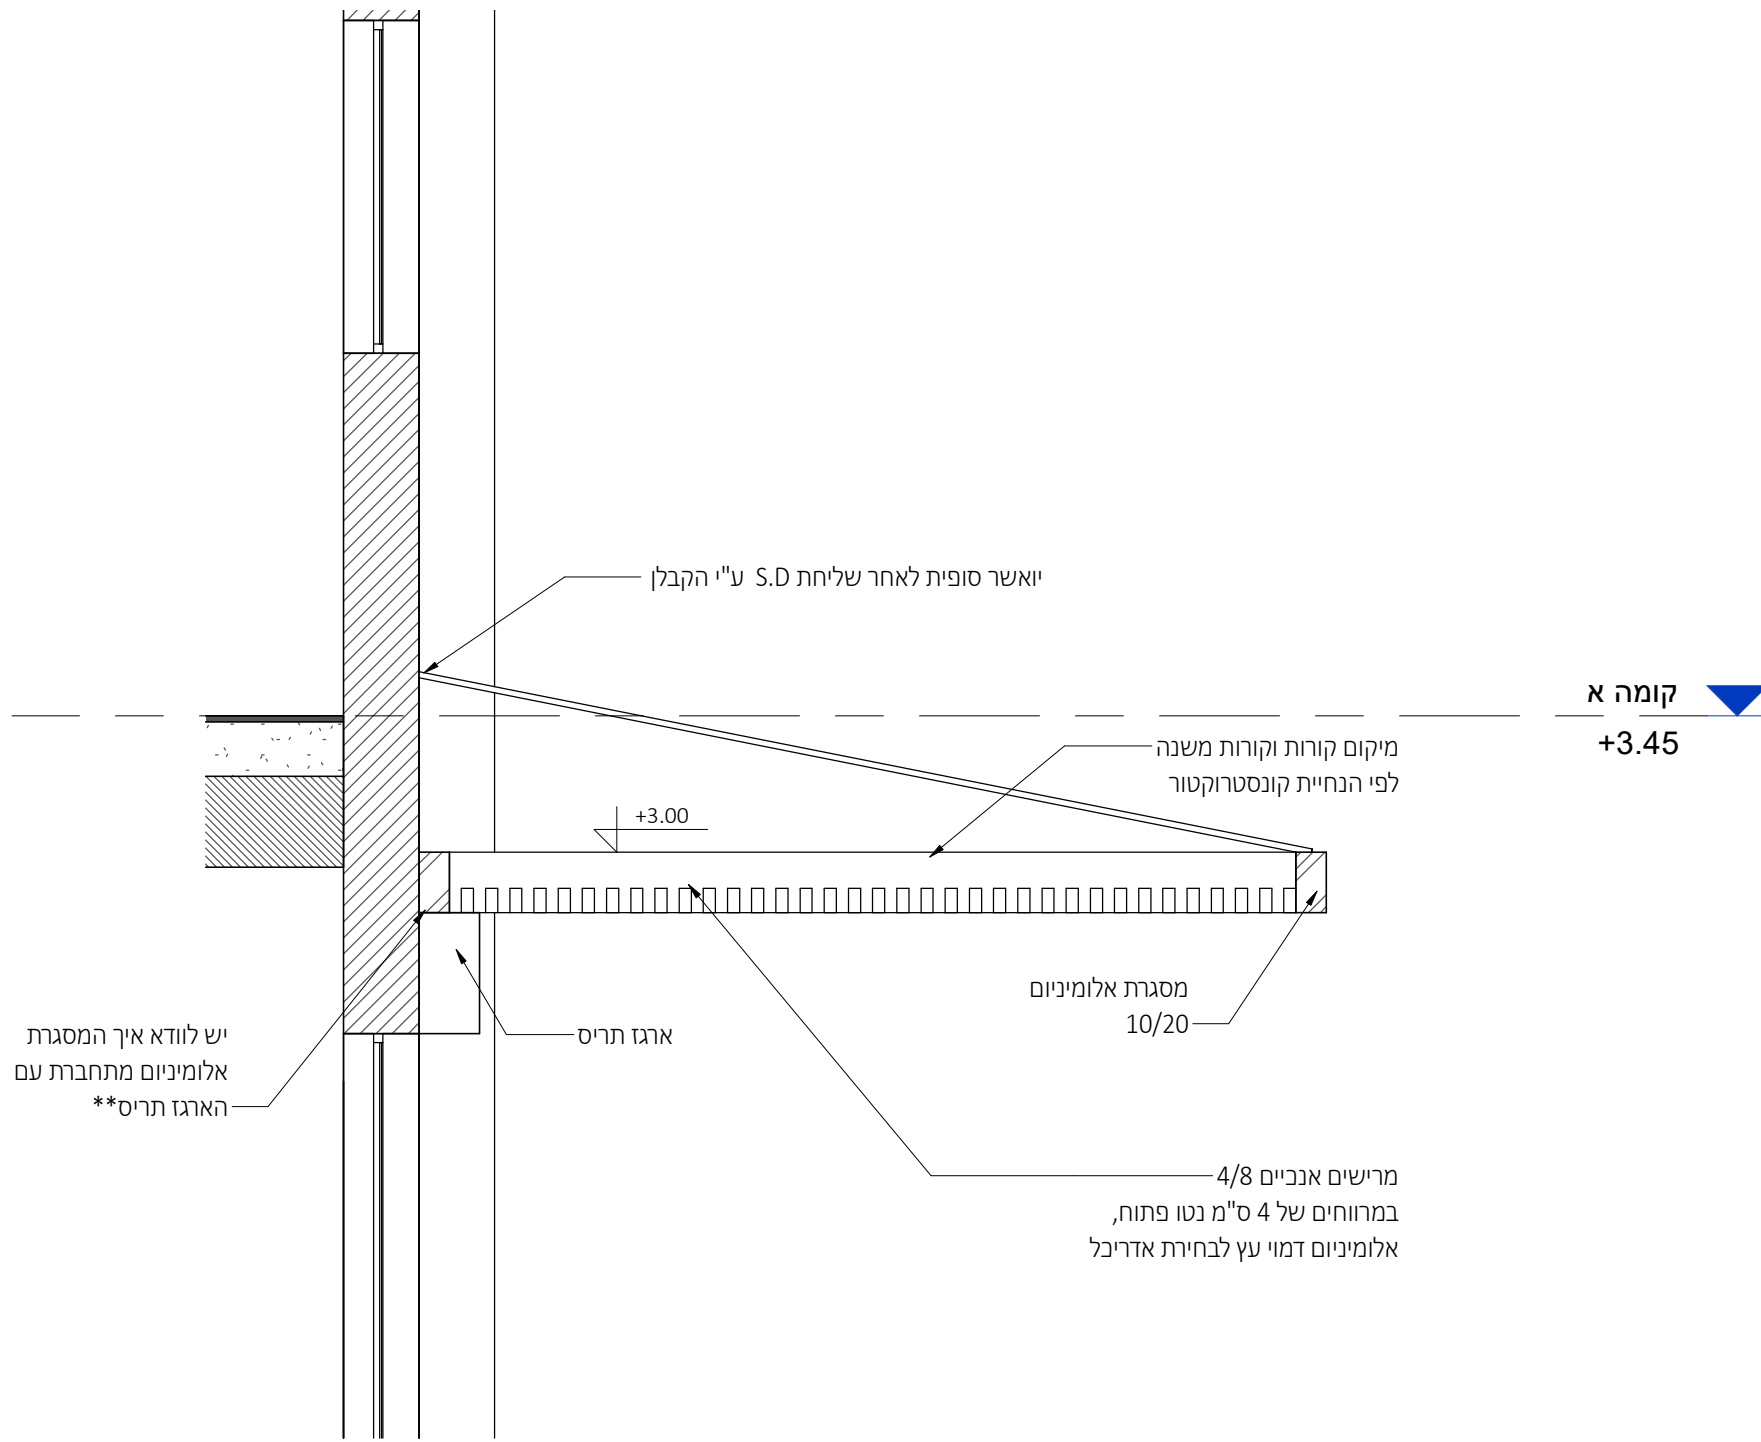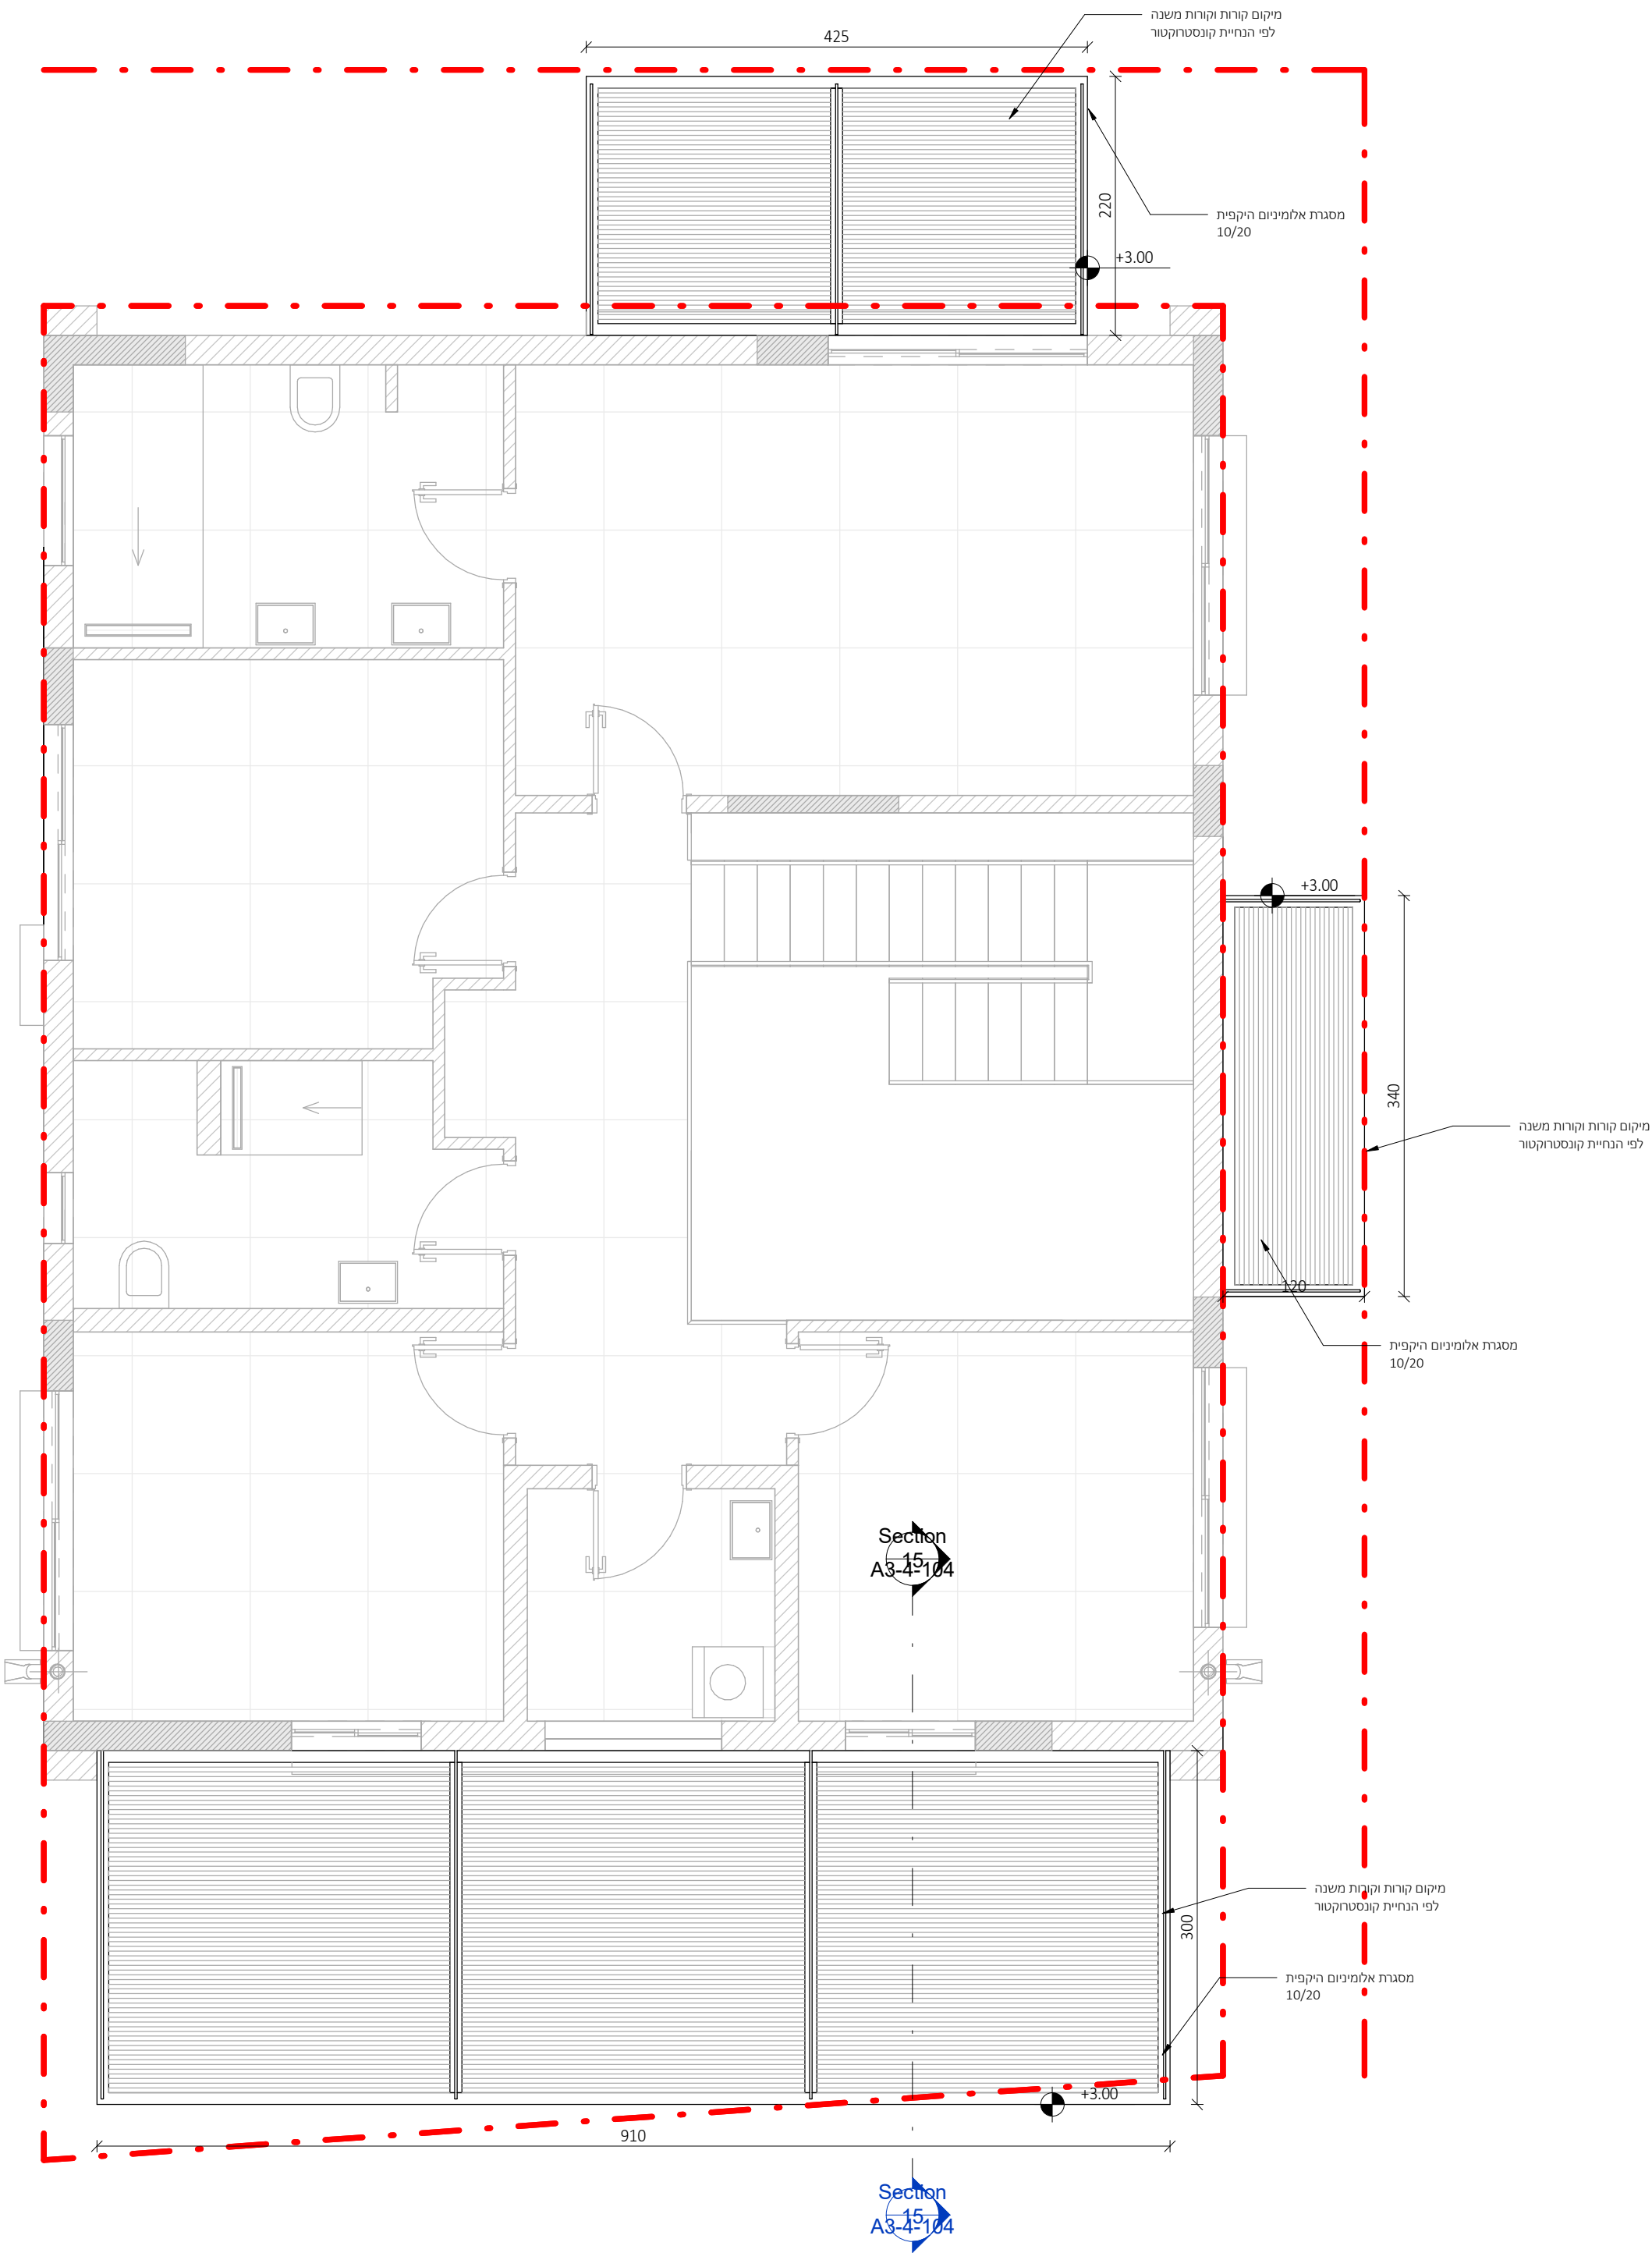


Section 15

1 : 25

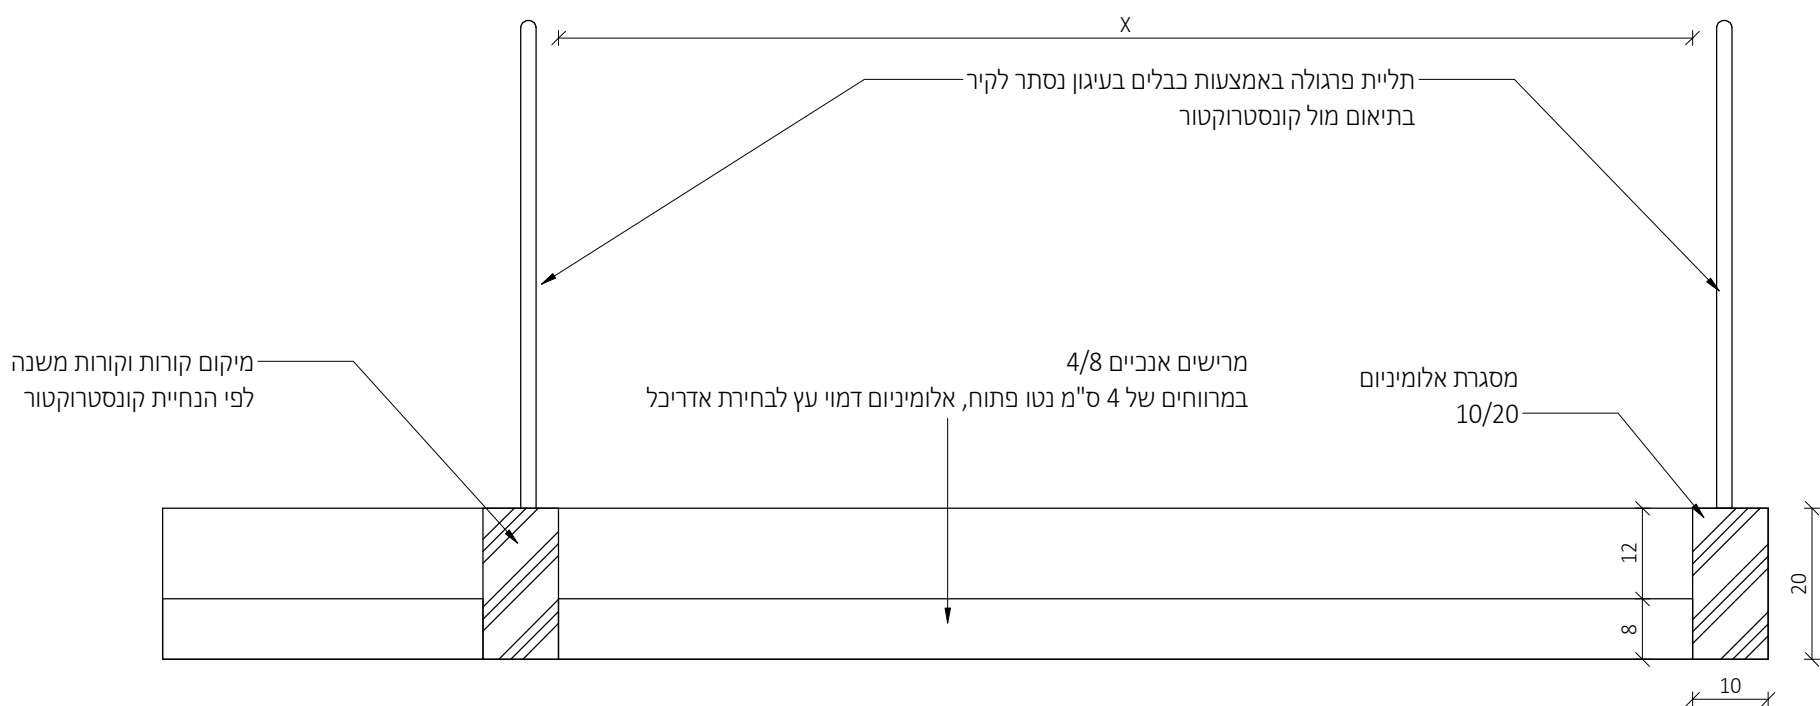

פרגולה - חתך אורך

1 : 10

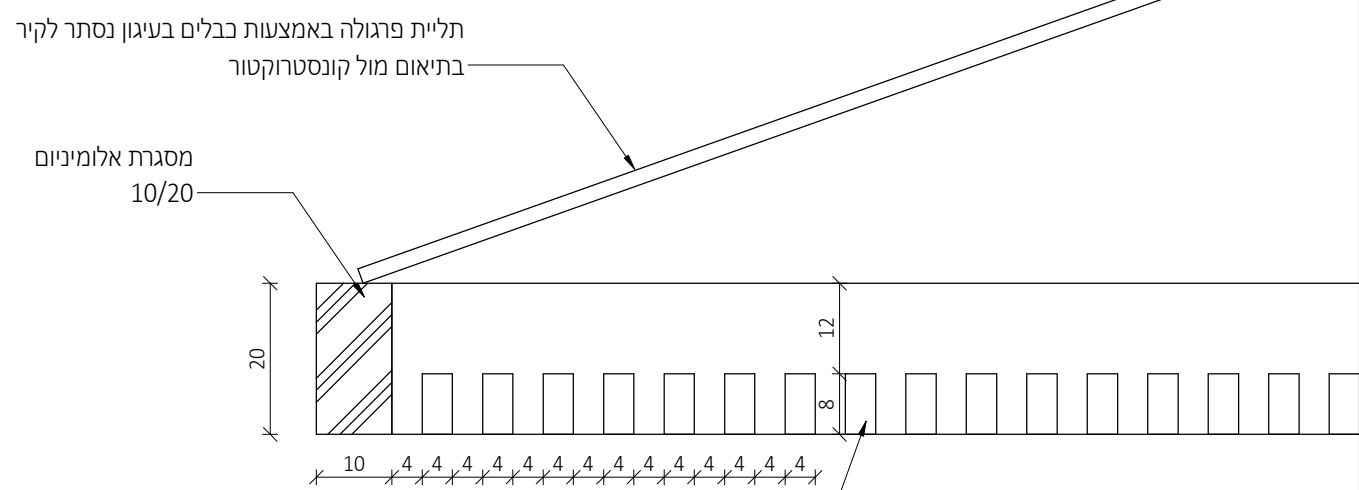

פרגולה - חתך רוחב

1 : 10


מתכננים:

ניהול פרויקט
מהיסוד - בן סלומון
פיקוח
מהיסוד - בן סולומון
קונסטרוקציה
ערן שילר
מיזוג אוויר
אייל ארז מהנדסים ויועצים בע"מ
אינסטלציה
איתן אלמסי
חשמל
איתן בסיס
אלומיניום
נוף
נתי בלוקא
חשמל חכם
חימום תת רצפתי
איטום
צבי טל
אקוסטיקה
מעליות
קרקע וביסוס
דיה הנדסת קרקע וביסוס
רישוי

± 0.00 = +252.80

- הערות:
1. תכנית זו יש לקרוא יחד עם תכנית הרישום.
 2. גובה אבסולוטי - ראו תכנית פיתוח.
 3. הפירות הן בין קירות הבניה ולא כולל פיתוח.
 4. פיתוח השטח סביב הבניה, כולל, מדרגות, גדרות, שבילים, ריצופים, שפופים, גדרים, חניה וכו' ראו תכנית פיתוח.
 5. איסוס קירות הרצפה הבונה כמתע עם הקרקע ובידוד תרמי לאורך העמודים והקורות וכל החתכים. כלירות או עם סימני (גובה) - ראו תכנית קונסטרוקציה.
 6. אף מים יבוצעו בכל מישור אופקי הכולל חתכו.
 7. סוף תרמי במסל"ד - ע"פ מפרט חומרים, מאושר ע"י פיקוח העיר.
- המבצע אחראי לסידור: עליו לבקר ולבדוק את כל המידות בתכנית ובמקום הבנייה.
- במסגרת של מידות או אי התאמה בתכנית /או בבנוי, עליו להודיע על כך מיד לאדריכל בסופו המשיך בעבודתו.
- המבצע ישתמש או ויק בתכנית שאושרו לכניסה.
- המבצע יחזיק באחריות, לכל מה, של משרדו של תכנית.
- אין לקבוע מידות על ידי חזירה בשו"מ.
- התכנית הינה רכוש האדריכל ואין לעשות כל שימוש בה או ברעיונות הגלומים בה, אלא באישור בכתב מהאדריכל.
- מחנדים /או ידוע אשר שמו רשום בתכנית זו, נושא לכד באחריות המקצועית והחוקית לתכנית.
- על המפקח והשקלן לזרז את האמת התכנית האדריכלית "לכניסה" לתכנית ויתר, המכר והתכנית האושרות ע"י כל גורמים הרשמיים.
- התכנית כוללת את כל האחריות והידוע על ליום תחלפת.

משרד קירות:

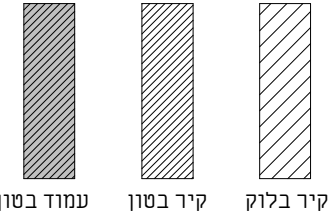

תאריך	תיאור	מהדורה
22.09.2025	מכרז	1

אדריכלות

שם המשיין:	CLIENT NAME:
קבוצת רכישה נופיה	
שם הפרויקט:	PROJECT NAME:
נופיה - מגרש 8	
שם הגיליון:	DRAWING NAME:
פרטי פרגולה	
מספר גיליון:	SHEET NUMBER:
A3-4-104	
תאריך:	EDITION:
22.09.25	קנה מידה:
	SCALE:
	STATUS:
למכרז	As indicated
שורשם ע"י:	נבדק ע"י:
תאריך:	DATE:
22.09.25	

רשימת חלונות					
סוג	תיאור	כמות	גובה	רוחב	מס פריט

ק.קרקע

1	580	240	1	צלון רפפה חיצוני חשמלי + ארגז חיצוני	ויטרינה פרופיל 7500 קליל
2	220	240	3	צלון רפפה חיצוני חשמלי + ארגז חיצוני	ויטרינה פרופיל 7500 קליל
3	85	240	1	צלון רפפה חיצוני חשמלי + ארגז חיצוני	דלת כנף פרופיל 4350 קליל
4	110	110	1	צלון רפפה חיצוני חשמלי + ארגז חיצוני	חלון קיפ פרופיל 4500 קליל
5	220	110	1	צלון רפפה חיצוני חשמלי + ארגז חיצוני	חלון הזזה פרופיל 7000 קליל

קומה א

6	60	110	1	תריס גלילה חשמלי	חלון קיפ פרופיל 4500 קליל
7	200	110	1	תריס גלילה חשמלי	חלון הזזה פרופיל 7000 קליל
8	110	110	1	תריס גלילה חשמלי	חלון קיפ פרופיל 4500 קליל
9	220	110	4	תריס גלילה חשמלי	חלון הזזה פרופיל 7000 קליל
10	110	110	2	תריס גלילה חשמלי	חלון הזזה פרופיל 7000 קליל

סוג זכוכית – בהתאם למפורט בדו"ח התרמי (תנאי המינימום בעמוד 9 מתוך המפרט התרמי). כמו כן, הזכוכית תקבע בתיאום עם הקבלן לאחר אישור יועץ התרמי וחברת הניהול

כל פריט יחולק למינימום הכנפיים האפשרי (לתיאום מול ספק האלומיניום ובמסגרת שרטוטי הshop drawing)

רשימת דלתות					
סוג	הערות	כמות	גובה	רוחב	מספר פריט

0	120	240	1	דלת כניסה	דלת חוץ דגם גארדה
1	70	210	1	דלת פנים	דלת פנים "אקוודור" תוצרת חמדיה
2	90	210	1	דלת פנים	דלת פנים "אקוודור" תוצרת חמדיה
3	80	210	8	דלת פנים	דלת פנים "אקוודור" תוצרת חמדיה
4	80	200	1	דלת נגרות ממ"ד	דלת פנים "אקוודור" תוצרת חמדיה

נוימן חיינר אדריכלים בע"מ

כל הזכויות שמורות
נ.ל.ח.

NeumanHaynerArchitects



רשימת פתחים			שם התכנית:
גליון מספר:	A3-6-1000	מהדורה:	01
שם הפרויקט:	נופיה - מגרש 8	תאריך:	22.09.2025
שם המממן:	קבוצת רכישה נופיה	סטטוס:	למכרז
		קנה מידה:	
11/11/2025 11:55:05			