


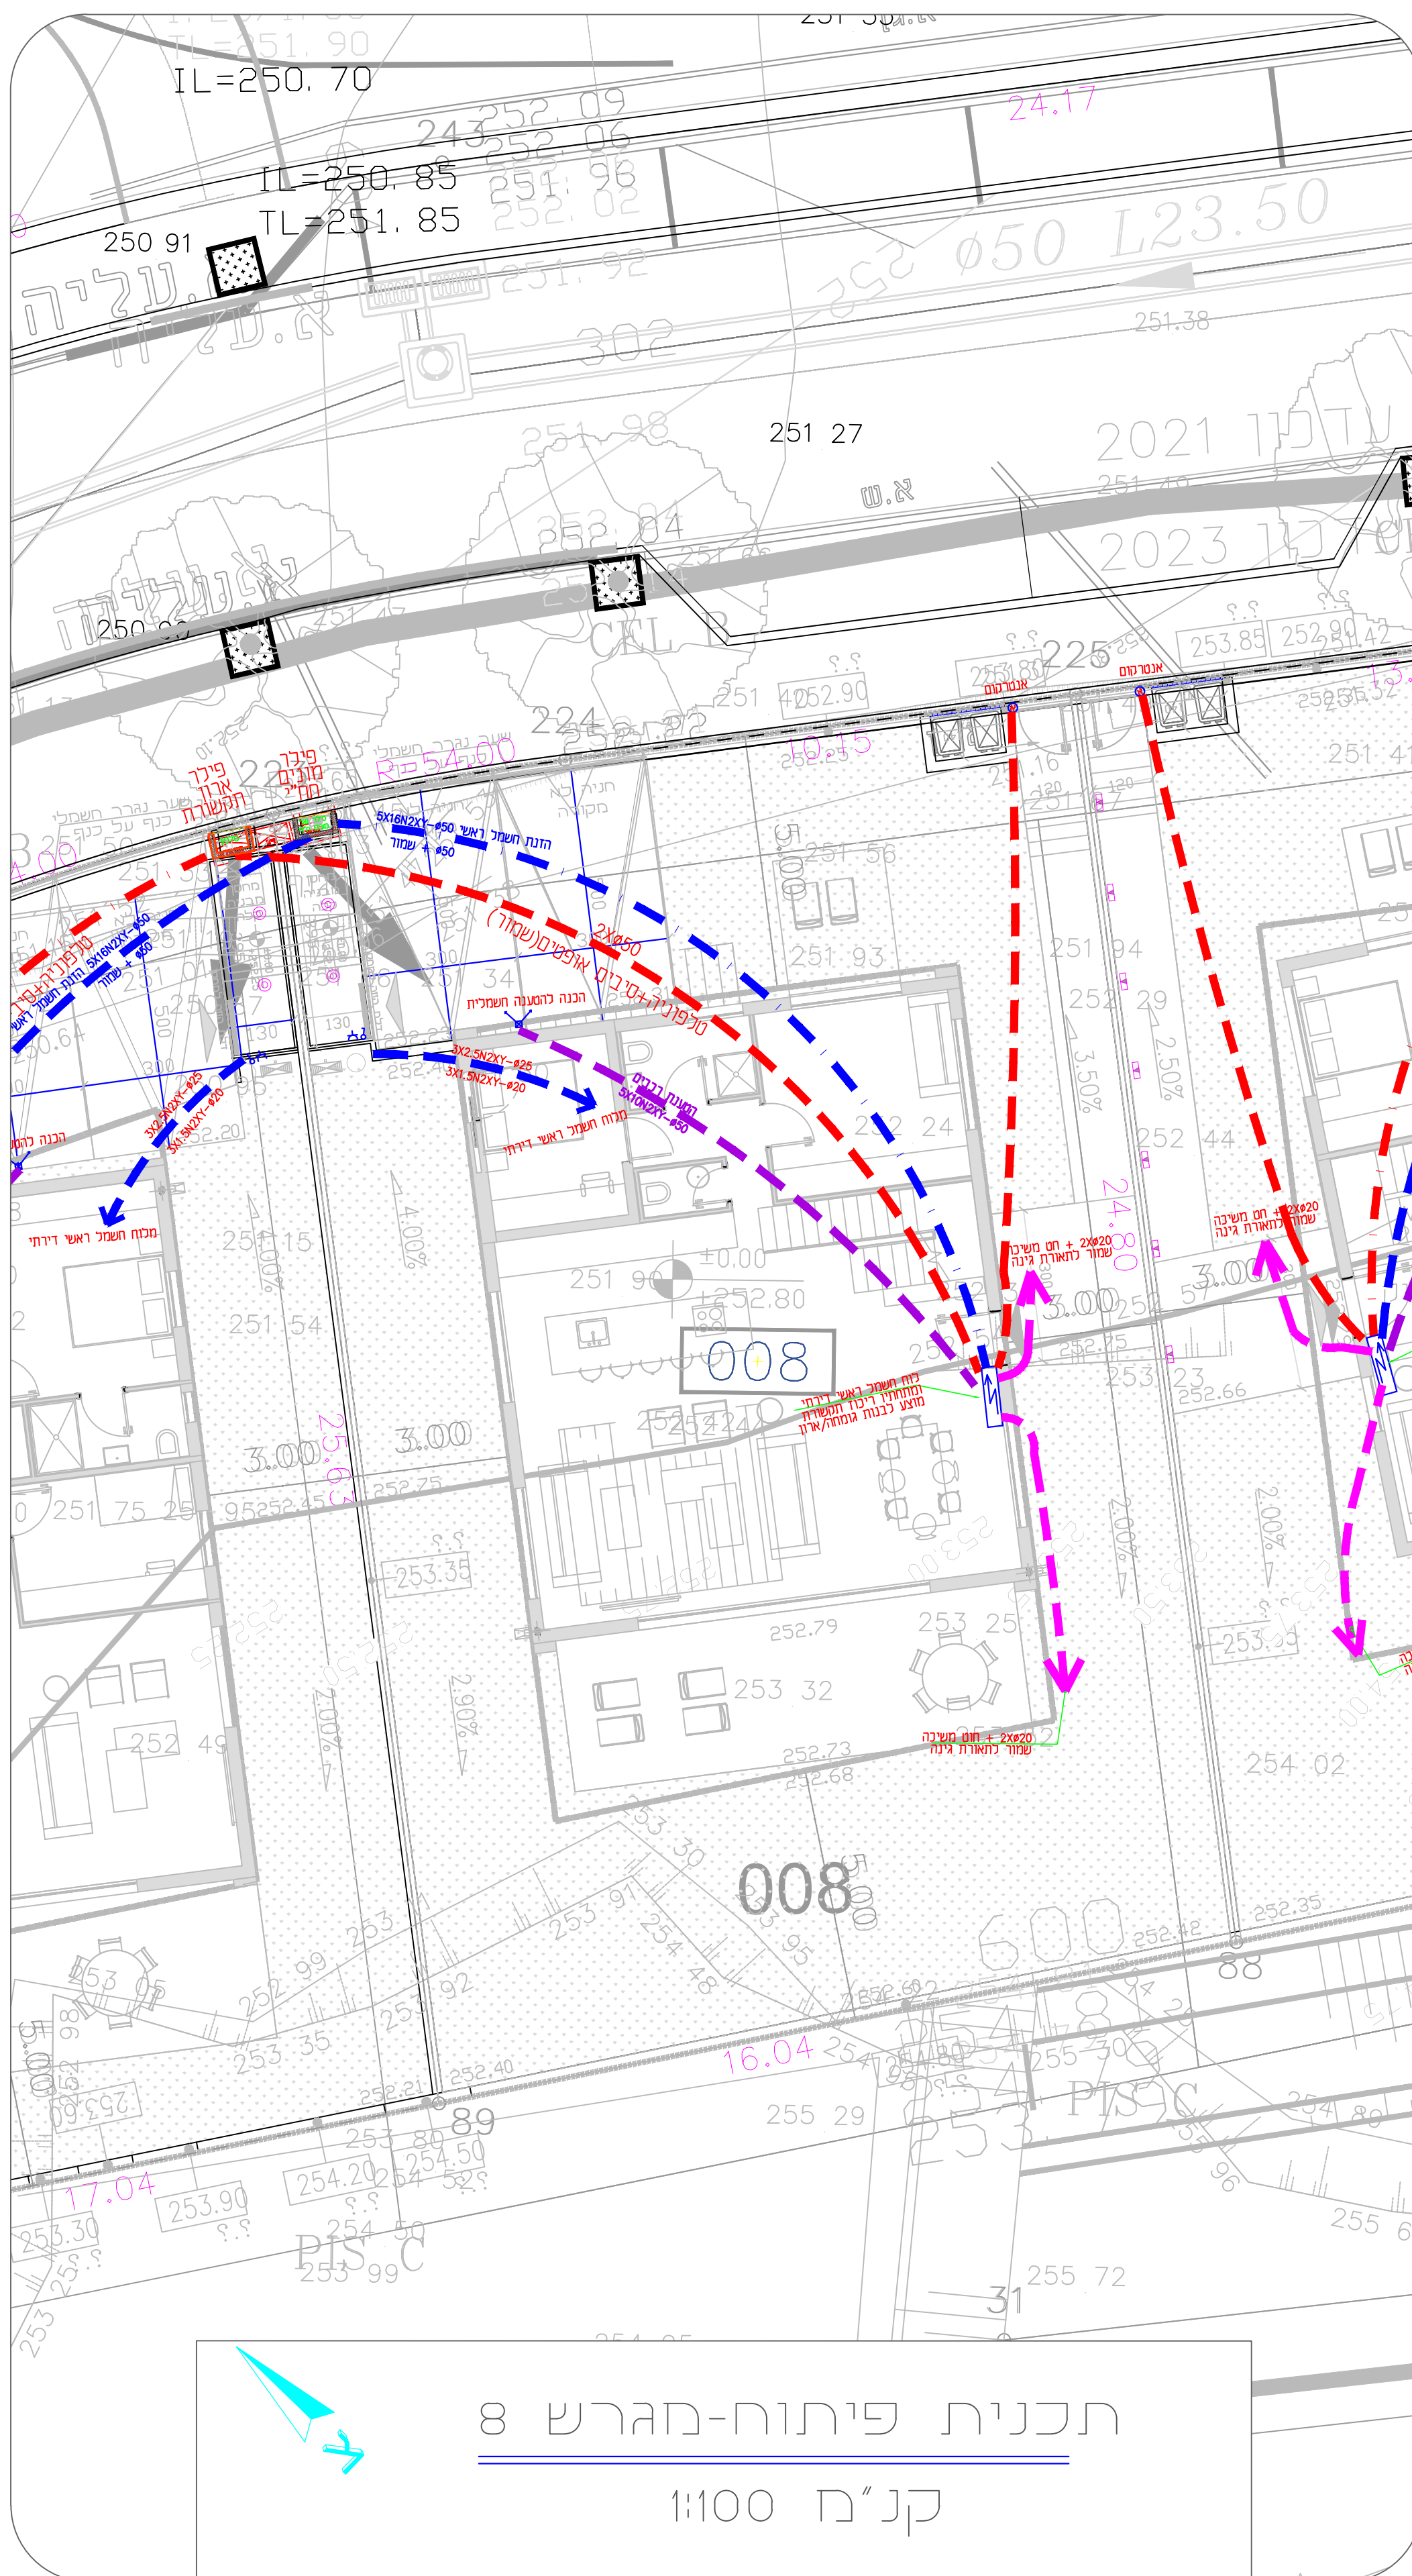

תפוצה		תאריך	
מנהל הפרויקט			
אדריכל			
מחשבי יום			
חשבת			
מבקר			
בטיחות			
אקוסטיקה			
אנוסטלציה			
אדריכל נוף			
מטבחים			
חברת חשמל			
חברת בזק			

[illegible]

עודכן ע"י: _____ רחל

הנדסת חשמל בע"מ
משרד: יד הרוצים 16, ירושלים 93420
טל: 074-7021015 נייד: 050-6550484
פקס: 077-5131015 ר"ת: 077-5131015
office@ebasis.co.il

שם הפרויקט: נופיה-אלפי מנשה

שם הגיליון: תוכנית פיתוח מגרש 8

○ ● ○ ○ לביצוע למכרז לאישור לעיון		קנה מידה: 1:100	
File: מס' קובץ: 675P.dwg		Date: תאריך: 17.06.2024	
אישר: איתן		שרטט: אילה	
מס' הפרויקט: 675		מס' הגליון: P8	
		מס' עדכון: 0	

