


פתיחי גישה אופן ארט בתיאום סופי מול אדריכל
כלל יחידות המיזוג אשר נמצאות בתוך נגרות יש לתאם סופית מול אדריכל ונגרות

Court 2
1st Floor


Option No.2
inverter duct unit in living
room and wall mounted in
rooms

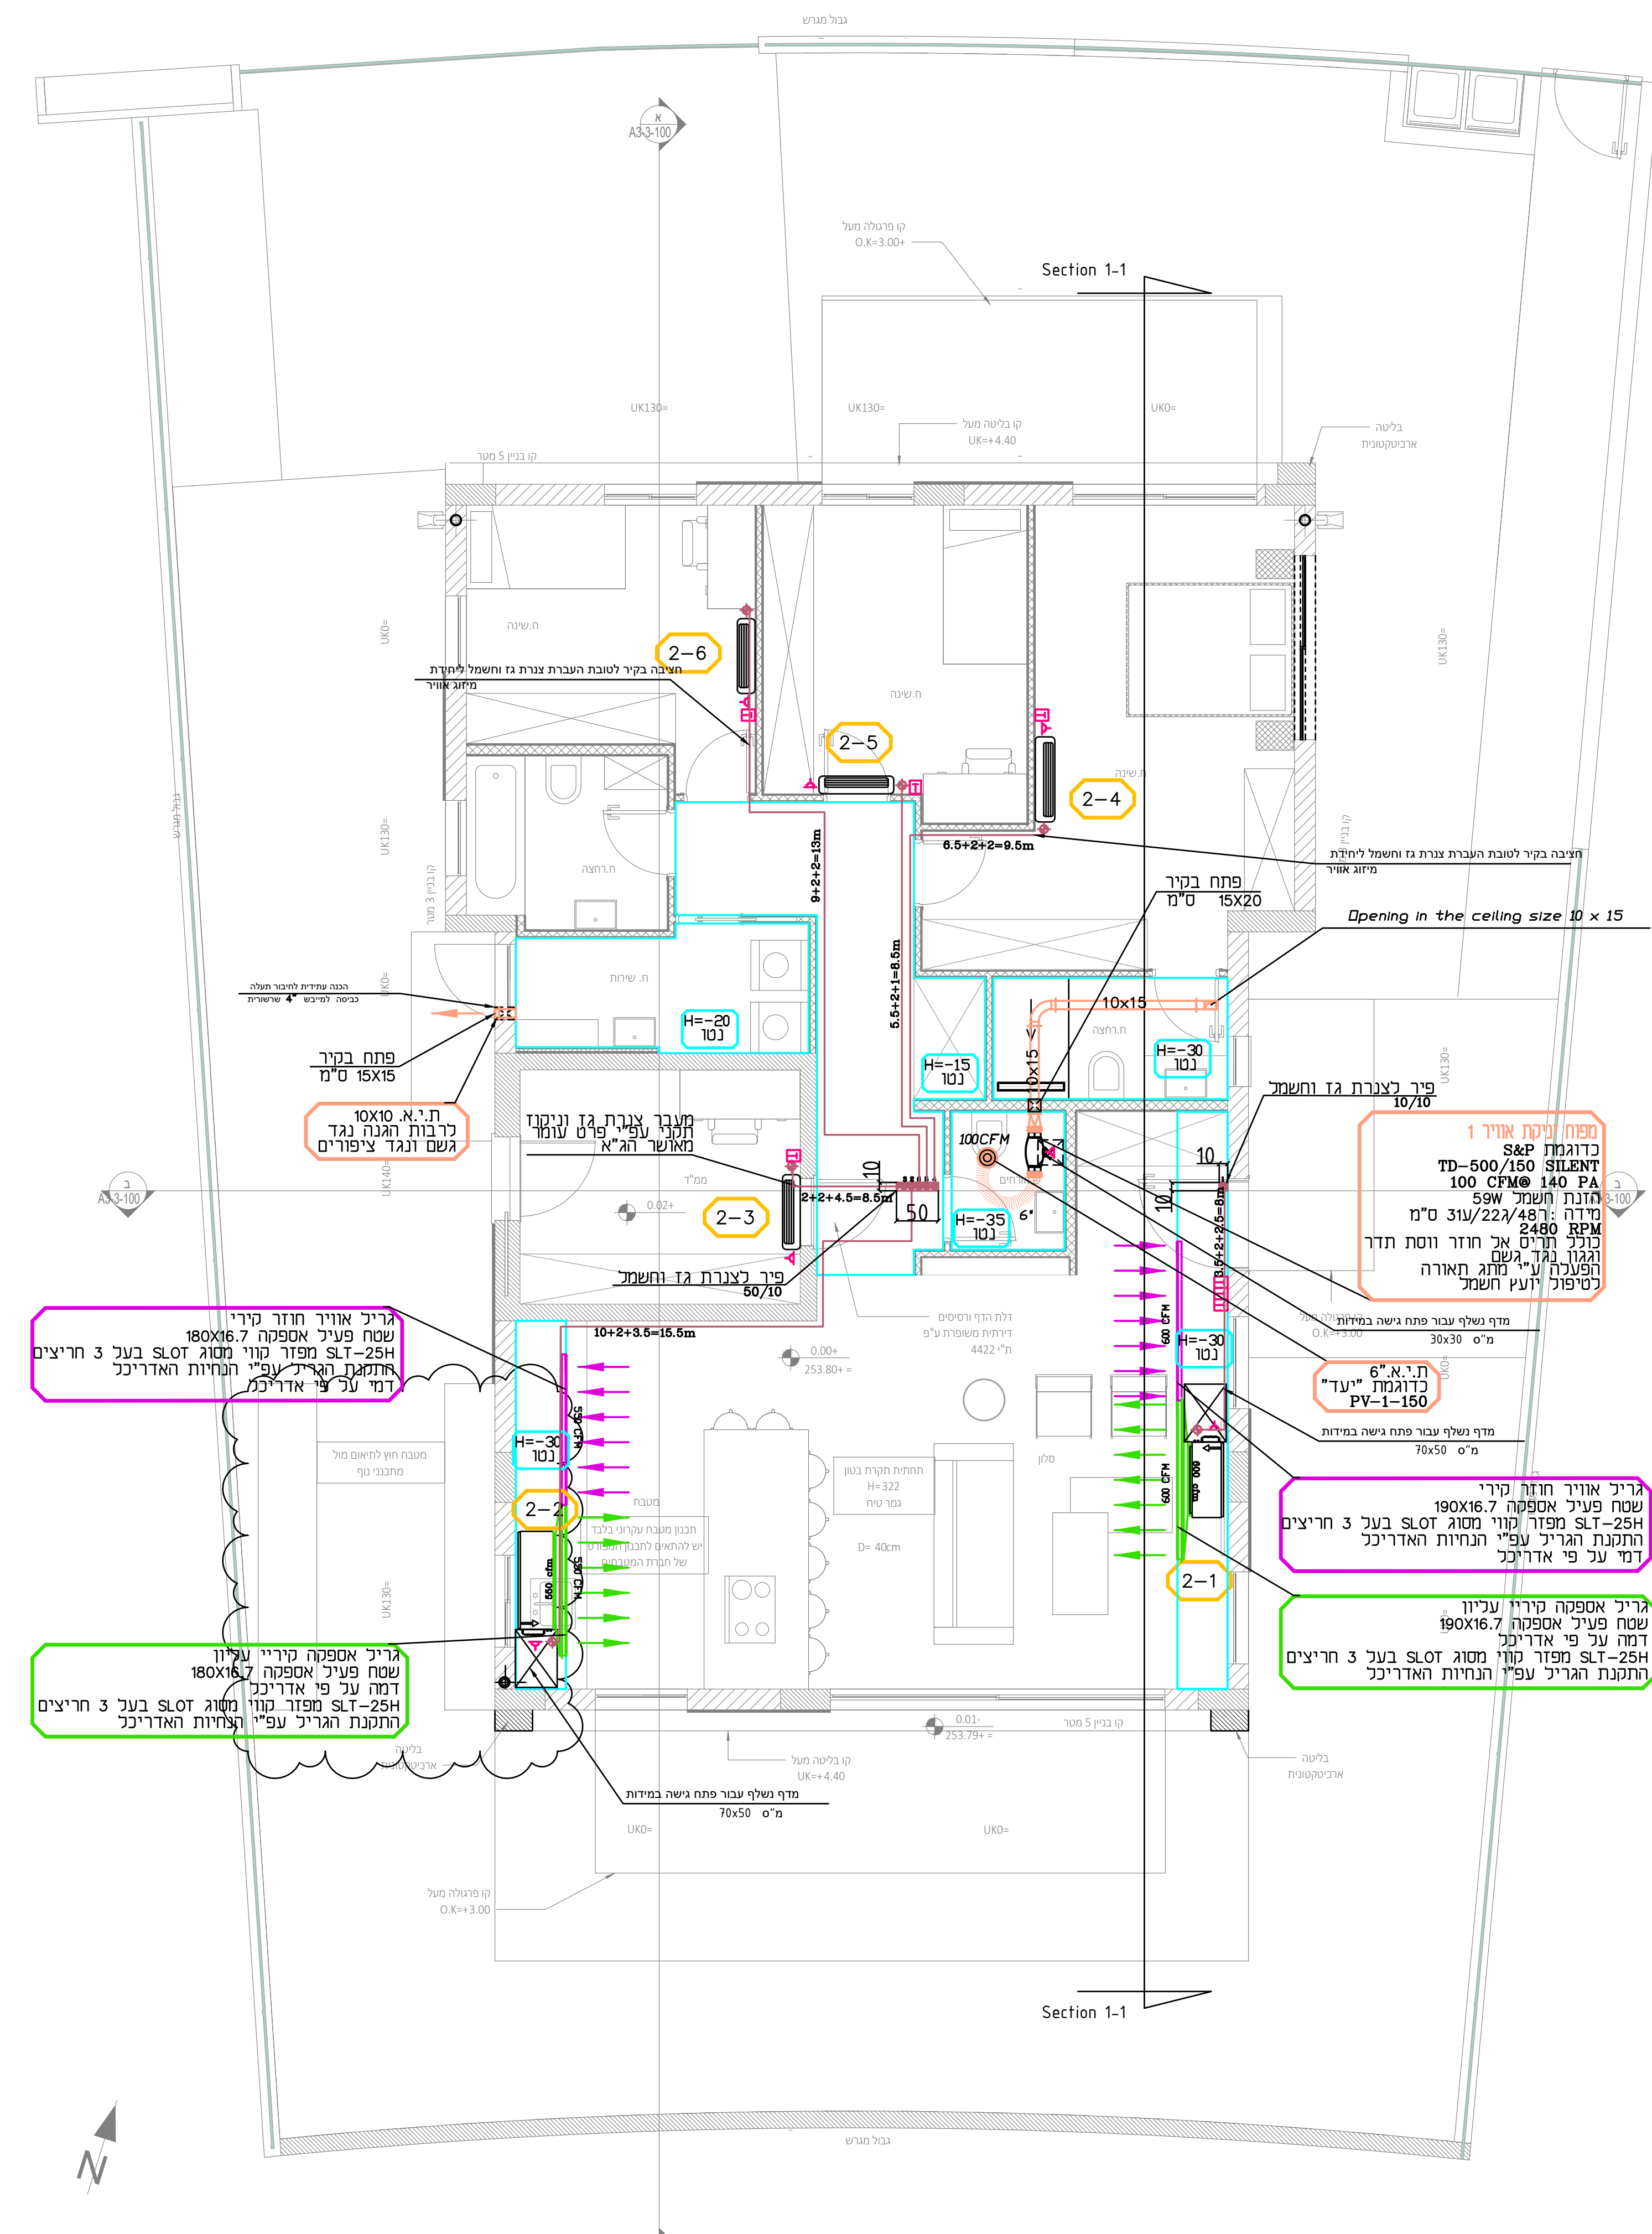

פיתוח נוף עפ"
יועץ נוף ראה פ

Court 2
Roof

Option No2
inverter duct unit in living
room and wall mounted in
rooms

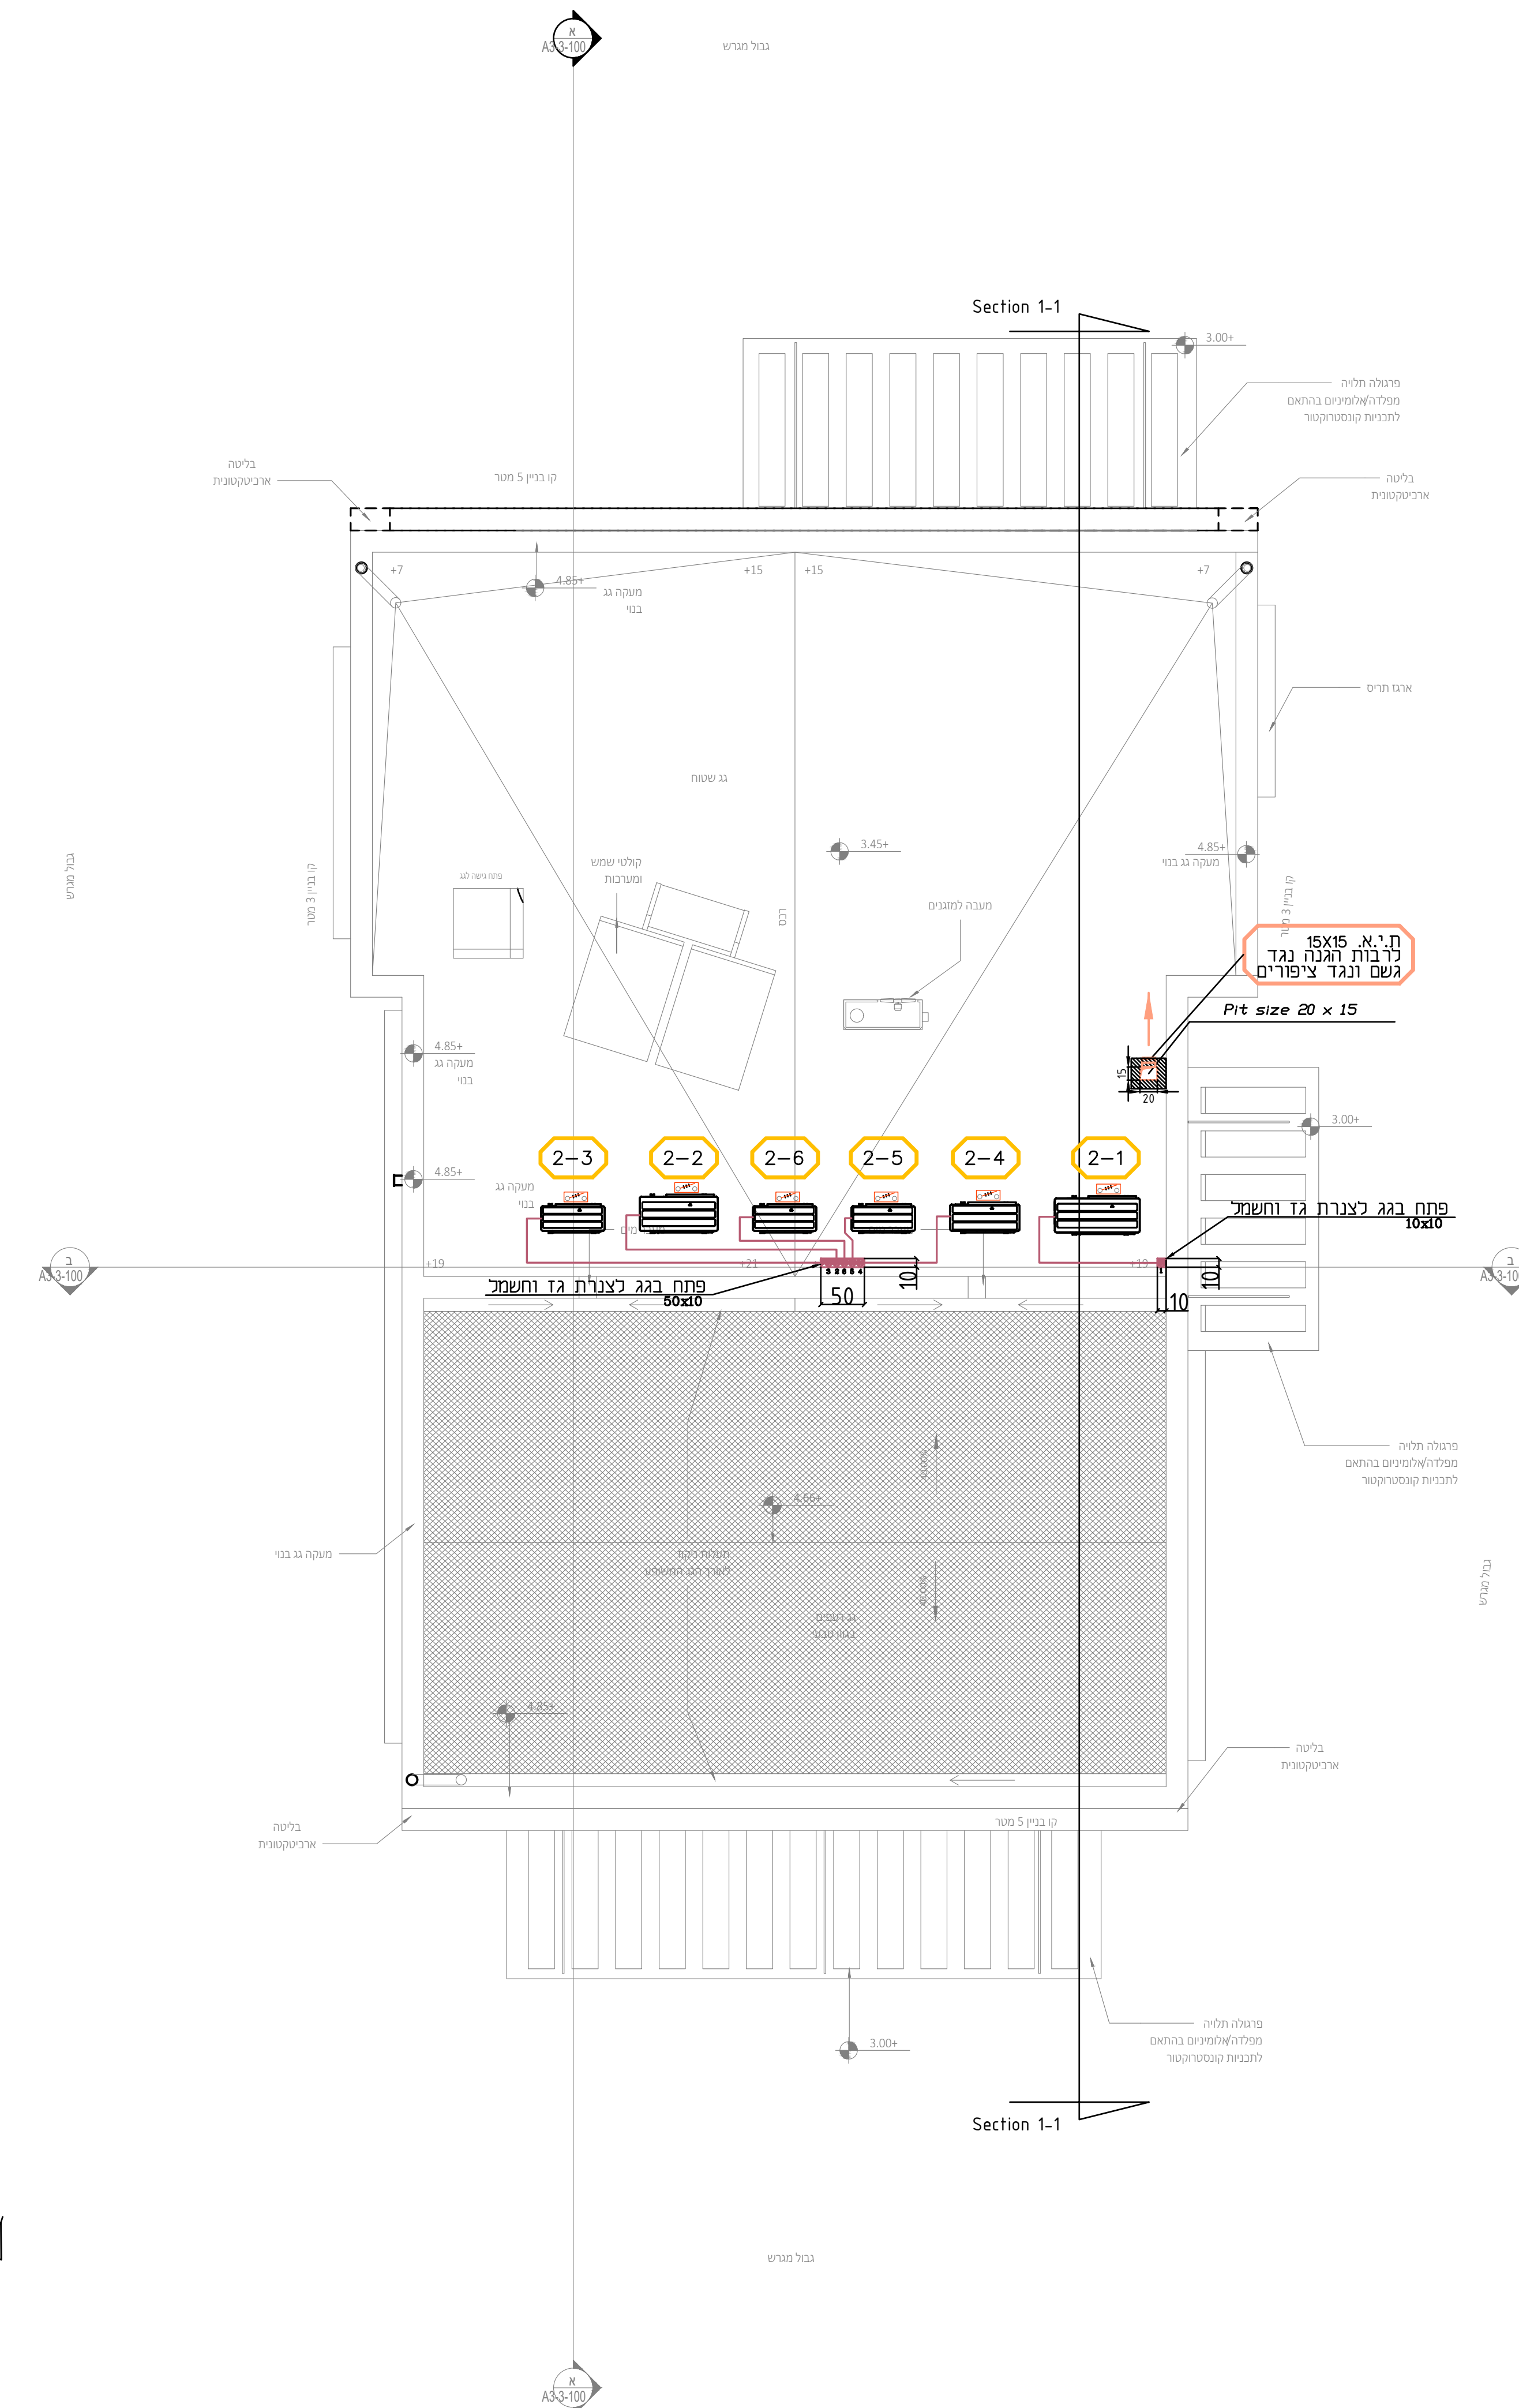

תפוצה

אדריכל	פנים
אונטסציה	
בסחות אש	
אונטסציה	
חשד ותאורה	
קונסטרוקציה	
קבץ ראש	
ניהול פרויקט	
קמח	
אדריכל	

מהדורה

תחילת תפקוד	08.05.2025	א
תחילת תפקוד	01.04.2025	א
תחילת תפקוד	11.03.2025	א
שנים:	חודשי:	סך:

המבצע אחראי למידות ולהתאמתן למציאות בכל מקרה של אי התאמה, סתירה או טעות עליו להודיע למתכנן לפני התקדמותו בביצועו. אין לקבוע מידות על סמך מדידה בשרטוט. אין לרעושת כל שימוש בתוכנית זו או ברעיונות הגלומים בה ללא אישור בכתב מאת המתכנן.

הערות

1. כל התעלות מחייל לממנה יבדודו
בידוד אקוסט פנימי 2"
מידות התעלות הן מידות פח
2. תעלות מזוג בתוך המבנה יבדודו
בידוד אקוסט פנימי 1"
מידות התעלות הן מידות פח
3. תעלות אוויר צה יבדודו
בידוד סרמי 1"
מידות התעלות הן מידות פח
4. יש לאסוף במסילקון את פינוח החיבור
שנעולת מזווח אוויר לפני כיפוף
החמים המתחברים

מקרא

- [illegible]

מקרא צבעים בתכנית

- | | |
|--------------------------|---|
| תעלות ותריסי אוויר חוזר |  |
| תעלות ותריסי אספקת אוויר |  |
| תעלות ותריסי אוויר צח |  |
| תעלות ותריסי יניקת אוויר |  |
| תעלות ותריסי שיחרור עשן |  |
| צנרת גז וחשמל |  |
| סימון מעגלי מזוג אוויר |  |

191	מבני מקדשים צמודי קרקע נפיה אפי' מנשה מגרש 2		
סד פריסם	סד פריסם		
1:50	מיזוג אוויר ואווירור		
מ"ס	קומה ראשונה וגג		
08.05.2025	סד פריסם		
הציון סטודיו			
3			
סטודיו			
☐ נביע ☐ סמך ☒ משרד ☐ עמך	תאריך: 11.03.2025 חבון משרד: איך איד		

אוריכל פנים	
אינסטיציה	
בסיחת אש	
אקוסטיקה	
חשתי והזרה	
קונסטרוקציה	
קבלו ראש	
ניחול פרויקט	
נמח	
אוריכל	

חברות לאשור	08.05.2025	⚠️
חברות לאשור	01.04.2025	⚠️
חברות כעיון	11.03.2025	⚠️
שנתיים:	חאריץ:	100

פס- פסוח	
מ.א.ב. - מפדז אוויר קורי	
מ.א.ת. - מפדז אוויר הקטני	
ת.א.ת. - תריס אוויר חודר	
ת.א.צ. - תריס אוויר צח	
ב.א. - בידוד אקוסטי	
ב.ס. - בידוד טרמי	
כ.ב. - כלא בידוד	
ד.ד. - דפדף אש	
דורמסטנט	
הפדז חתמל	
הפדז חתמל	
תעלות ותריסי אוויר חוזר	
תעלות ותריסי אספקת אוויר	
תעלות ותריסי אוויר צח	
תעלות ותריסי יניקת אוויר	
תעלות ותריסי שיחרור עשן	
צנרת גז וחשמל	
סימון מעגלי מזוג אוויר	

אייל ארז | מהנדסים יועצים
 יעץ וינגטון העירייה מרכז המידע, פיקוח עליון

#	Model name	length in project	factory length
2-3	ALFA PRO INV 140 NG	8.5	15
2-5		8.5	15
2-6		13.0	15
2-4	ALFA PRO INV 240 NG	9.5	15
2-2	AMCOR SLIM INV SQ-240/IP	15.5	30
2-1	SUPER SLIM INV 26	8.0	30