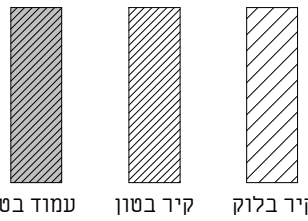


## מתכונים:


|                               |
|-------------------------------|
| ניהול פרויקט                  |
| מהיסוד - בן סלומון            |
| פיקוח                         |
| מהיסוד - בן סלומון            |
| קונסטרוקציה                   |
| ערן שילר                      |
| מיזוג אוויר                   |
| אייל ארז מהנדסים ויועצים בע"מ |
| אינסטלציה                     |
| איתן אלמסי                    |
| חשמל                          |
| איתן בסיס                     |
| אלומיניום                     |
| נוף                           |
| נתי בלוקא                     |
| חשמל חכם                      |
| חימום תת רצפתי                |
| איטום                         |
| צבי טל                        |
| אקוסטיקה                      |
| מעליות                        |
| קרקע וביסוס                   |
| דיה הנדסת קרקע וביסוס         |
| רישוי                         |

[illegible]

מקרא קירות:

[illegible]

## אדריכלות
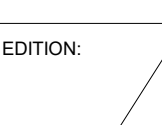
|                   |           |                                                                                     |       |
|-------------------|-----------|-------------------------------------------------------------------------------------|-------|
| CLIENT NAME:      |           | המזכיר                                                                              |       |
| קבוצת רכישה נופיה |           |                                                                                     |       |
| PROJECT NAME:     |           | הפרויקט:                                                                            |       |
| נופיה - מגרש 9    |           |                                                                                     |       |
| DRAWING NAME:     |           | שם הגרסה:                                                                           |       |
| גליון שער         |           |                                                                                     |       |
| SHEET NUMBER:     |           | מספר הגליון:                                                                        |       |
| A3-1-100          |           |                                                                                     |       |
| SCALE:            | קנה מידה: | EDITION:                                                                            | דפוס: |
| סטוס              |           |  |       |
| למכור             |           |                                                                                     |       |
| נבדק עדיין        |           |                                                                                     |       |
| DATE:             | 11.08.25  | תאריך:                                                                              |       |




office@nh-arch.com  
www.nh-arch.com

וימן חיינר אדריכלים  
מורד ההדרים 2, בית חירות  
טל 09-9545842

זכויות יוצר / ע"פ הנחיות עו"ד

| נפיה - מגרש 9 |                              |        |                   |
|---------------|------------------------------|--------|-------------------|
| מס' גיליון    | שם גיליון                    | מהדורה | תאריך הפצת מהדורה |
|               |                              |        |                   |
| A3-1-100      | גיליון שער                   | 1      | 22.09.2025        |
| A3-1-101      | קומת קרקע                    | 1      | 22.09.2025        |
| A3-1-102      | קומת גג                      | 1      | 22.09.2025        |
| A3-1-103      | תוכנית תקרה ותאורה קומת קרקע | 1      | 22.09.2025        |
| A3-2-200      | חזיתות 1                     | 1      | 22.09.2025        |
| A3-2-201      | חזיתות 2                     | 1      | 22.09.2025        |
| A3-3-100      | חתיכים                       | 1      | 22.09.2025        |
| A3-4-103      | פרטים                        | 1      | 22.09.2025        |
| A3-4-104      | פרטי פרגולה                  | 1      | 22.09.2025        |
| A3-6-1000     | רשימת פתחים                  | 1      | 22.09.2025        |

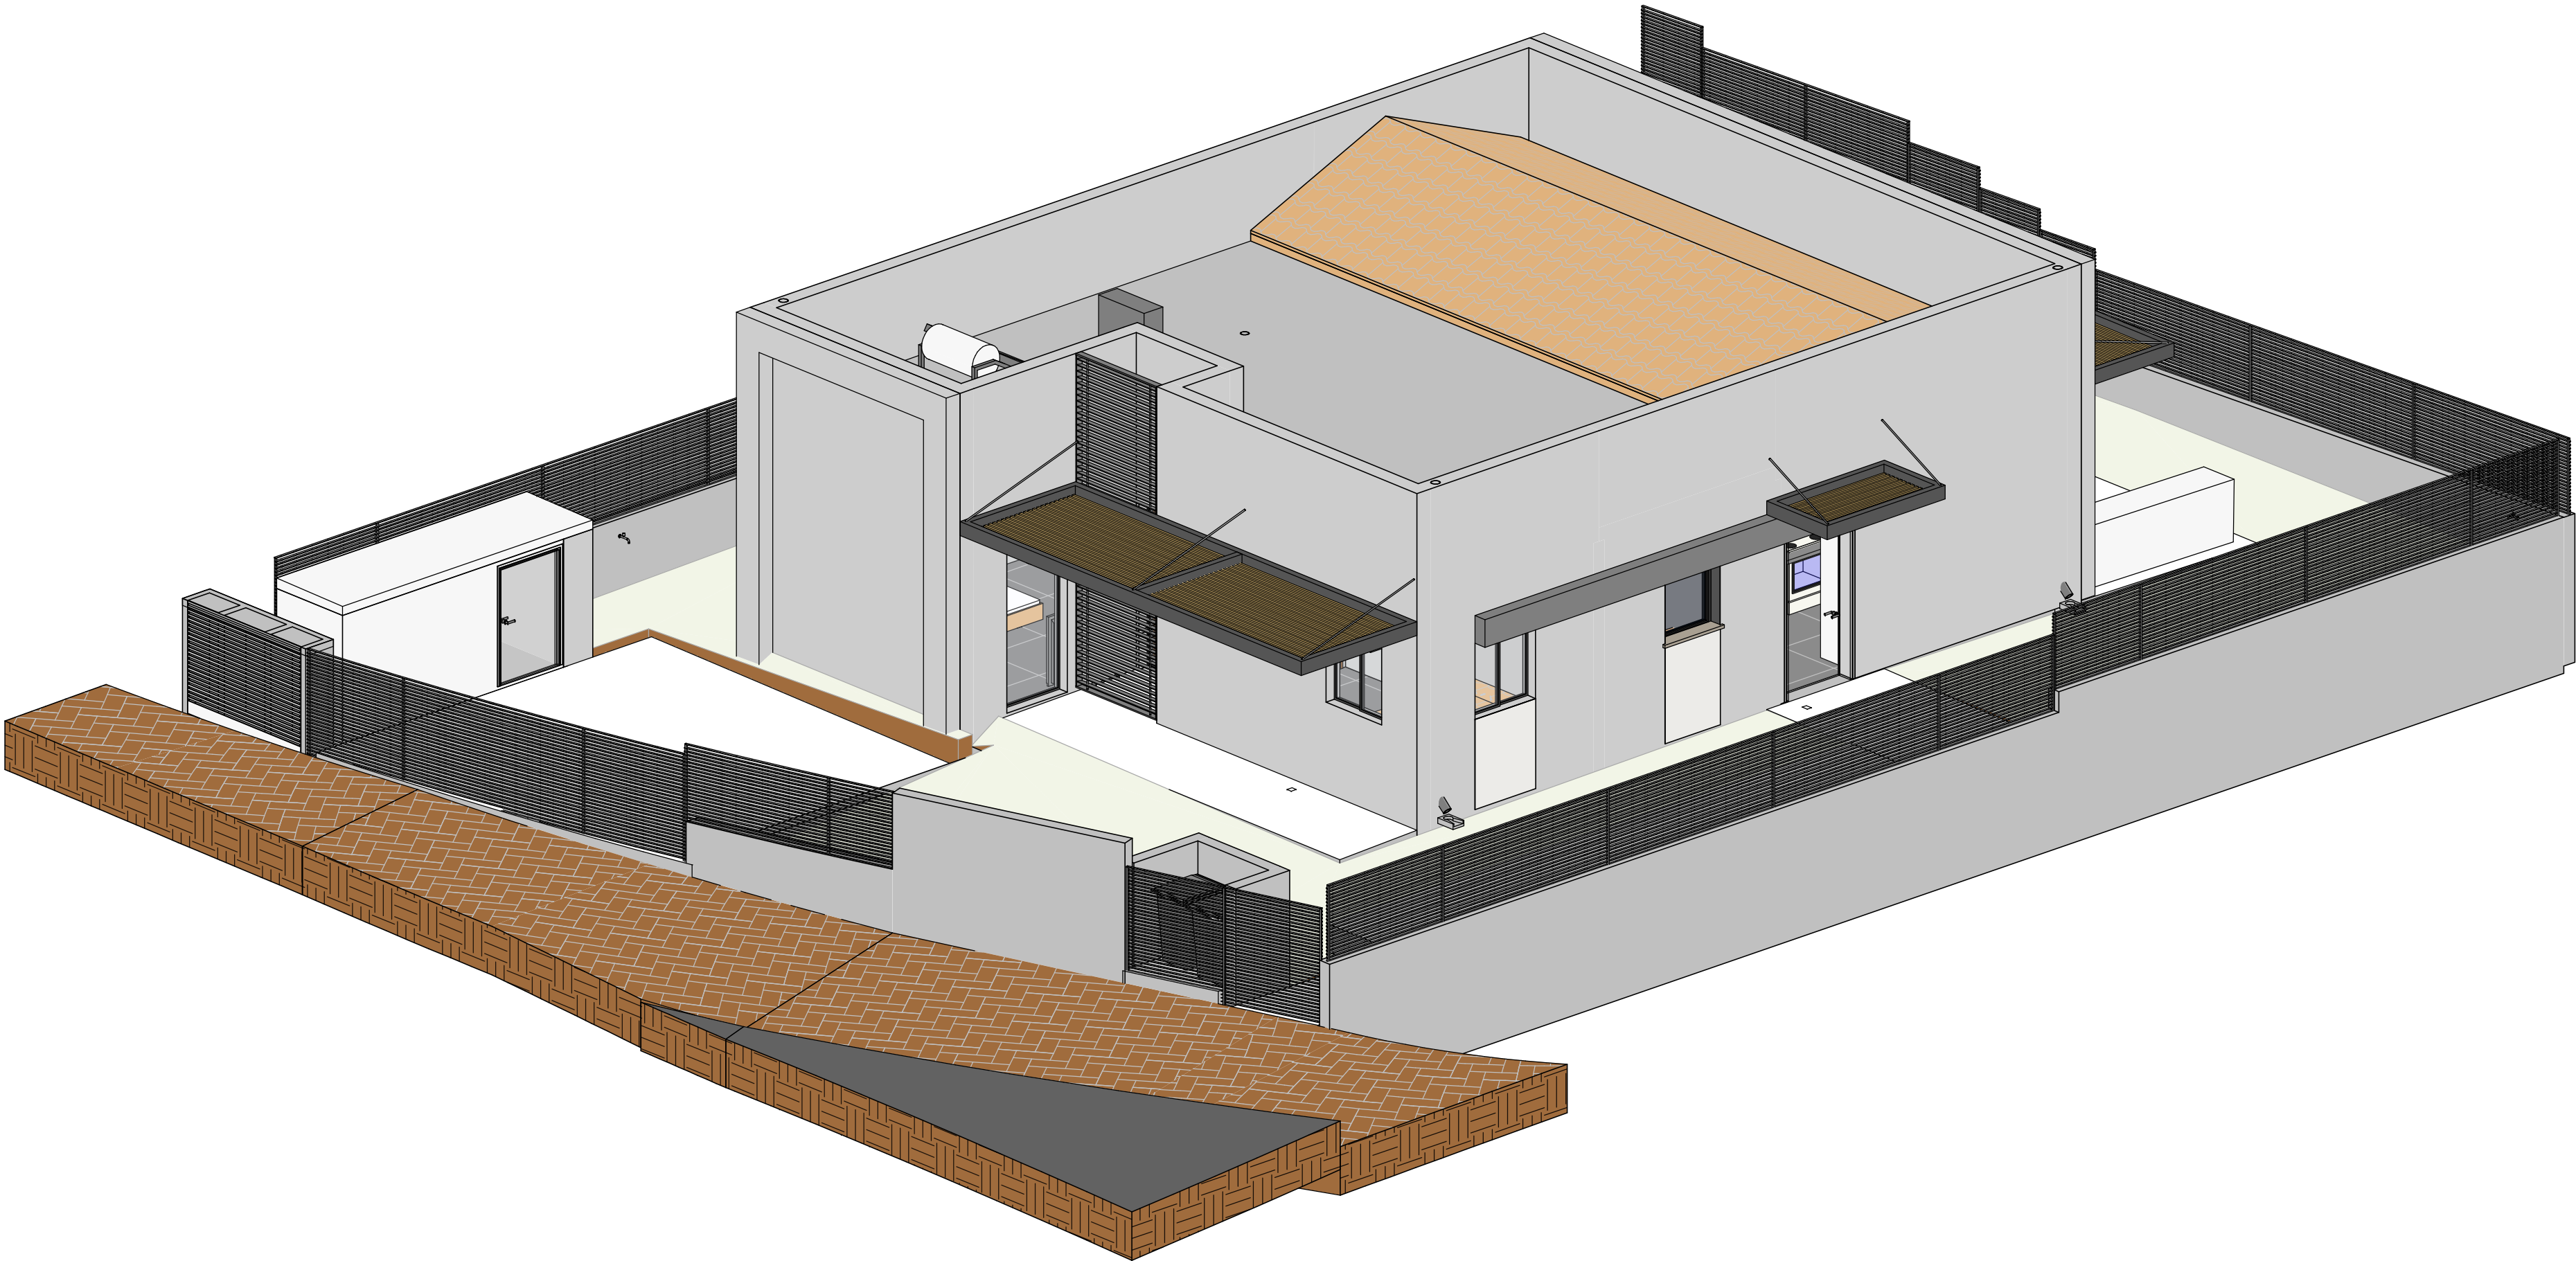

|                               |
|-------------------------------|
| ניהול פרויקט                  |
| מהיסוד - בן סלומון            |
| פיקוח                         |
| מהיסוד - בן סלומון            |
| קונסטרקציה                    |
| ערן שילר                      |
| מיזוג אוויר                   |
| אייל ארז מהנדסים ויועצים בע"מ |
| אינסטלציה                     |
| איתן אלמסי                    |
| חשמל                          |
| איתן בסיס                     |
| אלומיניום                     |
|                               |
| נוף                           |
| נתי בלוקא                     |
| חשמל חכם                      |
|                               |
| חימום תת רצפתי                |
|                               |
| איטום                         |
| צבי טל                        |
| אקוסטיקה                      |
|                               |
| מעליות                        |
|                               |
| קרקע וביסוס                   |
| דיה הנדסת קרקע וביסוס         |
| רישוי                         |

[illegible][illegible][illegible]

CLIENT NAME: \_\_\_\_\_ שם המזמין:

## PROJECT NAME: \_\_\_\_\_ שם הפרויקט: \_\_\_\_\_

DRAWING NAME: סגליון:

SHEET NUMBER: 198 גליון:

|        |           |          |        |
|--------|-----------|----------|--------|
| SCALE: | קנה מידה: | EDITION: | הדורה: |
|--------|-----------|----------|--------|

|        |                                                                                     |
|--------|-------------------------------------------------------------------------------------|
| 1 : 50 |  |
|--------|-------------------------------------------------------------------------------------|

למחרת

|          |           |
|----------|-----------|
| רמט ע"י: | נבדק ע"י: |
|----------|-----------|


DATE: 11.08.25 זמיר:



NeumanHaynerArchitects

office@nh-arch.com  
www.nh-arch.com

זכויות ייצור / ע"פ הנחיות עו"ד

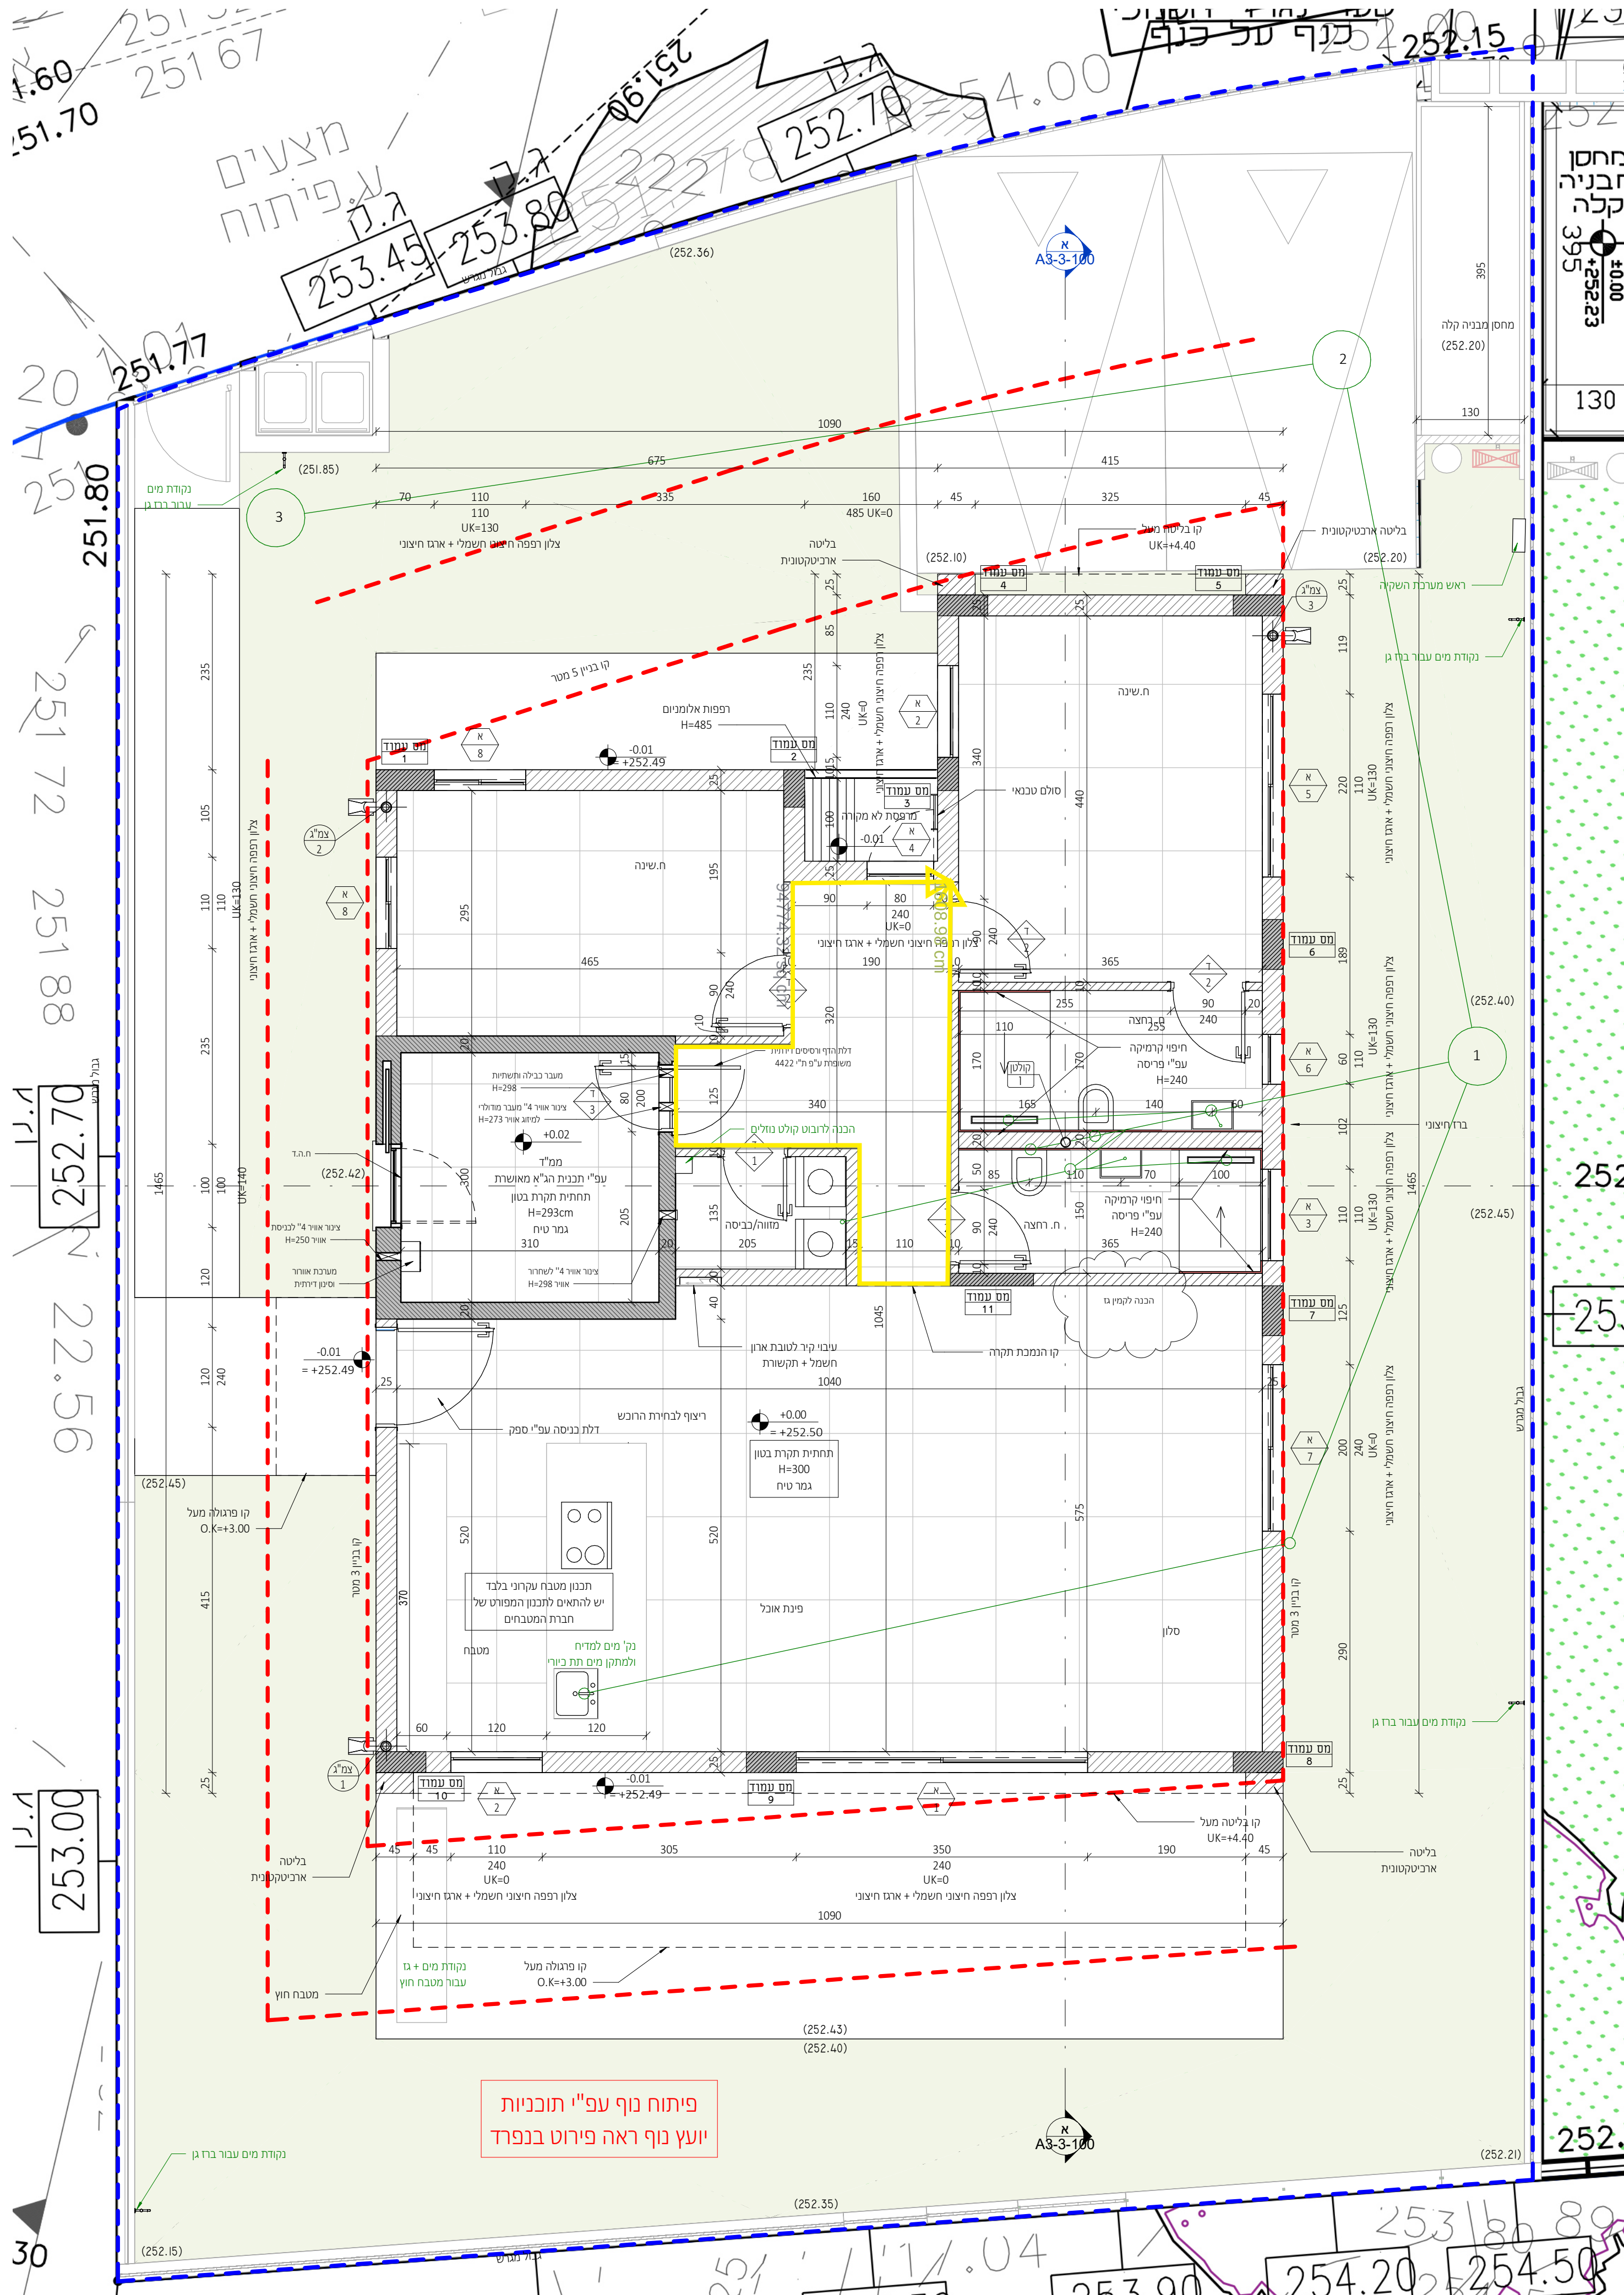

1 : 50

1. יש לעבוד במקביל לתכניות יועצים המאושרות על ידי האדריכל.
2. פרטי ספי חלון - עפ"י חוברת אלומיניום של הספק הנבחר ובתיאום מול אדריכל.
3. חימום תת רצפתי (במידה ויש במגרש זה) עפ"י פרטי הספק ובתיאום מול אדריכל.
4. יש לעבוד במקביל לתכניות עיצוב פנים (במידה ויש מעצב פנים במגרש זה) המאושרות על ידי האדריכל.
5. באחריות הקבלן לעדכן את האדריכל על אי התאמה בין התכניות יועצים לאדריכלות.
6. כל הדלתות לפי מפרט מצורף.
7. כל אלמנטי הבטון יקבלו התייחסות תרמית לפי הנחיות יועץ.
8. פרטי איטום, בידוד וניקוז עפ"י תכניות יועצים ובאחריות הקבלן.

## מתכונים:


|                               |
|-------------------------------|
| ניהול פרויקט                  |
| מהיסוד - בן סלומון            |
| פיקוח                         |
| מהיסוד - בן סלומון            |
| קונסטרוקציה                   |
| ערן שילר                      |
| מיזוג אוויר                   |
| אייל ארז מהנדסים ויועצים בע"מ |
| אינסטלציה                     |
| איתן אלמסי                    |
| חשמל                          |
| איתן בסיס                     |
| אלומיניום                     |
| בופ                           |
| נתי בלוקא                     |
| חשמל חכם                      |
| חימום תת רצפתי                |
| איטום                         |
| צבי טל                        |
| אקוסטיקה                      |
| מעלות                         |
| קרקע וביסוס                   |
| דיה הנדסת קרקע וביסוס         |
| רישוי                         |

$$\pm 0.00 = +252.50$$

**הערות:**  
 1. תכנית זו יש לקרוא יחד עם תכניות הוועצים.  
 2. גובה אבסולוטי – ראו תכנית פיתוח.  
 3. המידות הן ב' ביורות תחתית' (ראו כלול 1.10).  
 4. פיתוח השטח בשטח חניה, הנהגה, כלכלי, מדרגות, גדרות, שביליים, רציפים,  
 5. פסיפוגים וכו'.  
 6. ראו תכנית פיתוח.  
 7. ראו תכנית פיתוח.  
 8. אסוס. תכנית ורצפות התקנה במגע עם הקרקע ובידוד תרמי לאורך המעטרים  
 9. הקורות ועל התקורות – כליות או עם מיני (גירון) – ראו תכניות קונסטרוקציה  
 10. א. פ. כ. יבוצע במישור אופקי חתוכי החתך.  
 11. ראו תרמי במסגרת – ראו פרט מורחב, חתוכי החתך. ע"י פיקוד מרחוק.

[illegible]

זקרא קירות:

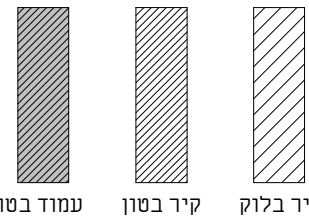[illegible]

## אדריכלות

CLIENT NAME: \_\_\_\_\_ שם המזמין:

## קבוצת רכישה נופיה

PROJECT NAME: \_\_\_\_\_ שם הפרויקט:

נופיה - מגרש 9

DRAWING NAME: ס הגליון:

## קומת גג

SHEET NUMBER: 190 גליון:

A3-1-102

SCALE:                      קנה מידה:    EDITION:                      הדורה:

1 : 50

STATUS: סמטוט 1

|      |                                                                                     |
|------|-------------------------------------------------------------------------------------|
| למכר |  |
|------|-------------------------------------------------------------------------------------|

רשט ע"י: \_\_\_\_\_ נבדק ע"י: \_\_\_\_\_




NeumanHaynerArchitects

office@nh-arch.com  
www.nh-arch.com

וימן חיינר אדריכלים  
אורז הקזרים 2 בית חירות

זכויות ייצור / ע"פ הנחיות עו"ד

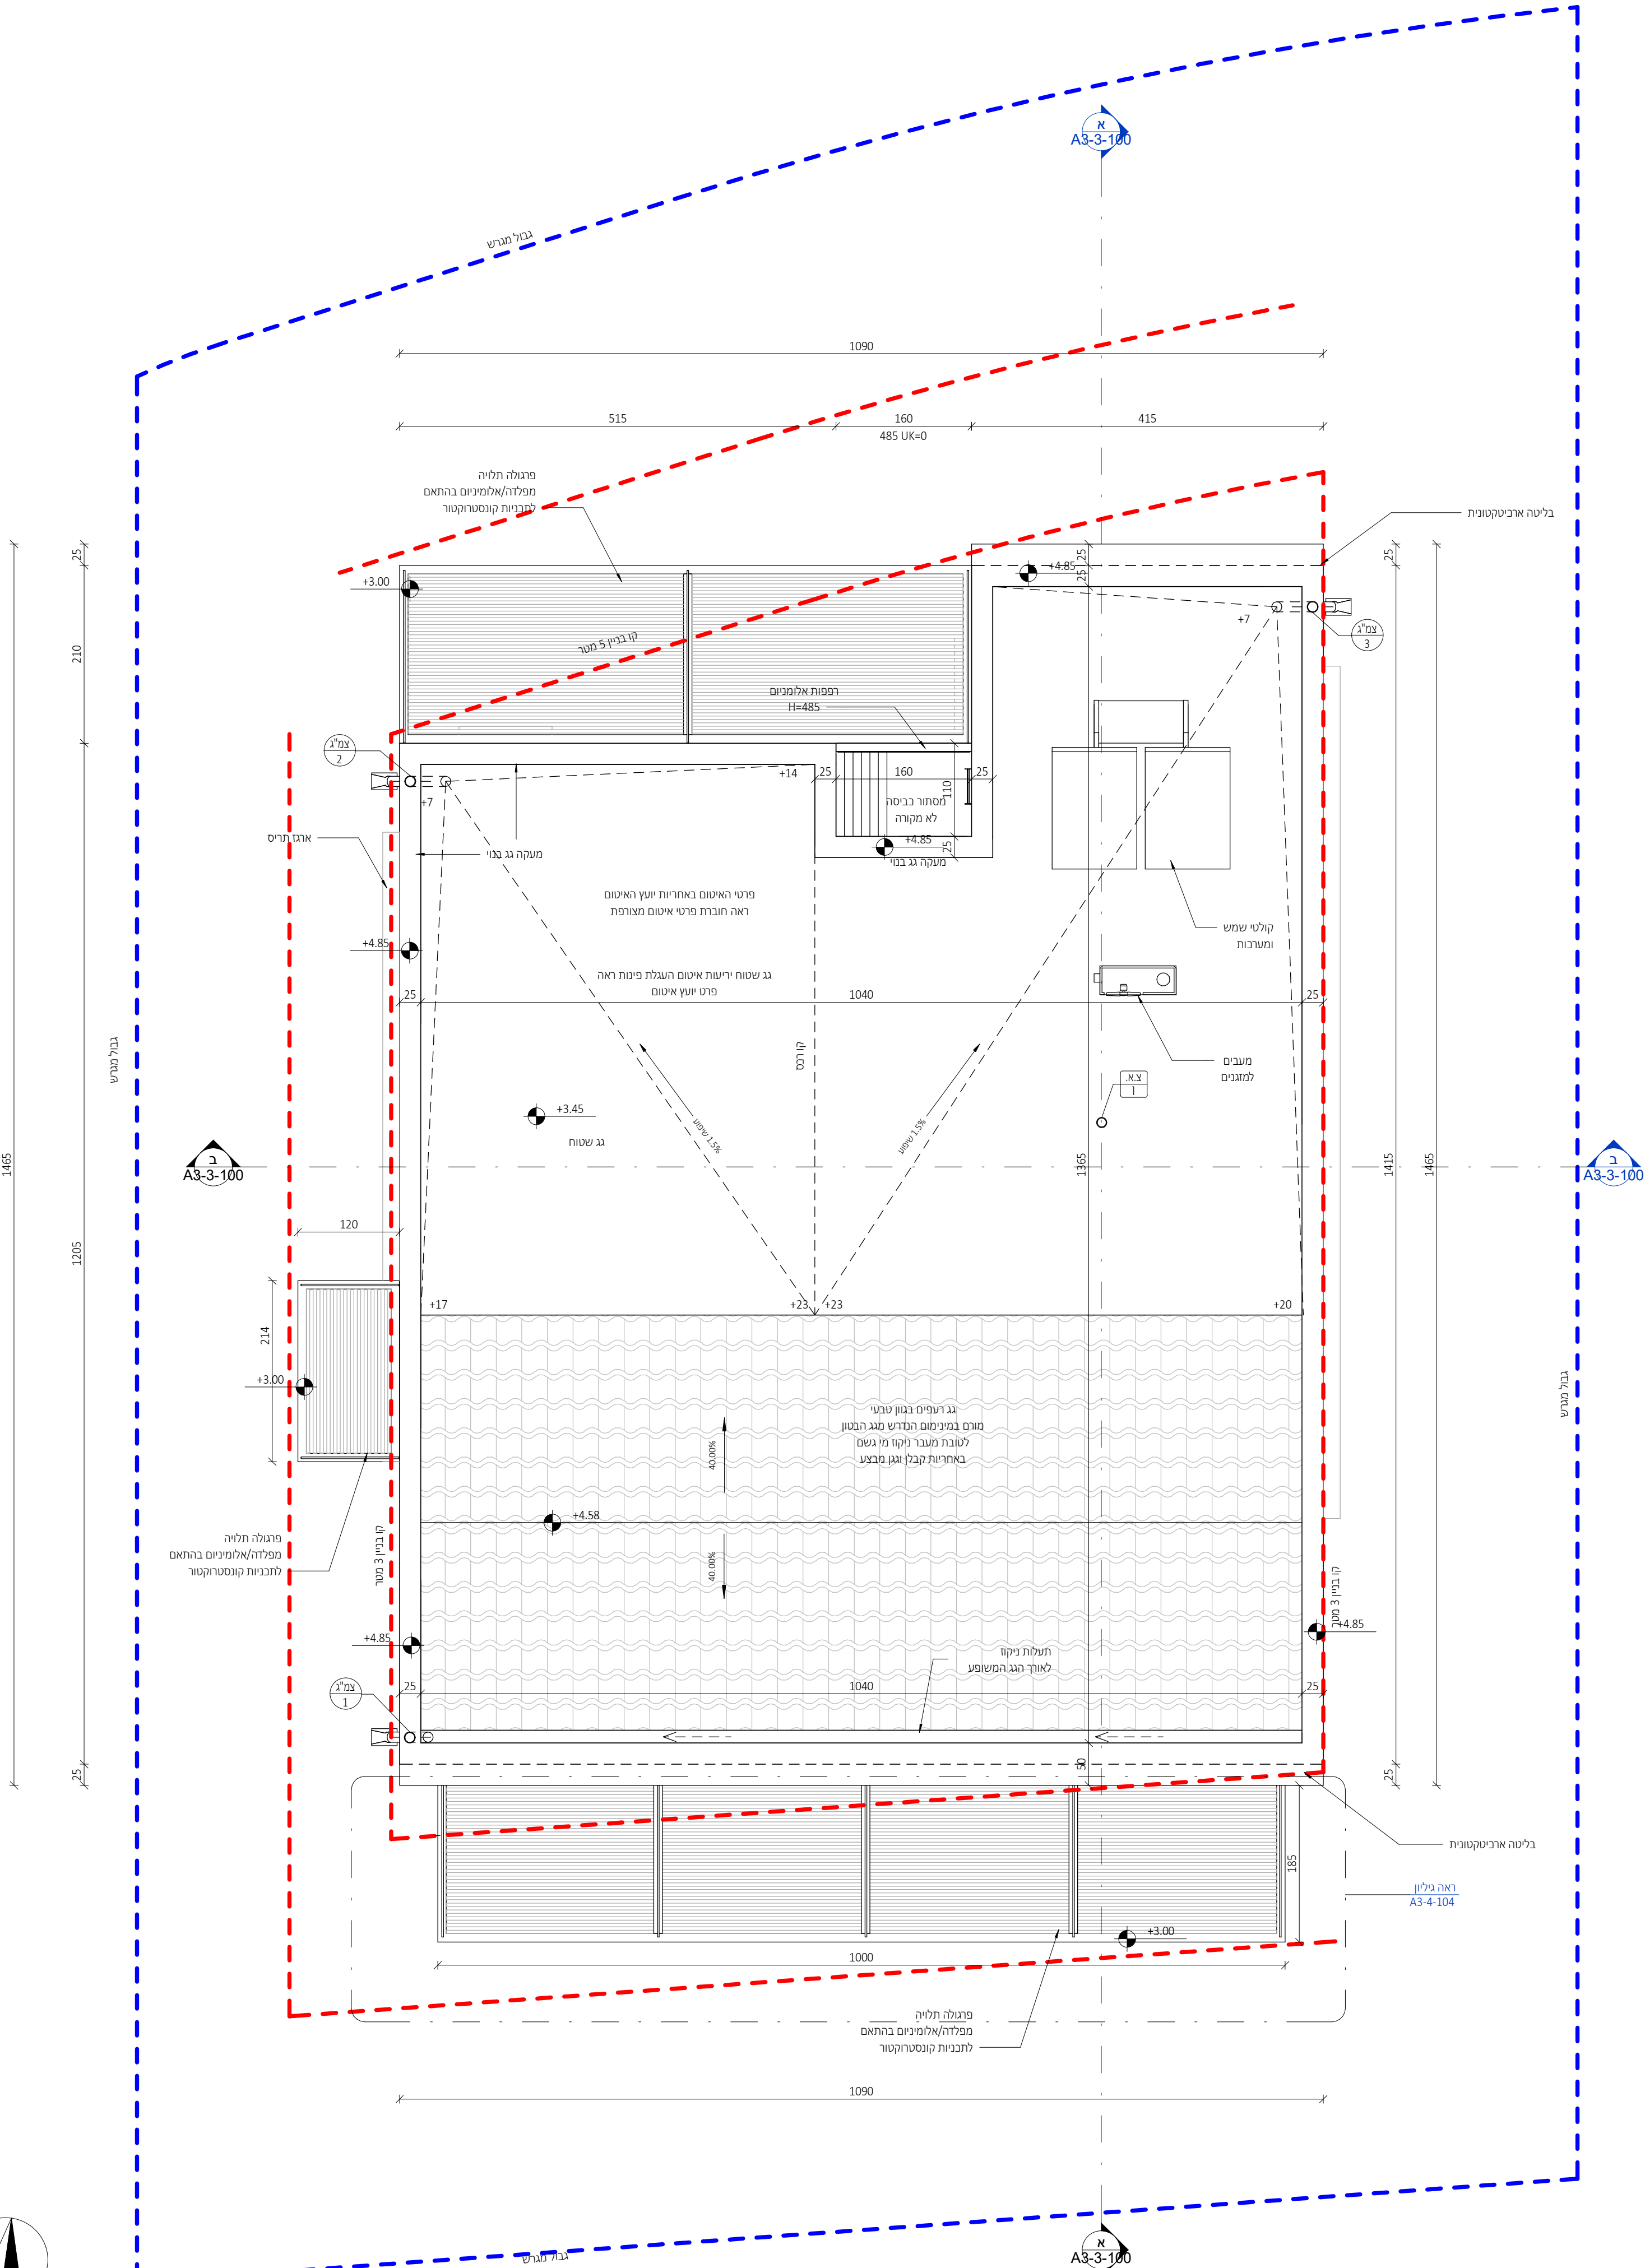

## תכנית גג

1 : 50

## מתכונים:

|                               |
|-------------------------------|
| ניהול פרויקט                  |
| מהיסוד - בן סלומון            |
| פיקוח                         |
| מהיסוד - בן סלומון            |
| קונסטרוקציה                   |
| ערן שילר                      |
| מיזוג אוויר                   |
| אייל ארז מהנדסים ויועצים בע"מ |
| אינסטלציה                     |
| איתן אלמסי                    |
| חשמל                          |
| איתן בסיס                     |
| אלומיניום                     |
| נוף                           |
| נתי בלוקא                     |
| חשמל חכם                      |
| חימום תת רצפתי                |
| איטום                         |
| צבי טל                        |
| אקוסטיקה                      |
| מעליות                        |
| קרקע וביסוס                   |
| דיה הנדסת קרקע וביסוס         |
| רישוי                         |

[illegible][illegible]

|   |                                                                                  |
|---|----------------------------------------------------------------------------------|
| <div> <div>אדריכלות</div> <div> <div>PROJECT NAME:</div> <div>התוכנית</div> </div> </div>                     |                                                                                  |
| <div> <div>קבוצת רכישה נופיה</div> <div> <div>PROJECT NAME:</div> <div>התוכנית</div> </div> </div>            |                                                                                  |
| <div> <div>נופיה - מגרש 9</div> <div> <div>DRAWING NAME:</div> <div>התוכנית</div> </div> </div>               |                                                                                  |
| <div> <div>תוכנית תקרה ותאורה קומת קרקע</div> <div> <div>DRAWING NAME:</div> <div>התוכנית</div> </div> </div> |                                                                                  |
| <div> <div>A3-1-103</div> <div> <div>SHEET NUMBER:</div> <div>960 גליון</div> </div> </div>                   |                                                                                  |
| <div> <div>CALE:</div> <div>עוד מידע:</div> </div>                                                            | <div> <div>EDITION:</div> <div>הדורה:</div> </div>                               |
| <div> <div>As indicated</div> <div> <div>TATUS:</div> <div>סטוס</div> </div> </div>                           | <div> <div>1</div> <div> <div>סטוס ע"י:</div> <div>בדוק ע"י:</div> </div> </div> |
| <div> <div>DATE:</div> <div>11.08.25</div> </div>                                                             | <div> <div>חידוש:</div> <div>חידוש</div> </div>                                  |



  
 יוֹסֵפִין חֵינֶר אדריכלים  
 יוֹרְד הַהוֹדִים 2, בֵּית חִירוֹת  
 7658454-09

---

זכרון יצור / ע"פ הנחיות ע"ר

office@nh-arch.com  
 www.nh-arch.com

NeumanHaynerArchitects

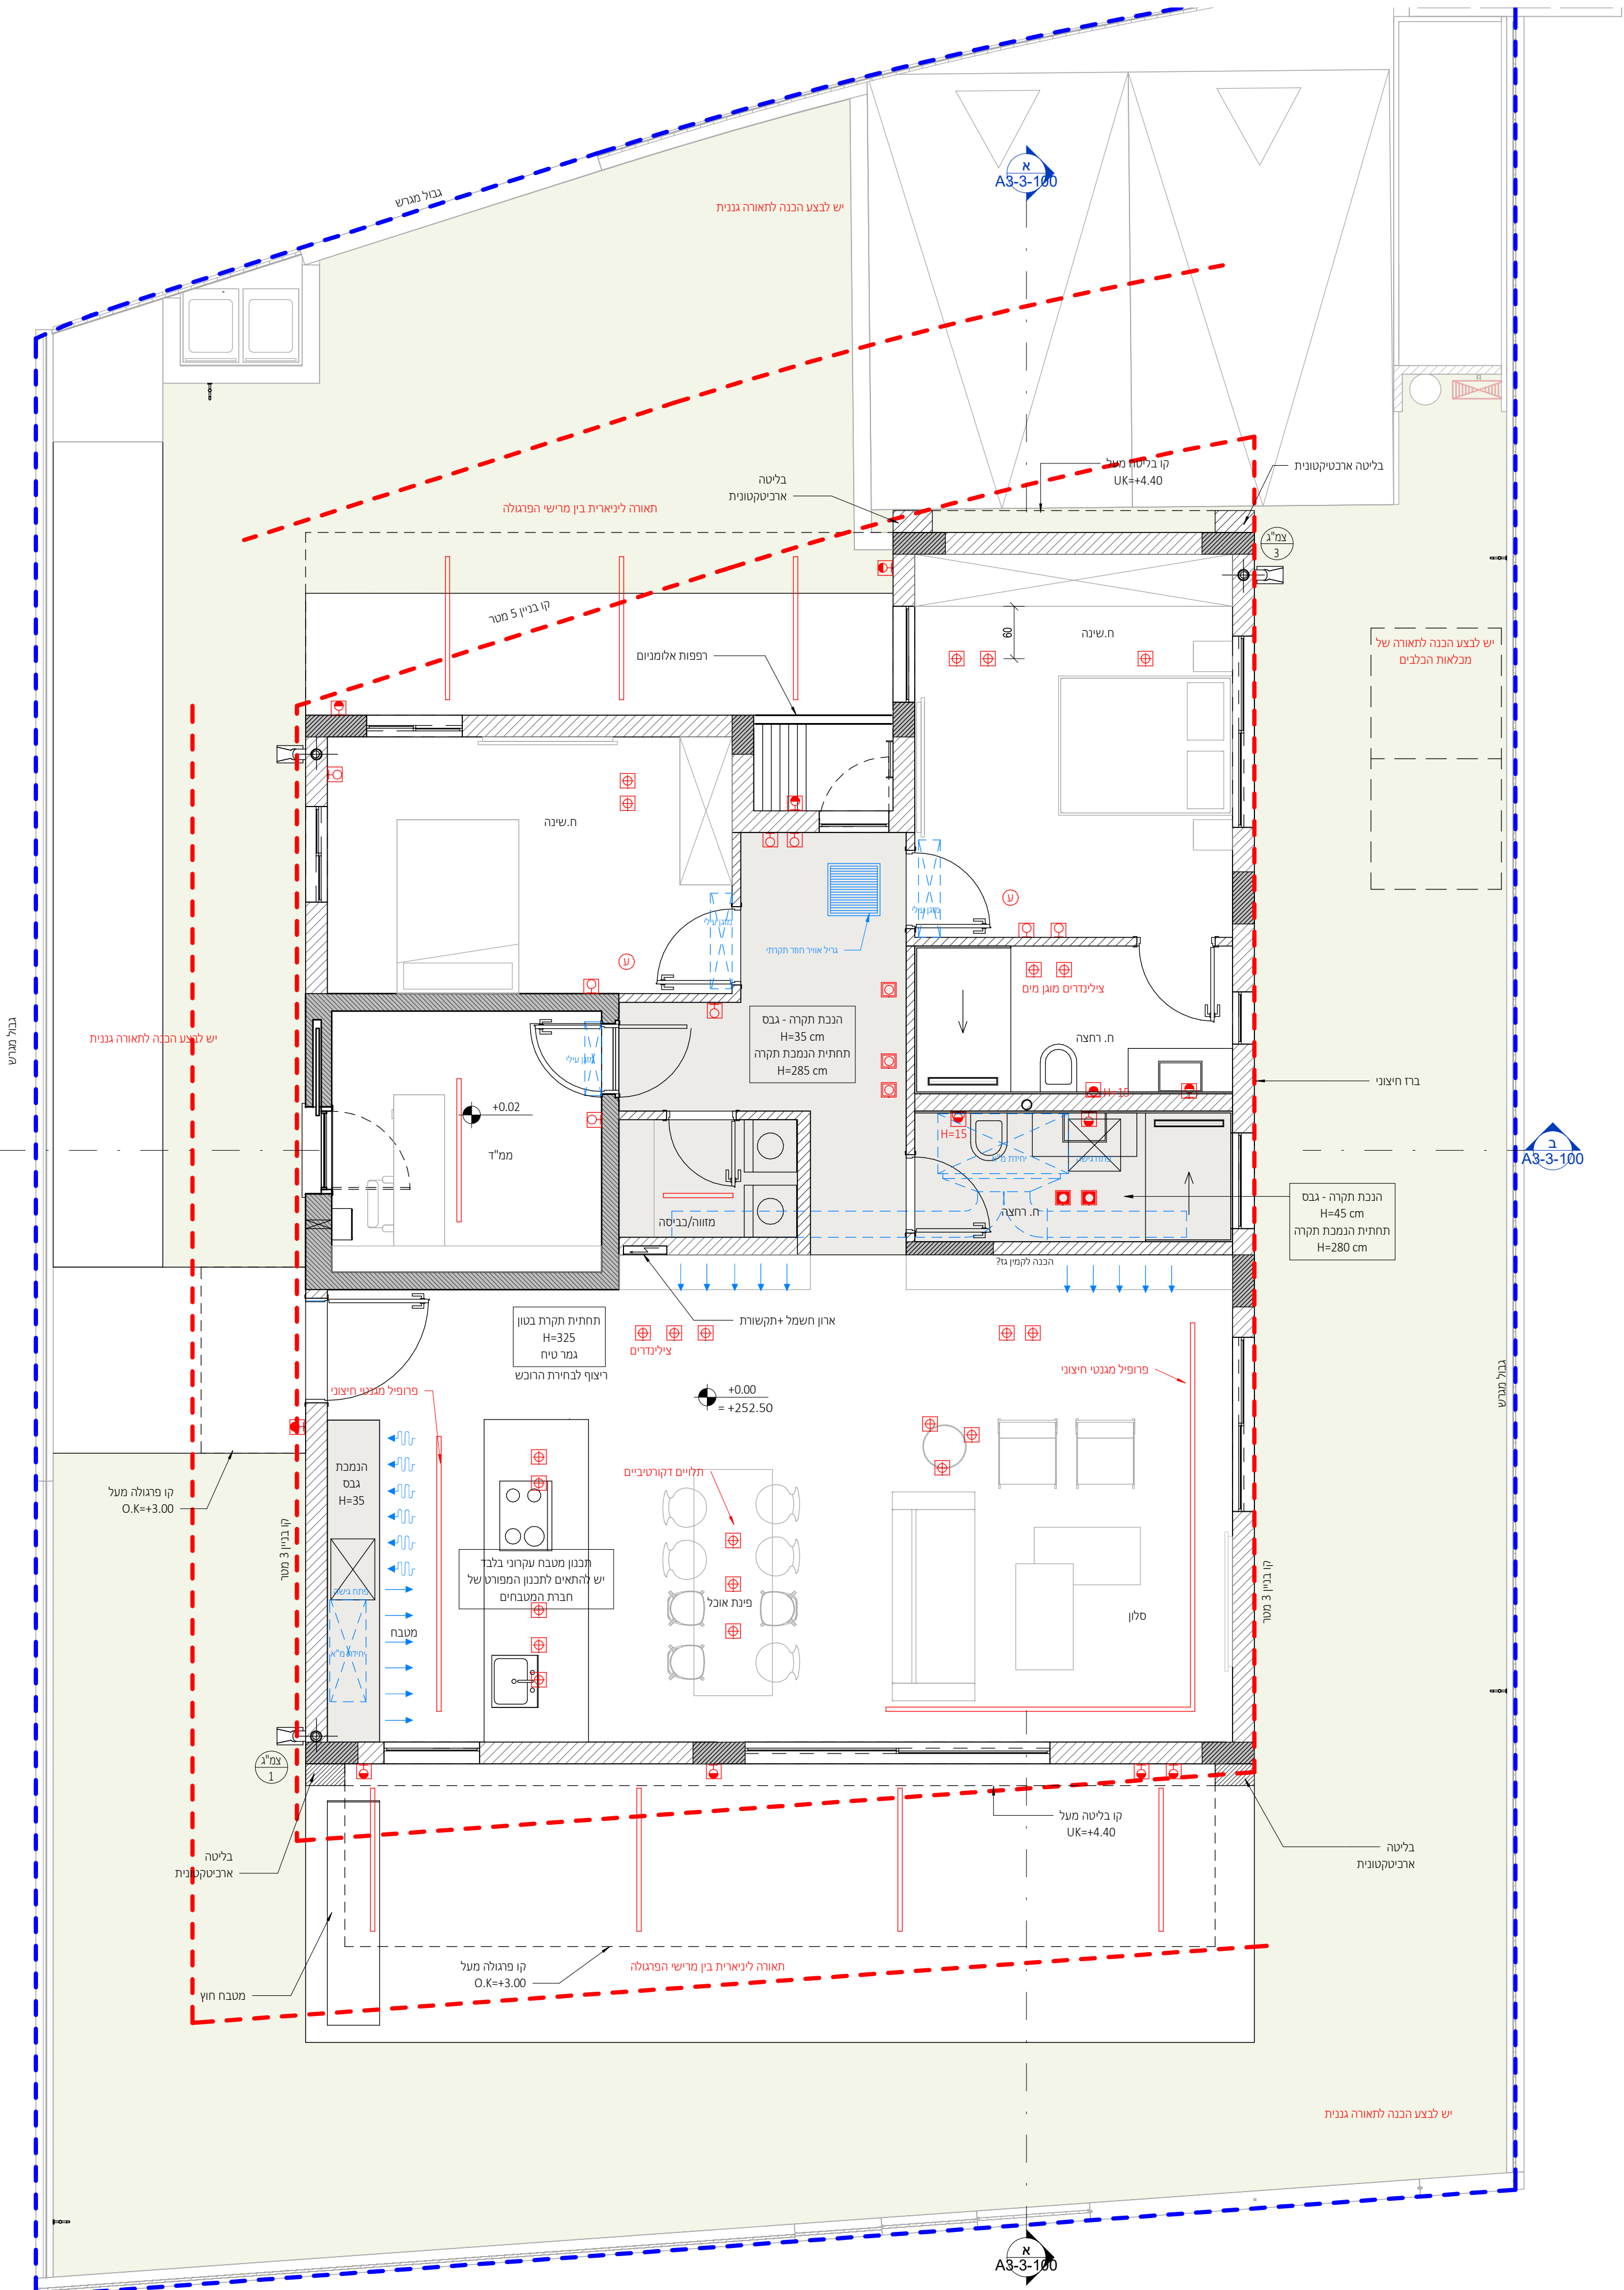

-תכנית חשמל - תהיה עפ"י גליון של יועץ חשמל.

2. תכנית תאורה, מיקום גופי תאורה - עפ"י גליון זה.

3. יש לעבוד במקביל לתכניות של מתכנן מיזוג אוויר, ובתיאום מול אדריכל.

4. מידות סופיות בין גופי תאורה ינתנו לאחר בחירה סופית של הדגמים.

5. מיזוג אוויר - מיקום התקנת יחידות ומיקום תריסים, פתחי שירות - לתיאום סופי מול אדריכל לפני ביצוע.

6. חימום תת רצפתי עפ"י פרטי הספק ובתיאום מול אדריכל.

## מקרא חשמל ותאורה

|                                 |  |  |
|---------------------------------|--|--|
| שקעים ואביזרים                  |  |  |
| בית תקע                         |  |  |
| בית תקע כוח                     |  |  |
| בית תקע מוגן מים                |  |  |
| נקודת טלפון                     |  |  |
| נקודת אינטרנט                   |  |  |
| נקודת תנור אמבטיה               |  |  |
| נקודת טל"כ / לוויין             |  |  |
| נקודת הזנה למנוע תריס חשמלי     |  |  |
| נקודת הפעלה לתריס חשמלי         |  |  |
| נקודת הזנה למנוע ונטה חשמלי     |  |  |
| צינור שרשרי 15 מ"מ עם חוט משיכה |  |  |
| נקודת אינטרקום                  |  |  |
| נקודת אינטרקום טלויזיוני        |  |  |
| פעמון דירתי תקני 12V            |  |  |
| H=40 סימבוקס אלא אם צוין אחרת   |  |  |

|                                    |                                                                                       |
|------------------------------------|---------------------------------------------------------------------------------------|
| אודיו וידאו                        |                                                                                       |
| רמקול באמצעות צינור פ.נ 16 מ"מ     |  |
| רמקול שקוע בקיר. קופסה לפי תוכנית  |  |
| רמקול שקוע בתקרה. קופסה לפי תוכנית |  |

|  |                   |                                                                                       |
|--|-------------------|---------------------------------------------------------------------------------------|
|  | בטחון             |                                                                                       |
|  | מקלדת הפעלה       |  |
|  | צופר אזעקה        |  |
|  | גלאי נפח          |  |
|  | גלאי יולון חיצוני |  |

## הנחיות


1. לקרוא תוכנית וזכור עיקרי מחזור
2. מקבוצה של 5 ימים, התאמה של "לדעת האדריכל"
3. במיתות (נ) למרכז אביראל אלא ציון אחרת
4. קיומם האבירים באיורים משותפים פטרוס פטרוס
5. ולמקום בהתאם
6. הבה התפקסין היו  $H=90$  אלא אם ציון אחרת
7. הבה תפקסין / מקלות-זקוקה / פיקוד-מגן אחד
8. הבה השני ש למרכזם צו להאמע
9. חזו על רכש של להשאר
10. חזו על 5 פ"ס
11. חזו על 5 פ"ס
12. בידועה רחוקה
13. ש לידע את האדריכל
14. גמר התפקסין בתואם ממו לאדריכל
15. חזו אודות רכש תפקסין בעוד לאדריכל הרכיב (מקורס הרכיב)
16. חזו הקשר לאותו אבית
17. מספק נדון אסמכניה ומספק נדון מים השליל  $H=150$  עפי' התקן
18. הבה השקעים היו  $H=40$  אלא אם ציון אחרת
19. הבה חסותות היו  $H=210$  אלא אם ציון אחרת
20. הבה חסותות היו  $H=15$  אלא אם ציון אחרת

מתכנים:

|                               |
|-------------------------------|
| ניהול פרויקט                  |
| מהיסוד - בן סלומון            |
| פיקוח                         |
| מהיסוד - בן סולומון           |
| קונסטרוקציה                   |
| ערן שילר                      |
| מיזוג אוויר                   |
| אייל ארז מהנדסים ויועצים בע"מ |
| אינסטלציה                     |
| איתן אלמסי                    |
| חשמל                          |
| איתן בסיס                     |
| אלומיניום                     |
| נוף                           |
| נתי בלוקא                     |
| חשמל חכם                      |
| חימום תת רצפתי                |
|                               |
| איטום                         |
| צבי טל                        |
| אקוסטיקה                      |
|                               |
| מעליות                        |
|                               |
| קרקע וביסוס                   |
| דיה הנדסת קרקע וביסוס         |
| רישוי                         |

|   |
|---|
| ± 0.00 = +252.50   |
| הערות:<br>1. תכנית זו הי לקרא יחד עם תכנית הרוטטים.<br>2. גובה אבטומטי - ראה תכנית פירוט.<br>3. הפירות הן בין קירות הבניה ולא כולל פחים.<br>4. פיתוח השטח סביב הבנוה, כולל, מדרגות, גדרות, שבילים, ריצופים, שטחים גזרים, חניה גינה ורא תכנית פירוט.<br>5. איטום קירות ורצפות הבנוה כמעט עם הקרקע ובידוד תרמי לאורך העמודים והקורות ופני המעקה. כלירות או עם סימני גיבס - ראה תכנית קונסטרוקציה.<br>6. אף דום יבוצע בכל מישור אופקי הבולם חתביון.<br>7. פחי תרמי במסג' ע"פ מפרט תרמוקור, מאושר ט"י פיקוד העורף.<br><br>המבצע אחראי למידות : עליו לבקר ולבדוק את כל המידות בתכנית ובמקום הבנויה.<br>במסג' של מידות או אי התאמה בתכנית /או בבנין, עליו להודיע על כך מיד לאדריכל בסופו המשיך בעבודתו.<br>המבצע ישתמש או ויק, בזכיות שאושרו לכניסיו.<br>המבצע יחזיק באחר, בכל עת, של מידות של תכנית.<br>אין לקבוע מידות על ידי חזירה בשו מוס.<br>התכנית הנה רכוש האדריכל ואין לשנות כל שימוש בה או ברעיונות הגלומים בה, אלא באישור בכתב מהאדריכל.<br>מחנדים /או יושע אשר שמו רשום בתכנית זו, נושא לכדי באחריות המקצועית והתקנית לתכנית.<br>על המפיק והמבצע לזרוא התאמת התכנית האדריכלית "כניסיו" לתכנית יחיד, המכר והתכנית המאושרות ע"י כל גורמים הרשמיים.<br>התכנית כוללת את כל האחריות והידוע על ליום תוצאתה. |


משרד קירות:

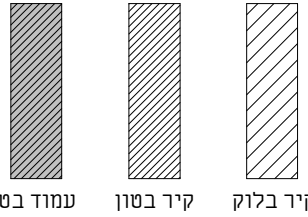

| תאריך      | תיאור | מהדורה |
|------------|-------|--------|
| 22.09.2025 | מכרז  | 1      |
|            |       |        |
|            |       |        |
אדריכלות


|                   |               |
|-------------------|---------------|
| שם המשיין:        | CLIENT NAME:  |
| קבוצת רכישה נופיה |               |
| שם הפרויקט:       | PROJECT NAME: |
| נופיה - מגרש 9    |               |
| שם הגיליון:       | DRAWING NAME: |
| חזיתות 1          |               |
| מספר גיליון:      | SHEET NUMBER: |
| A3-2-200          |               |
| תאריך:            | DATE:         |
| 11.08.25          |               |

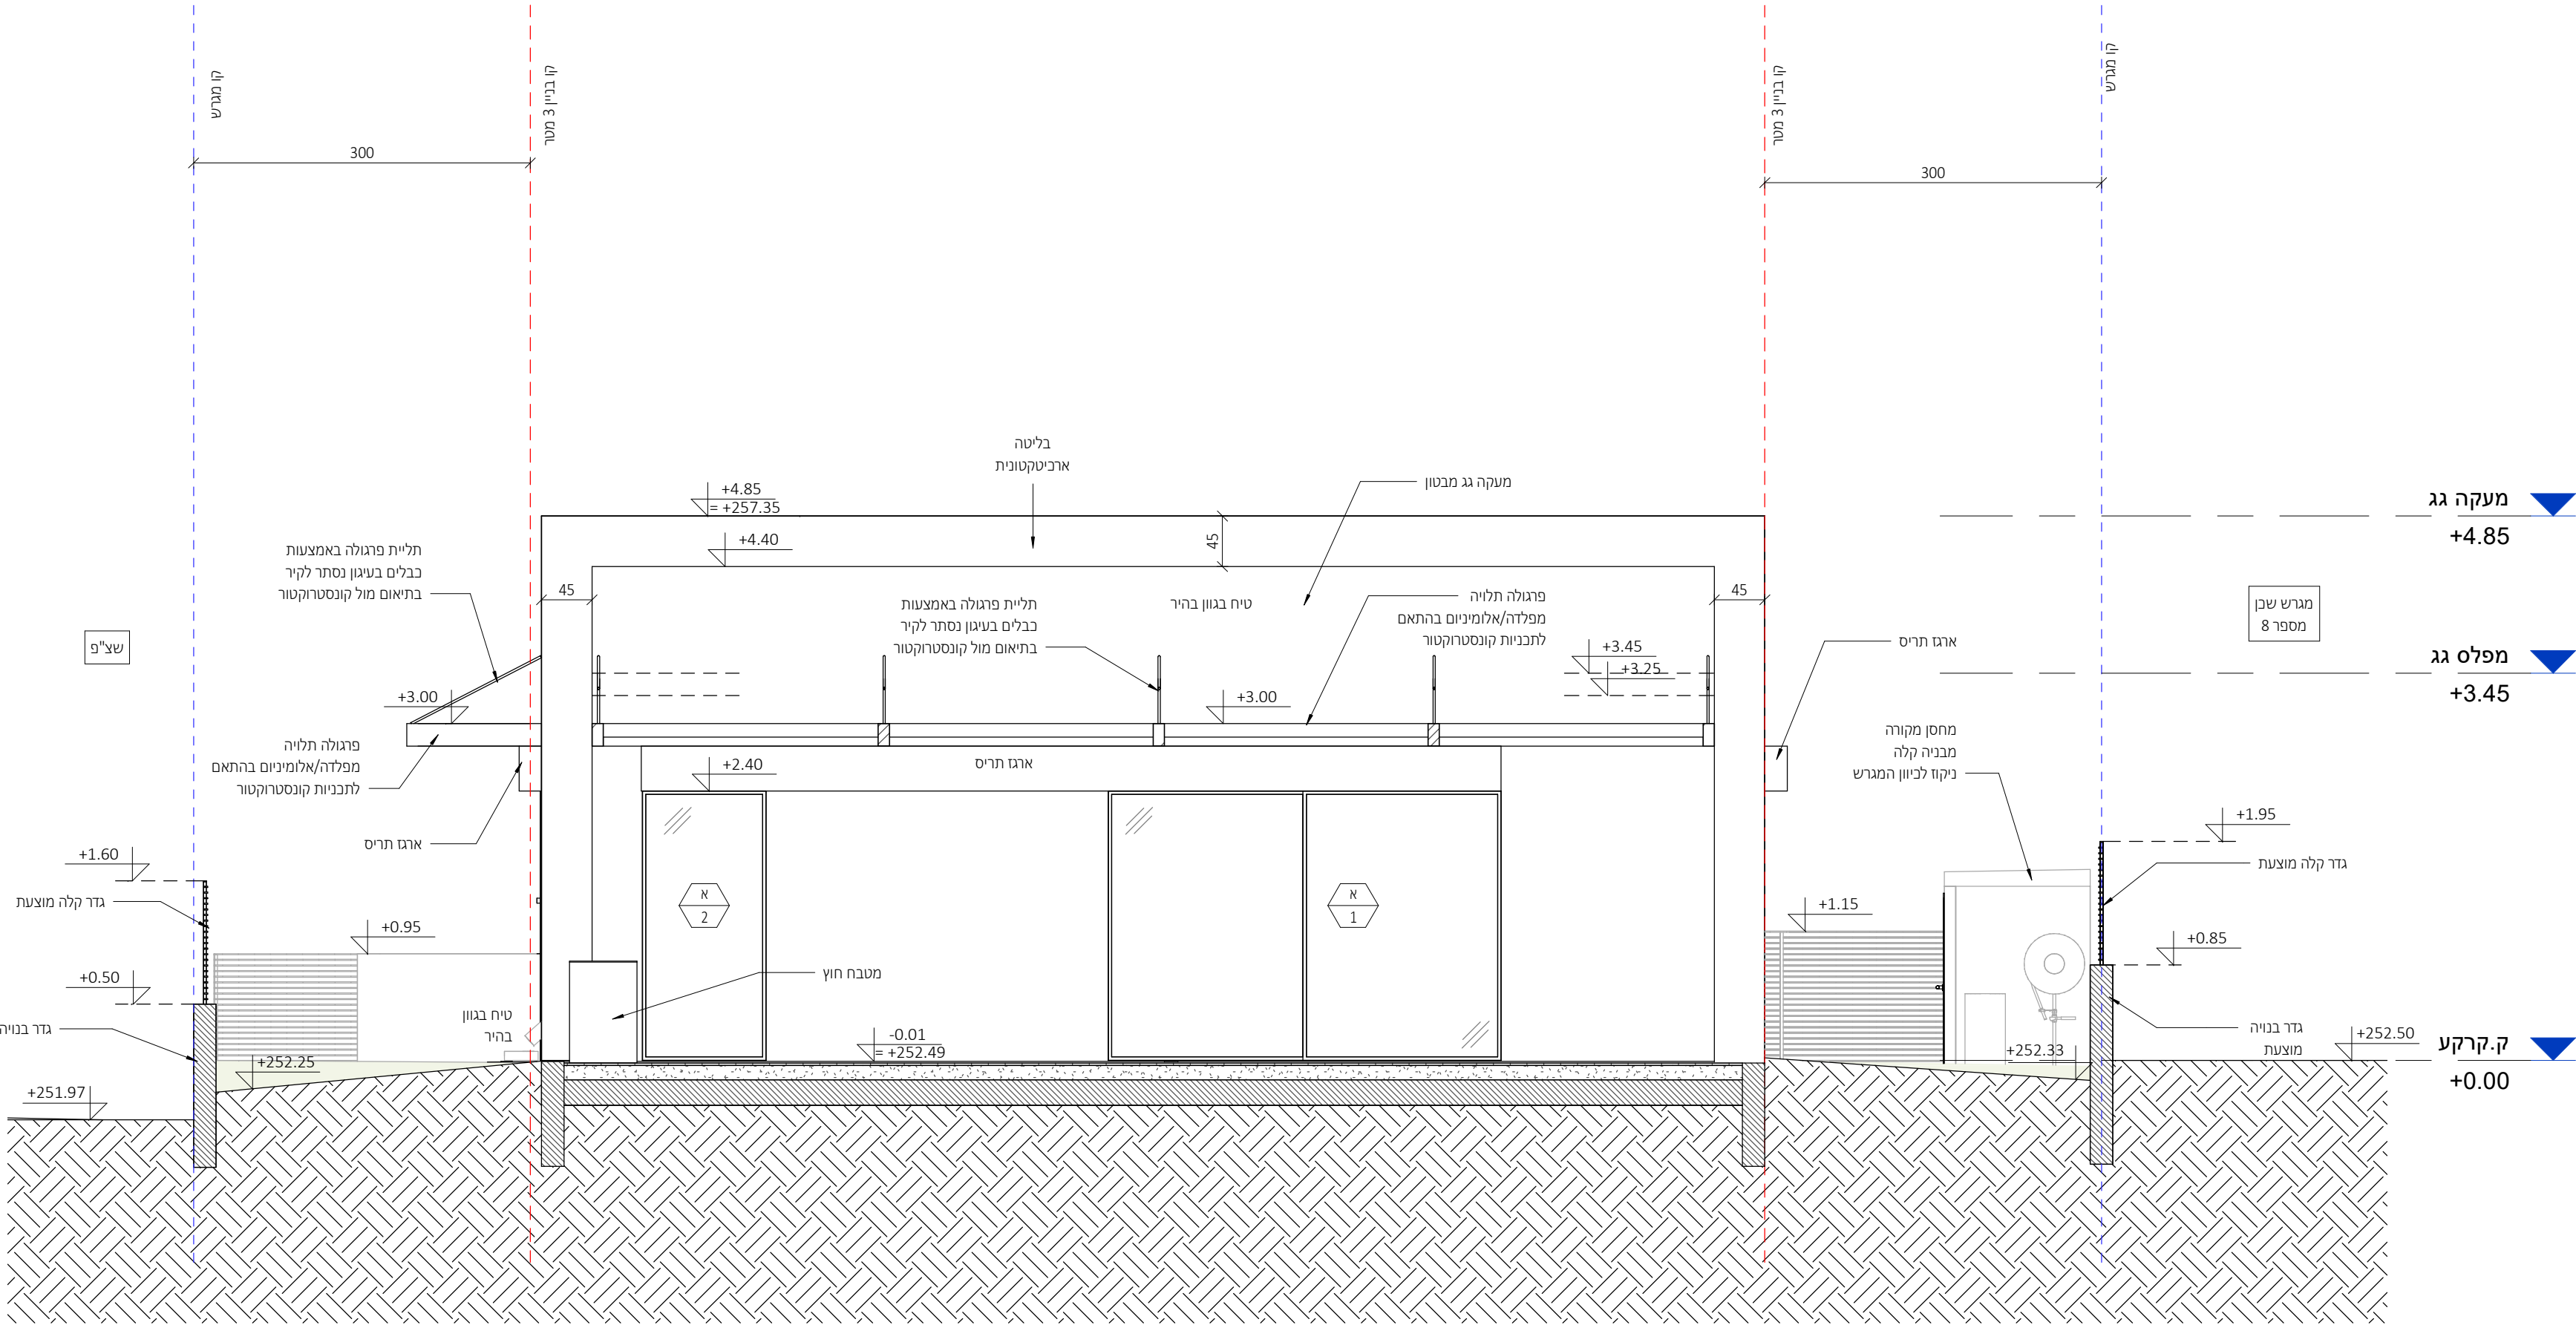

פיתוח נוף עפ"י תוכניות  
יועץ נוף ראה פירוט בנפרד

חזית דרומית

1 : 50

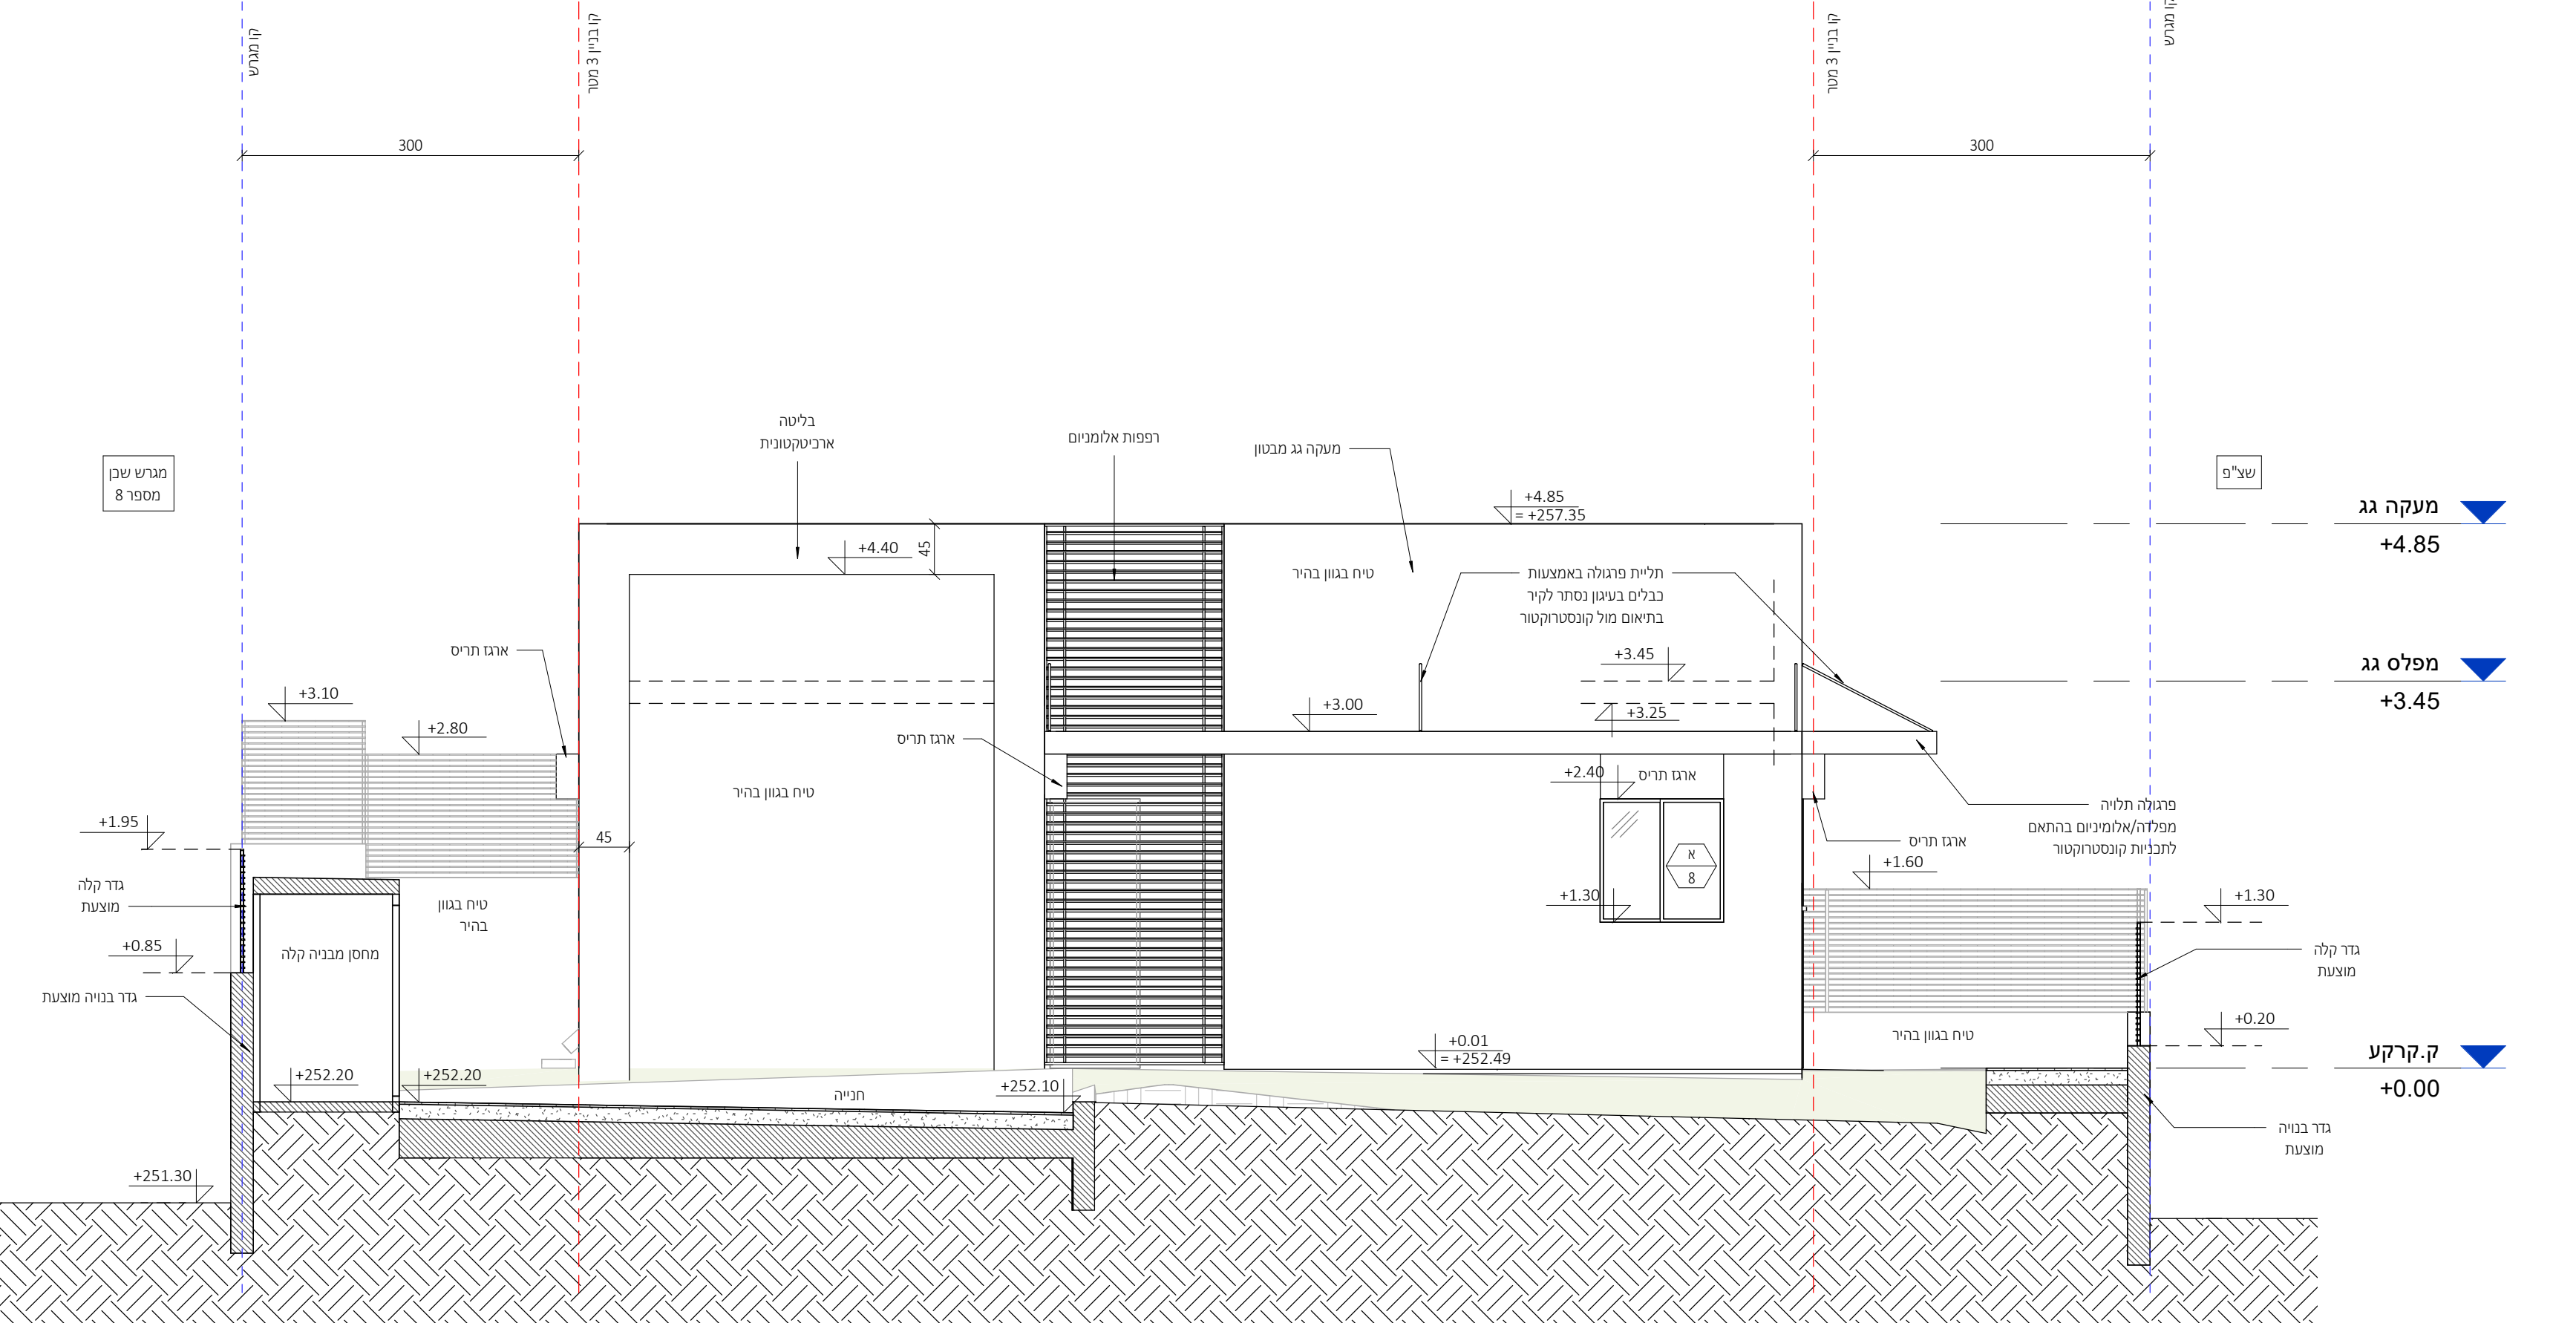

פיתוח נוף עפ"י תוכניות  
יועץ נוף ראה פירוט בנפרד

חזית צפונית

1 : 50


פרטי איטום, בידוד וניקוז עפ"י תכניות יועצים ובאחריות הקבלן

## מתכונים:


|                               |
|-------------------------------|
| ניהול פרויקט                  |
| מהיסוד - בן סלומון            |
| פיקוח                         |
| מהיסוד - בן סלומון            |
| קונסטרוקציה                   |
| ערן שילר                      |
| מיזוג אוויר                   |
| אייל ארז מהנדסים ויועצים בע"מ |
| אינסטלציה                     |
| איתן אלמסי                    |
| חשמל                          |
| איתן בסיס                     |
| אלומיניום                     |
| נוף                           |
| נתי בלוקא                     |
| חשמל חכם                      |
| חימום תת רצפתי                |
| איטום                         |
| צבי טל                        |
| אקוסטיקה                      |
| מעליות                        |
| קרקע וביסוס                   |
| דיה הנדסת קרקע וביסוס         |
| רישוי                         |

[illegible]

זקרא קירות:

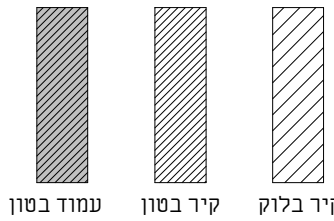[illegible]


## אדריכלות
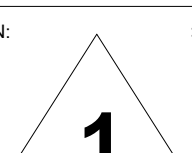
|                   |           |                                                                                     |
|-------------------|-----------|-------------------------------------------------------------------------------------|
| CLIENT NAME:      | המחלקה    |                                                                                     |
| קבוצת רכישה נופיה |           |                                                                                     |
| PROJECT NAME:     | הפרויקט   |                                                                                     |
| נופיה - מגרש 9    |           |                                                                                     |
| DRAWING NAME:     | התוכנית   |                                                                                     |
| חזיתות 2          |           |                                                                                     |
| SHEET NUMBER:     | הפרק 10   |                                                                                     |
| A3-2-201          |           |                                                                                     |
| SCALE:            | קנה מידה: | EDITION:                                                                            |
| 1 : 50            |           | הדורה:                                                                              |
| STATUS:           | סטטוס     |  |
| למכר              |           |                                                                                     |
|                   | נבדק ע"י: | דוסס ע"י:                                                                           |
| DATE:             | 11.08.25  |                                                                                     |
|                   | חידוש:    |                                                                                     |

NeumanHaynerArchitects


וימן חיינר אדריכלים  
מורד ההדרים 2, בית חירות  
טל 09-9545842

פיתוח נוף עפ"י תוכניות  
ועץ נוף ראה פירוט בנפרד

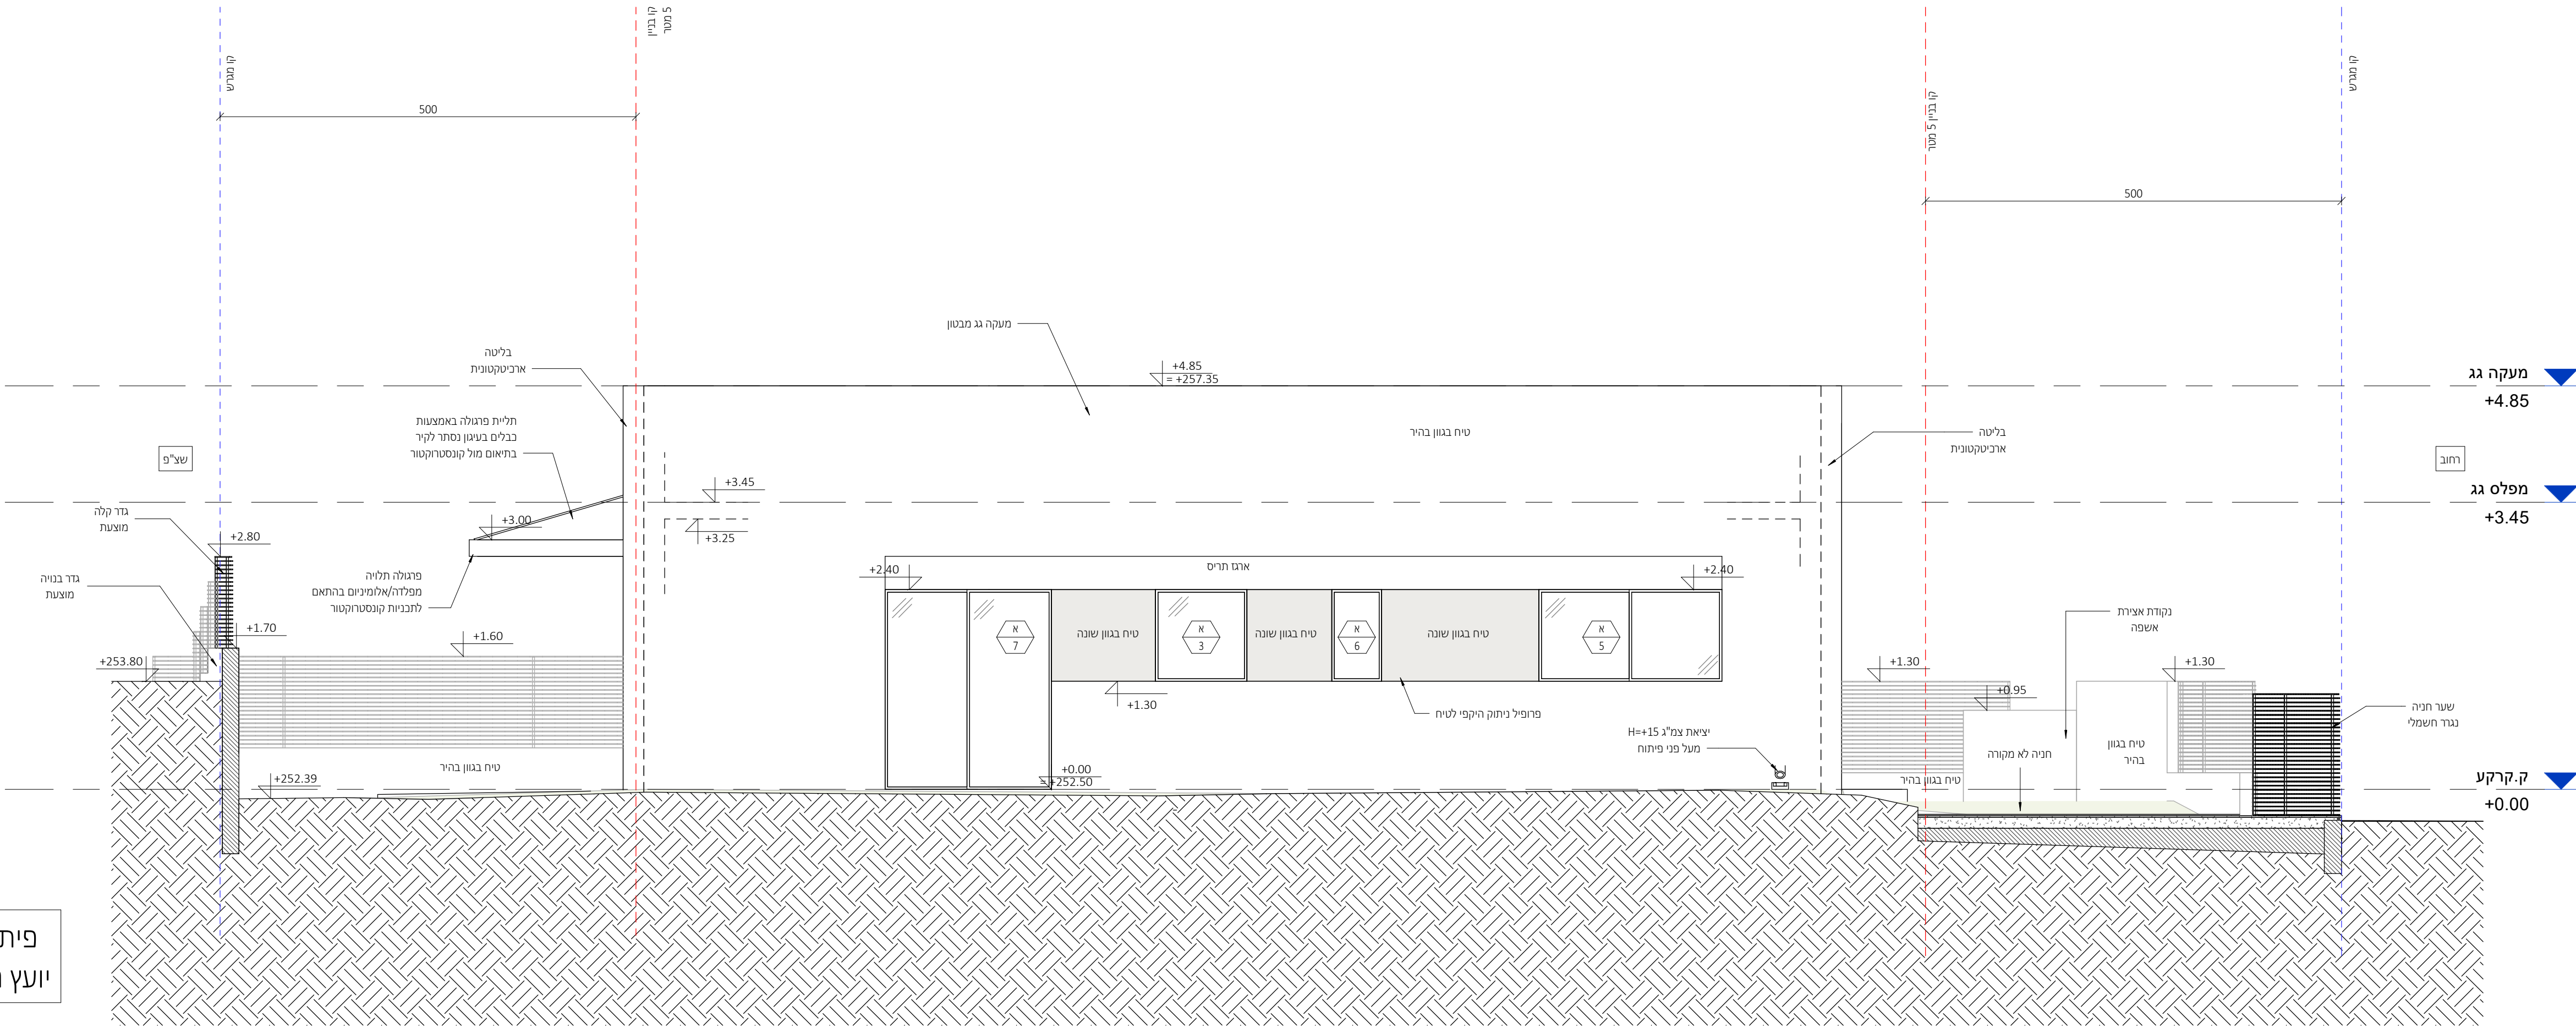

## חזית מזרחית

1 : 50

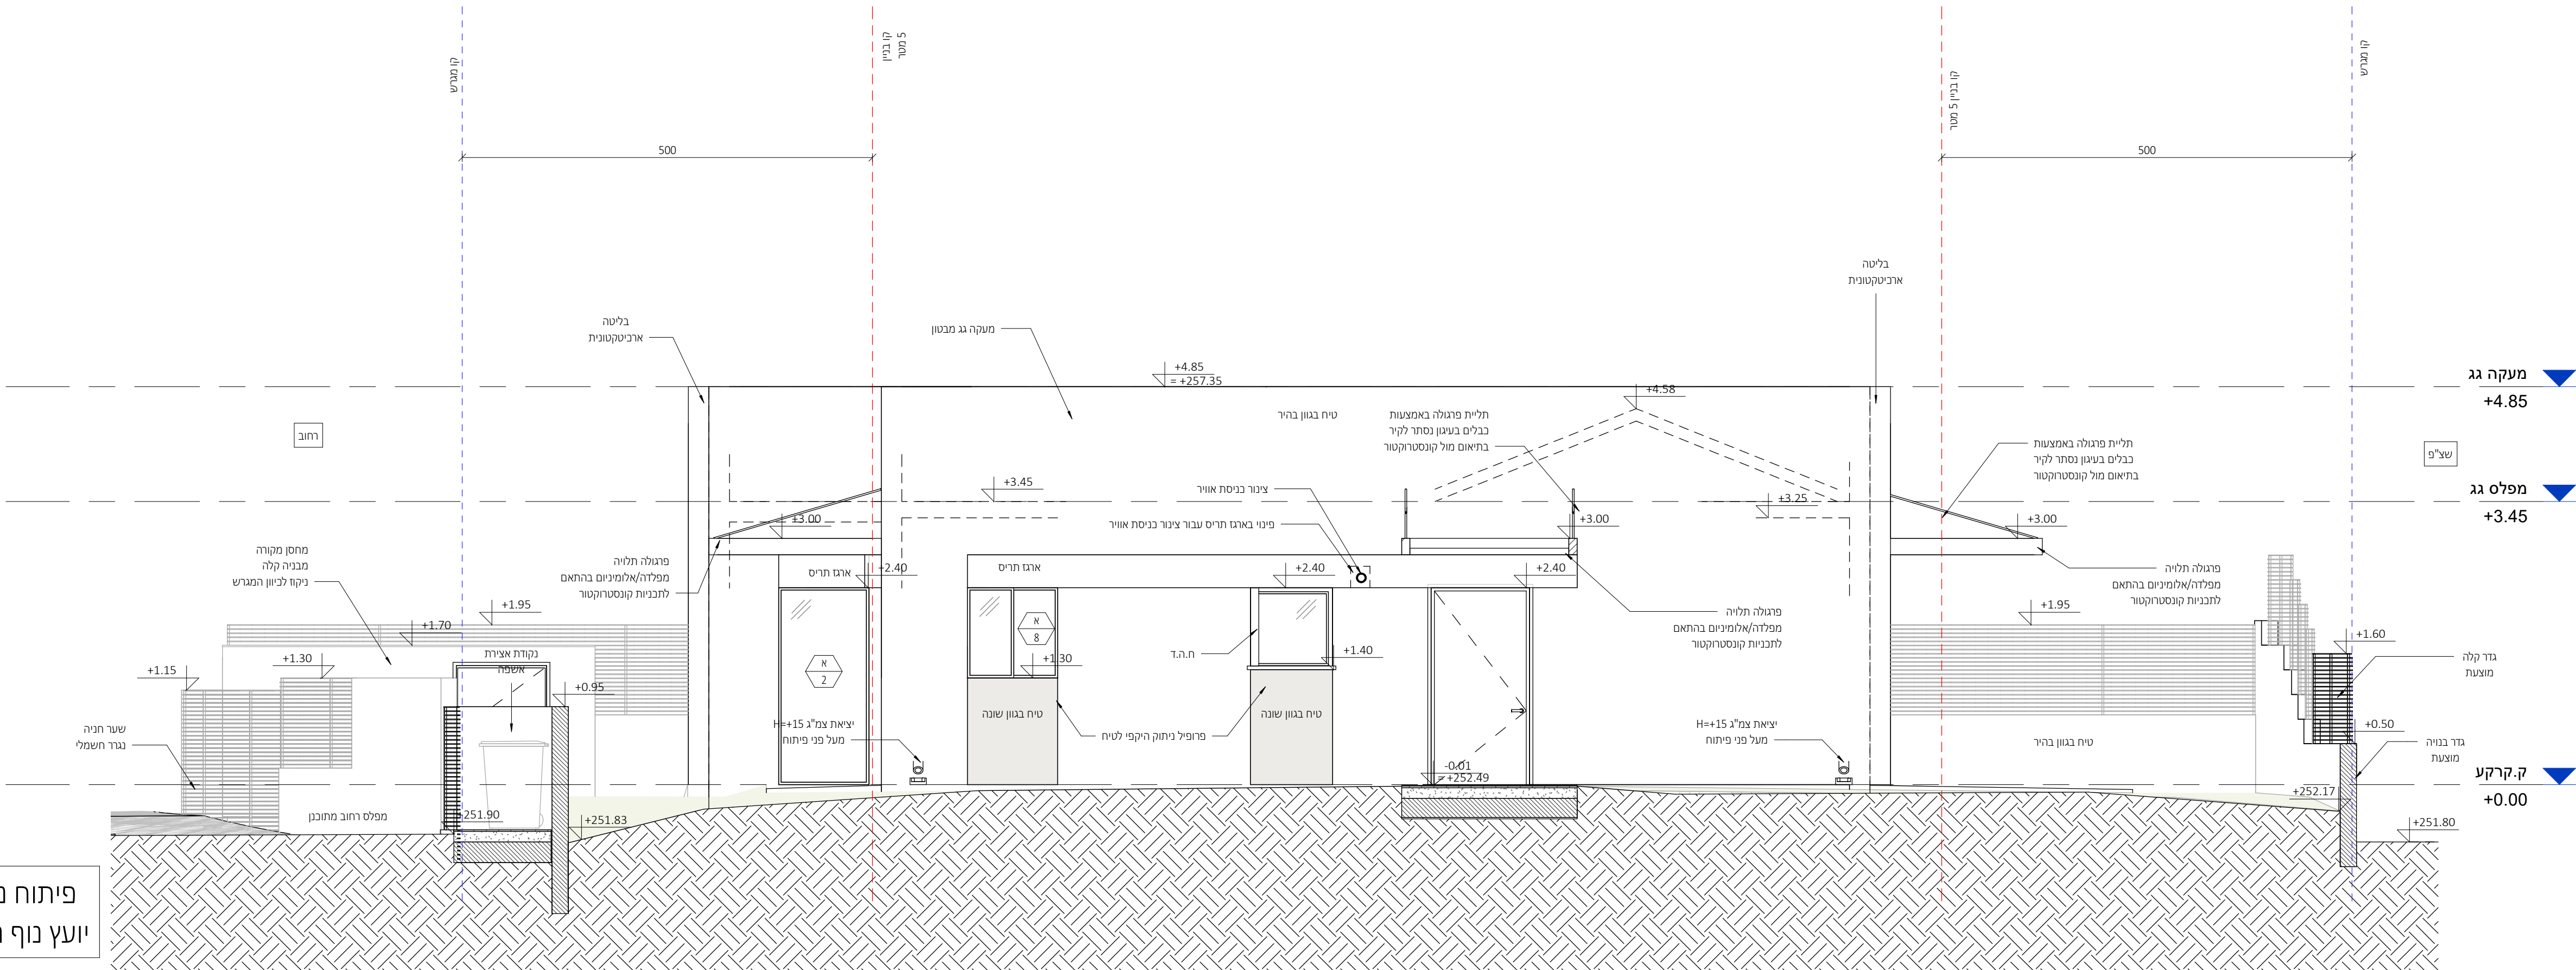

## חזית מערבית

1 : 50


פרטי איטום, בידוד וניקוז עפ"י תכניות יועצים ובאחריות הקבלן

## מתכונים:

|                               |
|-------------------------------|
| ניהול פרויקט                  |
| מהיסוד - בן סלומון            |
| פיקוח                         |
| מהיסוד - בן סלומון            |
| קונסטרוקציה                   |
| ערן שילר                      |
| מיזוג אוויר                   |
| אייל ארז מהנדסים ויועצים בע"מ |
| אינסטלציה                     |
| איתן אלמסי                    |
| חשמל                          |
| איתן בסיס                     |
| אלומיניום                     |
| בופ                           |
| נתי בלוקא                     |
| חשמל חכם                      |
| חימום תת רצפתי                |
| איטום                         |
| צבי טל                        |
| אקוסטיקה                      |
| מעלות                         |
| קרקע וביסוס                   |
| דיה הנדסת קרקע וביסוס         |
| רישוי                         |

[illegible]

מקרא קירות:

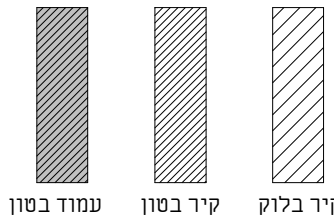[illegible]

# אדריכלות

ש המזמין:

CLIENT NAME:

## קבוצת רכישה נופיה

ש הפרויקט

PROJECT NAME

נופיה - מגרש 9

ס הגליון:

DRAWING NAME

SHEET NUMBER:

SHEET NUMBER

A3-3-100

הדורה:

SCALE:

---

---

[illegible]

|  |
|--|
|  |
|--|


DATE: 11.08.25

NeumanHaynerArchitects


office@nh-arch.com  
www.nh-arch.com

וימן חיינר אדריכלים  
מאור ההדריס 2, בית חירות  
טל 09-9545842

זכויות ייצור / ע"פ הנחיות עו"ד

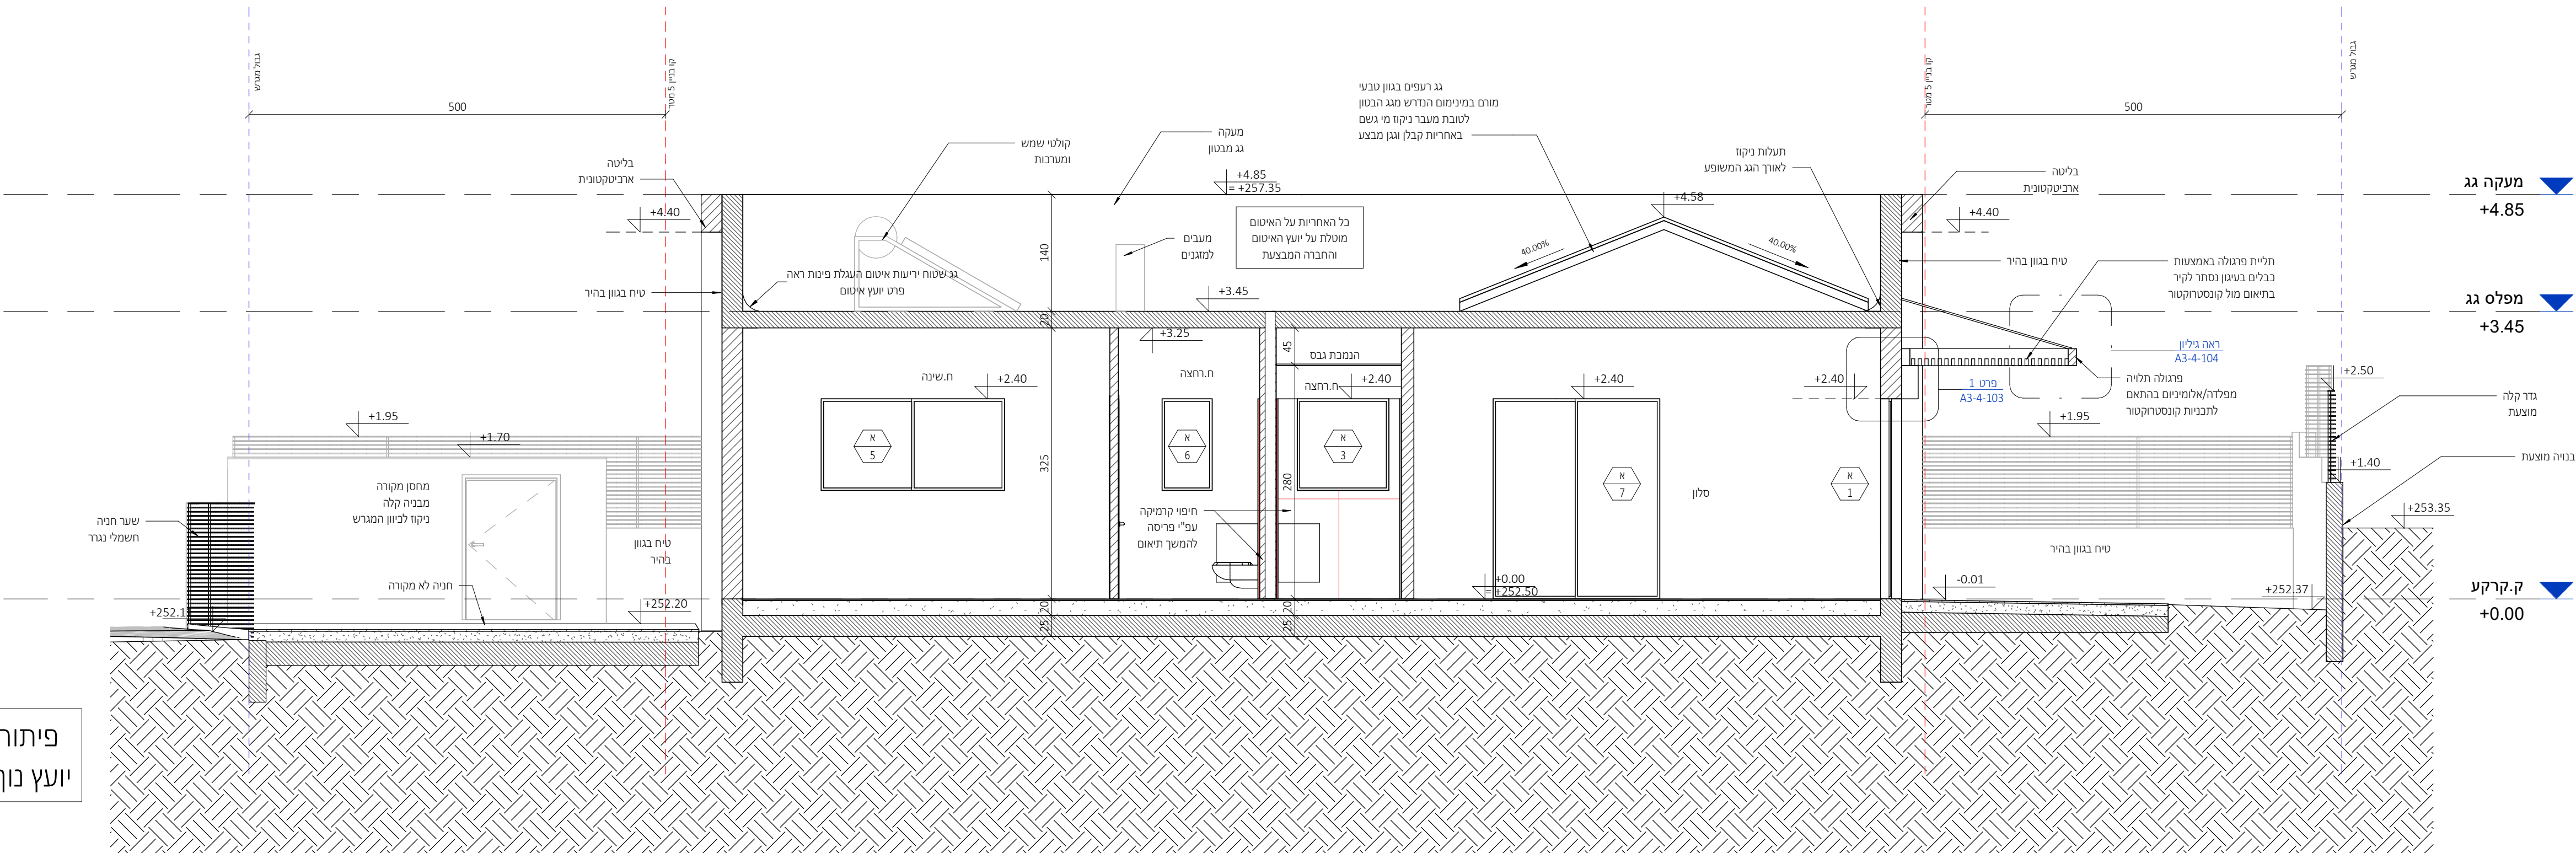

פיתוח נוף עפ"י תוכניות  
עץ נוף ראה פירוט בנפרד

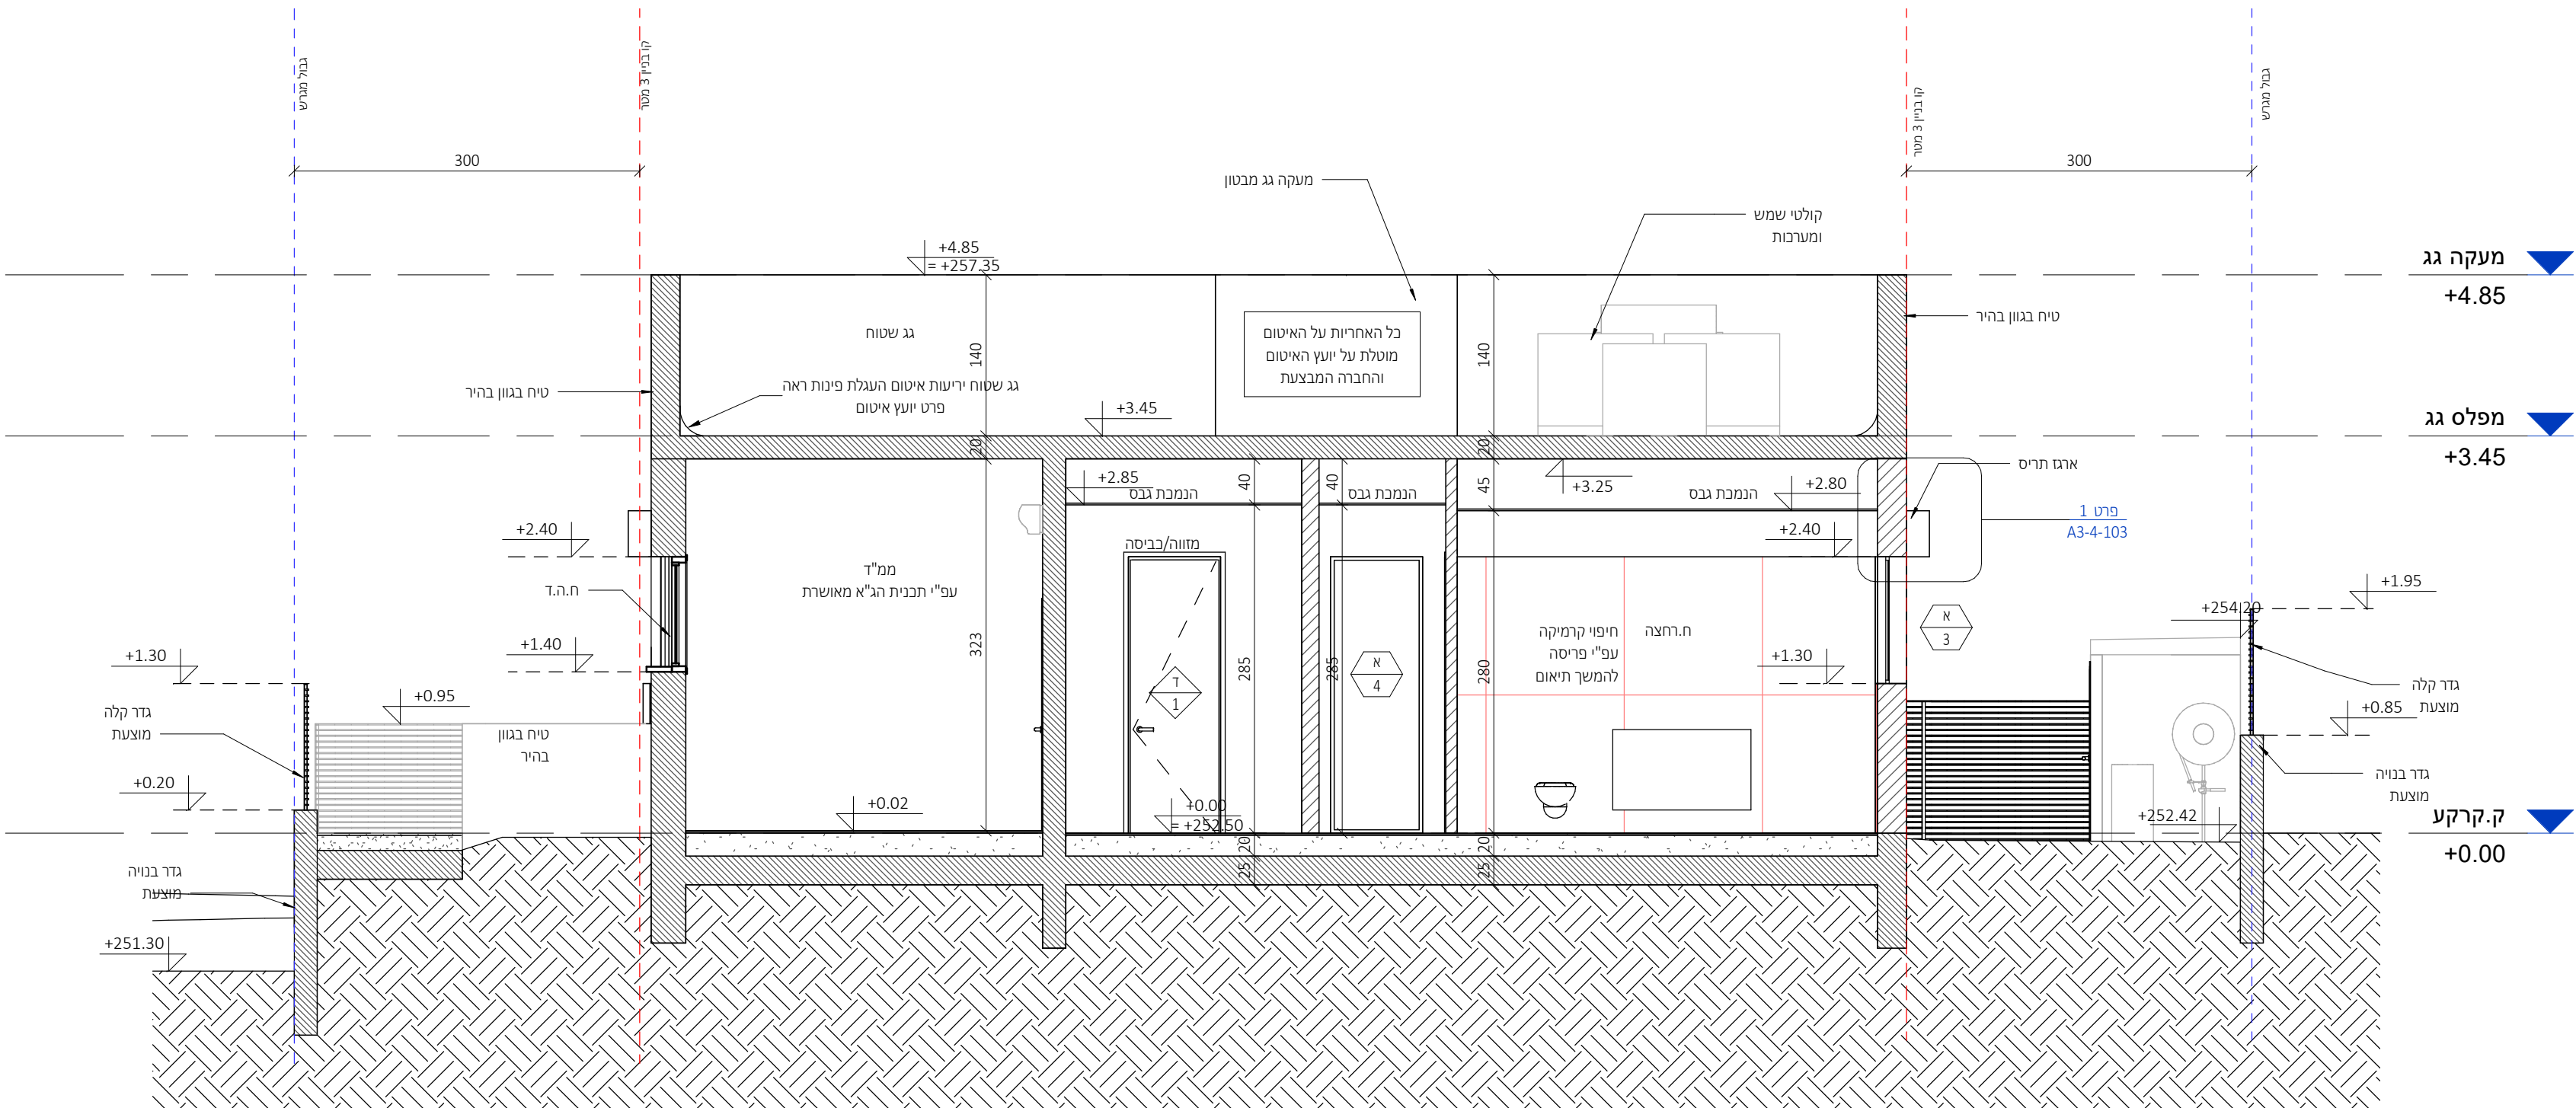

פיתוח נוף עפ"י תוכניות  
יועץ נוף ראה פירוט בנפרד

## חתך א-א

1 : 50

## חתך ב-ב

1 : 50

|                               |
|-------------------------------|
| ניהול פרויקט                  |
| מהיסוד - בן סלומון            |
| פיקוח                         |
| מהיסוד - בן סלומון            |
| קונסטרוקציה                   |
| ערן שילר                      |
| מיזוג אוויר                   |
| אייל ארז מהנדסים ויועצים בע"מ |
| אינסטלציה                     |
| איתן אלמסי                    |
| חשמל                          |
| איתן בסיס                     |
| אלומיניום                     |
| נוף                           |
| נתי בלוקא                     |
| חשמל חכם                      |
| חימום תת רצפתי                |
| איטום                         |
| צבי טל                        |
| אקוסטיקה                      |
| מעליות                        |
| קרקע וביסוס                   |
| דיה הנדסת קרקע וביסוס         |
| רישוי                         |

[illegible][illegible]

CLIENT NAME: \_\_\_\_\_ שם המזמין:

## PROJECT NAME: \_\_\_\_\_ שם הפרויקט: \_\_\_\_\_

DRAWING NAME: ס הגליון:

SHEET NUMBER: 190 גליון:

|           |          |       |   |
|-----------|----------|-------|---|
| קנה מידה: | EDITION: | דפוס: | ▲ |
|-----------|----------|-------|---|

STATUS: 01000

|           |           |
|-----------|-----------|
| דטסט ע"י: | נבדק ע"י: |
|-----------|-----------|


DATE: 11.08.25




NeumanHaynerArchitects

office@nh-arch.com


זכויות יוצר / ע"פ הנחיות עו"ד

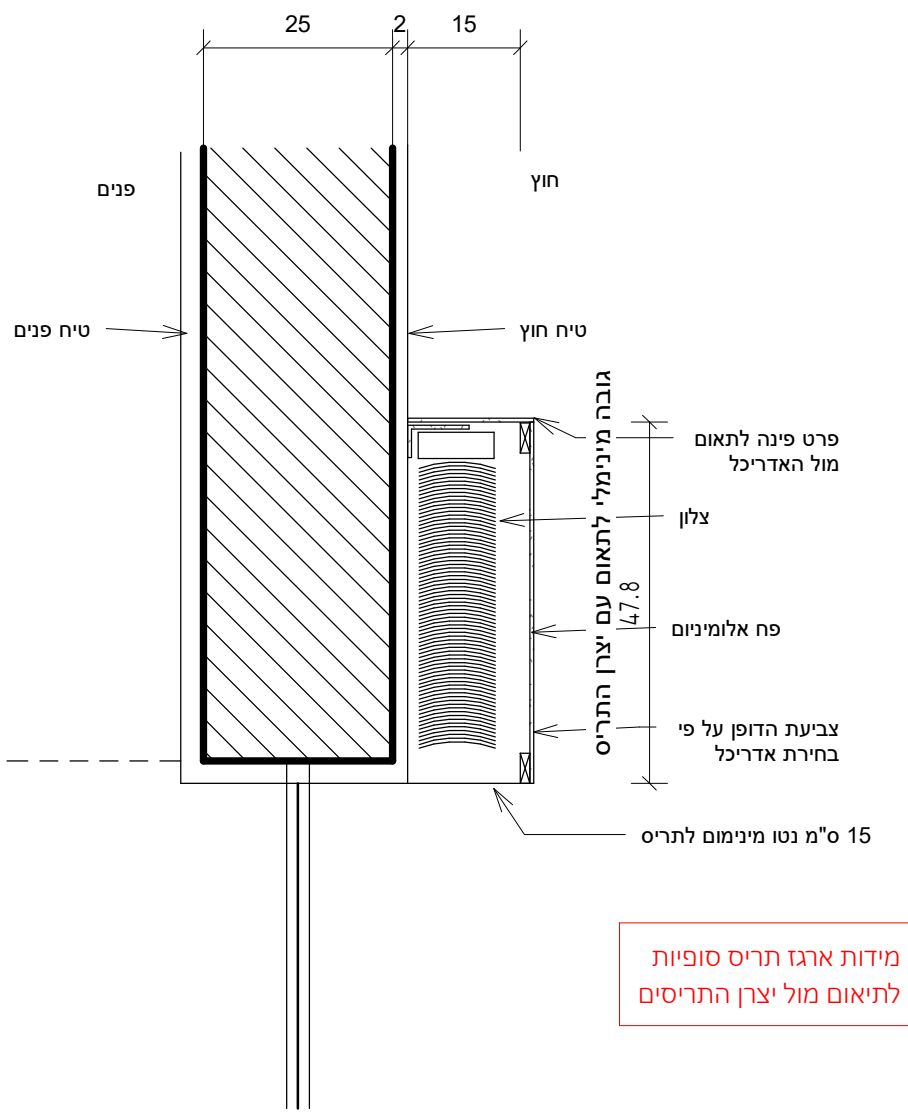


1 : 10

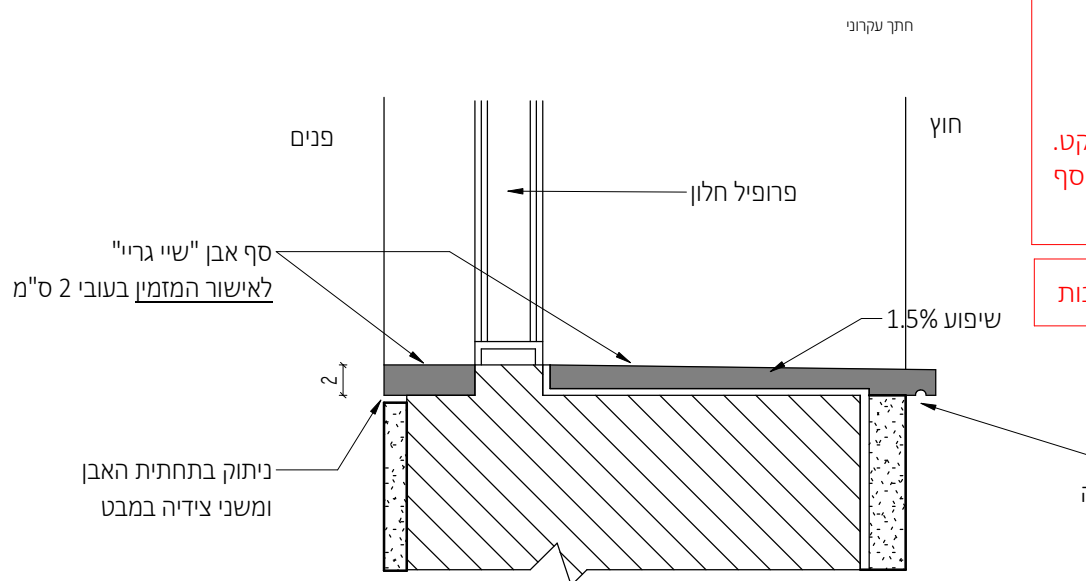


1 : 5

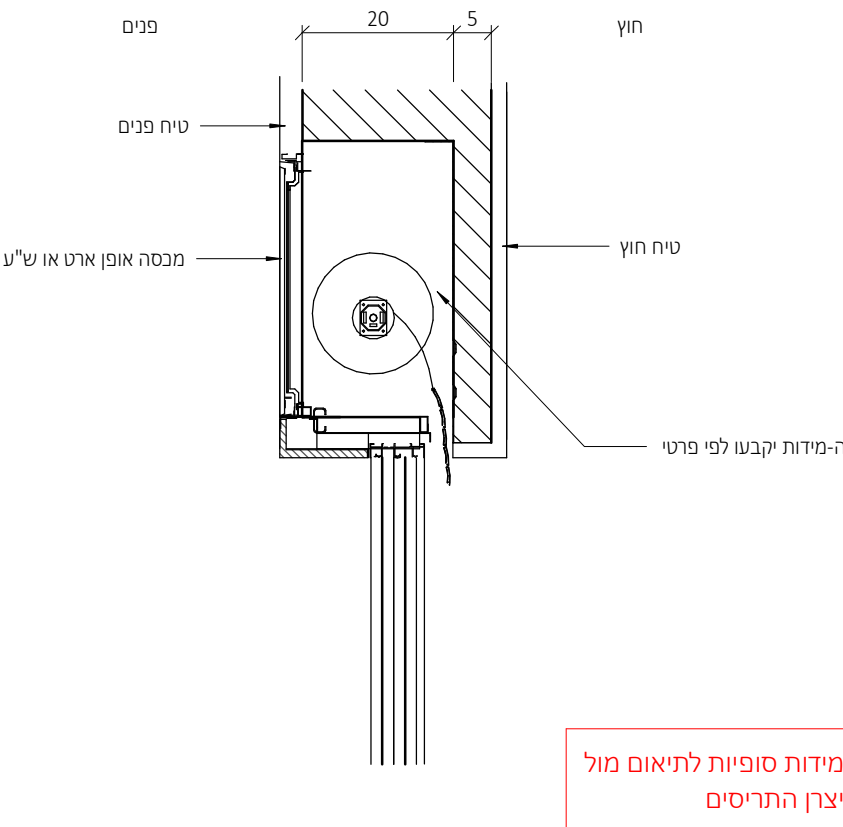


1 : 10

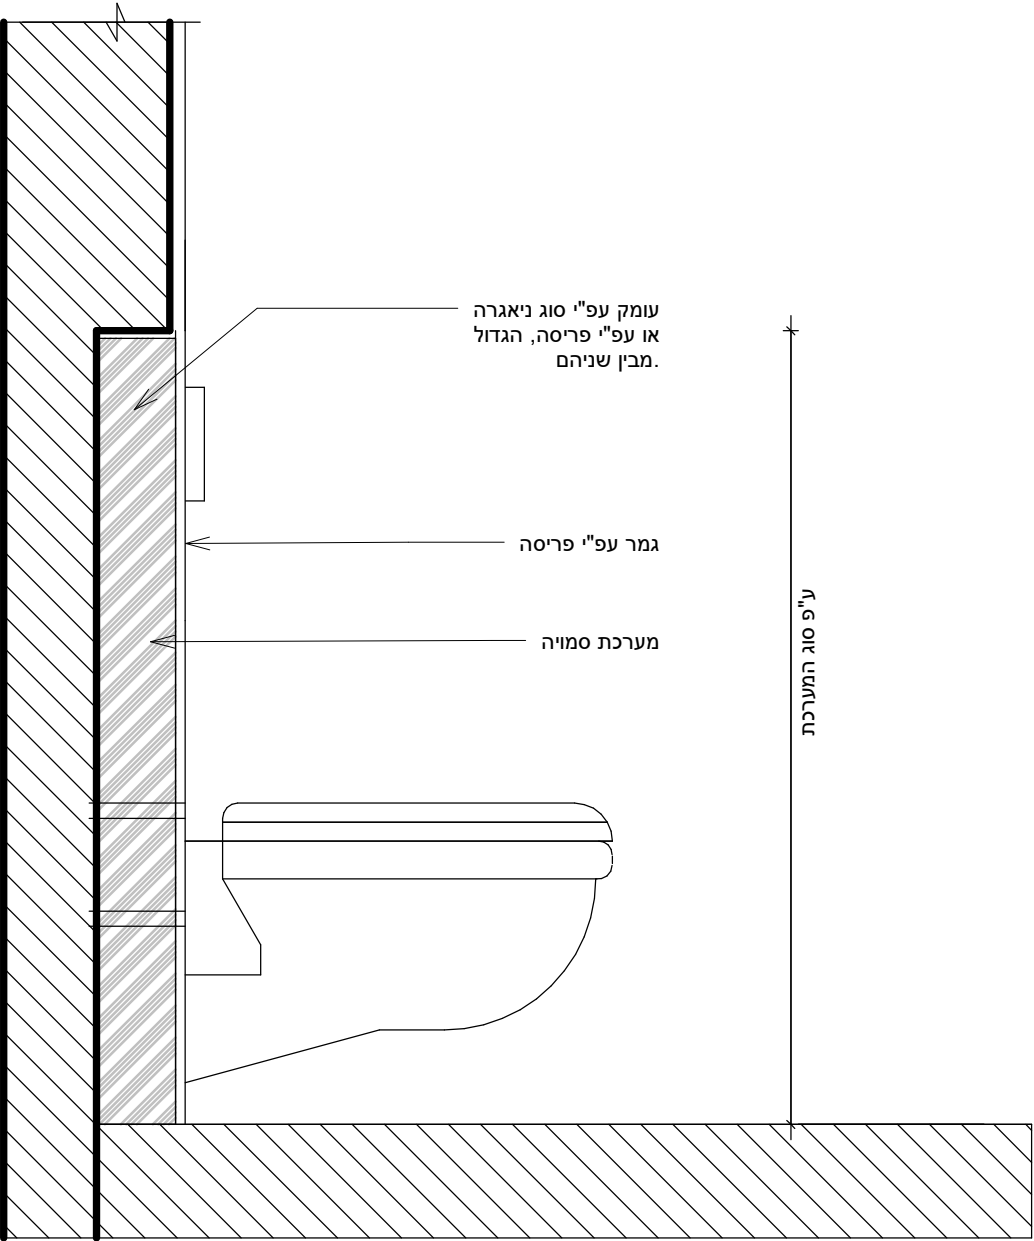

1 : 10

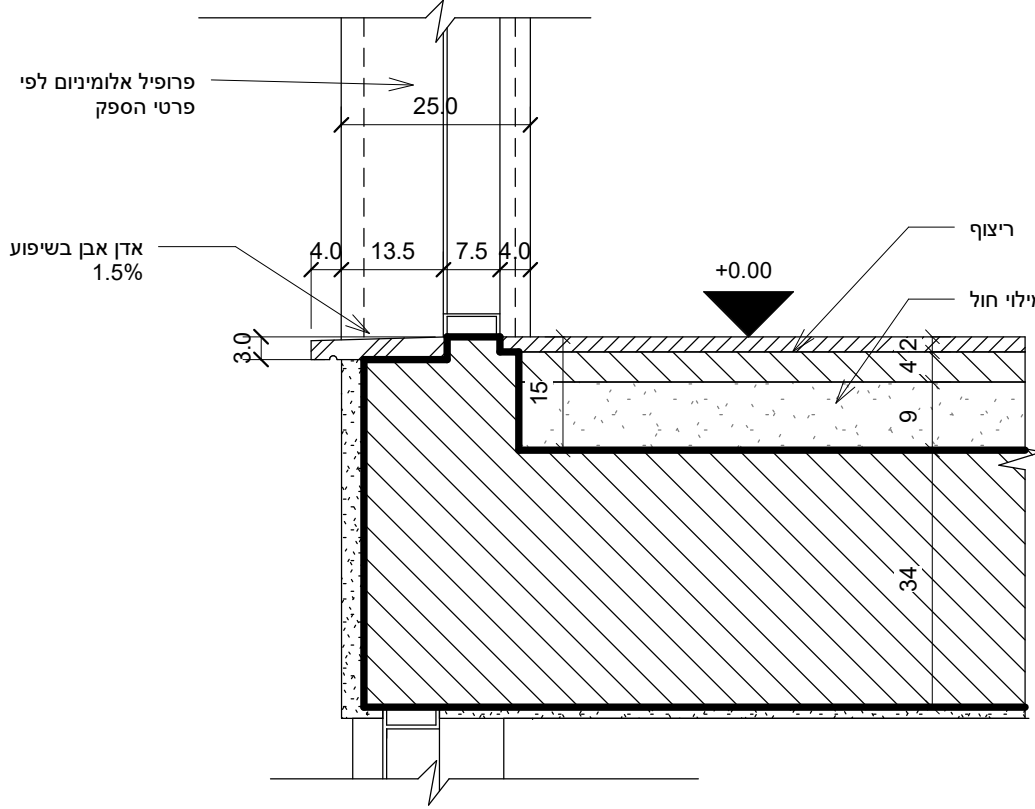

1 : 10

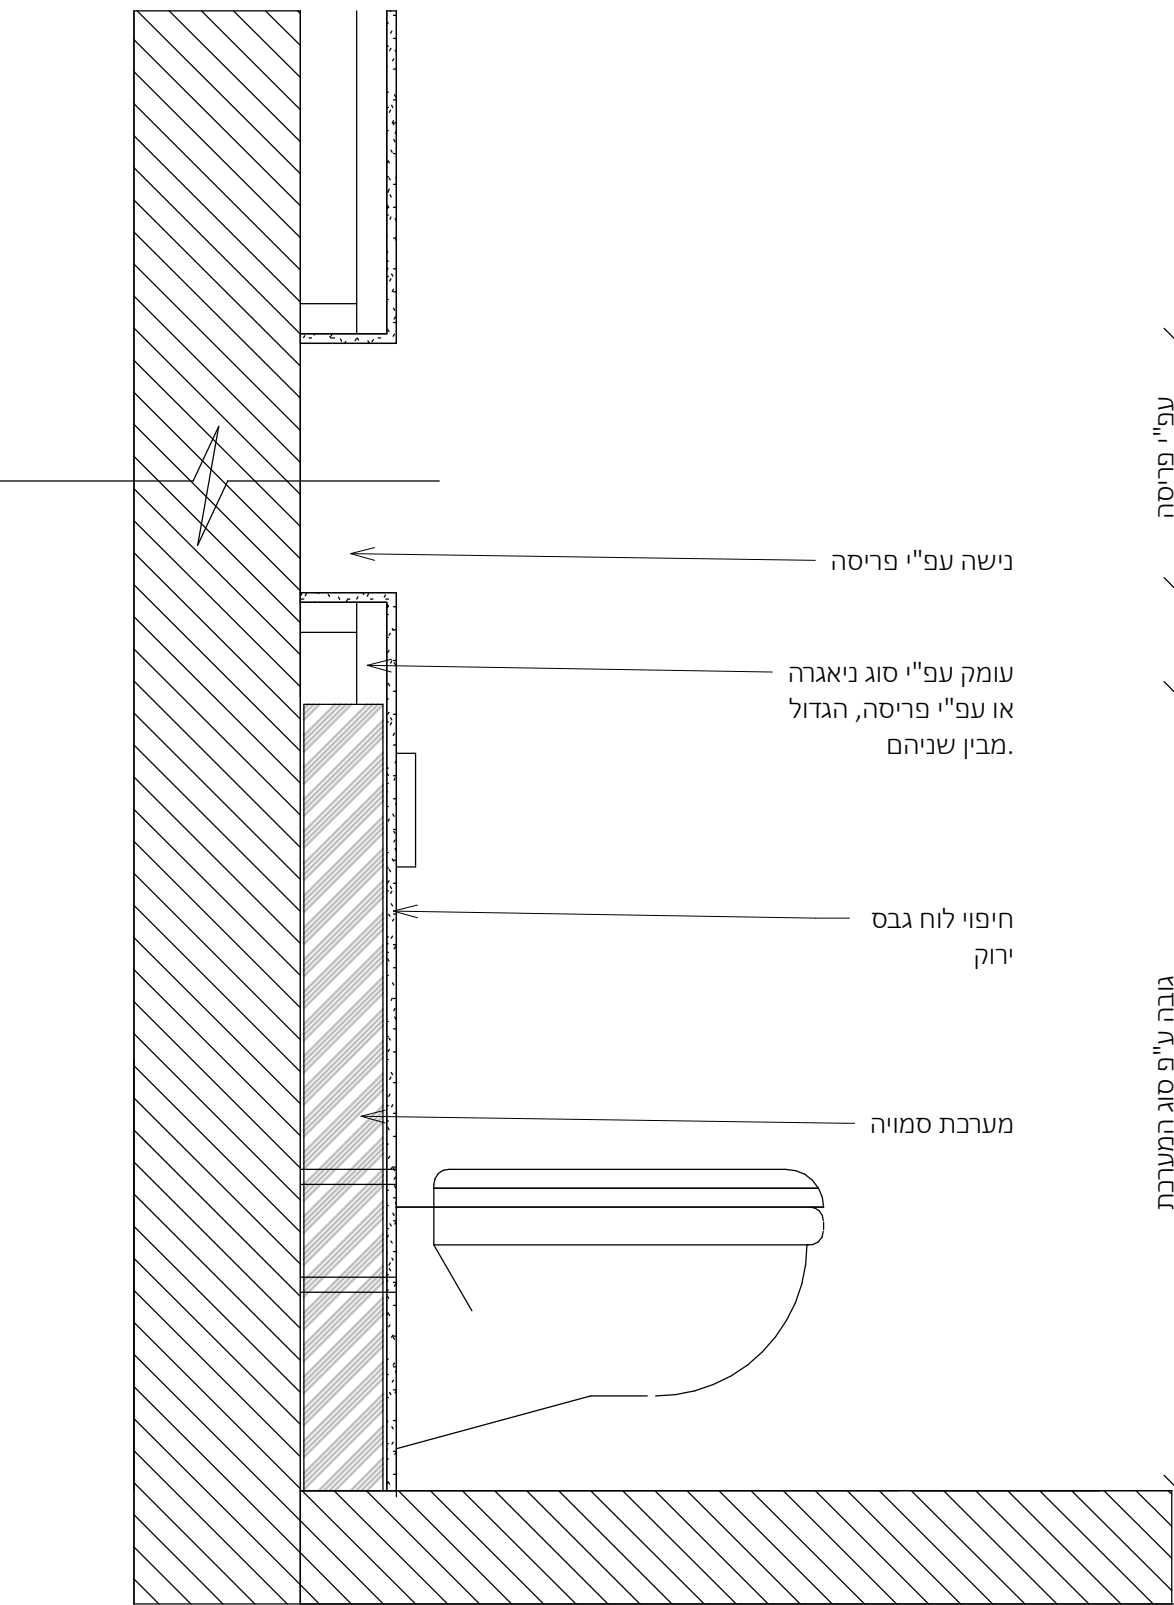

1 : 10

פרטי האיטום באחריות יועץ האיטום  
ראה חוברת פרטי איטום מצורפת


# להמשך תיאום

פרגולת אלומיניום




תמונה להמחשה בלבד

להמשך תיאום

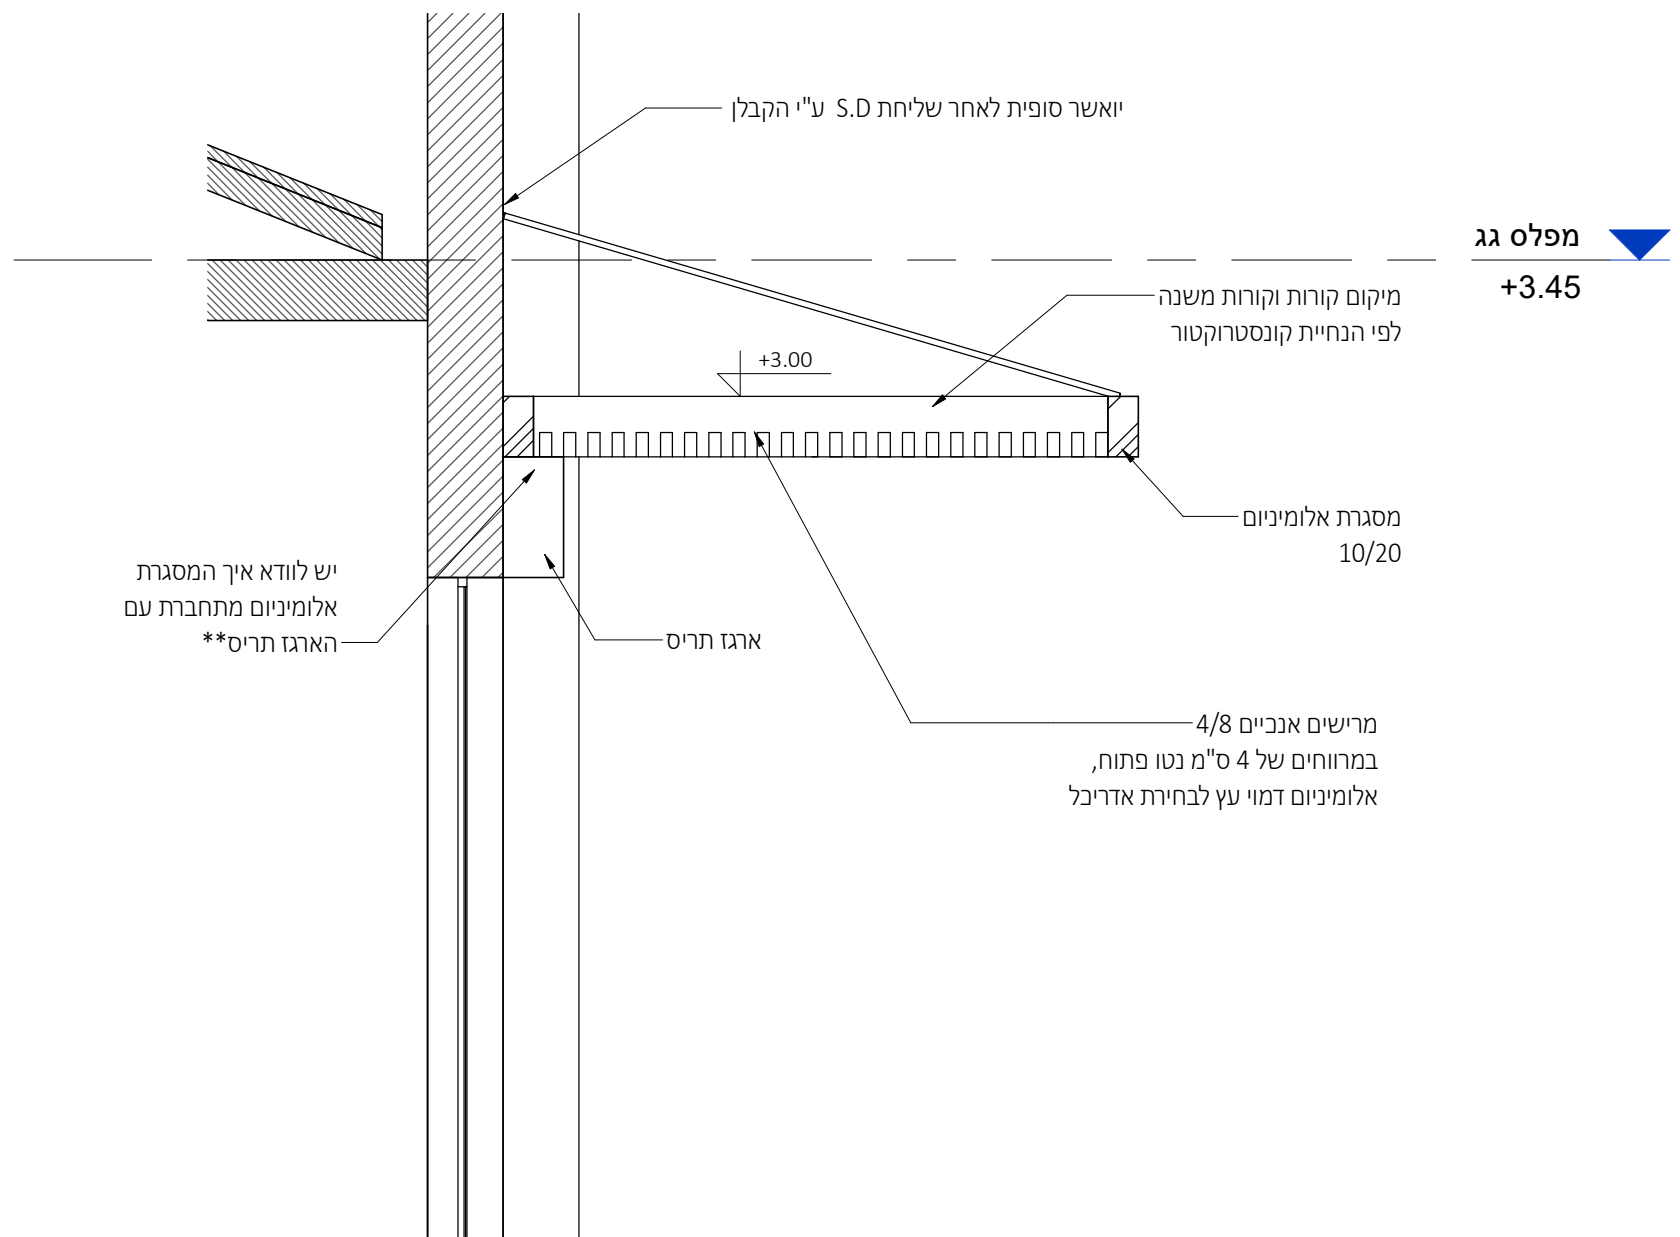


Section 11

1 : 25

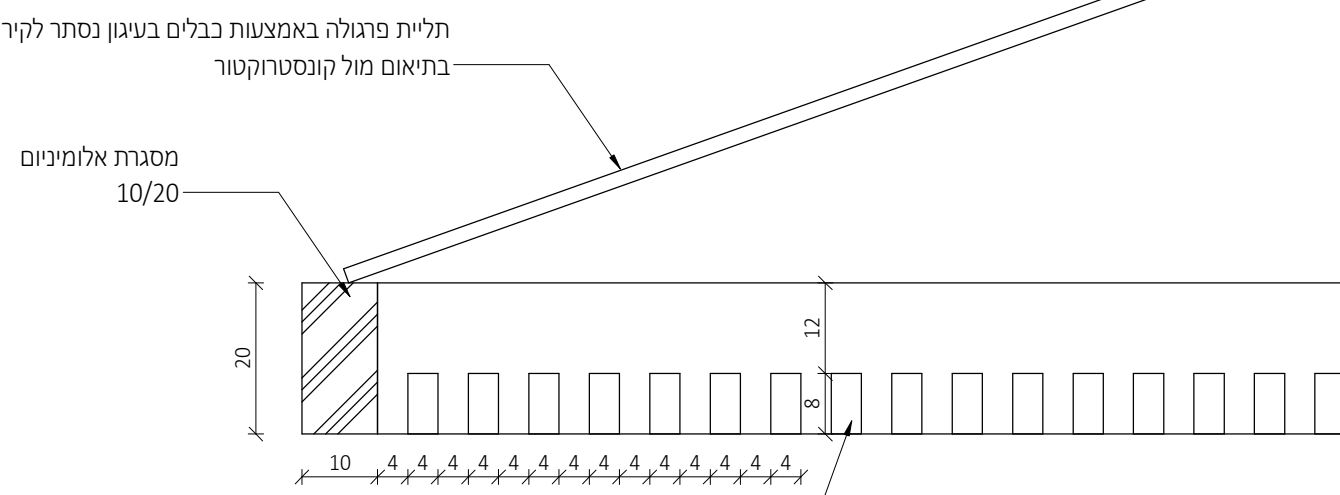



פרגולה - חתך רוחב

1 : 10

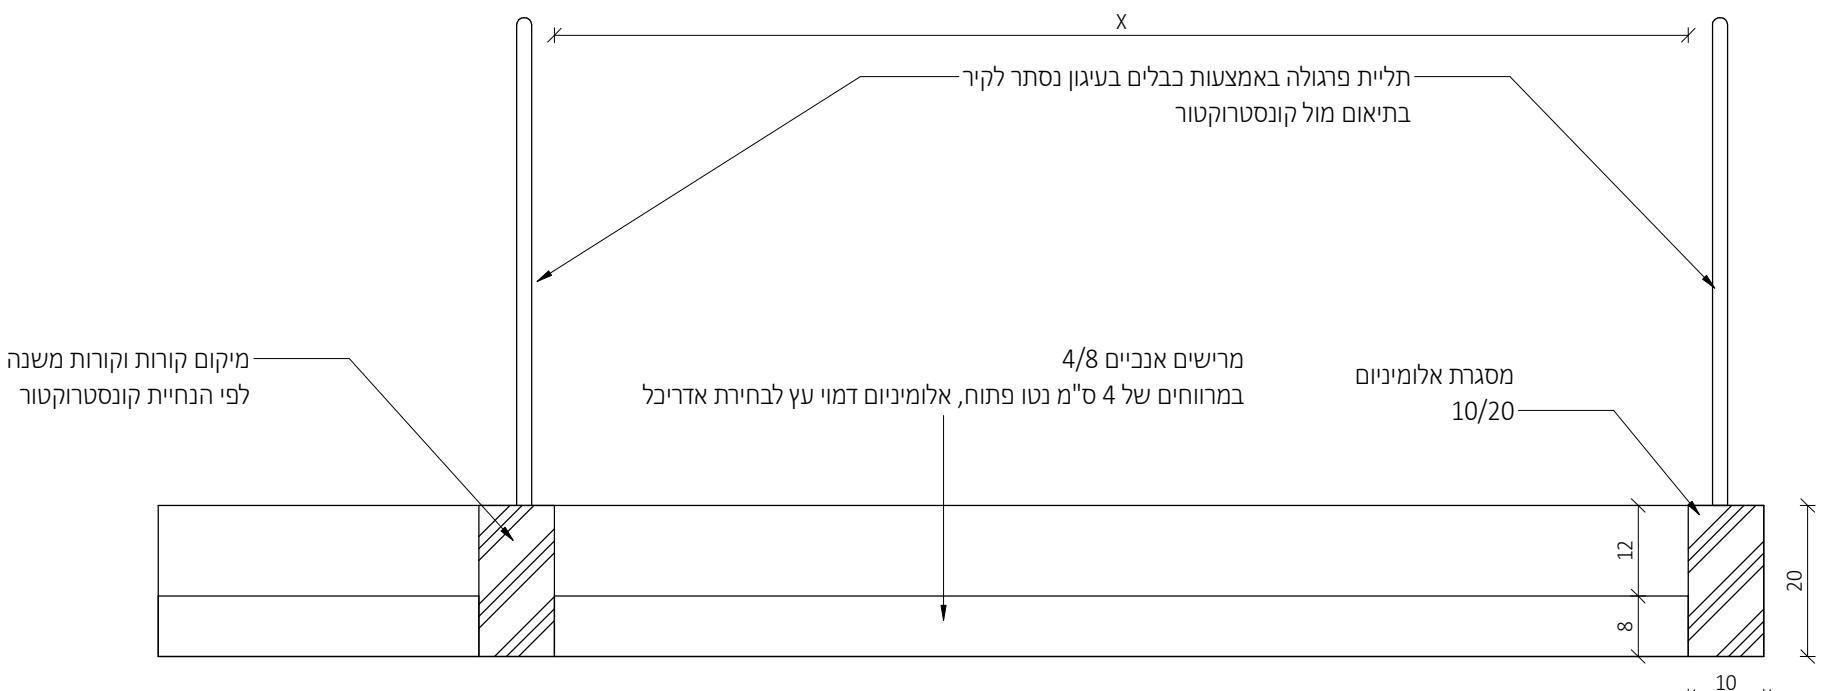

פרגולה - חתך אורך

1 : 10

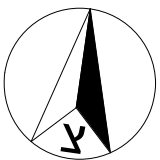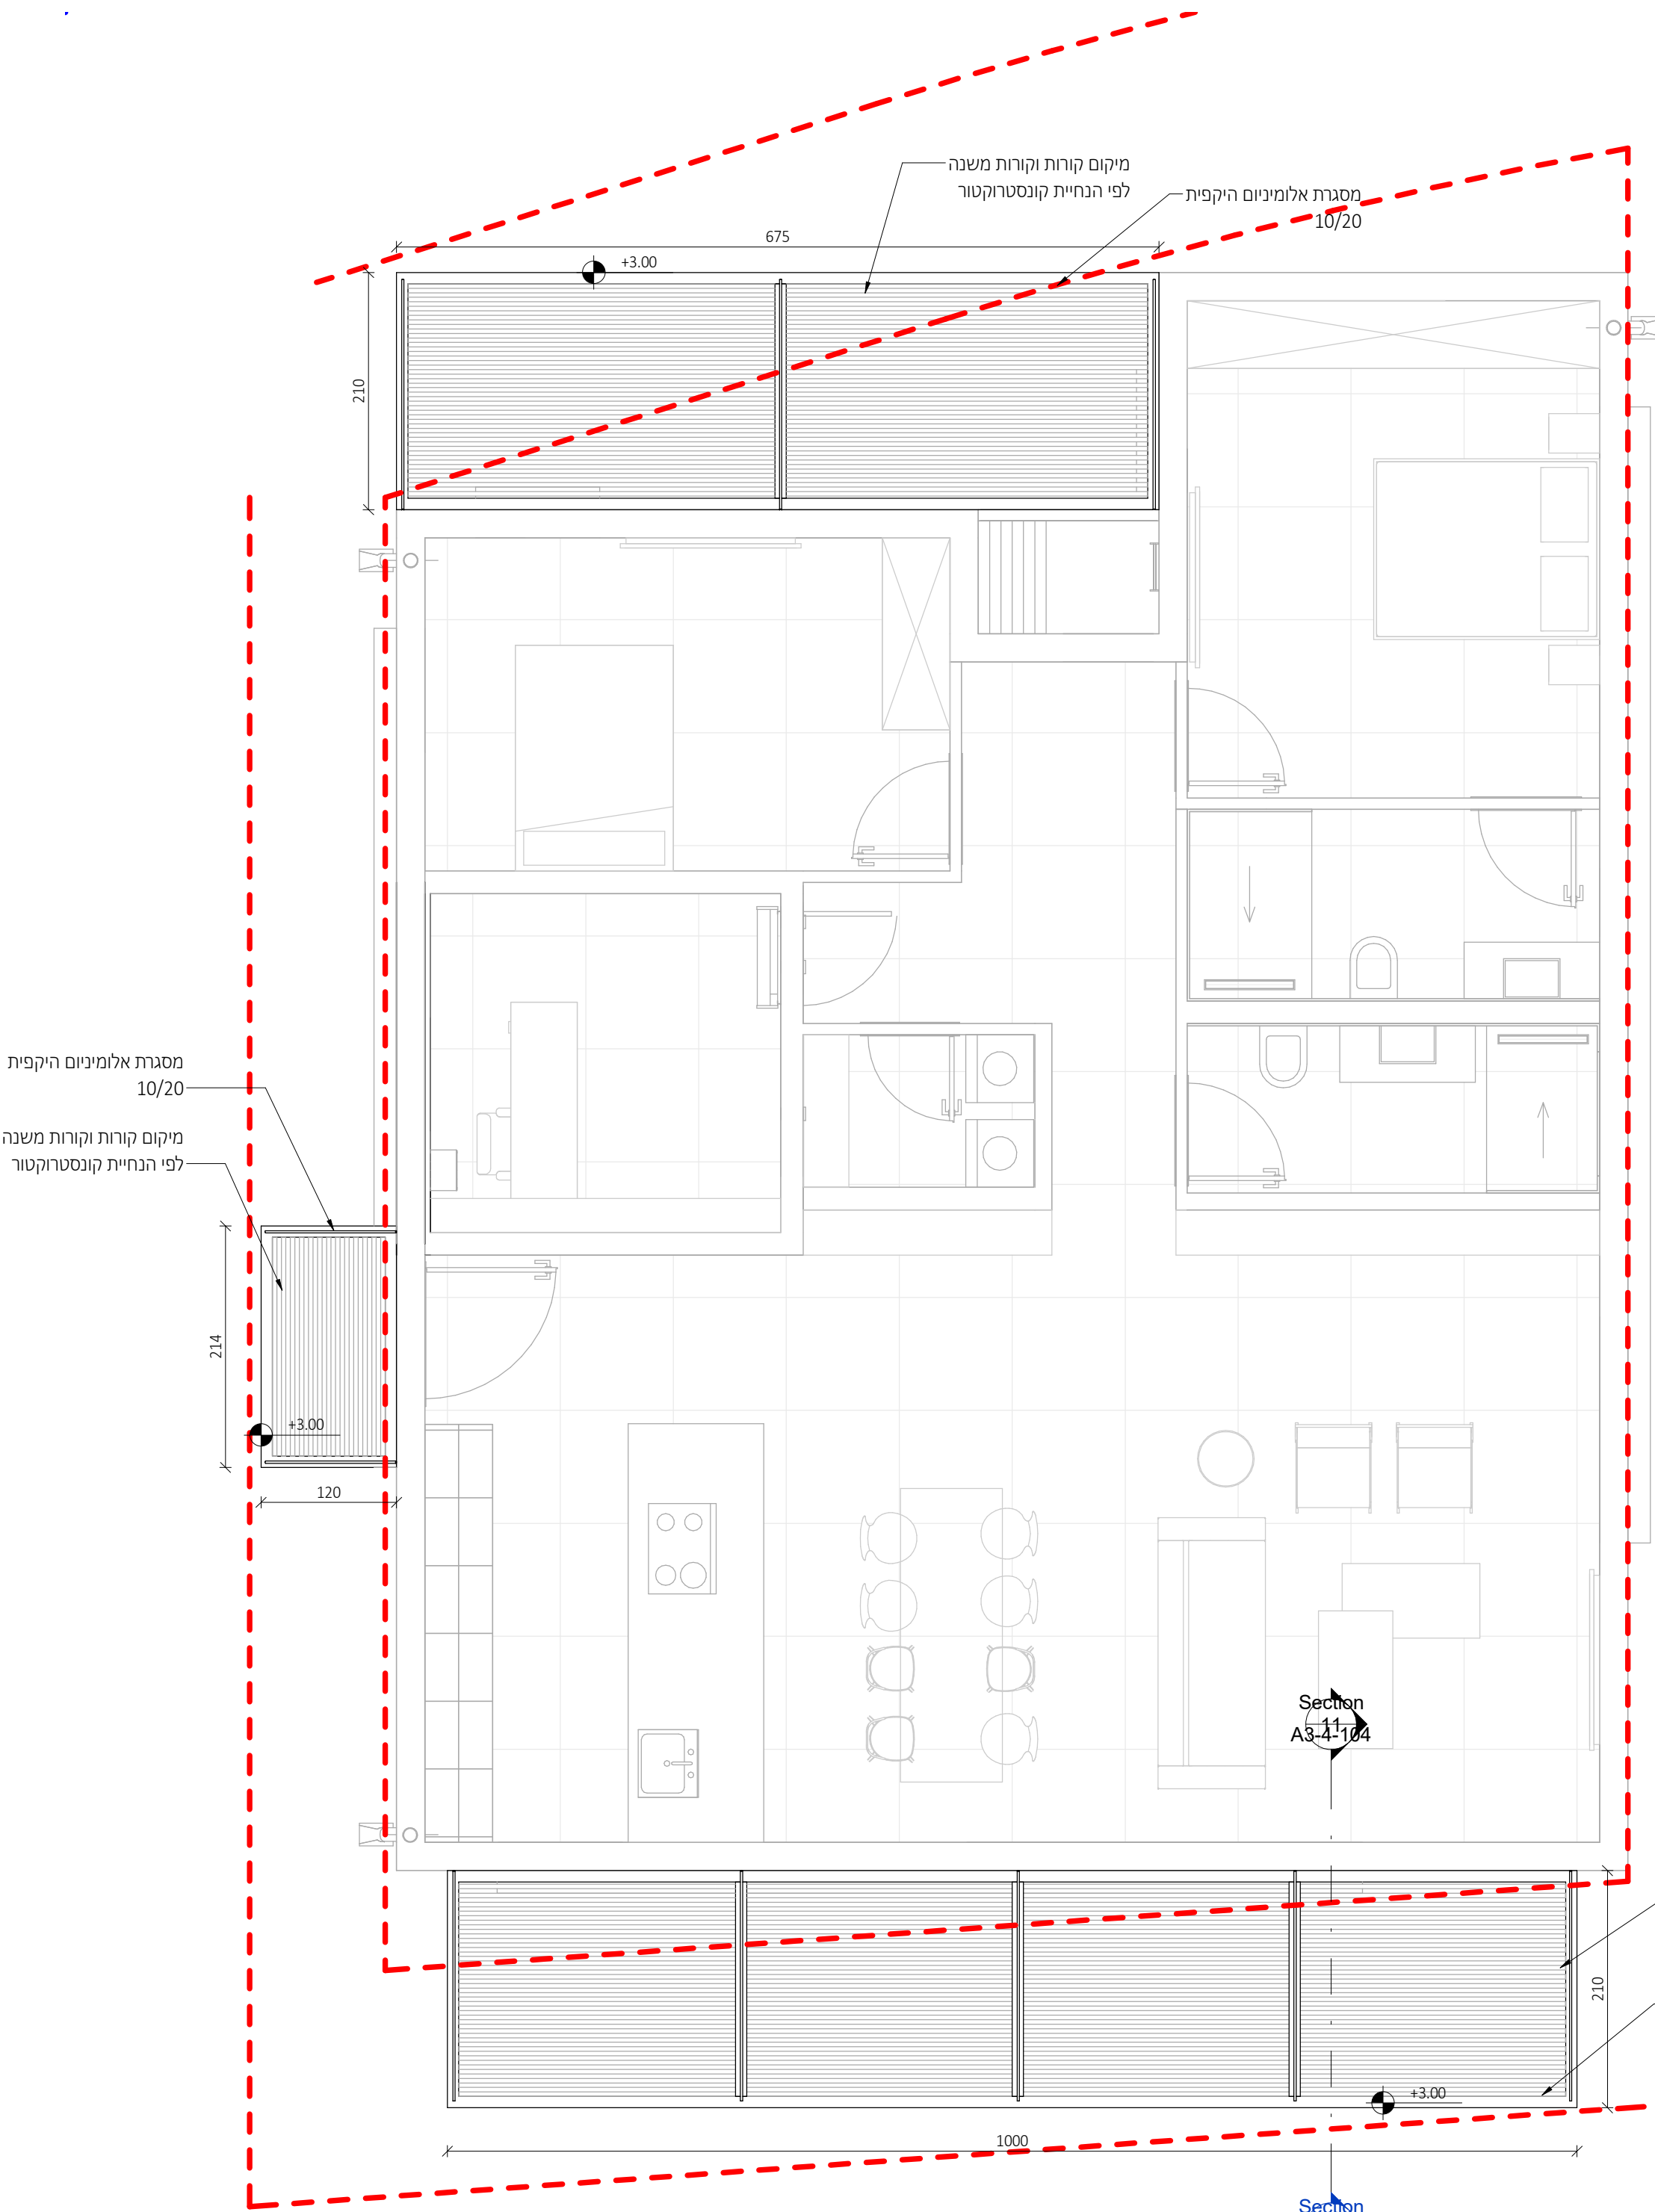


מתכננים:

|                               |
|-------------------------------|
| ניהול פרויקט                  |
| מהיסוד - בן סלומון            |
| פיקוח                         |
| מהיסוד - בן סולומון           |
| קונסטרוקציה                   |
| ערן שילר                      |
| מיזוג אוויר                   |
| אייל ארז מהנדסים ויועצים בע"מ |
| אינסטלציה                     |
| איתן אלמסי                    |
| חשמל                          |
| איתן בסיס                     |
| אלומיניום                     |
| נוף                           |
| נתי בלוקא                     |
| חשמל חכם                      |
| חימום תת רצפתי                |
| איטום                         |
| צבי טל                        |
| אקוסטיקה                      |
| מעליות                        |
| קרקע וביסוס                   |
| דיה הנדסת קרקע וביסוס         |
| רישוי                         |

|   |
|---|
| ± 0.00 = +252.50   |
| הערות:<br>1. תכנית זו יש לקרוא יחד עם תכנית הוויסטים.<br>2. גובה אבטמנטים: ראו תכנית פיתוח.<br>3. הפניות הן בין קירות הבניה ולא כולל פיתוח.<br>4. פיתוח השטח סביב הבנוה, כולל, מדרגות, גדרות, שבילים, ריצופים, שטחים בגנים, חניה וגן וראו תכנית פיתוח.<br>5. איסוף קורות הצפונה במגע עם הקרקע ובזווית תחסי לאורך העמודים והקורות וכל המפרט. כליות לא עם סימני גיבס. ראו תכנית קונסטרוקציה.<br>6. אף דים יבוצע בכל מישור אופקי הכולל מהגבול.<br>7. סוף תחסי במסלול ע"פ מפרט התמקור, מאושר ע"י פיקוח העורך.<br>המבצע אחראי לסידור: עליו לבקר ולבדוק את כל המידות בתכנית ובמקום המבנוה.<br>במסלול של מידות או אי התאמה בתכנית/או בבנוי, עליו להודיע על כך מיד לאדריכל בסופו המשיך בעבודתו.<br>המבצע יחזיק באחריות על תכניתו ויש לוודא כי המבצע יבצע את כל המידות על ידי תחיה בשטח.<br>התכנית היתה רכוש האדריכל ואין לשנות כל שינוש בה או ברעיונות הגולמים בה, אלא באישור בכתב מהאדריכל.<br>המבצע יחזיק באחריות על המבצע.<br>על המבצע והמבצע לוודא התאמה התכנית האדריכלית "כביצוע" לתכנית ויחסי. המבצע והתכנית האדריכלית יש כל הגורמים והשינויים. התכנית כוללת את כל האחריות והידוע על ליום תחמשת. |

משרד קירות:

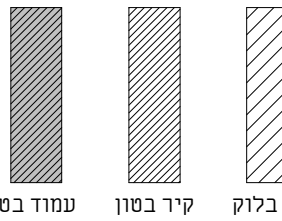

| תאריך      | תיאור | מהדורה |
|------------|-------|--------|
| 22.09.2025 | מכרז  | 1      |
|            |       |        |
|            |       |        |
אדריכלות

|                   |               |
|-------------------|---------------|
| שם המסמך:         | CLIENT NAME:  |
| קבוצת רכישה נופיה |               |
| שם הפרויקט:       | PROJECT NAME: |
| נופיה - מגרש 9    |               |
| שם הגיליון:       | DRAWING NAME: |
| פרטי פרגולה       |               |
| מספר גיליון:      | SHEET NUMBER: |
| A3-4-104          |               |
| תאריך:            | DATE:         |
| 11.08.25          |               |



נירן חיינר אדריכלים  
מנכ"ל  
09-5545642  
www.nh-arch.com  
office@nh-arch.com

22/09/2025 13:36:22

FILE NAME: -----\nofia\תכנית\0019\להיתר\