לוח חשמל דירתי ראשי #1
מגרש 9

5x16N2XY-2XØ50
מוזן ממונה חח"י
3x32A C
4X40A 30mA Type B
3x16A C
3X16A C1 AC3
10A C
3X16A C2 AC3
3x16A C
16A C
3x20A C
C3 AC3
0 I 1 יד 2 שעון
שעון מכני עם רזרבה תוצרת גריזליין דגם 211 תוצרת גרמניה
C1
C2
C3
מאור כללי
שעון שבת לתאורה
תאורת חוץ וחניה
שעון שבת לתאורת חוץ
מיזוג אויר
שעון שבת מיזוג מיני מרכזי
יעודכן לפני תכנית יועץ מיזוג
40
5x10N2XY-Ø50
הכנה למערכת הטענה רכבים חשמליים בחניה
L1 3X1.5N2XY-Ø20 חלל כניסה
L2 3X1.5N2XY-Ø20 פינת אוכל סלון
L3 3X1.5N2XY-Ø20 מטבח
L5 3X1.5N2XY-Ø20 חדרי שינה
L6 3X1.5N2XY-Ø20 חדר שינה הורים
L7 3X1.5N2XY-Ø20 מסדרון +ח. שירות
L8 שמור
L4 3X1.5N2XY-Ø20 ח. רחצה שירותים
L8 3X1.5N2XY-Ø20 תאורת פרגולה
L9 3X1.5N2XY-Ø20 תאורת חוץ חניה גינה שביל כניסה
L10 3X1.5N2XY-Ø20 גלאי עשן
תאורה
S1 5x2.5N2XY-Ø25 הכנה לשער חשמלי חניה
P1 3x2.5N2XY-Ø20 סלון
P2 3x2.5N2XY-Ø20 ממ"ד+ ח. שינה
P3 3x2.5N2XY-Ø20 מערכת סינון ממ"ד
P4 3x2.5N2XY-Ø20 חדר הורים ומסדרון
P5 3x2.5N2XY-Ø20 תנור
P6 3x2.5N2XY-Ø20 תנור
P7 3x2.5N2XY-Ø20 מקרר
P8 3x2.5N2XY-Ø20 מדיח
P9 3x2.5N2XY-Ø20 שירות
P10 3x2.5N2XY-Ø20 שירות
P11 5x2.5N2XY-Ø25 כיריים חשמליות
מטבח
P12 3x2.5N2XY-Ø20 תנור חימום מקלחת הורים
P13 3x2.5N2XY-Ø20 תנור חימום אמבטיה משפחה
P14 3x2.5N2XY-Ø20
P15 3x2.5N2XY-Ø20
מכונת כביסה מייבש כביסה
P16 3x2.5N2XY-Ø20 שקעים חוץ
P17 3X2.5N2XY-Ø20 חימום מים בגז
P18 3x2.5N2XY-Ø20 בוילר
P19 3x2.5N2XY-Ø20 ארון תקשורת
M1 3x2.5N2XY-Ø20 תריס חשמלי
M2 3x2.5N2XY-Ø20 תריס חשמלי
M3 3x2.5N2XY-Ø20 תריס חשמלי
M4 3x2.5N2XY-Ø20 תריס חשמלי
M5 3x2.5N2XY-Ø20 תריס חשמלי
M6 3x2.5N2XY-Ø20 תריס חשמלי
M7 3x2.5N2XY-Ø20 תריס חשמלי
שקעים
AC1 5x4N2XY-Ø25 הזנה למזגן מיני מרכזי
AC1 3x2.5N2XY-Ø20
AC2 3x2.5N2XY-Ø20
AC3 3x2.5N2XY-Ø20
AC4 3x2.5N2XY-Ø20
AC5 3x2.5N2XY-Ø20
ממ"ד
מיזוג אויר יחידות עיליות
P20
P21
P22
P23
שמור

הנחיות לבניית לוח חשמל:

- מבנה לוח חשמל פלסטי חסין אש סדרת FW מתוצרת Hager דגם FW62US2 ל-144 מודולים (6x12)2X לפחות
- דלת פח IP30 מתכתית
- בדיד כפול Class-2
- צבע לבן
- מהדקי אפס והארקה עם חיבור מהיר
- ציוד חשמלי יהיה מסוג ABB שניידר הגר או EATON בלבד בעל זרם
- יש לשמור בלוח 30% מקום לתוספת עתידית בלוח

תפוצה														תאריך
מנהל הפרויקט	אדריכל	מזמין/יזם	חשמל	קבלן	בטיחות	אקוסטיקה	אינסטלציה	קונסטרוקציה	אדריכל נוף	מטבחים	חברת חשמל	חברת בזק		

מס'	שינויים	תאריך

עודכן ע"י: יפעת

א. בסיס
הנדסת חשמל בע"מ
משרד: יד חרוצים 16, ירושלים 93420
טל: 074-7021015 נייד: 050-6550484
פקס: 077-5131015 דוא"ל: office@ebasis.co.il

שם הפרויקט: נופיה-אלפי מנשה

שם התכנית: לוח #1 - מגרש 9, נופיה

קנה מידה: 1:50

○ לעיון ○ לאישור ○ למכרז ● לביצוע

תאריך: Date: 05.03.2025

מס' קובץ: File: 675W.dwg

תכנן: יפעת

שרטט: ליאל

אישר: איתן

מס' עדכון: 0

מס' הגליון: 9

מס' הפרויקט: 675

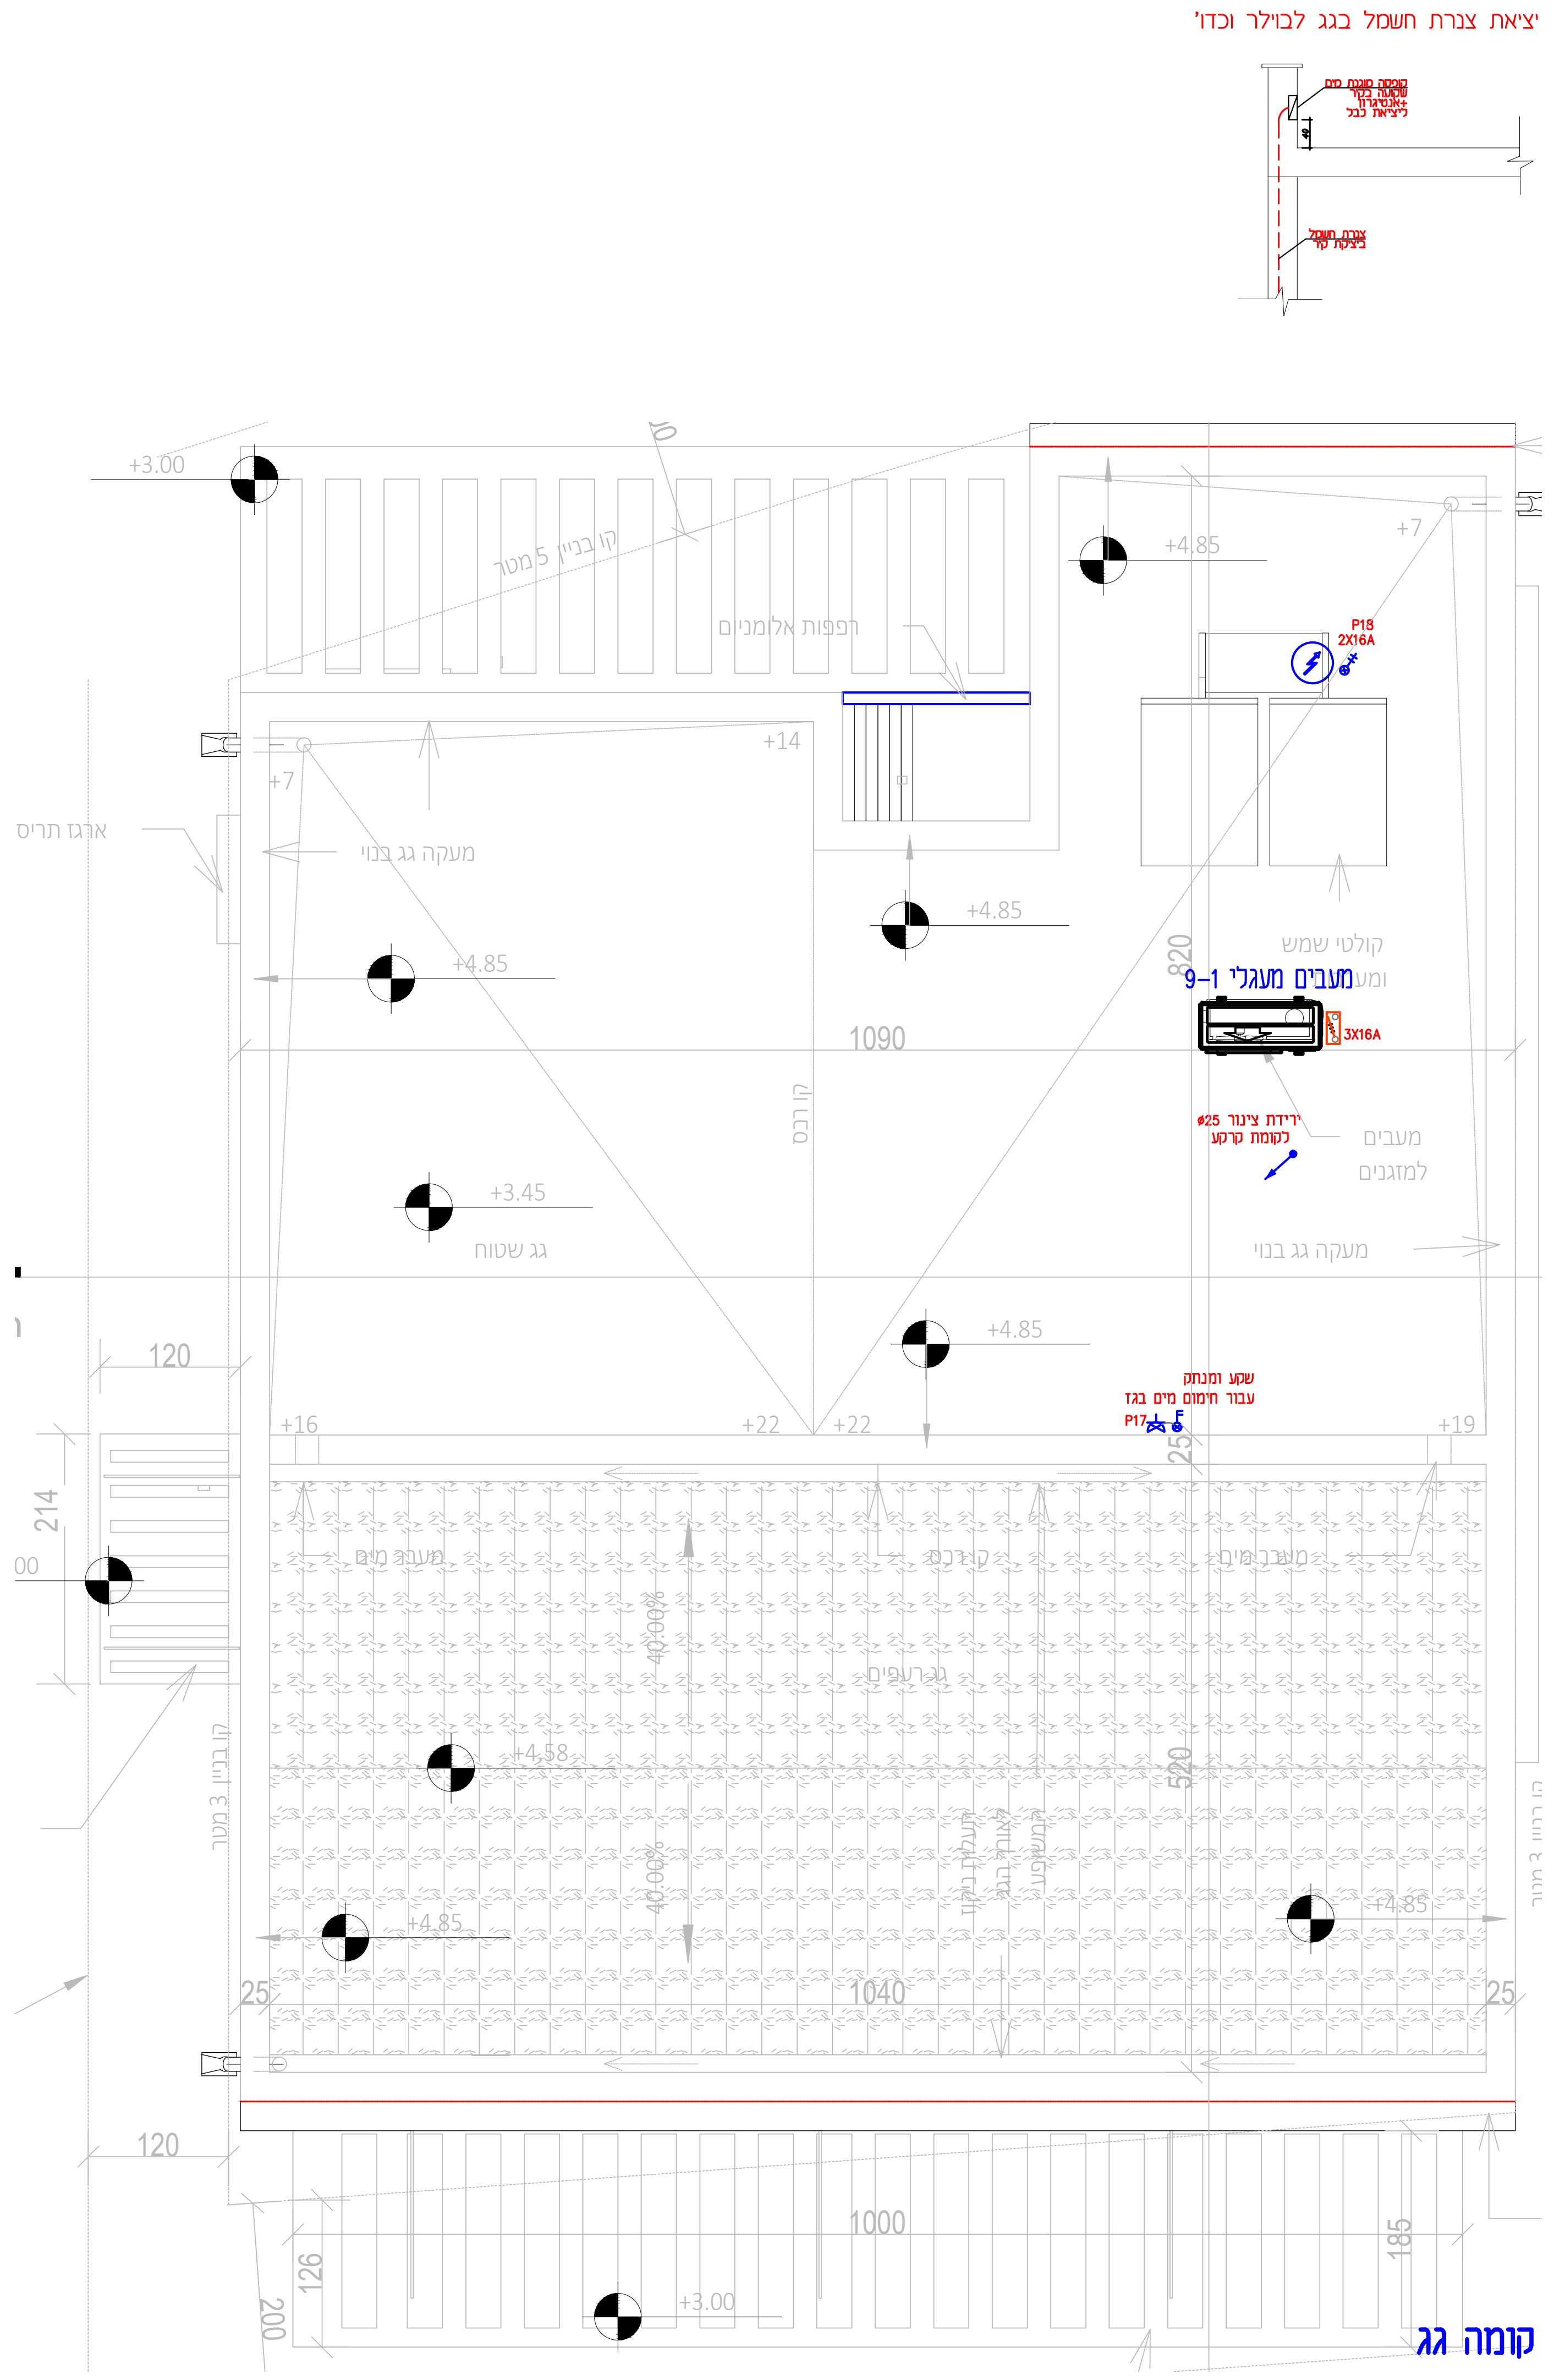

קומת גג

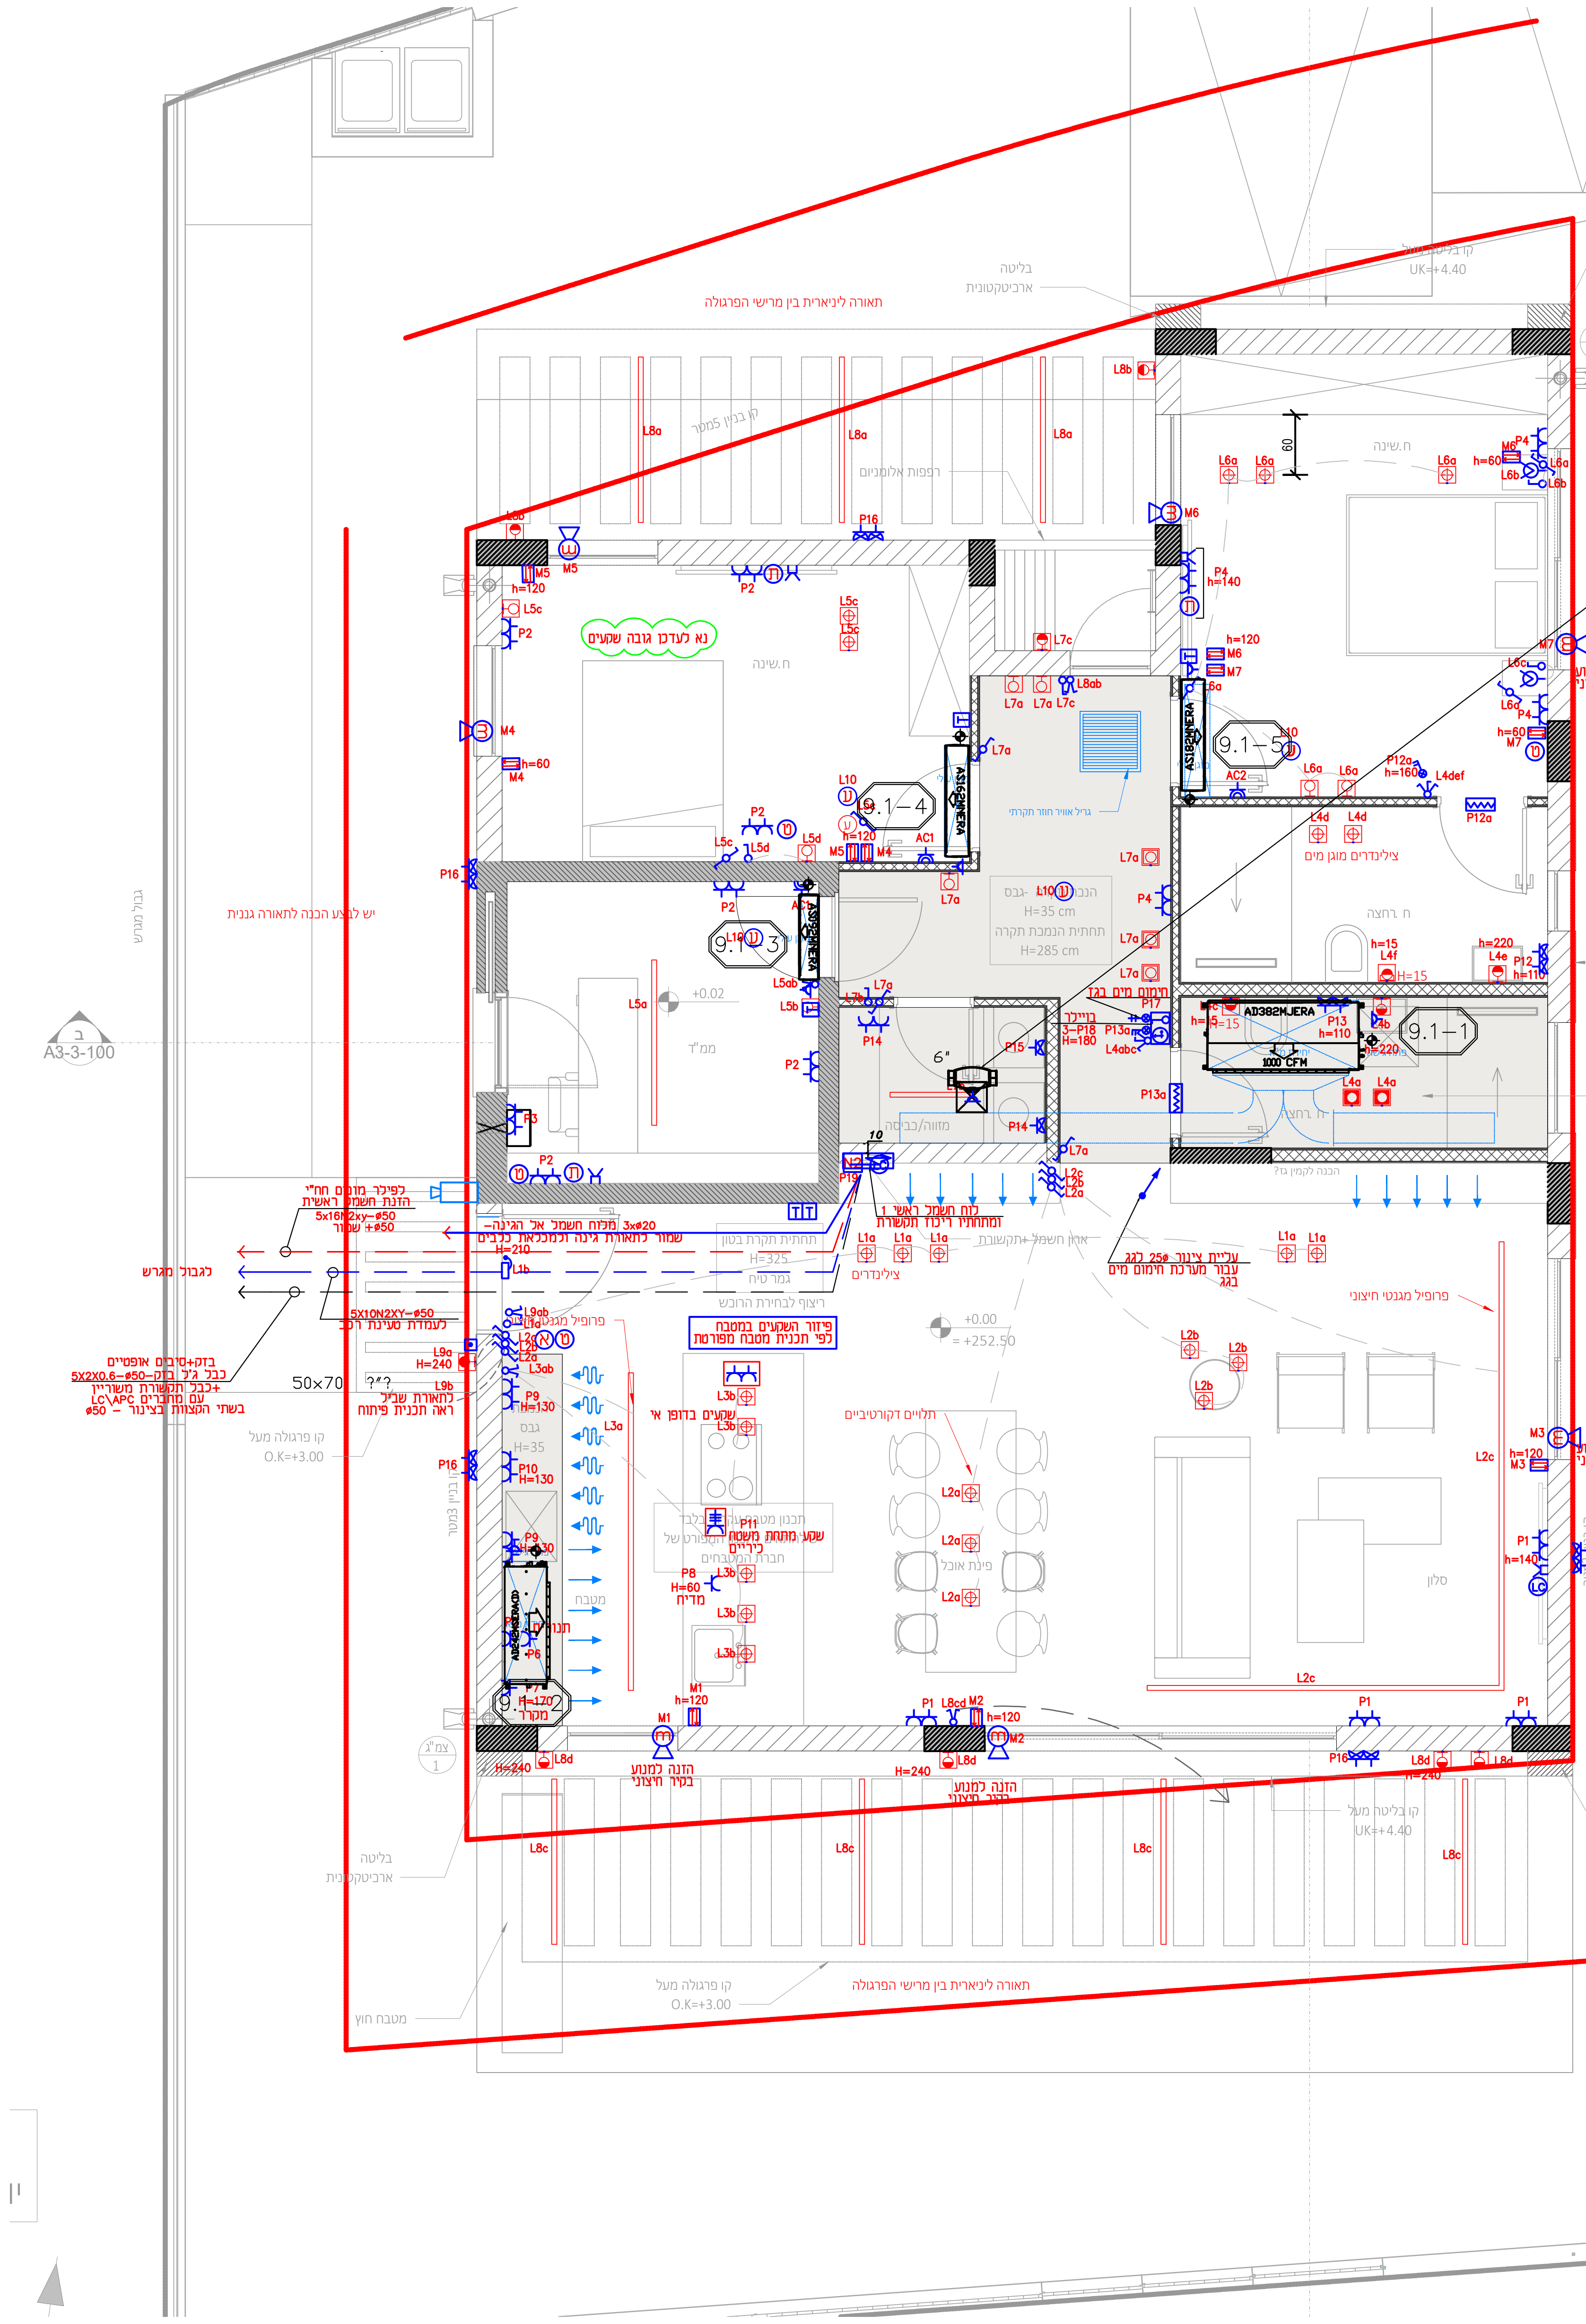

מפוח יניקת אוויר 1
כדוגמת S&P
TD-500/150 SILENT
100 CFM@ 140 PA
הזנת חשמל 59W
מידה: ר48/ג22/ע31 ס"מ
2480 RPM
כולל תריס אל חוזר ווסת תדר
וגגון נגד גשם
הפעלה ע"י מתג תאורה
לטיפול יועץ חשמל

קומת קרקע

מקרא חשמל ותאורה:

לוח	⚡	לוח חשמל
חשמל ותקשורת	⅄	שקע 16A בודד H=60 אלא אם צוין אחרת
	⅄⅄	זוג שקעי 16A H=60 אלא אם צוין אחרת
	N2	מקבץ שקעים טיפוסי סיום באביזר N2 "ניסקו" בארון תקשורת מתחת לוח חשמל
	⅄	שקע חד פאזי מוגן מים H=60 אלא אם צוין אחרת
	⅄	שקע ליחידת מ"א 16A H=220 מיקום סופי לפי תכנית מיזוג ובתיאום מול אדריכל
	ט	נקודת טלפון מלאה-צנרת, כבילה ושקע טלפון H=60
	◎	CIMA BOX הכולל: 4 שקעי שרות+2 תקשורת
	ת	נקודת תקשורת H=60, צינור ø25 עם חוט משיכה מריכוז תקשורת דירתי
	Ӿ	נקודת טלויזיה מושלמת+צינור שמור ø20 H=60
	LC	נקודת תקשורת מלאה הכוללת: כבל תקשורת אופטי תקני מותקן בצינור ø25 סיום בית תקע אופטי LC\APD לפי דרישות ת"י 1-11801 עם ראשים מוכנים מראש להתקנה בארון תקשורת דירתי ובסלון עם חוט משיכה מריכוז תקשורת דירתי
	m	מנוע חשמלי H=200
	T	הכנה לתרמוסטט מזגן- צינור 20 לחלל תקרה
	T	תרמוסטט חימום תת רצפתי- יבוצע לפי הנחיות ספק
	▭	שקע לתנור חימום חשמלי 10 סמ מעל פתח דלת
	⚡	בויילר
	⊗	הכנה לוונטה סיום בשקע
מפסקים	♂	מפסק מאור בודד H=90 אלא אם צוין אחרת במפסקי הדלקה ליד מיטה H=60
	♂	מפסק כפול H=90 אלא אם צוין אחרת במפסקי הדלקה ליד מיטה H=60
	♂	מפסק מאור מחליף H=90 אלא אם צוין אחרת במפסקי הדלקה ליד מיטה H=60
	▣	לחצן פעמון דלת H=90
	⊗	מנתק מואר 2X16A / 3X16A
	F	מפסק דו קוטבי מואר לתנור חימום חשמלי H=160
	↕	מפסק הרמה/הורדה לתריס חשמלי 5 סמ מעל מפסק תאורה ע"פ פרט
	◷	מפסק עם שעון בקיר לבויילר H=180
	א	פנל צפיה (מוניטור) +לחצן פתיחה דלת H=120
תאורה וגילוי אש	⊗	תאורת חרום חד תכליתית LED 3w
	ע	גלאי עשן בתקרה
	◎	נקודת מאור בתקרה
	⊗	ג"ת פנים תקרתי מוגן מים
	⊗	ג"ת LED עגול שקוע בתקרה
	⊗	ג"ת LED עגול קירי גובה H=220
	⊗	ג"ת פנים קירי למנורת לילה H=120
	⊗	ג"ת פנים/חוץ קירי מוגן מים H=240 , במרתף H=220
	◓	ג"ת קירי נמוך לתאורת התמצאות מדרגות/שירותים, h=15 מהרצפה/ מרום מדרגה
	▭	ג"ת מלבני IP65 להתקנה על פרגולה
	✱	מאוורר להתקנה בחוץ
	⊸	פעמון דלת 220V (גונג) התקנה מעל דלת כניסה
	▭	הכנה מצלמה אבטחה, צינור 25 וחוט משיכה מארון תקשורת דירתי

חזית לוח חשמל ראשי וארונות תקשורת

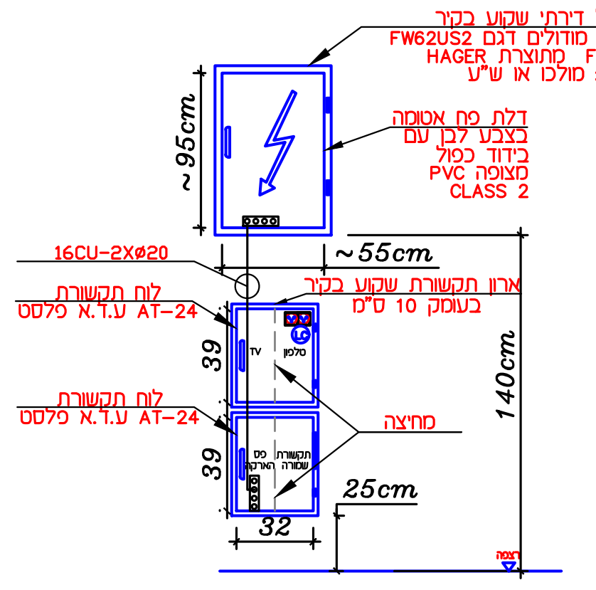

מעגלים שמורים ליחידות
מ"א פנימיות:
1-AC1
1-AC2
1-AC3

פרט לגבהים של הדלקות,
תאורה ותריסים:

תפוצה															תאריך
מנהל הפרויקט	אדריכל	מזמין/יזם	חשמל	קבלן	בטיחות	אקוסטיקה	אינסטלציה	קונסטרוקציה	אדריכל נוף	מטבחים	חברת חשמל	חברת בזק			

מס'	שינויים	תאריך
1	עדכון תכנית	15.12.24
2	עדכון תכנית	23.12.24
3	עדכון תוכנית אדריכלית ותאורה	12.2.25
4	עדכון תוכנית	20.2.25
5	עדכון תוכנית	27.3.25
6	עדכון תוכנית	2.4.25
7	עדכון תוכנית	8.5.25
8	עדכון תוכנית עפ"י הערות אדריכלית	21.5.25
9	הטמעת מ"א	3.6.25
10	עדכון תאורה	4.6.25

עודכן ע"י: שלומית

הערות:

-במידה והוחלט על הכנות לבית חכם: כהכנה לבית חכם ולדלת חכמה יש להשחיל חוט 0 כחול נוסף בכל מפסק הדלקה התכנון עצמו יעשה ע"י ספק בית חכם

-הכנות למיזוג אויר,חימום תת רצפתי, מערכות אבטחה, וחימום מים בחשמל יהיו עפ הנחיות יועץ לכל תחו141

-יש לקרוא תכנית זו יחד עם תכנית אדריכלות למקרא בלוקים אדריכלות

הערות:

- * כל הגבהים בתכנית הינם למרכז אביזר אלא אם ציין במפורש אחרת
- * מיקום סופי לנקודות תאורה ייקבע ע"פ תכנית עיצוב פנים תאורת חוץ -ע"פ יועץ פיתוח
- * מיקום סופי לשקעי מיזוג עפ"י תוכנית יועץ מיזוג

יחידות קצה מעגל 9-1											
מס' יחידה בתכנית	תוצרת	דגם	מאייד	תפוקת קרור Btu/h	ספיקת אויר CFM	רמת רעש db(A)	משקל KG	מידות גוף	מידות פנל	מתח הזנה V/Hz/Ph	הספק נצרך W
9-1.2	Haier	AD242MSERA(D)	Slim Duct Low ESP	24,200	547	36	24	ר117/ג18.5/ע42 ס"מ	---	230/50/1	---
9-1.1	Haier	AD382MJERA	Duct Medium ESP	38,200	1000	42	48	ר150/ג25/ע70 ס"מ	---	230/50/1	---
9-1.3	Haier	AS092MNERA	מאייד עילי	9,500	352	36	10	ר85.5/ג28/ע20 ס"מ	---	230/50/1	---
9-1.4	Haier	AS162MNERA	מאייד עילי	15,300	471	39	16	ר111.5/ג33.6/ע25 ס"מ	---	230/50/1	---
9-1.5	Haier	AS182MNERA	מאייד עילי	19,100	541	40	16	ר111.5/ג33.6/ע25 ס"מ	---	230/50/1	---

106,300

א. בסיס
הנדסת חשמל בע"מ
משרד: יד חרוצים 16, ירושלים 93420
טל: 074-7021015 נייד: 050-6550484
פקס: 077-5131015 דוא"ל: office@ebasis.co.il

שם הפרויקט:
נופיה-אלפי מנשה
מגרש 9

שם הגיליון:
תוכנית חשמל

○ לעיון ○ לאישור ● למכרז ○ לביצוע

קנה מידה: 1:50

מס' קובץ: File: 675-9.dwg

תאריך: Date: 16.09.2024

תכנן: איתן

שרטט: רחל

אישר: איתן

מס' עדכון: 10

מס' הגליון: E

מס' הפרויקט: 675