


פתחי גישה אופן ארט בתיאום סופי מול אדריכל
כלל יחידות המיזוג אשר נמצאות בתוך נגרות יש לתאם סופית מול אדריכל ונגרות

Court 9
1st Floor

Option ~~No~~1
VRF duct unit in living room
and wall mounted in rooms

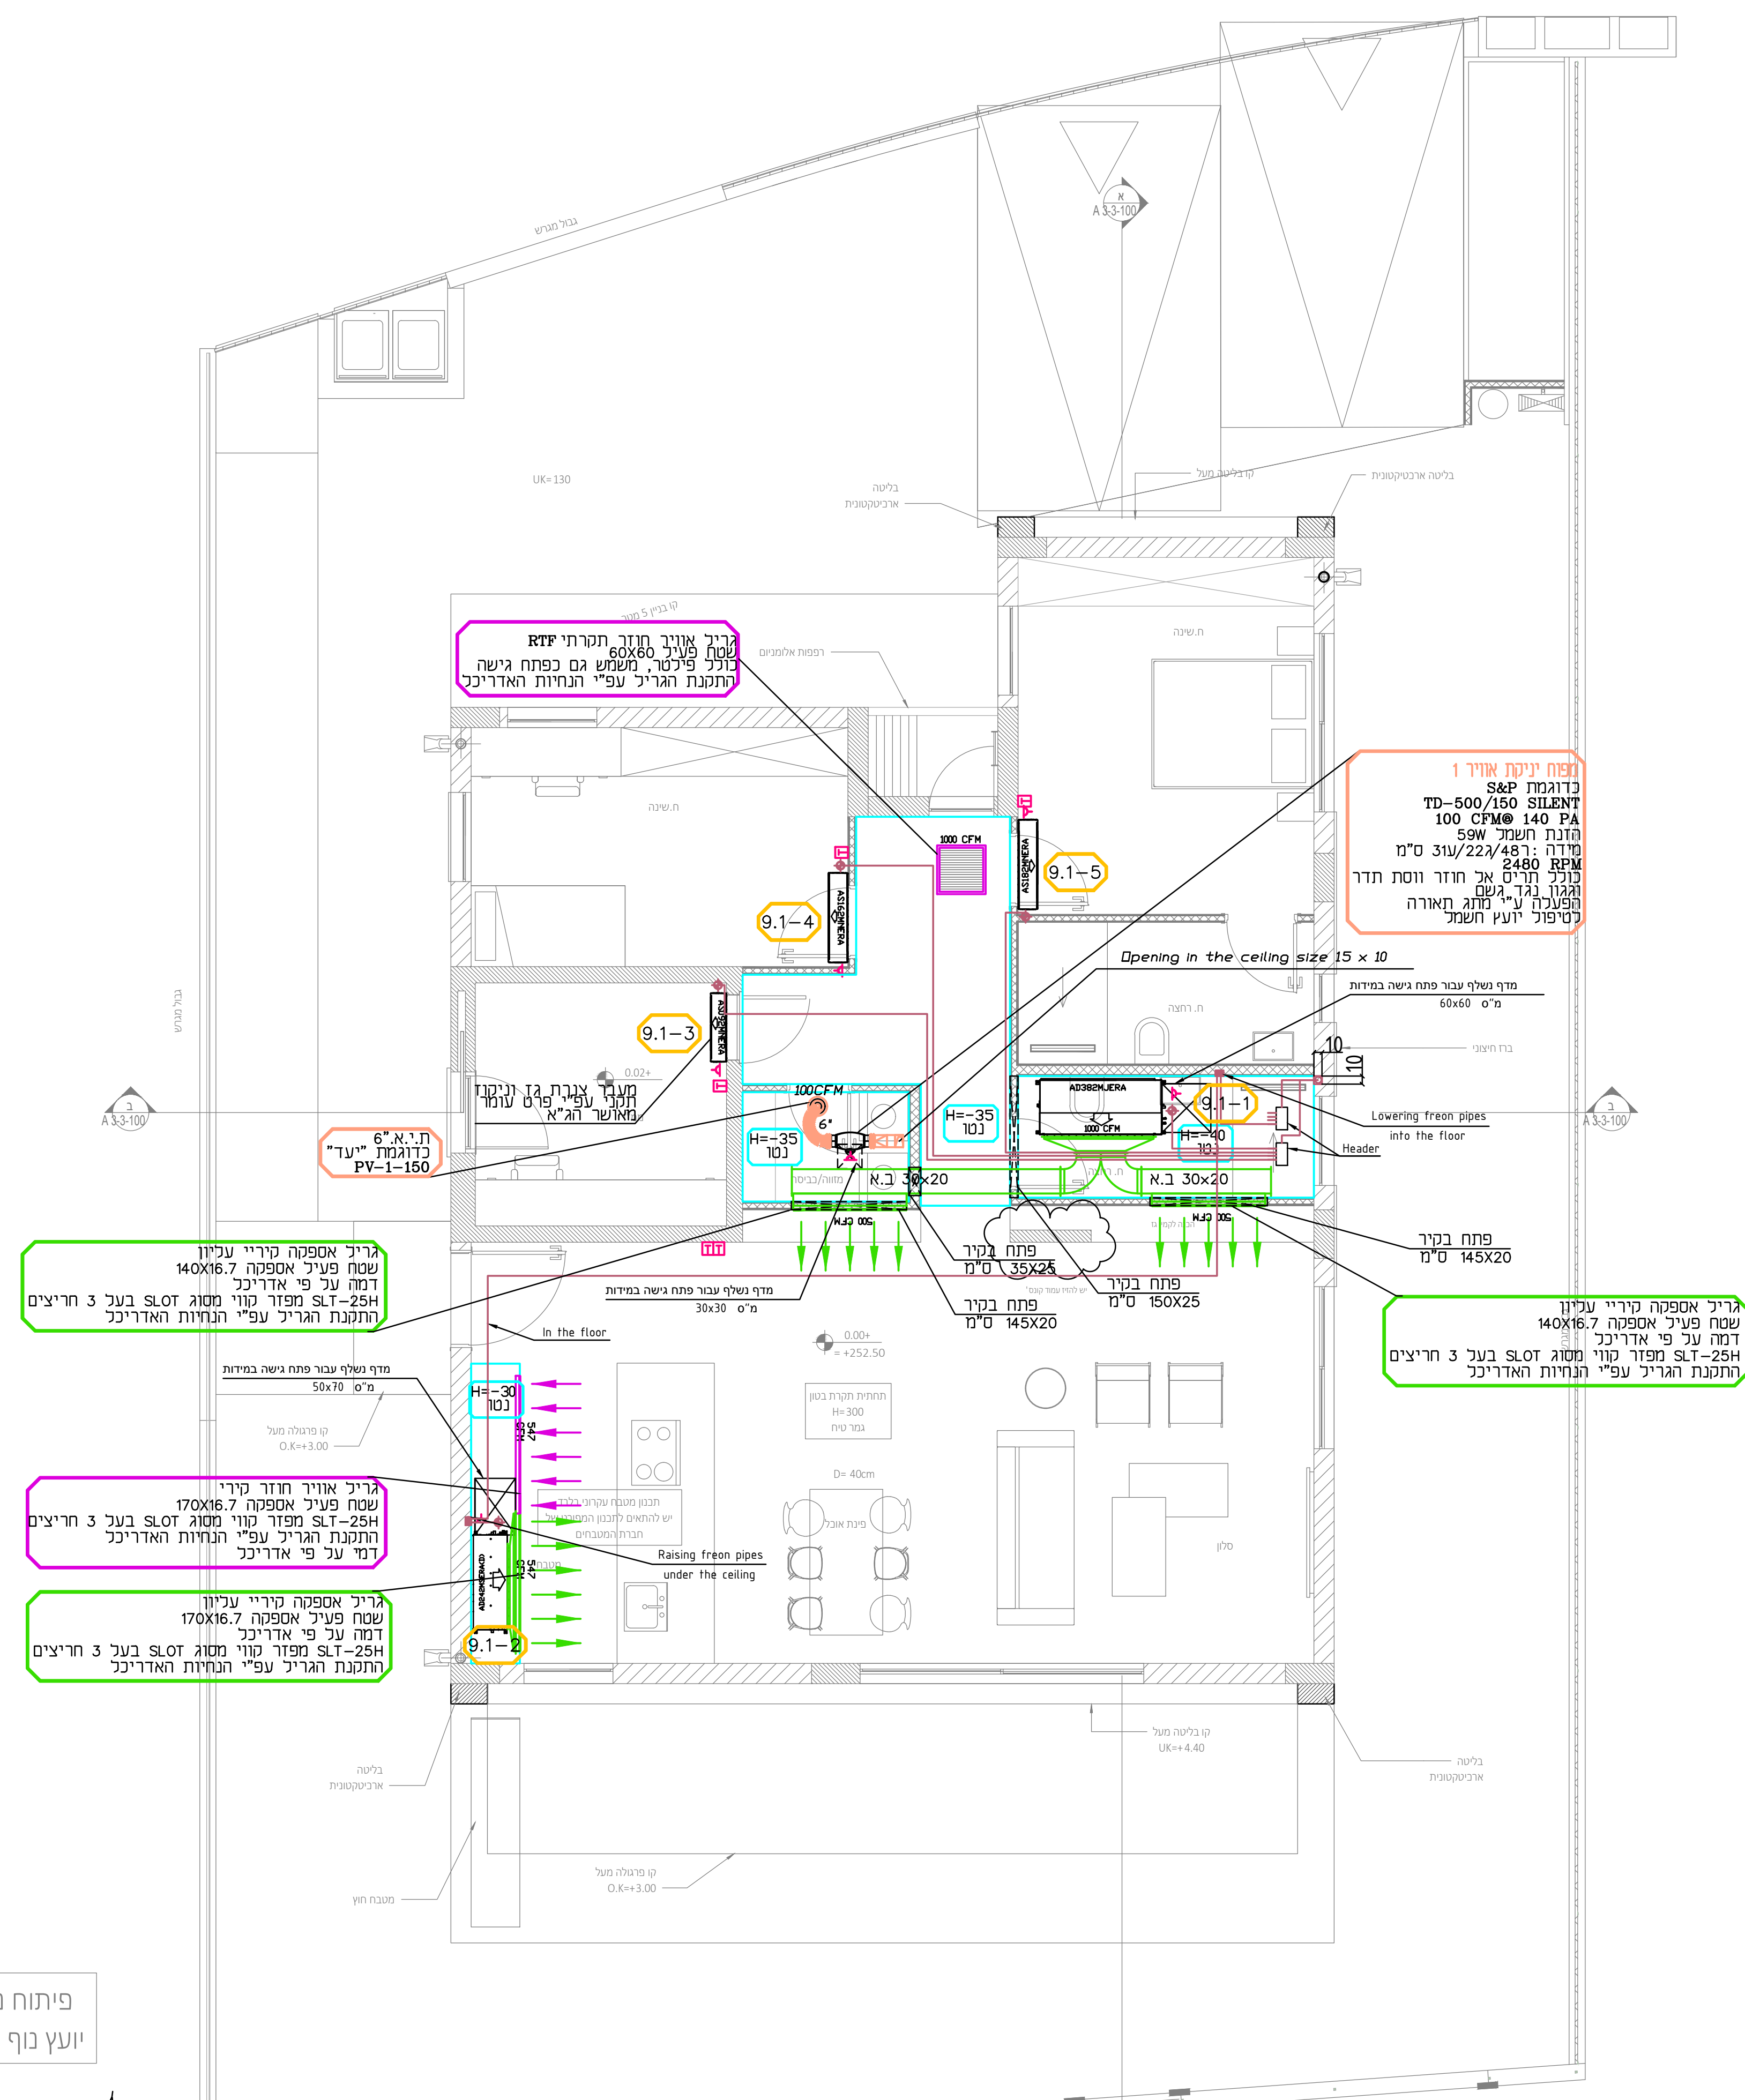


פיתוח נוף עפ"י תוכניות
יועץ נוף ראה פירוט בנפרד

3

Court 9
Roof

Option No1
VRF duct unit in living room and wall mounted in rooms

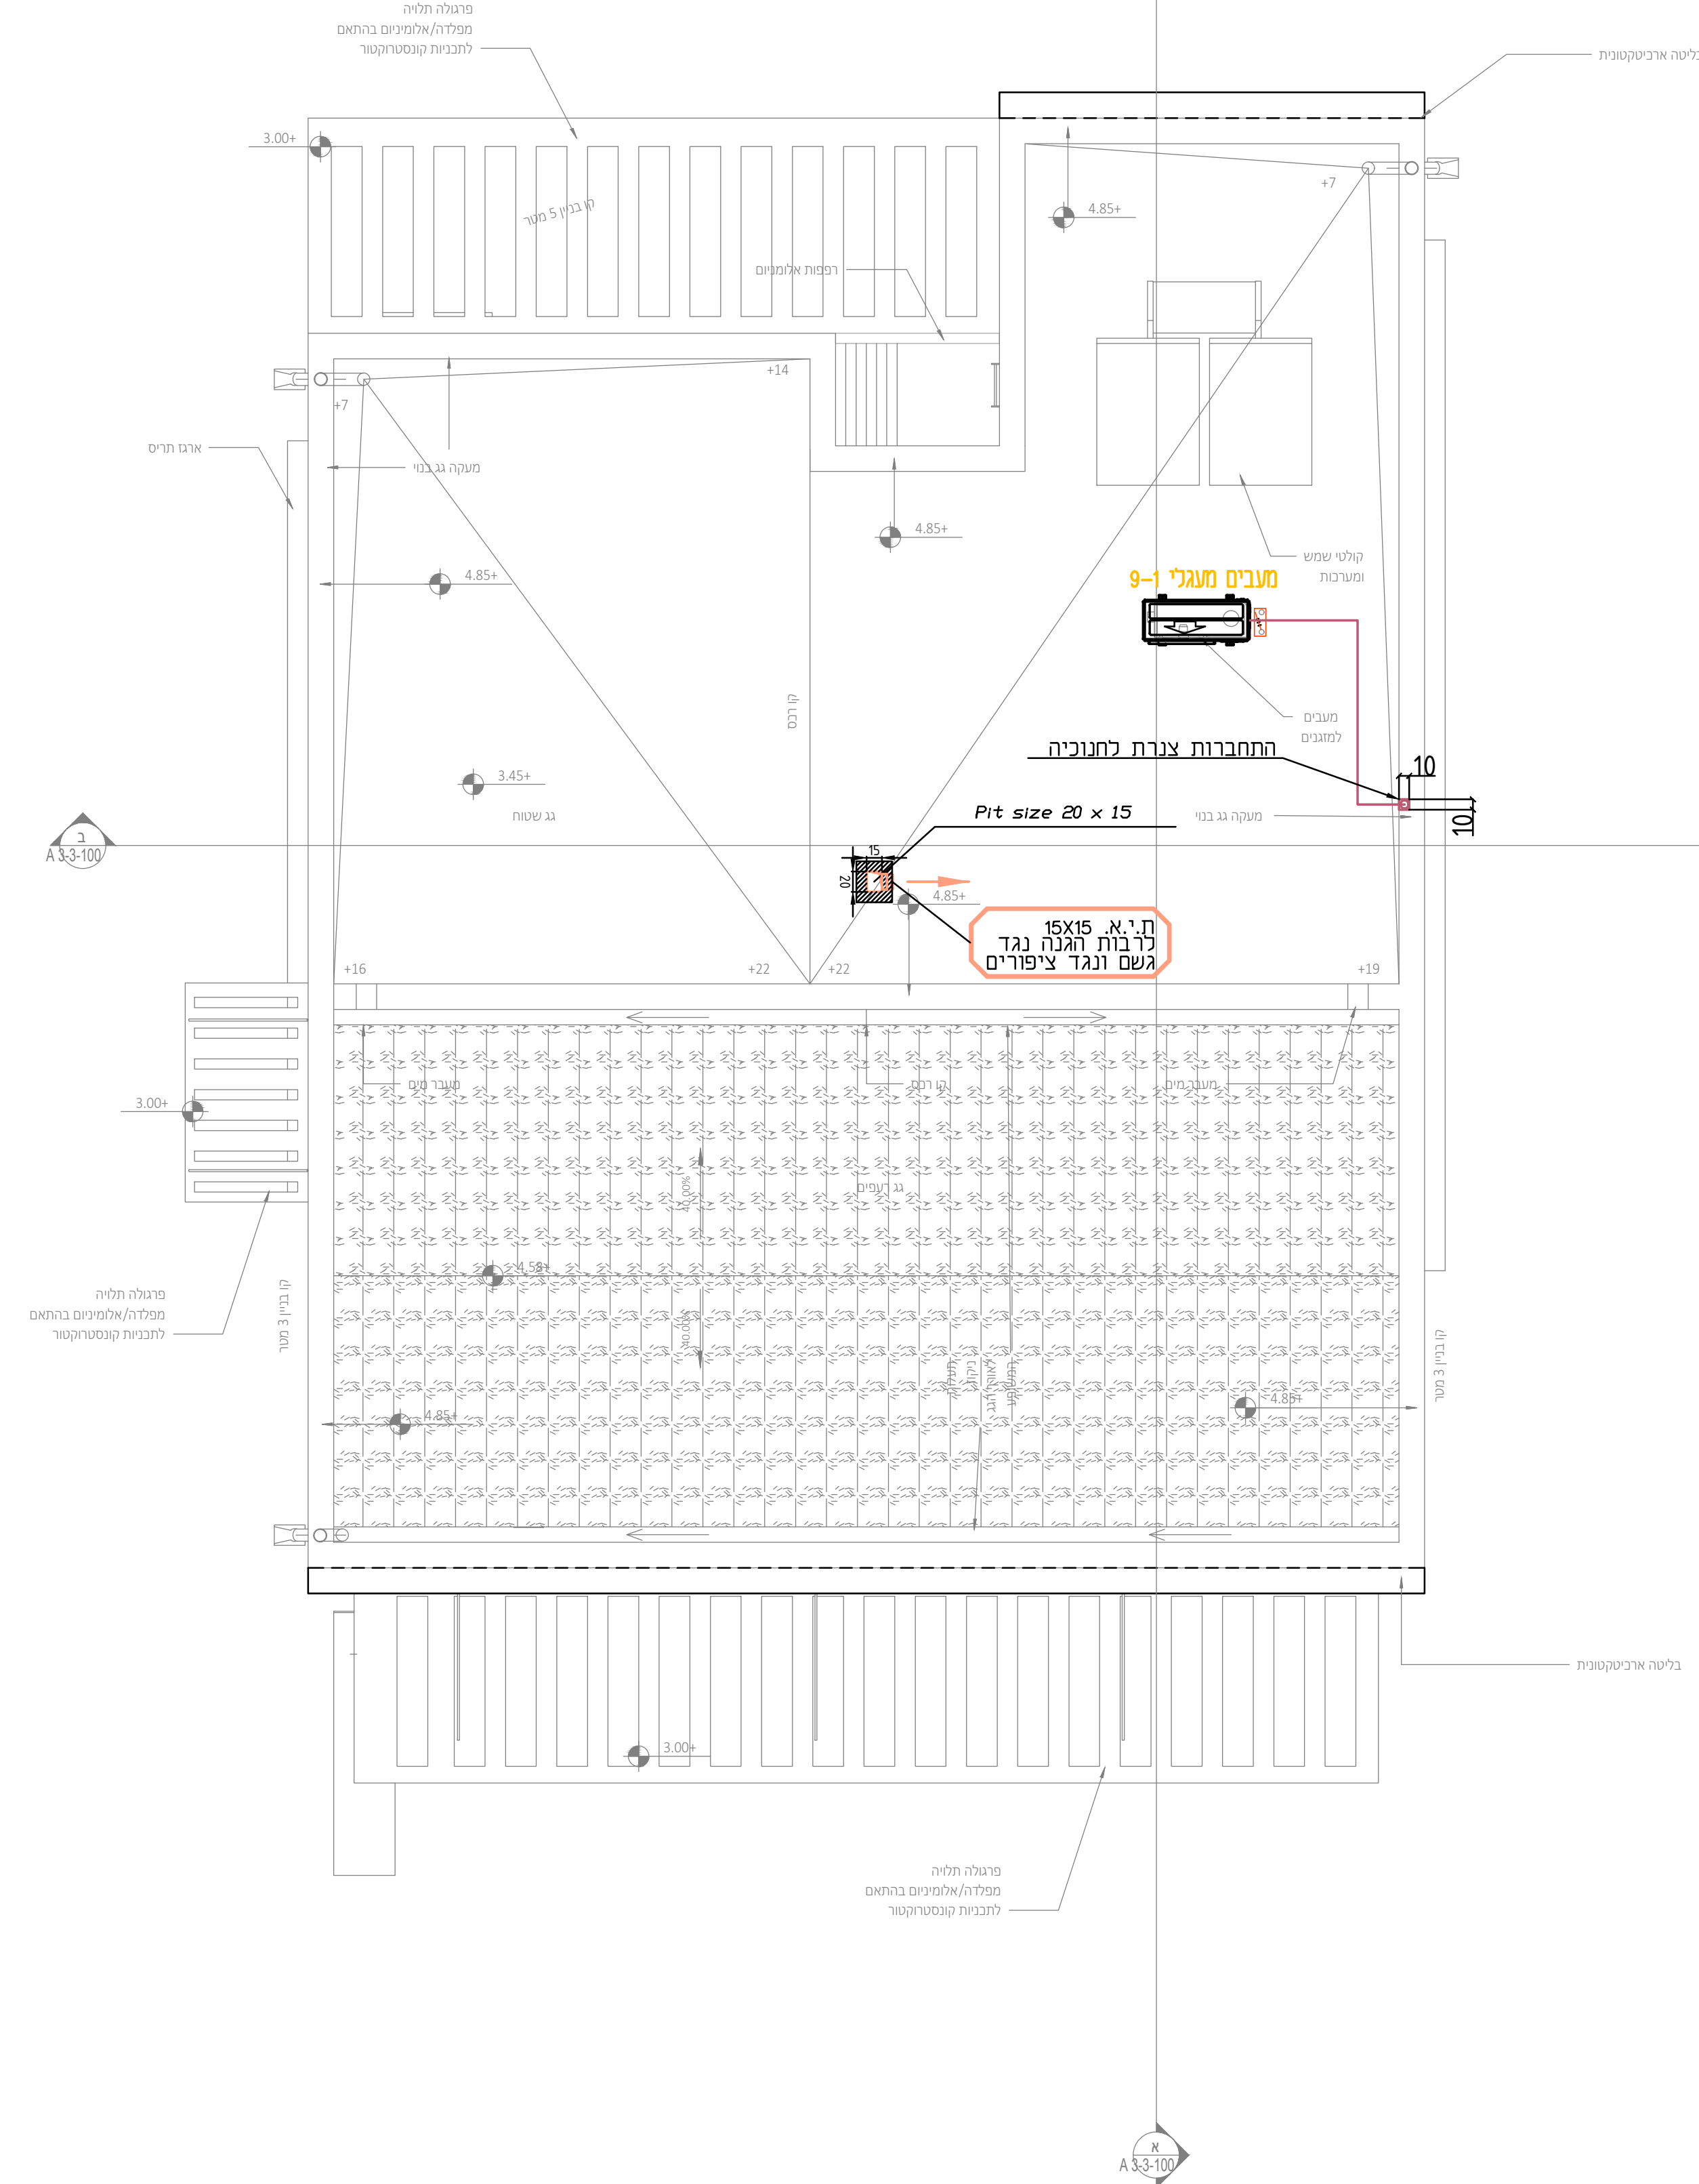

תפוצה

[illegible]

מהדורה

חברות ראשון	08.05.2025	⚠️
חברות ראשון	28.03.2025	⚠️
חברות כעיון	11.03.2025	⚠️
שנייה:	חברות:	⚠️

המבצע אחראי כמידות ולהתאמתו למציאות בכל מקרה של אי התאמה, סתירה או טעות עליו להודיע למתכנן לפני התקדמותו בביצועו אין לקבוע מידות על סמך מדידה בשרטוט. אין לעשות כל שימוש בתוכנית זו או ברעיונות הגלומים בה ללא אישור בכתב מאת המתכנן.

הערות

1. כל התעלות מחזק לעמנה יבורדו
בבידוד אקוסטי בעו"מ 2"
מידות התעלות הן מידות פח
2. תעלות מוזג בתוך המגנה יבורדו
בבידוד אקוסטי פנימי 1"
מידות התעלות הן מידות פח
3. תעלות אוויר צף יבורדו
בבידוד סרטי 1"
מידות התעלות הן מידות פח
4. יש לטאסם בסיועיון או פינות החיבור
של תעלות מידות אוויר לפני כיפוף
הפחים המתחברים

מקרא

- [illegible]

מקרא צבעים בתכנית

- | | |
|--------------------------|---|
| תעלות ותריסי אוויר חוזר |  |
| תעלות ותריסי אספקת אוויר |  |
| תעלות ותריסי אוויר צח |  |
| תעלות ותריסי 'ניקת אוויר |  |
| תעלות ותריסי שחרור עשן |  |
| גנרת גז וחשמל |  |
| סימון מעגלי מ'זוג אוויר |  |

191	מבני מגורים צמודי רקעק נופה אפרי ענשה מגרש 9	ספ תוריסם
1:50	מיזוג אוויר ואיוורור	ספ תוריסם
08.05.2025	קומת רקעק וגג	ספ תוריסם
העדר פחורות		ספ תוריסם
3		ספ תוריסם
פחורות		ספ תוריסם
לביצוע	מכרז	כאשר
		לעיון
		11.03.2025
		אחיה
		הנחיה מרשם אילי ארז



יחידות קצה מעל ו-9											
מס' יחידה בתכנית	חיצות	דגם	מאייד	תפנית Btu/h	ספיקת אייר CFM	רמת רעש db(A)	משקל KG	מידות גוף	מידות פנל V/Hx/Ph	חמם חזנה W	הספק נצרך
9-1.2	Haier	AD242MSERA(D)	Slim Duct Low ESP	24,200	547	36	24	ר170/18.5/42 ס"מ	230/50/1	---	---
9-1.1	Haier	AD382MJERA	Duct Medium ESP	38,200	1000	42	48	ר200/25/70 ס"מ	230/50/1	---	---
9-1.3	Haier	AS092MNERA	מאייד עילי	9,500	352	36	10	ר200/28/20 ס"מ	230/50/1	---	---
9-1.4	Haier	AS182MNERA	מאייד עילי	15,300	471	38	16	ר250/33.6/111.5 ס"מ	230/50/1	---	---
9-1.5	Haier	AS182MNERA	מאייד עילי	19,100	541	40	16	ר250/33.6/111.5 ס"מ	230/50/1	---	---